

CÔNG TY TNHH ĐẦU TƯ PHÚ VIỆT TÍN

ĐỊA CHỈ: LÔ 18-19 QUỐC LỘ 1A, XÃ DẦU GIÂY, TỈNH ĐỒNG NAI, VIỆT NAM

# HỒ SƠ THIẾT KẾ BẢN VẼ THI CÔNG

DỰ ÁN: KHU DÂN CƯ A1-C1 (ĐÔ THỊ DẦU GIÂY)

ĐỊA ĐIỂM: XÃ DẦU GIÂY, TỈNH ĐỒNG NAI

CHỦ ĐẦU TƯ: CÔNG TY TNHH ĐẦU TƯ PHÚ VIỆT TÍN

CÔNG TRÌNH: NHÀ Ở THƯƠNG MẠI LIÊN KÈ

HẠNG MỤC: MẪU NHÀ T3-2b



HOÀN THÀNH 07/2025

# PHẦN KIẾN TRÚC














# DANH MỤC BẢN VẼ

| STT                               | KÝ HIỆU | NỘI DUNG BẢN VẼ BỘ MÔN KIẾN TRÚC              |
|-----------------------------------|---------|-----------------------------------------------|
| A00 - TỔNG THỂ                    |         |                                               |
| 01                                | A00-01  | DANH MỤC BẢN VẼ                               |
| 02                                | A00-02  | BẢNG GHI CHÚ CẤU TẠO VẬT LIỆU HOÀN THIỆN TỜ 1 |
| 03                                | A00-03  | BẢNG GHI CHÚ CẤU TẠO VẬT LIỆU HOÀN THIỆN TỜ 2 |
| 04                                | A00-04  | BẢNG GHI CHÚ CẤU TẠO VẬT LIỆU HOÀN THIỆN TỜ 3 |
| 05                                | A00-06  | CHI TIẾT CẤU TẠO                              |
| 06                                | A00-07  | CHI TIẾT CẤU TẠO                              |
| A01 - MẶT BẰNG ĐỊNH VỊ            |         |                                               |
| 07                                | A01-01  | MẶT BẰNG VỊ TRÍ MẪU NHÀ                       |
| 08                                | A01-02  | BẢNG THÔNG SỐ LỖ ĐẤT                          |
| A02 - MẶT BẰNG CÔNG NĂNG - XÂY TÔ |         |                                               |
| 09                                | A02-01  | MẶT BẰNG ĐỊNH HƯỚNG CÔNG NĂNG TẦNG 1          |
| 10                                | A02-02  | MẶT BẰNG ĐỊNH HƯỚNG CÔNG NĂNG TẦNG 2, TẦNG 3  |
| 11                                | A02-51  | MẶT BẰNG XÂY TÔ TẦNG 1                        |
| 12                                | A02-52  | MẶT BẰNG XÂY TÔ TẦNG 2                        |
| 13                                | A02-53  | MẶT BẰNG XÂY TÔ TẦNG 3, MÁI                   |
| A03 - MẶT ĐỨNG                    |         |                                               |
| 14                                | A03-01  | MẶT ĐỨNG TRỤC A-C, TRỤC C-A                   |
| 15                                | A03-02  | MẶT ĐỨNG TRỤC 4-1                             |
| A04 - MẶT CẮT                     |         |                                               |
| 16                                | A04-01  | MẶT CẮT                                       |
| 17                                | A04-02  | MẶT CẮT                                       |
| A05 - MẶT BẰNG KÝ HIỆU            |         |                                               |
| 18                                | A05-01  | MẶT BẰNG KÝ HIỆU TẦNG 1, TẦNG 2               |
| 19                                | A05-02  | MẶT BẰNG KÝ HIỆU TẦNG 3, MÁI                  |





| STT                                                    | KÝ HIỆU | NỘI DUNG BẢN VẼ BỘ MÔN KIẾN TRÚC  |
|--------------------------------------------------------|---------|-----------------------------------|
| A06 - CHI TIẾT THANG                                   |         |                                   |
| 20                                                     | A06-01  | CHI TIẾT THANG                    |
| 21                                                     | A06-02  | CHI TIẾT THANG (TT)               |
| 22                                                     | A06-03  | 3D CẦU THANG                      |
| A08 - CHI TIẾT CỬA ĐI CỬA SỔ VÁCH KÍNH - CHI TIẾT KHÁC |         |                                   |
| 23                                                     | A08-01  | CHI TIẾT BAN CÔNG 1               |
| 24                                                     | A08-02  | CHI TIẾT BAN CÔNG 2               |
| 25                                                     | A08-03  | CHI TIẾT BAN CÔNG 3               |
| 26                                                     | A08-04  | CHI TIẾT BAN CÔNG 4               |
| 27                                                     | A08-05  | CHI TIẾT BAN CÔNG 4 (TT)          |
| 28                                                     | A08-06  | CHI TIẾT SÂN THƯỢNG TẦNG 3        |
| 29                                                     | A08-07  | CHI TIẾT LAM MÁI TẦNG 3           |
| 30                                                     | A08-08  | CHI TIẾT SÂN PHƠI TẦNG 3          |
| 31                                                     | A08-09  | CHI TIẾT NÁP THẨM MÁI, SENO       |
| 32                                                     | A08-10  | CHI TIẾT NÁP THẨM MÁI, SENO (TT)  |
| 33                                                     | A08-11  | CHI TIẾT HÀNG RÀO SAU NHÀ         |
| 34                                                     | A08-12  | CHI TIẾT HÀNG RÀO SAU NHÀ (TT)    |
| 35                                                     | A08-51  | CHI TIẾT CỬA ĐI                   |
| 36                                                     | A08-52  | CHI TIẾT CỬA ĐI, CỬA SỔ           |
| 37                                                     | A08-53  | CHI TIẾT VÁCH KÍNH                |
| 38                                                     | A09-01  | MẶT BẰNG TRẮNG ĐÈN TẦNG 1         |
| 39                                                     | A09-02  | MẶT BẰNG TRẮNG ĐÈN TẦNG 2, TẦNG 3 |
| A10 - MẶT BẰNG CHỐNG THẨM                              |         |                                   |
| 40                                                     | A10-01  | MẶT BẰNG CHỐNG THẨM TẦNG 2        |
| 41                                                     | A10-02  | MẶT BẰNG CHỐNG THẨM TẦNG 3, MÁI   |




|   |                          |                 |
|---|--------------------------|-----------------|
| GHI CHÚ:<br>- CÁC ĐƠN VỊ THI CÔNG PHẢI PHỐI HỢP BẢN VẼ CỦA TẤT CẢ CÁC BỘ MÔN KHÁC NẾU THẤY SỰ KHÁC BIỆT PHẢI BẢO CHO ĐƠN VỊ THIẾT KẾ XỬ LÝ.<br>- KHI XỬ LÝ SỰ KHÁC BIỆT, PHẢI THỰC HIỆN ƯU TIÊN THEO THỨ TỰ GIỮA CÁC BỘ MÔN: KIẾN TRÚC → KẾT CẤU / BỘ MÔN KHÁC; HOẶC ƯU TIÊN TRONG CÙNG BỘ MÔN: CHI TIẾT → TỔNG THỂ<br>- CÁC SỐ LƯU KỊCH THUỘC PHẢI ĐƯỢC KIỂM TRA THỰC TẾ TẠI CÔNG TRÌNH, NẾU THẤY SỰ KHÁC BIỆT SƠ VỚI BẢN VẼ THI PHẢI BẢO CHO ĐƠN VỊ THIẾT KẾ. |                          |                 |
| HIỆU CHỈNH:   |                          |                 |
| REV   | NGÀY                     | NỘI DUNG        |
|   |                          |                 |
| CHỦ ĐẦU TƯ:<br>CÔNG TY TNHH ĐẦU TƯ<br><b>PHÚ VIỆT TÍN</b><br>ĐỊA CHỈ: LÔ 18-19 QUỐC LỘ 1A, XÃ DẦU GIẤY,<br>TỈNH ĐỒNG NAI, VIỆT NAM   |                          |                 |
|   |                          |                 |
| CTHĐT.V:   |                          | ĐẠNG PHƯỚC BÌNH |
| ĐƠN VỊ THIẾT KẾ:<br>CÔNG TY CỔ PHẦN TƯ VẤN THIẾT KẾ<br><b>BASE ARC</b><br>ĐỊA CHỈ: 138 ĐIỆN BIÊN PHỦ, PHƯỜNG TÂN ĐỊNH,<br>TP. HỒ CHÍ MINH, VIỆT NAM   |                          |                 |
|   |                          |                 |
| TỔNG GIÁM ĐỐC:   |                          | TRẦN ĐỨC AN     |
| CHỦ NHIỆM DỰ ÁN:   |                          |                 |
| KTS. NGUYỄN THÀNH THÁI   |                          |                 |
| CHỦ TRÌ THIẾT KẾ:   |                          |                 |
| KTS. NGUYỄN THÀNH THÁI   |                          |                 |
| THIẾT KẾ:   |                          |                 |
| KTS. LÊ ĐÌNH TÂM   |                          |                 |
| KIỂM TRA:   |                          |                 |
| KTS. NGUYỄN ĐỨC THÁI   |                          |                 |
| DỰ ÁN:<br>KHU DÂN CƯ A1-C1 (ĐÔ THỊ DẦU GIẤY)<br>ĐỊA ĐIỂM: XÃ DẦU GIẤY, TỈNH ĐỒNG NAI   |                          |                 |
| CÔNG TRÌNH:<br><br>NHÀ Ở THƯƠNG MẠI LIÊN KẾ   |                          |                 |
| HẠNG MỤC:<br><br>MẪU NHÀ T3-2b   |                          |                 |
| TÊN BẢN VẼ:<br><br>DANH MỤC BẢN VẼ   |                          |                 |
| MỤC ĐÍCH PHÁT HÀNH:   |                          |                 |
|   | BẢN VẼ MỜI THẦU          |                 |
|   | THIẾT KẾ CƠ SỞ           |                 |
| ✓   | THIẾT KẾ BẢN VẼ THI CÔNG |                 |
|   | BẢN VẼ HOÀN CÔNG         |                 |
| HOÀN THÀNH   |                          | 07/2025         |
| TỶ LỆ   |                          | NTS             |
| SỐ HIỆU BẢN VẼ   |                          | A00-01          |



**BẢNG GHI CHÚ VẬT LIỆU HOÀN THIỆN SẢN**
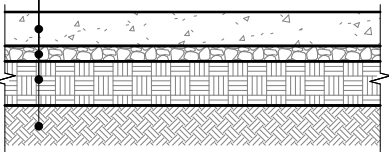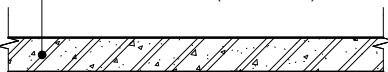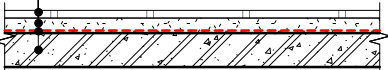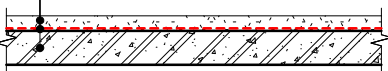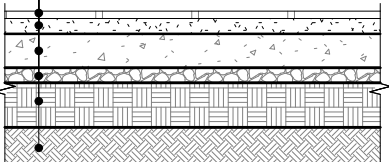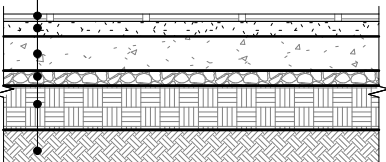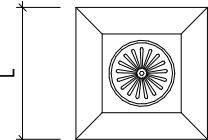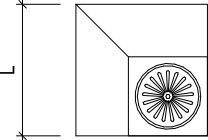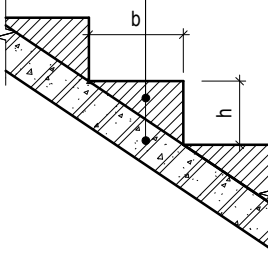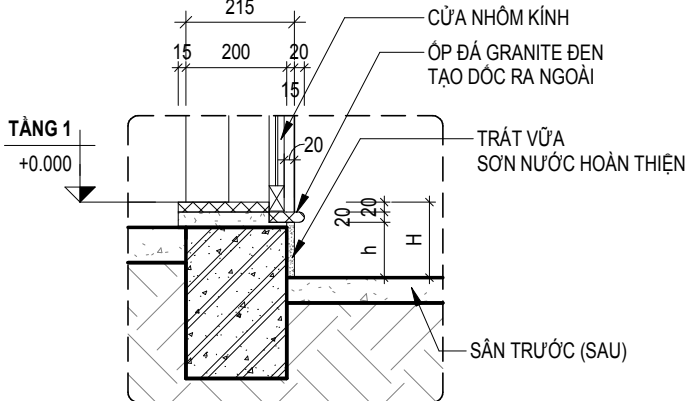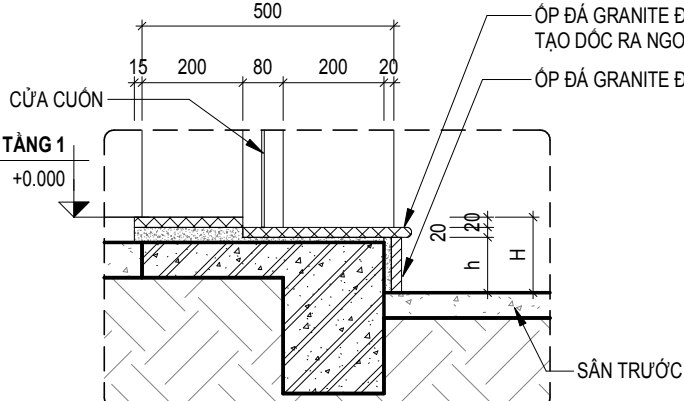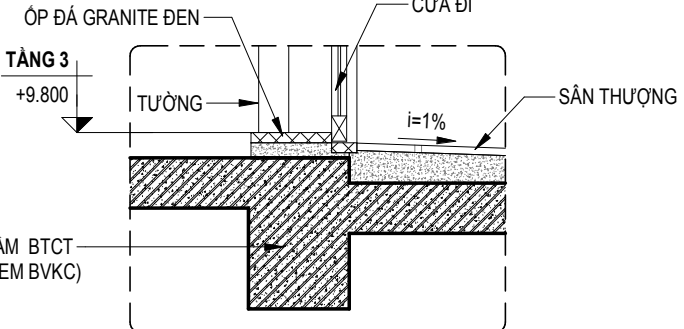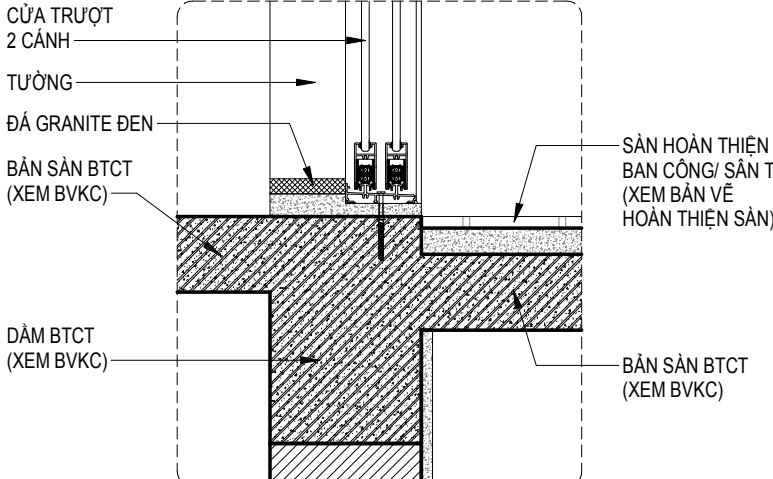
|    |  |   |  |   |  |   |  |   |  |   |  |                            |  |   |  |
|----|--|---|--|---|--|---|--|---|--|---|--|----------------------------|--|---|--|
| N1 |  | NỀN TẦNG 1   |  | N2   |  | NỀN TẦNG 2, 3   |  | N3   |  | SÀN BAN CÔNG, LÔ GIA, SÂN THƯỢNG   |  | N4                         |  | SÀN MÁI   |  |
|    |  | <div><div>1. NỀN BÊ TÔNG ĐÁ 10x20mm B15, DÂY 70mm</div><div>2. LỚP ĐÁ 0x40mm ĐẪM CHẶT</div><div>3. LỚP CÁT SAN NỀN ĐẪM CHẶT K=0,9, TỪNG LỚP DÂY 300mm</div><div>4. LỚP ĐẤT TỰ NHIÊN DỌN SẠCH BỀ MẶT ĐẪM CHẶT</div></div> <div></div>   |  |   |  | <div><div>1. BÀN SÀN BTCT (XEM BVKC)</div></div> <div></div>   |  |   |  | <div><div>1. SÀN LÁT GẠCH NHÁM MẶT 300x600mm</div><div>2. LỚP VỮA CÁN NỀN B5 TẠO DỐC i=1% VỀ PHẪU THU, CHỖ MÔNG NHẤT (VỊ TRÍ PHẪU THU) MIN=20mm.</div><div>3. QUÉT CHỐNG THẨM CAO LÊN TƯỜNG BAO 300mm</div><div>4. BÀN SÀN BTCT (XEM BVKC)</div></div> <div></div> |  |                            |  | <div><div>1. LỚP VỮA CÁN NỀN B5 TẠO DỐC i=1% VỀ PHẪU THU NƯỚC</div><div>2. QUÉT CHỐNG THẨM SÀN, CUỘN CHÂN TƯỜNG CAO 300mm (CHIỀU DÂY LỚP CHỐNG THẨM THEO CHỈ DẪN NHÀ SẢN XUẤT)</div><div>3. BÀN SÀN BTCT (XEM BVKC)</div></div> <div></div> |  |
| Ns |  | NỀN SÀN TRƯỚC   |  | Ns1   |  | NỀN SÀN SAU   |  |   |  | CHI TIẾT ĐẶT PHẪU   |  |                            |  | CHI TIẾT BẠC THANG ĐIỂN HÌNH   |  |
|    |  | <div><div>1. NỀN LÁT GẠCH TERRAZZO 400x400mm</div><div>2. LỚP VỮA XI MĂNG B5 DÂY 30mm, TẠO DỐC ĐỎ RA VÍA HỀ CHỖ MÔNG NHẤT DÂY 20mm</div><div>3. NỀN BÊ TÔNG ĐÁ 10x20mm B12,5, DÂY 70mm</div><div>4. LỚP ĐÁ 0x40mm ĐẪM CHẶT</div><div>5. LỚP CÁT SAN NỀN ĐẪM CHẶT K=0,9, TỪNG LỚP DÂY 300mm</div><div>6. LỚP ĐẤT TỰ NHIÊN DỌN SẠCH BỀ MẶT ĐẪM CHẶT</div></div> <div></div> |  |   |  | <div><div>1. NỀN LÁT GẠCH PORCELAIN 600x600mm</div><div>2. LỚP VỮA XI MĂNG B5 DÂY 30mm, TẠO DỐC VỀ PHẪU THU CHỖ MÔNG NHẤT DÂY 20mm</div><div>3. NỀN BÊ TÔNG ĐÁ 10x20mm B12,5, DÂY 70mm</div><div>4. LỚP ĐÁ 0x40mm ĐẪM CHẶT</div><div>5. LỚP CÁT SAN NỀN ĐẪM CHẶT K=0,9, TỪNG LỚP DÂY 300mm</div><div>6. LỚP ĐẤT TỰ NHIÊN DỌN SẠCH BỀ MẶT ĐẪM CHẶT</div></div> <div></div> |  |   |  | <div><div></div><div></div><div>L</div><div>GHI CHÚ: L THEO KÍCH THƯỚC CỦA VIÊN GẠCH</div></div>                                                                                |  |                            |  | <div><div>1. BẠC THANG XÂY GẠCH RỒNG 2 LỖ</div><div>2. BÀN THANG BTCT (XEM BVKC)</div></div> <div></div>   |  |
|    |  | NC1   |  | CHI TIẾT NGẠCH CỬA MỞ RA (ĐIỂN HÌNH)   |  | NC2   |  | CHI TIẾT NGẠCH CỬA CUỐN (ĐIỂN HÌNH)   |  |   |  | TỔNG GIÁM ĐỐC:             |  | TRẦN ĐỨC AN   |  |
|    |  |   |  | <div><div></div><div>TẦNG 1<br/>+0.000</div><div>CỬA NHÔM KÍNH</div><div>ÔP ĐÁ GRANITE ĐEN TẠO DỐC RA NGOÀI</div><div>TRÁT VỮA SƠN NƯỚC HOÀN THIỆN</div><div>SÂN TRƯỚC (SAU)</div></div> |  |   |  | <div><div></div><div>TẦNG 1<br/>+0.000</div><div>CỬA CUỐN</div><div>ÔP ĐÁ GRANITE ĐEN TẠO DỐC RA NGOÀI</div><div>ÔP ĐÁ GRANITE ĐEN</div><div>SÂN TRƯỚC</div></div>   |  |   |  | CHỦ NHIỆM DỰ ÁN:           |  |   |  |
|    |  |   |  | NC3   |  | CHI TIẾT NGẠCH CỬA MỞ RA SÂN THƯỢNG (ĐIỂN HÌNH)   |  | NC4   |  | CHI TIẾT NGẠCH CỬA TRƯỢT SÂN THƯỢNG - BAN CÔNG (ĐIỂN HÌNH)   |  | KTS. NGUYỄN THÀNH THÁI     |  | CHỦ TRÌ THIẾT KẾ:   |  |
|    |  |   |  | <div><div></div><div>TẦNG 3<br/>+9.800</div><div>ÔP ĐÁ GRANITE ĐEN</div><div>TƯỜNG</div><div>CỬA ĐI</div><div>SÂN THƯỢNG</div><div>DẪM BTCT (XEM BVKC)</div></div>                       |  |   |  | <div><div></div><div>CỬA TRƯỢT 2 CẢNH</div><div>TƯỜNG</div><div>ĐÁ GRANITE ĐEN</div><div>BÀN SÀN BTCT (XEM BVKC)</div><div>DẪM BTCT (XEM BVKC)</div><div>SÂN HOÀN THIỆN BAN CÔNG/ SÂN THƯỢNG (XEM BẢN VẼ HOÀN THIỆN SÀN)</div><div>BÀN SÀN BTCT (XEM BVKC)</div></div> |  |   |  | KTS. NGUYỄN THÀNH THÁI     |  | THIẾT KẾ:   |  |
|    |  |   |  |   |  |   |  |   |  |   |  | KTS. LÊ ĐÌNH TÂM           |  | KIỂM TRA:   |  |
|    |  |   |  |   |  |   |  |   |  |   |  | KTS. NGUYỄN ĐỨC THÁI       |  |   |  |
|    |  |   |  |   |  |   |  |   |  |   |  | DỰ ÁN:                     |  | KHU DÂN CƯ A1-C1 (ĐÔ THỊ DẦU GIẤY)   |  |
|    |  |   |  |   |  |   |  |   |  |   |  |                            |  | ĐỊA ĐIỂM: XÃ DẦU GIẤY, TỈNH ĐỒNG NAI   |  |
|    |  |   |  |   |  |   |  |   |  |   |  | CÔNG TRÌNH:                |  | NHÀ Ở THƯƠNG MẠI LIÊN KẾ   |  |
|    |  |   |  |   |  |   |  |   |  |   |  | HẠNG MỤC:                  |  | MẪU NHÀ T3-2b   |  |
|    |  |   |  |   |  |   |  |   |  |   |  | TÊN BẢN VẼ:                |  | BẢNG GHI CHÚ CẤU TẠO VẬT LIỆU HOÀN THIỆN TỜ 1   |  |
|    |  |   |  |   |  |   |  |   |  |   |  | MỤC ĐÍCH PHÁT HÀNH:        |  |   |  |
|    |  |   |  |   |  |   |  |   |  |   |  | BẢN VẼ MỜI THẦU            |  |   |  |
|    |  |   |  |   |  |   |  |   |  |   |  | THIẾT KẾ CƠ SỞ             |  |   |  |
|    |  |   |  |   |  |   |  |   |  |   |  | ✓ THIẾT KẾ BẢN VẼ THI CÔNG |  |   |  |
|    |  |   |  |   |  |   |  |   |  |   |  | BẢN VẼ HOÀN CÔNG           |  |   |  |
|    |  |   |  |   |  |   |  |   |  |   |  | HOÀN THÀNH                 |  | 07/2025   |  |
|    |  |   |  |   |  |   |  |   |  |   |  | TỶ LỆ                      |  | NTS   |  |
|    |  |   |  |   |  |   |  |   |  |   |  | SỐ HIỆU BẢN VẼ             |  | A00-02   |  |

BẢNG GHI CHÚ VẬT LIỆU HOÀN THIỆN TƯỜNG
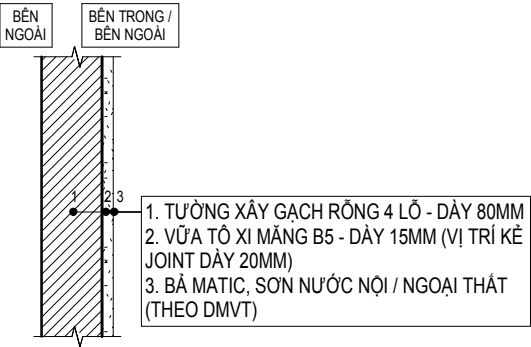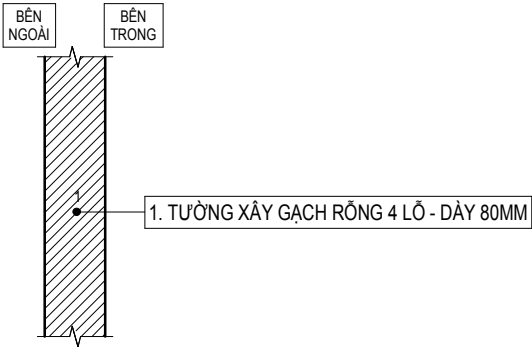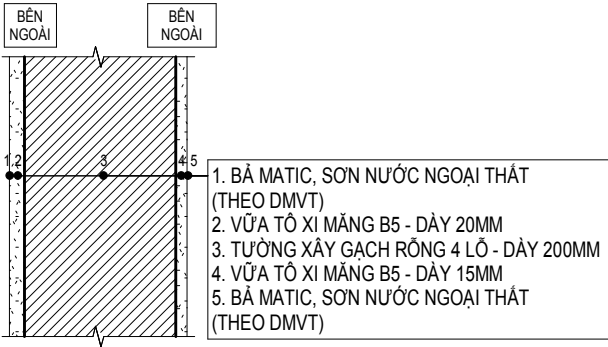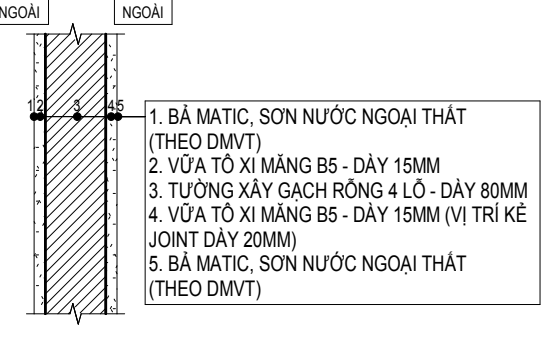
|                                                                                   |                                         |                                                                                    |                                         |                                                                                     |                                          |                                                                                     |                                                |
|-----------------------------------------------------------------------------------|-----------------------------------------|------------------------------------------------------------------------------------|-----------------------------------------|-------------------------------------------------------------------------------------|------------------------------------------|-------------------------------------------------------------------------------------|------------------------------------------------|
| <b>W01</b>                                                                        | <b>TƯỜNG BAO - 95, HOÀN THIỆN 1 MẶT</b> | <b>W01a</b>                                                                        | <b>TƯỜNG BAO - 80, KHÔNG HOÀN THIỆN</b> | <b>W02</b>                                                                          | <b>TƯỜNG BAO - 235, HOÀN THIỆN 2 MẶT</b> | <b>W04</b>                                                                          | <b>TƯỜNG BAO - 110 / 115, HOÀN THIỆN 2 MẶT</b> |
| GHI CHÚ: TƯỜNG NGĂN GIỮA CÁC NHÀ LIỀN KẾ, TƯỜNG HỘP GEN                           |                                         | GHI CHÚ: TƯỜNG HỘP GEN GIÁP CÁC CĂN LIỀN KẾ                                        |                                         |                                                                                     |                                          |                                                                                     |                                                |
|  |                                         |  |                                         |  |                                          |  |                                                |

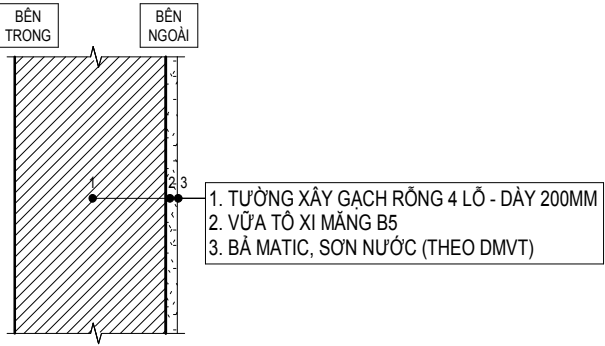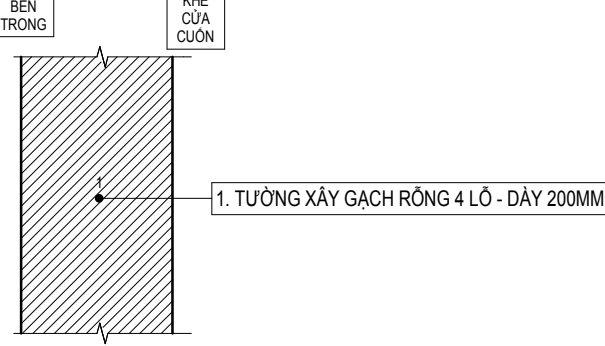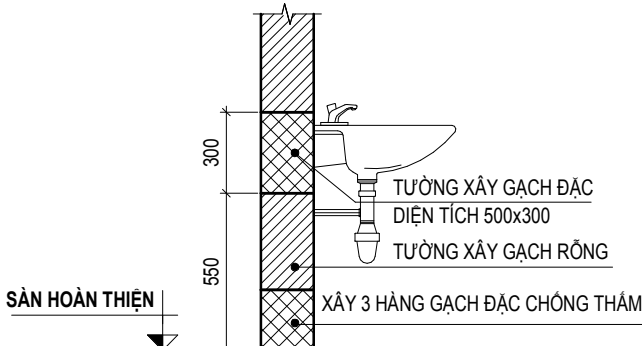
|                                                                                    |                                          |                                                                                      |                                      |                                                                                      |                                |
|------------------------------------------------------------------------------------|------------------------------------------|--------------------------------------------------------------------------------------|--------------------------------------|--------------------------------------------------------------------------------------|--------------------------------|
| <b>W09</b>                                                                         | <b>TƯỜNG BAO - 220, HOÀN THIỆN 1 MẶT</b> | <b>W09a</b>                                                                          | <b>TƯỜNG - 200, KHÔNG HOÀN THIỆN</b> | <b>T1</b>                                                                            | <b>TƯỜNG VỊ TRÍ LẮP LAVABO</b> |
|  |                                          |  |                                      |  |                                |
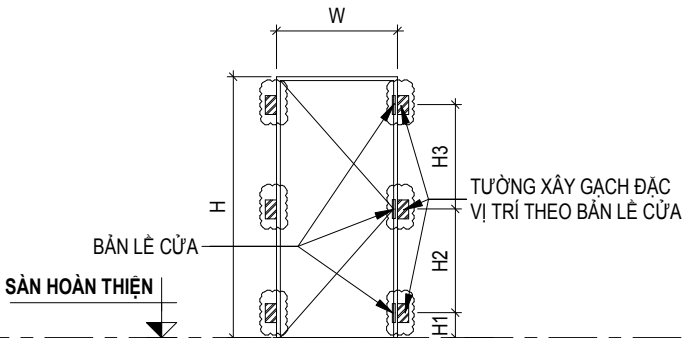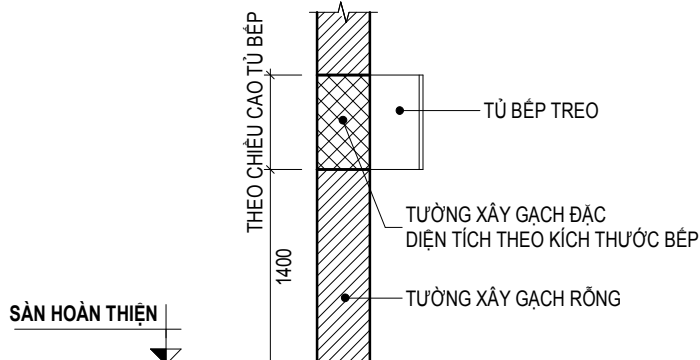
|                                                                                     |                                |                                                                                      |                                |
|-------------------------------------------------------------------------------------|--------------------------------|--------------------------------------------------------------------------------------|--------------------------------|
| <b>T2</b>                                                                           | <b>TƯỜNG VỊ TRÍ LẮP CỬA ĐI</b> | <b>T3</b>                                                                            | <b>TƯỜNG VỊ TRÍ LẮP TỦ BẾP</b> |
|  |                                |  |                                |

- TẤT CẢ CÁC LOẠI TƯỜNG PHẢI XÂY 3 HÀNG GẠCH RỒNG 2 LỖ (GẠCH THỂ) DƯỚI CHÂN TƯỜNG, NGOẠI TRỪ TRƯỜNG HỢP CÓ GHI CHÚ CHI TIẾT.  
- TẤT CẢ CÁC LOẠI TƯỜNG ĐÔI ( CHIỀU RỘNG TƯỜNG ≥ 200MM) CÁCH 5 HÀNG GẠCH ĐỌC THÌ PHẢI CÓ 1 LỖP HÀNG GẠCH RỒNG 2 LỖ (GẠCH THỂ) QUAY NGANG.  
- PHẢI THỰC HIỆN BẢN VẼ SHOPDRAWING TƯỜNG XÂY TRƯỚC KHI THI CÔNG.

|   |          |
|---|----------|
| GHI CHÚ:<br>- CÁC ĐƠN VỊ THI CÔNG PHẢI PHỐI HỢP BẢN VẼ CỦA TẤT CẢ CÁC BỘ MÔN KHÁC NẾU THẤY SỰ KHÁC BIỆT PHẢI BÁO CHO ĐƠN VỊ THIẾT KẾ XỬ LÝ.<br>- KHU XỬ LÝ SỰ KHÁC BIỆT, PHẢI THỰC HIỆN ƯU TIÊN THEO THỨ TỰ GIỮA CÁC BỘ MÔN: KIẾN TRÚC → KẾT CẤU / BỘ MÔN KHÁC; HOẶC ƯU TIÊN TRONG CÙNG BỘ MÔN: CHI TIẾT → TỔNG THỂ<br>- CÁC SỐ LIỆU KÍCH THƯỚC PHẢI ĐƯỢC KIỂM TRA THỰC TẾ TẠI CÔNG TRÌNH, NẾU THẤY SỰ KHÁC BIỆT SƠ VỚI BẢN VẼ THI PHẢI BÁO CHO ĐƠN VỊ THIẾT KẾ. |          |
| HIỆU CHỈNH:   |          |
| REV   | NỘI DUNG |
| CHỦ ĐẦU TƯ:<br>CÔNG TY TNHH ĐẦU TƯ<br><b>PHÚ VIỆT TÍN</b><br>ĐỊA CHỈ: LÔ 18-19 QUỐC LỘ 1A, XÃ DẦU GIẤY, TỈNH ĐỒNG NAI, VIỆT NAM   |          |
| CTHĐT.V: ĐẶNG PHƯỚC BÌNH   |          |
| ĐƠN VỊ THIẾT KẾ:<br>CÔNG TY CỔ PHẦN TƯ VẤN THIẾT KẾ<br><b>BASE ARC</b><br>ĐỊA CHỈ: 138 ĐIỆN BIÊN PHỦ, PHƯỜNG TÂN ĐỊNH, TP. HỒ CHÍ MINH, VIỆT NAM   |          |
| TỔNG GIÁM ĐỐC: TRẦN ĐỨC AN   |          |
| CHỦ NHIỆM DỰ ÁN:   |          |
| KTS. NGUYỄN THÀNH THÁI   |          |
| CHỦ TRÌ THIẾT KẾ:   |          |
| KTS. NGUYỄN THÀNH THÁI   |          |
| THIẾT KẾ:   |          |
| KTS. LÊ ĐÌNH TÂM   |          |
| KIỂM TRA:   |          |
| KTS. NGUYỄN ĐỨC THÁI   |          |
| DỰ ÁN:<br>KHU DÂN CƯ A1-C1 (ĐÔ THỊ DẦU GIẤY)<br>ĐỊA ĐIỂM: XÃ DẦU GIẤY, TỈNH ĐỒNG NAI   |          |
| CÔNG TRÌNH:<br>NHÀ Ở THƯƠNG MẠI LIỀN KẾ   |          |
| HẠNG MỤC:<br>MẪU NHÀ T3-2b   |          |
| TÊN BẢN VẼ:<br>BẢNG GHI CHÚ CẤU TẠO VẬT LIỆU HOÀN THIỆN TỶ 2   |          |
| MỤC ĐÍCH PHÁT HÀNH:   |          |
| BẢN VẼ MỜI THẦU   |          |
| THIẾT KẾ CƠ SỞ   |          |
| ✓ THIẾT KẾ BẢN VẼ THI CÔNG   |          |
| BẢN VẼ HOÀN CÔNG   |          |
| HOÀN THÀNH   | 07/2025  |
| TỶ LỆ   | NTS      |
| SỐ HIỆU BẢN VẼ   | A00-03   |

CẤU TẠO TƯỜNG

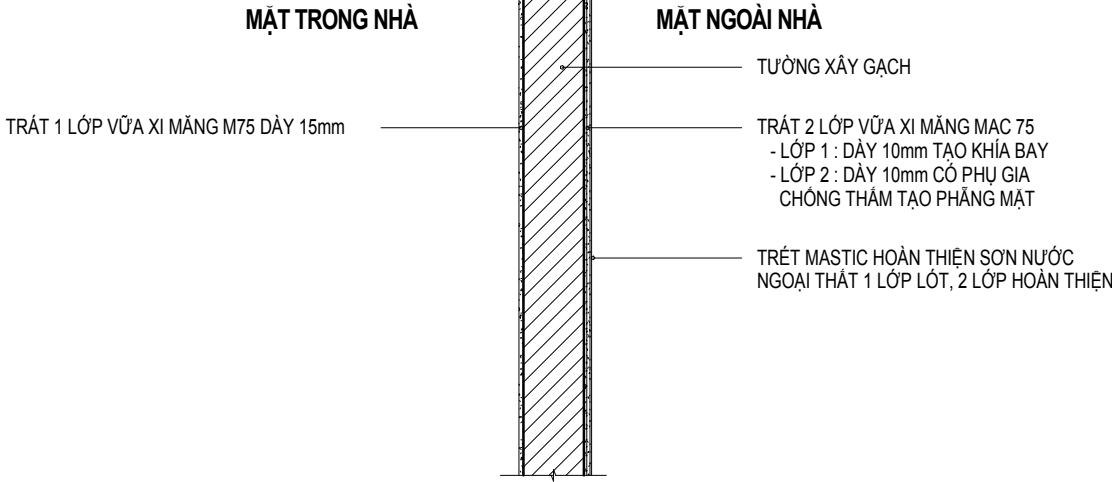


GHI CHÚ:  
- CÁC ĐƠN VỊ THI CÔNG PHẢI PHỐI HỢP BẢN VẼ CỦA TẤT CẢ CÁC BỘ MÔN KHÁC NẾU THẤY SỰ KHÁC BIỆT PHẢI BẢO CHO ĐƠN VỊ THIẾT KẾ ĐỂ XỬ LÝ.  
- KHI XỬ LÝ SỰ KHÁC BIỆT, PHẢI THỰC HIỆN ƯU TIÊN THEO THỨ TỰ GIỮA CÁC BỘ MÔN: KIẾN TRÚC → KẾT CẤU / BỘ MÔN KHÁC; HOẶC ƯU TIÊN TRONG CÙNG BỘ MÔN: CHI TIẾT → TỔNG THỂ  
- CÁC SỐ LIEU KÍCH THƯỚC PHẢI ĐƯỢC KIỂM TRA THỰC TẾ TẠI CÔNG TRÌNH, NẾU THẤY SỰ KHÁC BIỆT SƠ VỚI BẢN VẼ THI PHẢI BẢO CHO ĐƠN VỊ THIẾT KẾ.


| HIỆU CHỈNH: |      |          |
|-------------|------|----------|
| REV         | NGÀY | NỘI DUNG |

CHỦ ĐẦU TƯ:  
CÔNG TY TNHH ĐẦU TƯ  
**PHÚ VIỆT TÍN**  
ĐỊA CHỈ: LÔ 18-19 QUỐC LỘ 1A, XÃ DẦU GIẤY,  
TỈNH ĐỒNG NAI, VIỆT NAM

CHI TIẾT TƯỜNG XÂY 200 CÓ CỬA ĐI

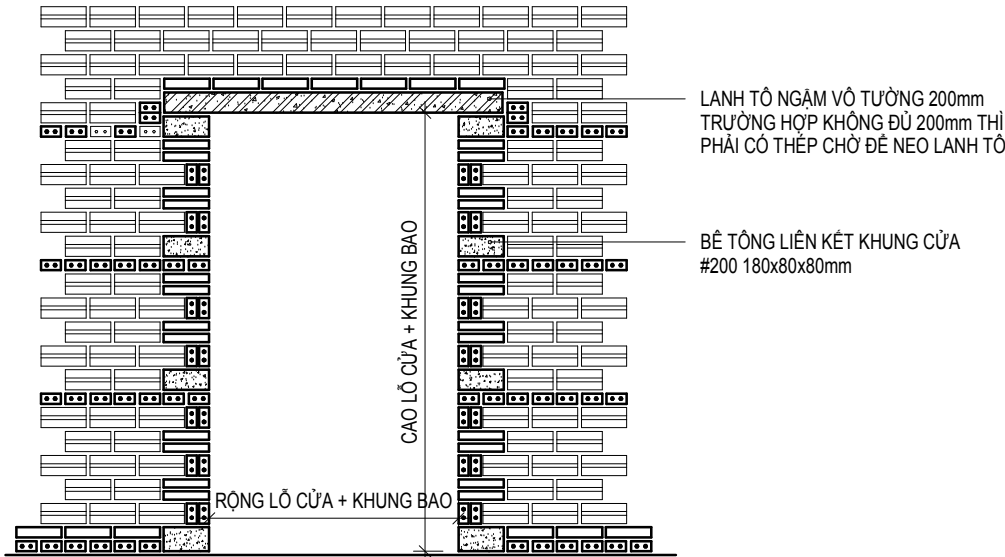

CHI TIẾT TƯỜNG XÂY 200 CÓ CỬA SỔ

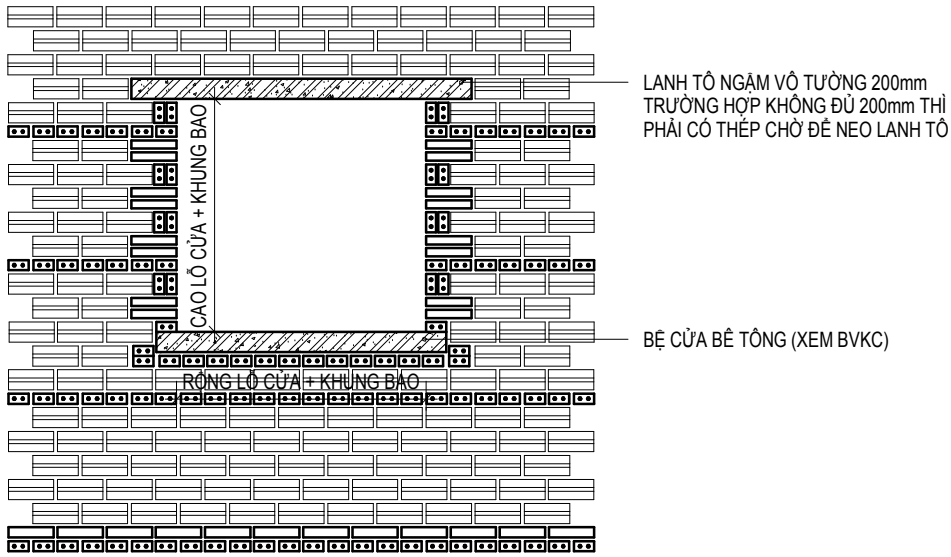


CTHĐTV: ĐẶNG PHƯỚC BÌNH

ĐƠN VỊ THIẾT KẾ:  
CÔNG TY CỔ PHẦN TƯ VẤN THIẾT KẾ  
**BASE ARC**  
ĐỊA CHỈ: 138 ĐIỆN BIÊN PHỦ, PHƯỜNG TÂN ĐỊNH,  
TP. HỒ CHÍ MINH, VIỆT NAM

TỔNG GIÁM ĐỐC: TRẦN ĐỨC AN  
CHỦ NHIỆM DỰ ÁN:  
KTS. NGUYỄN THÀNH THÁI  
CHỦ TRÌ THIẾT KẾ:  
KTS. NGUYỄN THÀNH THÁI  
THIẾT KẾ:  
KTS. LÊ ĐÌNH TÂM  
KIỂM TRA:  
KTS. NGUYỄN ĐỨC THÁI

CHI TIẾT XÂY TƯỜNG

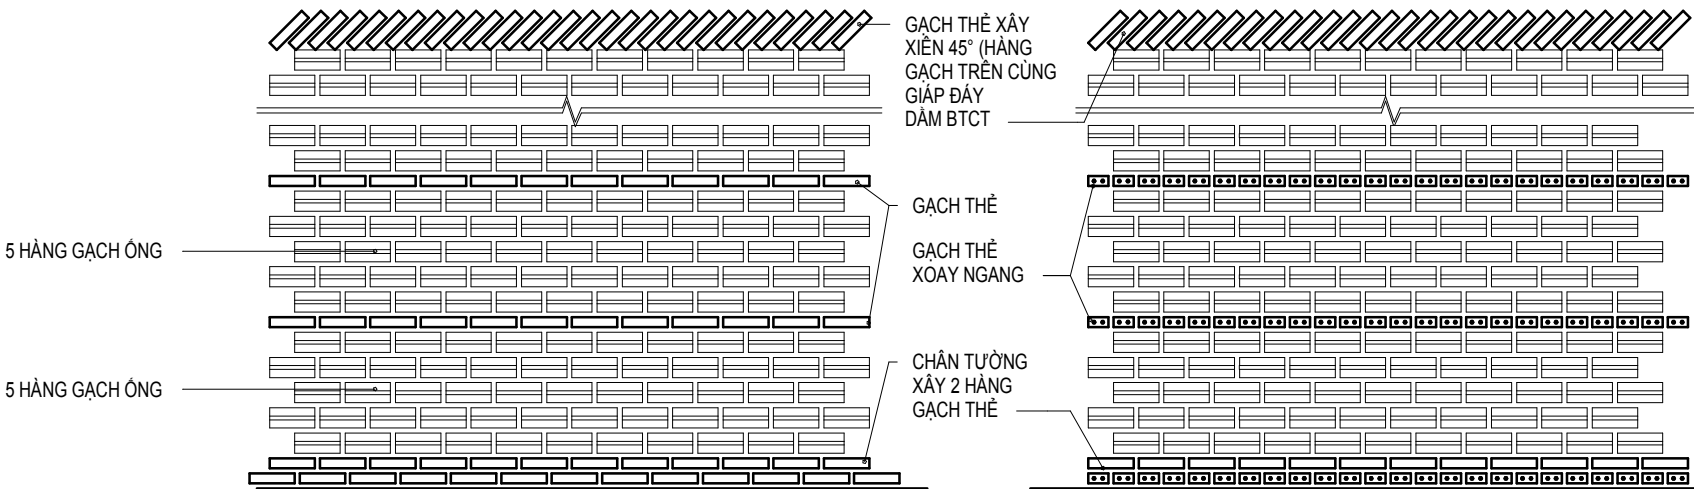

CHI TIẾT ĐIỂN HÌNH XÂY TƯỜNG 100mm

CHI TIẾT ĐIỂN HÌNH XÂY TƯỜNG 200mm

DỰ ÁN:  
KHU DÂN CƯ A1-C1 (ĐÔ THỊ DẦU GIẤY)  
ĐỊA ĐIỂM: XÃ DẦU GIẤY, TỈNH ĐỒNG NAI


CÔNG TRÌNH:  
NHÀ Ở THƯƠNG MẠI LIÊN KẾ

HẠNG MỤC:  
MẪU NHÀ T3-2b

TÊN BẢN VẼ:  
CHI TIẾT CẤU TẠO


| MỤC ĐÍCH PHÁT HÀNH:                                          |         |
|--------------------------------------------------------------|---------|
| <input type="checkbox"/> BẢN VẼ MỜI THẦU                     |         |
| <input type="checkbox"/> THIẾT KẾ CƠ SỞ                      |         |
| <input checked="" type="checkbox"/> THIẾT KẾ BẢN VẼ THI CÔNG |         |
| <input type="checkbox"/> BẢN VẼ HOÀN CÔNG                    |         |
| HOÀN THÀNH                                                   | 07/2025 |
| TỶ LỆ                                                        | NTS     |
| SỐ HIỆU BẢN VẼ                                               | A00-06  |

CHI TIẾT ỐP LƯỚI CHỐNG NÚT

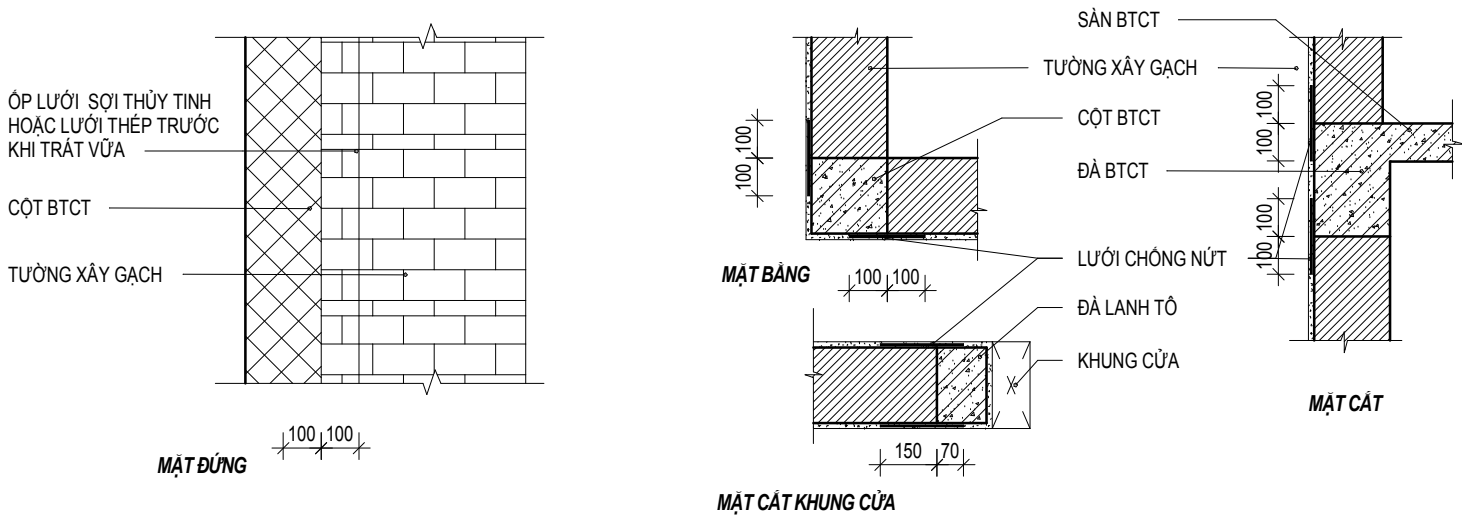

- CÁC VỊ TRÍ CẦN ĐÓNG LƯỚI CHỐNG NÚT :
- VỊ TRÍ TIẾP GIÁP GIỮA 2 KẾT CẤU BĂNG VẬT LIỆU KHÁC NHAU.
  - VỊ TRÍ CÁC ĐẦU CỬA ĐI, CỬA SÔ

CHI TIẾT TẮM TRẦN CEMBOARD

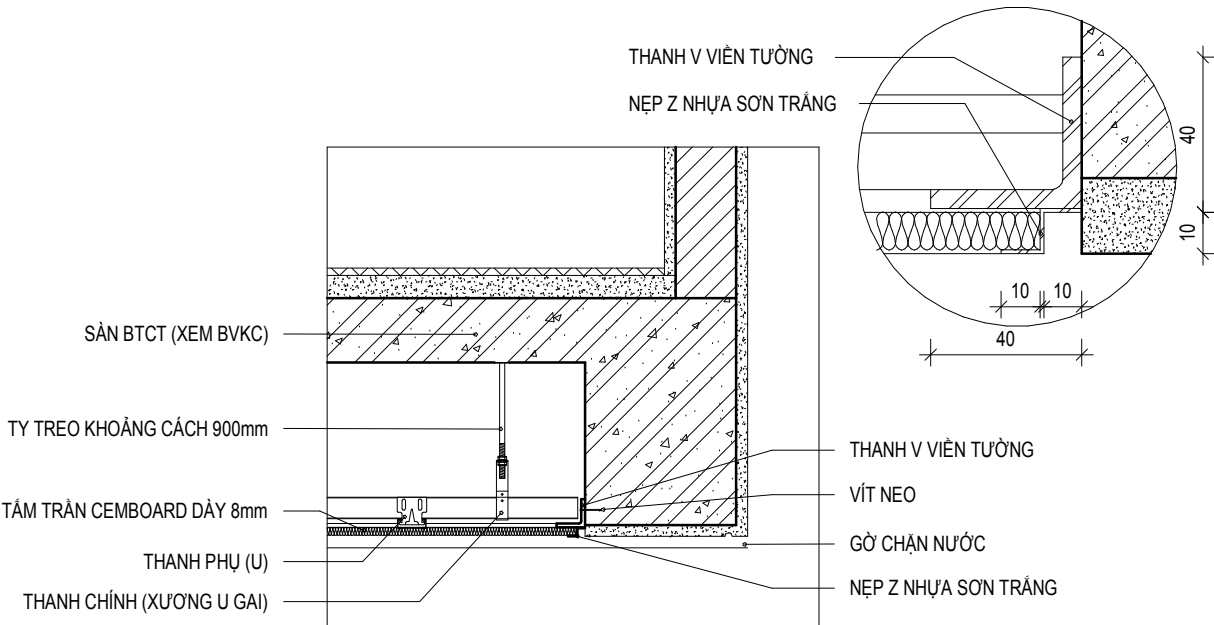

GHI CHÚ:  
- CÁC ĐƠN VỊ THI CÔNG PHẢI PHỐI HỢP BẢN VẼ CỦA TẤT CẢ CÁC BỘ MÔN KHÁC NẾU THẤY SỰ KHÁC BIỆT PHẢI BẢO CHO ĐƠN VỊ THIẾT KẾ ĐỀ XỬ LÝ.  
- KHI XỬ LÝ SỰ KHÁC BIỆT, PHẢI THỰC HIỆN ƯU TIÊN THEO THỨ TỰ GIỮA CÁC BỘ MÔN: KIẾN TRÚC → KẾT CẤU / BỘ MÔN KHÁC; HOẶC ƯU TIÊN TRONG CÙNG BỘ MÔN: CHI TIẾT → TỔNG THỂ  
- CÁC SỐ LIỆU KÍCH THƯỚC PHẢI ĐƯỢC KIỂM TRA THỰC TẾ TẠI CÔNG TRÌNH, NẾU THẤY SỰ KHÁC BIỆT SƠ VỚI BẢN VẼ THI PHẢI BẢO CHO ĐƠN VỊ THIẾT KẾ.

HIỆU CHỈNH:  
REV | NGÀY | NỘI DUNG

CHỦ ĐẦU TƯ:  
CÔNG TY TNHH ĐẦU TƯ  
**PHÚ VIỆT TÍN**  
ĐỊA CHỈ: LÔ 18-19 QUỐC LỘ 1A, XÃ DẦU GIẤY,  
TỈNH ĐỒNG NAI, VIỆT NAM

CTHĐT.V: ĐẶNG PHƯỚC BÌNH

ĐƠN VỊ THIẾT KẾ:  
CÔNG TY CỔ PHẦN TƯ VẤN THIẾT KẾ  
**BASE ARC**  
ĐỊA CHỈ: 138 ĐIỆN BIÊN PHỦ, PHƯỜNG TÂN ĐỊNH,  
TP. HỒ CHÍ MINH, VIỆT NAM

TỔNG GIÁM ĐỐC: TRẦN ĐỨC AN

CHỦ NHIỆM DỰ ÁN:

KTS. NGUYỄN THÀNH THÁI

CHỦ TRÌ THIẾT KẾ:

KTS. NGUYỄN THÀNH THÁI

THIẾT KẾ:

KTS. LÊ ĐÌNH TÂM

KIỂM TRA:

KTS. NGUYỄN ĐỨC THÁI

DỰ ÁN:

KHU DÂN CƯ A1-C1 (ĐÔ THỊ DẦU GIẤY)  
ĐỊA ĐIỂM: XÃ DẦU GIẤY, TỈNH ĐỒNG NAI

CÔNG TRÌNH:

NHÀ Ở THƯƠNG MẠI LIÊN KẾ

HẠNG MỤC:

MẪU NHÀ T3-2b

TÊN BẢN VẼ:

CHI TIẾT CẤU TẠO

MỤC ĐÍCH PHÁT HÀNH:

BẢN VẼ MỜI THẦU

THIẾT KẾ CƠ SỞ

✓ THIẾT KẾ BẢN VẼ THI CÔNG

BẢN VẼ HOÀN CÔNG


HOÀN THÀNH 07/2025

TỶ LỆ NTS

SỐ HIỆU BẢN VẼ A00-07

# KHU DÂN CƯ A1-C1 (ĐÔ THỊ DẦU GIẦY)

ĐỊA ĐIỂM: XÃ DẦU GIẦY, TỈNH ĐỒNG NAI

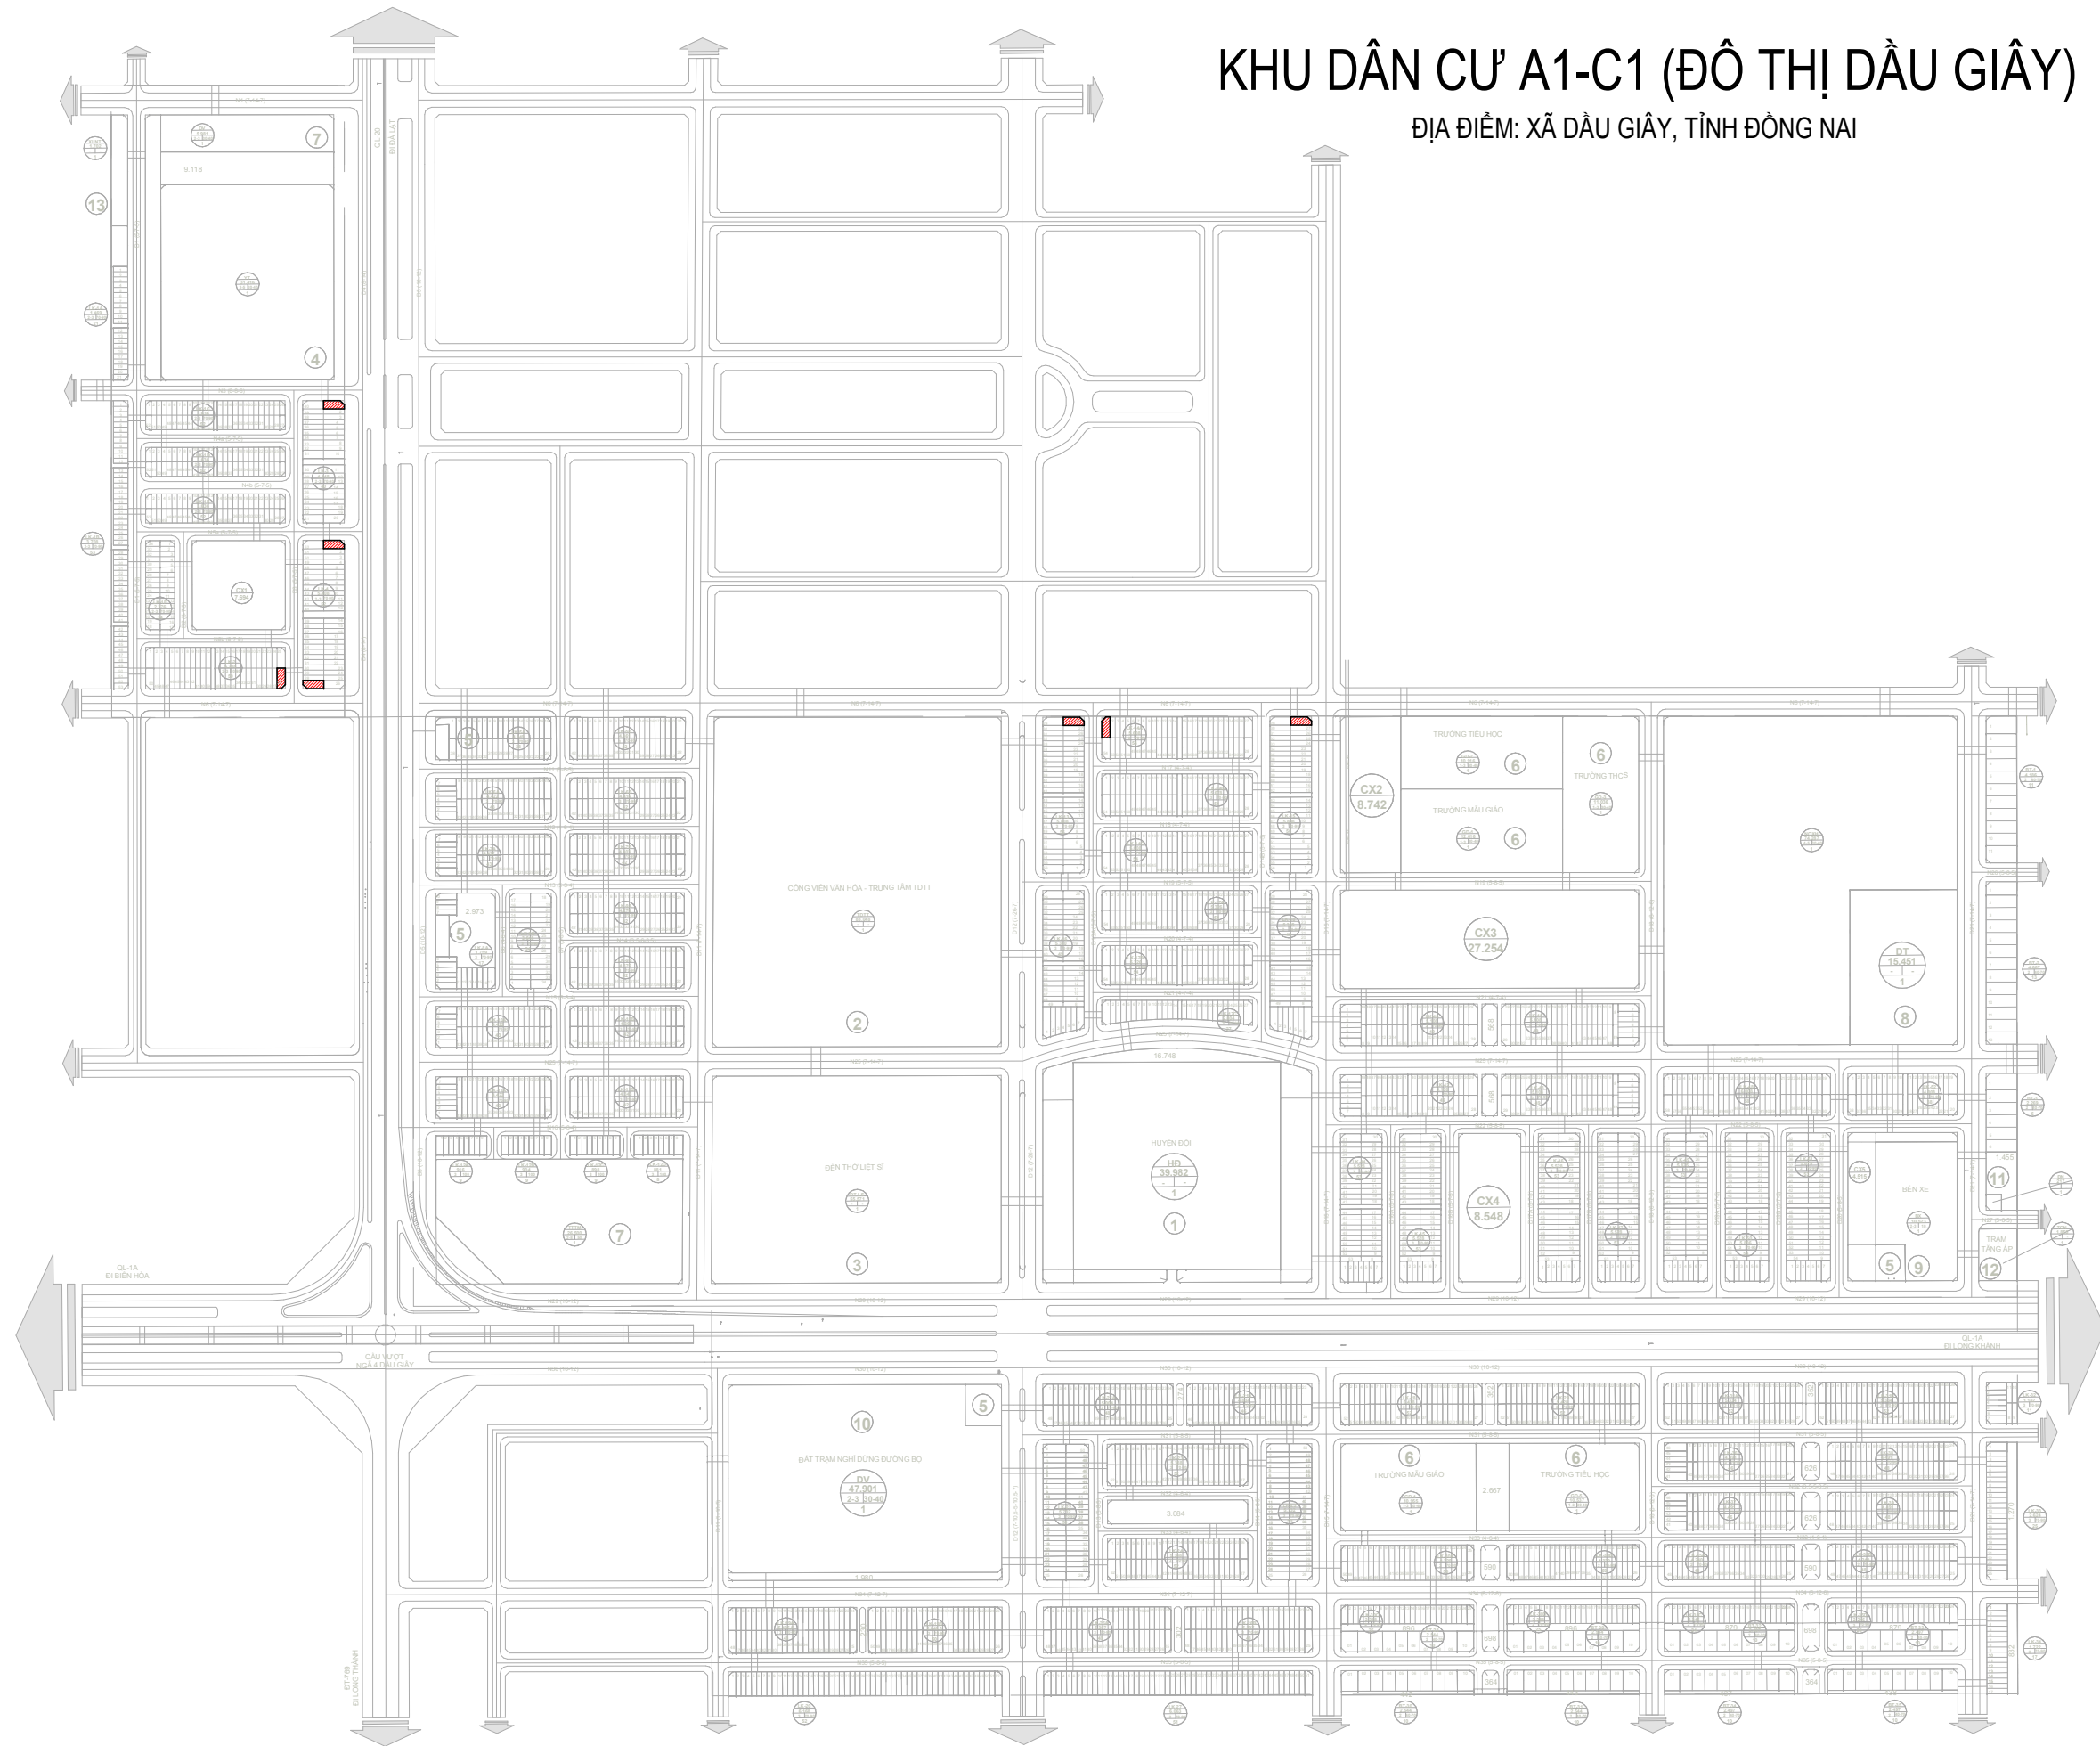

MẶT BẰNG VỊ TRÍ MẪU NHÀ



VỊ TRÍ MẪU NHÀ

## GHI CHÚ:

- CÁC ĐƠN VỊ THI CÔNG PHẢI PHỐI HỢP BẢN VẼ CỦA TẤT CẢ CÁC BỘ MÔN KHÁC NẾU THẤY SỰ KHÁC BIỆT PHẢI BẢO CHỨNG CHO ĐƠN VỊ THIẾT KẾ XỬ LÝ.
- KHI XỬ LÝ SỰ KHÁC BIỆT, PHẢI THỰC HIỆN ƯU TIÊN THEO THỨ TỰ GIỮA CÁC BỘ MÔN: KIẾN TRÚC → KẾT CẤU / BỘ MÔN KHÁC; HOẶC ƯU TIÊN TRONG CÙNG BỘ MÔN: CHI TIẾT → TỔNG THỂ.
- CÁC SỐ LIỆU KÍCH THƯỚC PHẢI ĐƯỢC KIỂM TRA THỰC TẾ TẠI CÔNG TRÌNH, NẾU THẤY SỰ KHÁC BIỆT SƠ VỚI BẢN VẼ THI PHẢI BÁO CHO ĐƠN VỊ THIẾT KẾ.

## HIỆU CHỈNH:

| REV | NGÀY | NỘI DUNG |
|-----|------|----------|
|-----|------|----------|

## CHỦ ĐẦU TƯ:

CÔNG TY TNHH ĐẦU TƯ

**PHÚ VIỆT TÍN**

ĐỊA CHỈ: LÔ 18-19 QUỐC LỘ 1A, XÃ DẦU GIẦY,  
TỈNH ĐỒNG NAI, VIỆT NAM

## CTHĐT:

ĐẶNG PHƯỚC BÌNH

## ĐƠN VỊ THIẾT KẾ:

CÔNG TY CỔ PHẦN TƯ VẤN THIẾT KẾ

**BASE ARC**

ĐỊA CHỈ: 138 ĐIỆN BIÊN PHỦ, PHƯỜNG TÂN ĐỊNH,  
TP. HỒ CHÍ MINH, VIỆT NAM

## TỔNG GIÁM ĐỐC:

TRẦN ĐỨC AN

## CHỦ NHIỆM DỰ ÁN:

KTS. NGUYỄN THÀNH THÁI

## CHỦ TRÌ THIẾT KẾ:

KTS. NGUYỄN THÀNH THÁI

## THIẾT KẾ:

KTS. LÊ ĐÌNH TÂM

## KIỂM TRA:

KTS. NGUYỄN ĐỨC THÁI

## DỰ ÁN:

KHU DÂN CƯ A1-C1 (ĐÔ THỊ DẦU GIẦY)

ĐỊA ĐIỂM: XÃ DẦU GIẦY, TỈNH ĐỒNG NAI

## CÔNG TRÌNH:

NHÀ Ở THƯƠNG MẠI LIÊN KẾ

## HẠNG MỤC:

MẪU NHÀ T3-2b

## TÊN BẢN VẼ:

MẶT BẰNG VỊ TRÍ MẪU NHÀ

## MỤC ĐÍCH PHÁT HÀNH:

|                                     |                          |
|-------------------------------------|--------------------------|
| <input type="checkbox"/>            | BẢN VẼ MỜI THẦU          |
| <input type="checkbox"/>            | THIẾT KẾ CƠ SỞ           |
| <input checked="" type="checkbox"/> | THIẾT KẾ BẢN VẼ THI CÔNG |
| <input type="checkbox"/>            | BẢN VẼ HOÀN CÔNG         |

|                |         |
|----------------|---------|
| HOÀN THÀNH     | 07/2025 |
| TỶ LỆ          | NTS     |
| SỐ HIỆU BẢN VẼ | A01-01  |

BẢNG THÔNG SỐ LÔ ĐẤT

| STT | VỊ TRÍ LÔ | Ô ĐẤT SỐ | DIỆN TÍCH KHU ĐẤT (M2) | MỖXD (%) | DIỆN TÍCH TÍNH MỖXD (M2) | DTXD TẦNG 1 (M2) | DTXD TẦNG 2 (M2) | DTXD TẦNG 3 (M2) | TỔNG DTXD (M2) | TẦNG CAO XÂY DỰNG (TẦNG) | HSSDĐ (LẦN) | CAO ĐỘ COTE +0.000 THEO VN2000 |
|-----|-----------|----------|------------------------|----------|--------------------------|------------------|------------------|------------------|----------------|--------------------------|-------------|--------------------------------|
| 1   | LK-2      | 26       | 152                    | 79.48%   | 120.8                    | 111.8            | 119.3            | 108.6            | 339.7          | 3 tầng                   | 2.23        | 144.15                         |
| 2   | LKP-3     | 1        | 152                    | 79.48%   | 120.8                    | 111.8            | 119.3            | 108.6            | 339.7          | 3 tầng                   | 2.23        | 145.36                         |
| 3   | LKP- 4    | 1        | 152                    | 79.48%   | 120.8                    | 111.8            | 119.3            | 108.6            | 339.7          | 3 tầng                   | 2.23        | 146.04                         |
| 4   | LKP- 4    | 27       | 152                    | 79.48%   | 120.8                    | 111.8            | 119.3            | 108.6            | 339.7          | 3 tầng                   | 2.23        | 144.94                         |
| 5   | LKP-13    | 28       | 152                    | 79.48%   | 120.8                    | 111.8            | 119.3            | 108.6            | 339.7          | 3 tầng                   | 2.23        | 165.79                         |
| 6   | LKP-14A   | 1        | 152                    | 79.48%   | 120.8                    | 111.8            | 119.3            | 108.6            | 339.7          | 3 tầng                   | 2.23        | 166.46                         |
| 7   | LKP-15    | 28       | 152                    | 79.48%   | 120.8                    | 111.8            | 119.3            | 108.6            | 339.7          | 3 tầng                   | 2.23        | 170.43                         |

GHI CHÚ:  
- CÁC ĐƠN VỊ THI CÔNG PHẢI PHỐI HỢP BẢN VẼ CỦA TẤT CẢ CÁC BỘ MÔN KHÁC NẾU THẤY SỰ KHÁC BIỆT PHẢI BẢO CHO ĐƠN VỊ THIẾT KẾ XỬ LÝ.  
- KHI XỬ LÝ SỰ KHÁC BIỆT, PHẢI THỰC HIỆN ƯU TIÊN THEO THỨ TỰ GIỮA CÁC BỘ MÔN: KIẾN TRÚC → KẾT CẤU / BỘ MÔN KHÁC; HOẶC ƯU TIÊN TRONG CÙNG BỘ MÔN: CHI TIẾT → TỔNG THỂ  
- CÁC SỐ LƯU KÍCH THƯỚC PHẢI ĐƯỢC KIỂM TRA THỰC TẾ TẠI CÔNG TRÌNH, NẾU THẤY SỰ KHÁC BIỆT SƠ VỚI BẢN VẼ THI PHẢI BẢO CHO ĐƠN VỊ THIẾT KẾ.

HIỆU CHỈNH:

|     |      |          |
|-----|------|----------|
| REV | NGÀY | NỘI DUNG |
|     |      |          |

CHỦ ĐẦU TƯ:

CÔNG TY TNHH ĐẦU TƯ

PHÚ VIỆT TÍN

ĐỊA CHỈ: LÔ 18-19 QUỐC LỘ 1A, XÃ DẦU GIẤY, TỈNH ĐỒNG NAI, VIỆT NAM

CTHĐT:

ĐẶNG PHƯỚC BÌNH

ĐƠN VỊ THIẾT KẾ:

CÔNG TY CỔ PHẦN TƯ VẤN THIẾT KẾ

BASE ARC

ĐỊA CHỈ: 138 ĐIỆN BIÊN PHỦ, PHƯỜNG TÂN ĐỊNH, TP. HỒ CHÍ MINH, VIỆT NAM

TỔNG GIÁM ĐỐC:

TRẦN ĐỨC AN

CHỦ NHIỆM DỰ ÁN:

KTS. NGUYỄN THÀNH THÁI

CHỦ TRÌ THIẾT KẾ:

KTS. NGUYỄN THÀNH THÁI

THIẾT KẾ:

KTS. LÊ ĐÌNH TÂM

KIỂM TRA:

KTS. NGUYỄN ĐỨC THÁI

DỰ ÁN:

KHU DÂN CƯ A1-C1 (ĐÔ THỊ DẦU GIẤY)

ĐỊA ĐIỂM: XÃ DẦU GIẤY, TỈNH ĐỒNG NAI

CÔNG TRÌNH:

NHÀ Ở THƯƠNG MẠI LIÊN KẾ

HẠNG MỤC:

MẪU NHÀ T3-2b


TÊN BẢN VẼ:

BẢNG THÔNG SỐ LÔ ĐẤT

MỤC ĐÍCH PHÁT HÀNH:

|   |                          |
|---|--------------------------|
|   | BẢN VẼ MỜI THẦU          |
|   | THIẾT KẾ CƠ SỞ           |
| ✓ | THIẾT KẾ BẢN VẼ THI CÔNG |
|   | BẢN VẼ HOÀN CÔNG         |

|                |         |
|----------------|---------|
| HOÀN THÀNH     | 07/2025 |
| TỶ LỆ          | NTS     |
| SỐ HIỆU BẢN VẼ | A01-02  |

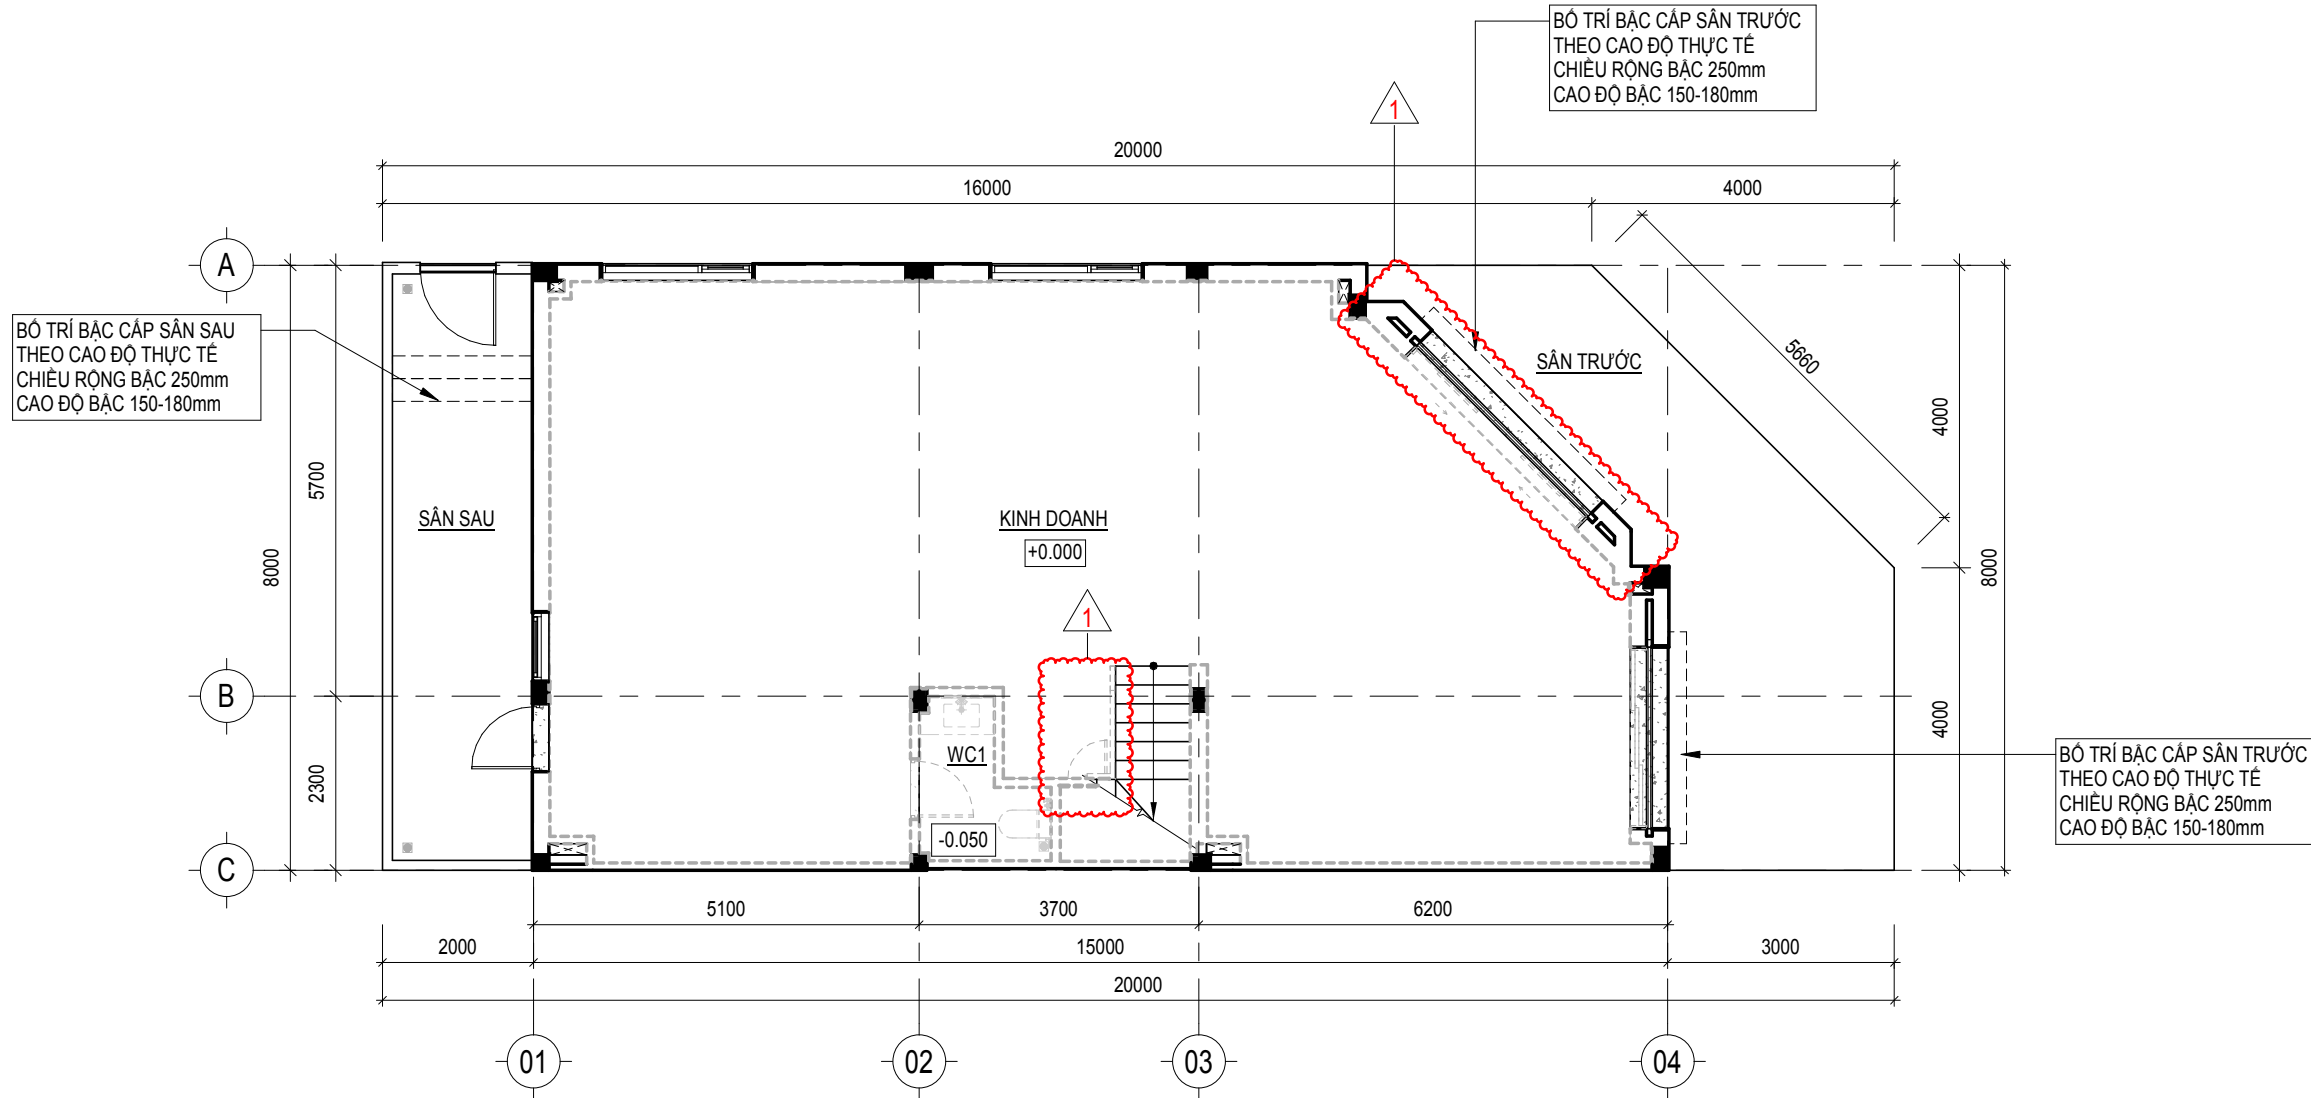

**MB ĐỊNH HƯỚNG CÔNG NĂNG TẦNG 1**  
TỶ LỆ 1 : 100

GHI CHÚ:  
- CÁC ĐƠN VỊ THI CÔNG PHẢI PHỐI HỢP BẢN VẼ CỦA TẤT CẢ CÁC BỘ MÔN  
KHÁC NẾU THẤY SỰ KHÁC BIỆT PHẢI BẢO CHỨNG ĐƠN VỊ THIẾT KẾ XỬ LÝ.  
- KHI XỬ LÝ SỰ KHÁC BIỆT, PHẢI THỰC HIỆN ƯU TIÊN THEO THỨ TỰ GIỮA CÁC  
BỘ MÔN: KIẾN TRÚC → KẾT CẤU / BỘ MÔN KHÁC; HOẶC ƯU TIÊN TRONG CÙNG  
BỘ MÔN: CHI TIẾT → TỔNG THỂ  
- CÁC SỐ LIỆU KÍCH THƯỚC PHẢI ĐƯỢC KIỂM TRA THỰC TẾ TẠI CÔNG TRÌNH,  
NẾU THẤY SỰ KHÁC BIỆT SƠ VỚI BẢN VẼ THI PHẢI BẢO CHỨNG ĐƠN VỊ THIẾT KẾ.

| HIỆU CHỈNH: |                                      |
|-------------|--------------------------------------|
| REV         | NỘI DUNG                             |
| 1           | 22/09/2024 ĐIỀU CHỈNH CỬA ĐI, CỬA SỐ |

CHỦ ĐẦU TƯ:  
CÔNG TY TNHH ĐẦU TƯ  
**PHÚ VIỆT TÍN**  
ĐỊA CHỈ: LÔ 18-19 QUỐC LỘ 1A, XÃ DẦU GIẤY,  
TỈNH ĐỒNG NAI, VIỆT NAM

CHỦ ĐẦU TƯ: ĐẶNG PHƯỚC BÌNH

ĐƠN VỊ THIẾT KẾ:  
CÔNG TY CỔ PHẦN TƯ VẤN THIẾT KẾ  
**BASE ARC**  
ĐỊA CHỈ: 138 ĐIỆN BIÊN PHỦ, PHƯỜNG TÂN ĐỊNH,  
TP. HỒ CHÍ MINH, VIỆT NAM

TỔNG GIÁM ĐỐC: TRẦN ĐỨC AN

CHỦ NHIỆM DỰ ÁN:

KTS. NGUYỄN THÀNH THÁI

CHỦ TRÌ THIẾT KẾ:

KTS. NGUYỄN THÀNH THÁI

THIẾT KẾ:

KTS. LÊ ĐÌNH TÂM

KIỂM TRA:

KTS. NGUYỄN ĐỨC THÁI

DỰ ÁN:

KHU DÂN CƯ A1-C1 (ĐÔ THỊ DẦU GIẤY)

ĐỊA ĐIỂM: XÃ DẦU GIẤY, TỈNH ĐỒNG NAI

CÔNG TRÌNH:

NHÀ Ở THƯƠNG MẠI LIÊN KẾ

HẠNG MỤC:

MẪU NHÀ T3-2b

TÊN BẢN VẼ:

MẶT BẰNG ĐỊNH HƯỚNG CÔNG NĂNG TẦNG 1

MỤC ĐÍCH PHÁT HÀNH:


|                                     |                          |
|-------------------------------------|--------------------------|
| <input type="checkbox"/>            | BẢN VẼ MỜI THẦU          |
| <input type="checkbox"/>            | THIẾT KẾ CƠ SỞ           |
| <input checked="" type="checkbox"/> | THIẾT KẾ BẢN VẼ THI CÔNG |
| <input type="checkbox"/>            | BẢN VẼ HOÀN CÔNG         |

HOÀN THÀNH 07/2025

TỶ LỆ NTS

SỐ HIỆU BẢN VẼ A02-01



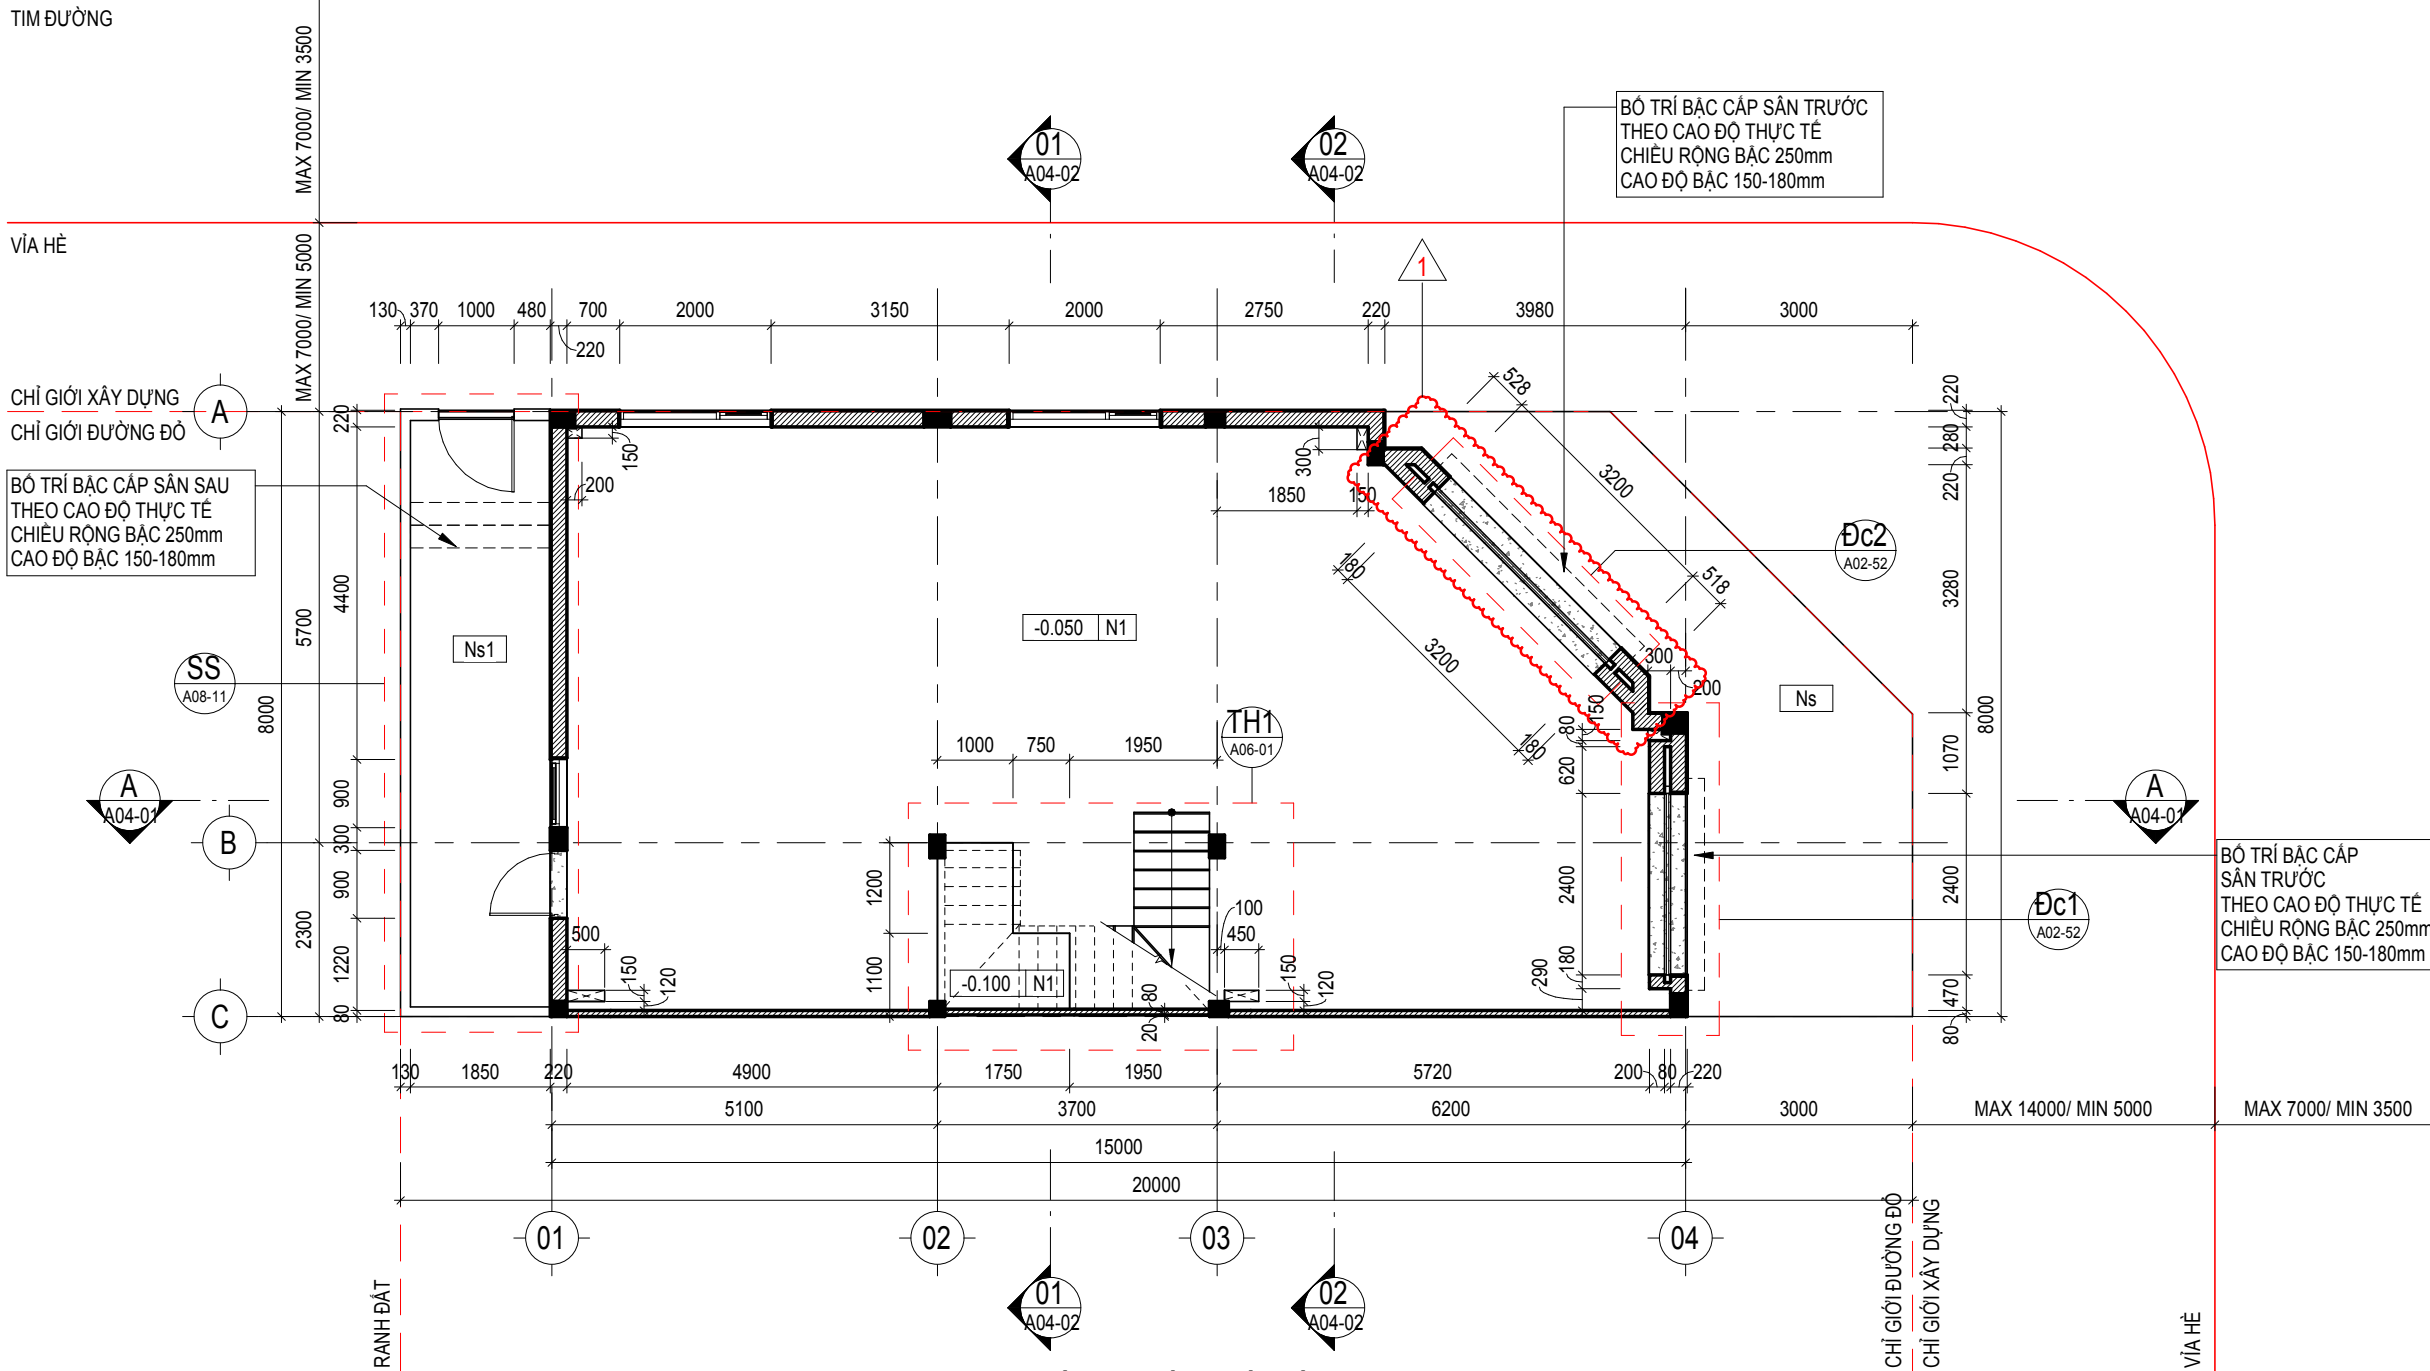

MẶT BẰNG XÂY TÔ TẦNG 1  
TỶ LỆ 1 : 100

GHI CHÚ:

- TẤT CẢ CÁC KÍCH THƯỚC PHẢI ĐƯỢC KIỂM TRA TẠI CÔNG TRƯỜNG TRƯỚC KHI THI CÔNG.

GHI CHÚ:

- CÁC ĐƠN VỊ THI CÔNG PHẢI PHỐI HỢP BẢN VẼ CỦA TẤT CẢ CÁC BỘ MÔN KHÁC NẾU THẤY SỰ KHÁC BIỆT PHẢI BẢO CHỨNG ĐƠN VỊ THIẾT KẾ XỬ LÝ.  
- KHI XỬ LÝ SỰ KHÁC BIỆT, PHẢI THỰC HIỆN ƯU TIÊN THEO THỨ TỰ GIỮA CÁC BỘ MÔN: KIẾN TRÚC → KẾT CẤU / BỘ MÔN KHÁC; HOẶC ƯU TIÊN TRONG CÙNG BỘ MÔN: CHI TIẾT → TỔNG THỂ  
- CÁC SỐ LIỆU KÍCH THƯỚC PHẢI ĐƯỢC KIỂM TRA THỰC TẾ TẠI CÔNG TRÌNH, NẾU THẤY SỰ KHÁC BIỆT SƠ VỚI BẢN VẼ THI PHẢI BẢO CHỨNG ĐƠN VỊ THIẾT KẾ.

HIỆU CHỈNH:

| REV | NGÀY       | NỘI DUNG                  |
|-----|------------|---------------------------|
| 1   | 22/09/2024 | ĐIỀU CHỈNH CỬA ĐI, CỬA SỔ |

CHỦ ĐẦU TƯ:

CÔNG TY TNHH ĐẦU TƯ

**PHÚ VIỆT TÍN**

ĐỊA CHỈ: LÔ 18-19 QUỐC LỘ 1A, XÃ DẦU GIẤY, TỈNH ĐỒNG NAI, VIỆT NAM

CTHĐT:

ĐẶNG PHƯỚC BÌNH

ĐƠN VỊ THIẾT KẾ:

CÔNG TY CỔ PHẦN TƯ VẤN THIẾT KẾ

**BASE ARC**

ĐỊA CHỈ: 138 ĐIỆN BIÊN PHỦ, PHƯỜNG TÂN ĐỊNH, TP. HỒ CHÍ MINH, VIỆT NAM

TỔNG GIÁM ĐỐC:

TRẦN ĐỨC AN

CHỦ NHIỆM DỰ ÁN:

KTS. NGUYỄN THÀNH THÁI

CHỦ TRÌ THIẾT KẾ:

KTS. NGUYỄN THÀNH THÁI

THIẾT KẾ:

KTS. LÊ ĐÌNH TÂM

KIỂM TRA:

KTS. NGUYỄN ĐỨC THÁI

DỰ ÁN:

KHU DÂN CƯ A1-C1 (ĐÔ THỊ DẦU GIẤY)

ĐỊA ĐIỂM: XÃ DẦU GIẤY, TỈNH ĐỒNG NAI

CÔNG TRÌNH:

NHÀ Ở THƯƠNG MẠI LIÊN KẾ

HẠNG MỤC:

MẪU NHÀ T3-2b

TÊN BẢN VẼ:

MẶT BẰNG XÂY TÔ TẦNG 1

MỤC ĐÍCH PHÁT HÀNH:

|                                     |                          |
|-------------------------------------|--------------------------|
| <input type="checkbox"/>            | BẢN VẼ MỜI THẦU          |
| <input type="checkbox"/>            | THIẾT KẾ CƠ SỞ           |
| <input checked="" type="checkbox"/> | THIẾT KẾ BẢN VẼ THI CÔNG |
| <input type="checkbox"/>            | BẢN VẼ HOÀN CÔNG         |



HOÀN THÀNH 07/2025

TỶ LỆ NTS

SỐ HIỆU BẢN VẼ A02-51

- TẤT CẢ CÁC KÍCH THƯỚC PHẢI ĐƯỢC KIỂM TRA TẠI CÔNG TRƯỜNG TRƯỚC KHI THI CÔNG.

**GHI CHÚ:**  
H: CAO ĐỘ SÂN THỰC TẾ  
h: CAO ĐỘ BẠC 150-180mm  
b: CHIỀU RỘNG BẠC 250mm

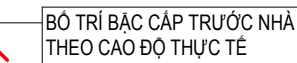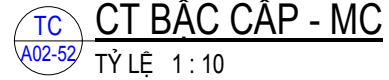





**CHI TIẾT KHE CỬA CUỐN Đc1 - MB**  
TỶ LỆ 1 : 35

|  |        |
|--|--------|
|  | A02-52 |
|--|--------|

**GHI CHÚ:**

- TẤT CẢ CÁC KÍCH THƯỚC PHẢI ĐƯỢC KIỂM TRA TẠI CÔNG TRƯỜNG TRƯỚC KHI THI CÔNG.

**GHI CHÚ:**

- CÁC ĐƠN VỊ THI CÔNG PHẢI PHỐI HỢP BẢN VẼ CỦA TẤT CẢ CÁC BỘ MÔN KHÁC NẾU THẤY SỰ KHÁC BIỆT PHẢI BÁO CHO ĐƠN VỊ THIẾT KẾ XỬ LÝ.  
- KHI XỬ LÝ SỰ KHÁC BIỆT, PHẢI THỰC HIỆN ƯU TIÊN THEO THỨ TỰ GIỮA CÁC BỘ MÔN: KIẾN TRÚC → KẾT CẤU / BỘ MÔN KHÁC; HOẶC ƯU TIÊN TRONG CÙNG BỘ MÔN: CHI TIẾT → TỔNG THỂ.  
- CÁC SỐ LƯU KÍCH THƯỚC PHẢI ĐƯỢC KIỂM TRA THỰC TẾ TẠI CÔNG TRÌNH, NẾU THẤY SỰ KHÁC BIỆT SƠ VỚI BẢN VẼ THI PHẢI BÁO CHO ĐƠN VỊ THIẾT KẾ.

**HIỆU CHỈNH:**

| REV | NGÀY       | NỘI DUNG                  |
|-----|------------|---------------------------|
| 1   | 22/09/2024 | ĐIỀU CHỈNH CỬA ĐI, CỬA SỐ |

**CHỦ ĐẦU TƯ:**

CÔNG TY TNHH ĐẦU TƯ  
**PHÚ VIỆT TÍN**  
ĐỊA CHỈ: LÔ 18-19 QUỐC LỘ 1A, XÃ DẦU GIẤY,  
TỈNH ĐỒNG NAI, VIỆT NAM

**CTHĐT:**

ĐẶNG PHƯỚC BÌNH

**ĐƠN VỊ THIẾT KẾ:**

CÔNG TY CỔ PHẦN TƯ VẤN THIẾT KẾ  
**BASE ARC**  
ĐỊA CHỈ: 138 ĐIỆN BIÊN PHỦ, PHƯỜNG TÂN ĐỊNH,  
TP. HỒ CHÍ MINH, VIỆT NAM

**TỔNG GIÁM ĐỐC:**

TRẦN ĐỨC AN

**CHỦ NHIỆM DỰ ÁN:**

KTS. NGUYỄN THÀNH THÁI

**CHỦ TRÌ THIẾT KẾ:**

KTS. NGUYỄN THÀNH THÁI

**THIẾT KẾ:**

KTS. LÊ ĐÌNH TÂM

**KIỂM TRA:**

KTS. NGUYỄN ĐỨC THÁI

**DỰ ÁN:**

KHU DÂN CƯ A1-C1 (ĐÔ THỊ DẦU GIẤY)  
ĐỊA ĐIỂM: XÃ DẦU GIẤY, TỈNH ĐỒNG NAI

**CÔNG TRÌNH:**

NHÀ Ở THƯƠNG MẠI LIÊN KẾ

**HẠNG MỤC:**

MẪU NHÀ T3-2b

**TÊN BẢN VẼ:**

MẶT BẰNG XÂY TÔ TẦNG 3, MÁI


**MỤC ĐÍCH PHÁT HÀNH:**

|                                     |                          |
|-------------------------------------|--------------------------|
| <input type="checkbox"/>            | BẢN VẼ MỜI THẦU          |
| <input type="checkbox"/>            | THIẾT KẾ CƠ SỞ           |
| <input checked="" type="checkbox"/> | THIẾT KẾ BẢN VẼ THI CÔNG |
| <input type="checkbox"/>            | BẢN VẼ HOÀN CÔNG         |

HOÀN THÀNH 07/2025


TỶ LỆ NTS

SỐ HIỆU BẢN VẼ A02-53

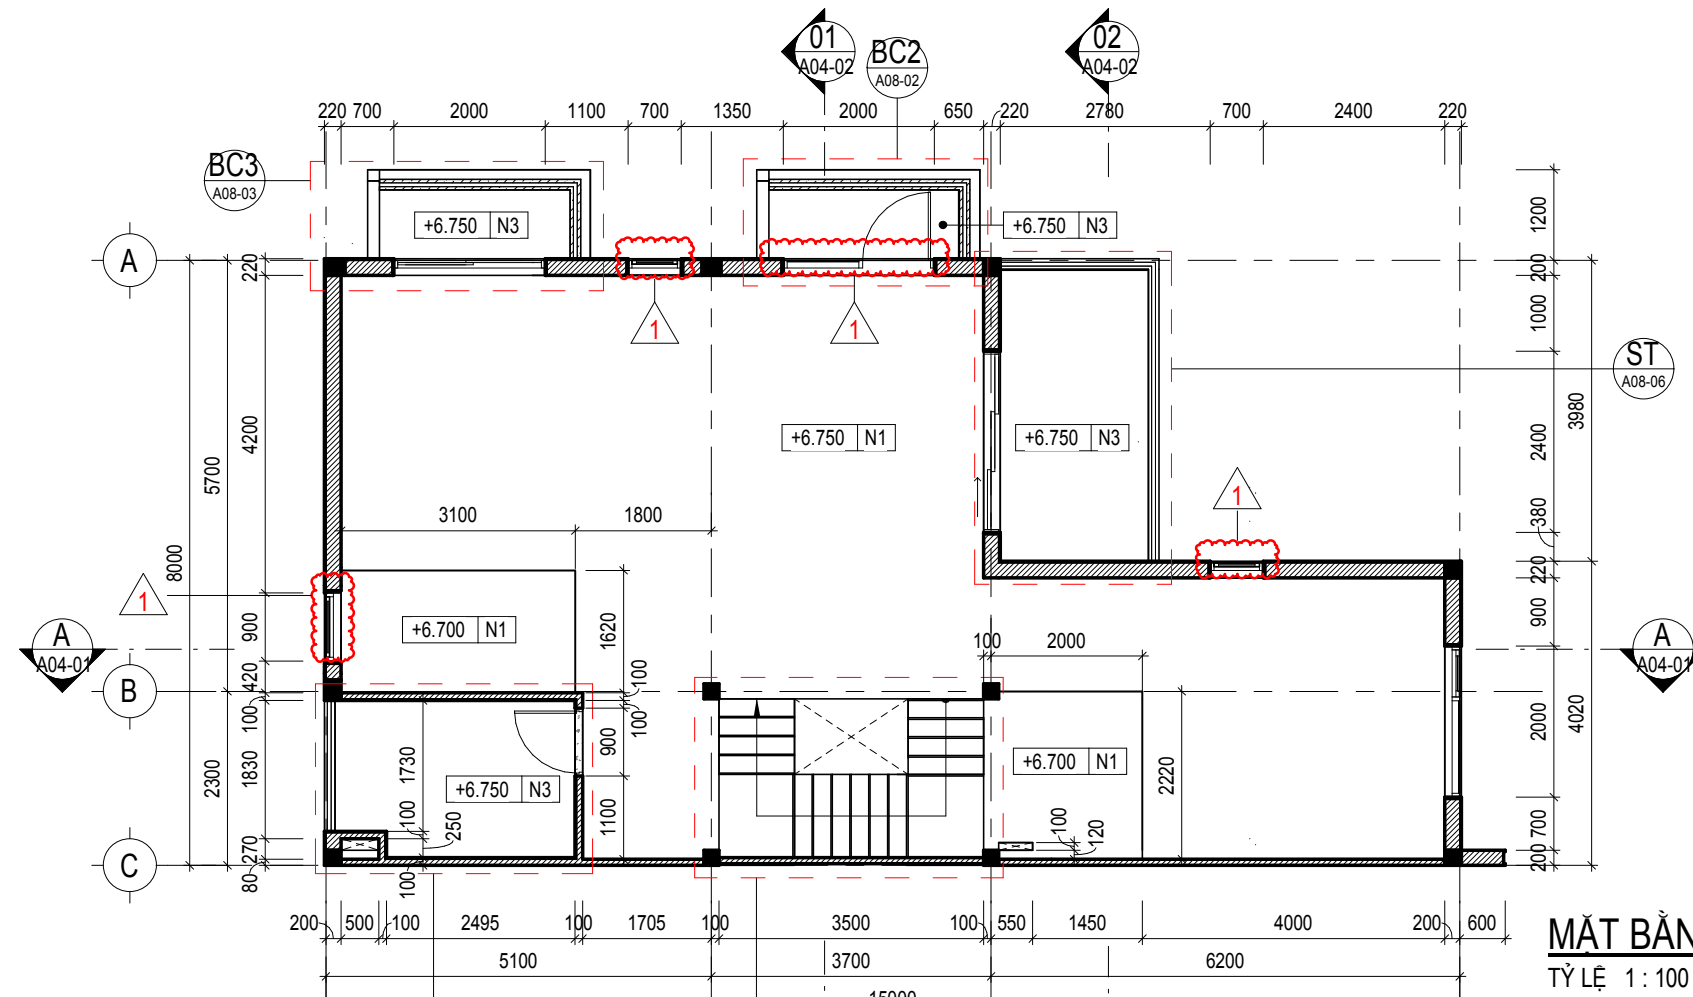

**MẶT BẰNG XÂY TÔ TẦNG 3**

TỶ LỆ 1 : 100

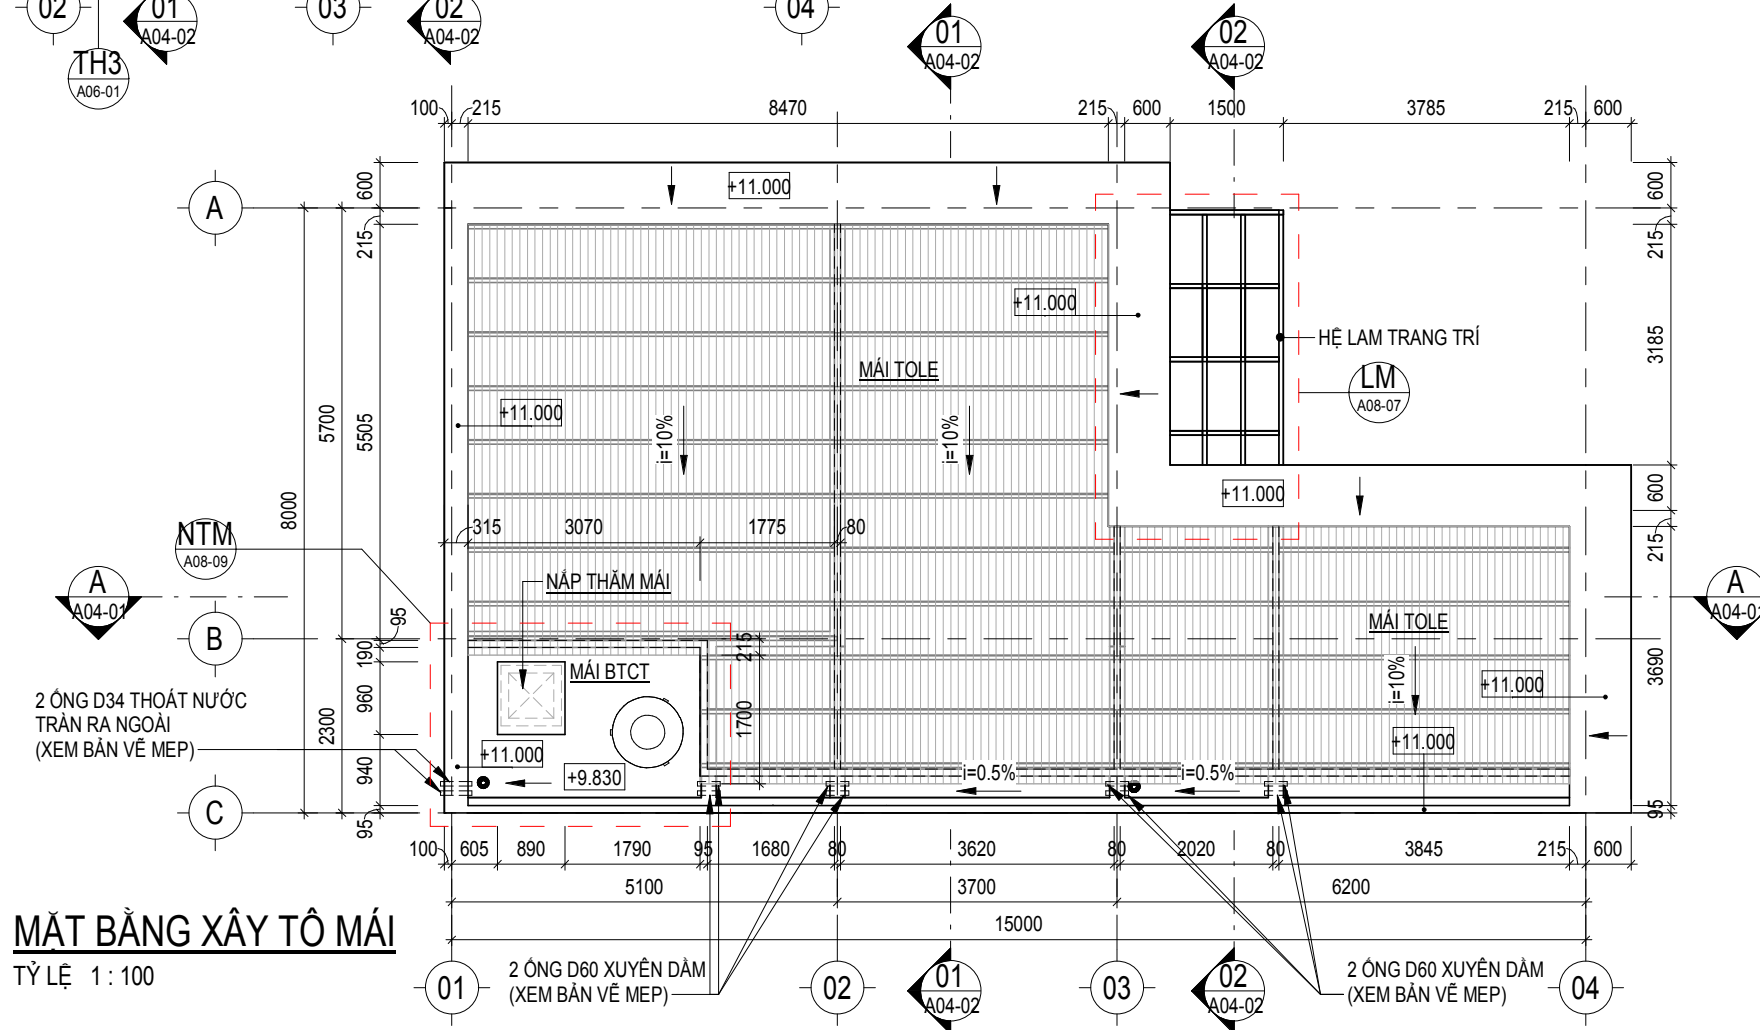


**MẶT BẰNG XÂY TÔ MÁI**

TỶ LỆ 1 : 100








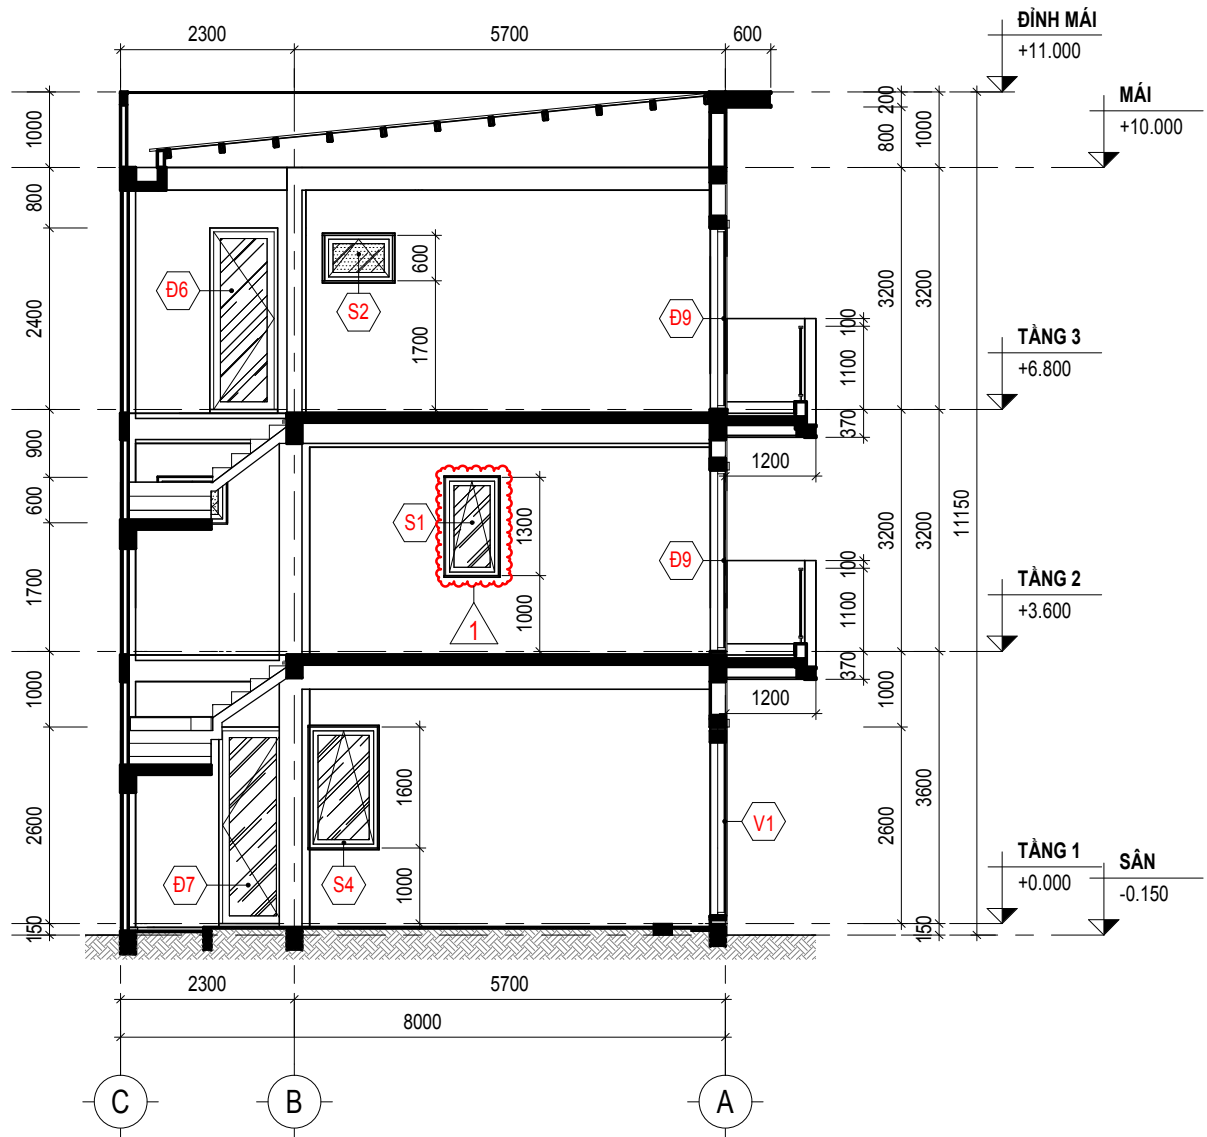

**MẶT CẮT 1-1**  
TỶ LỆ 1:100

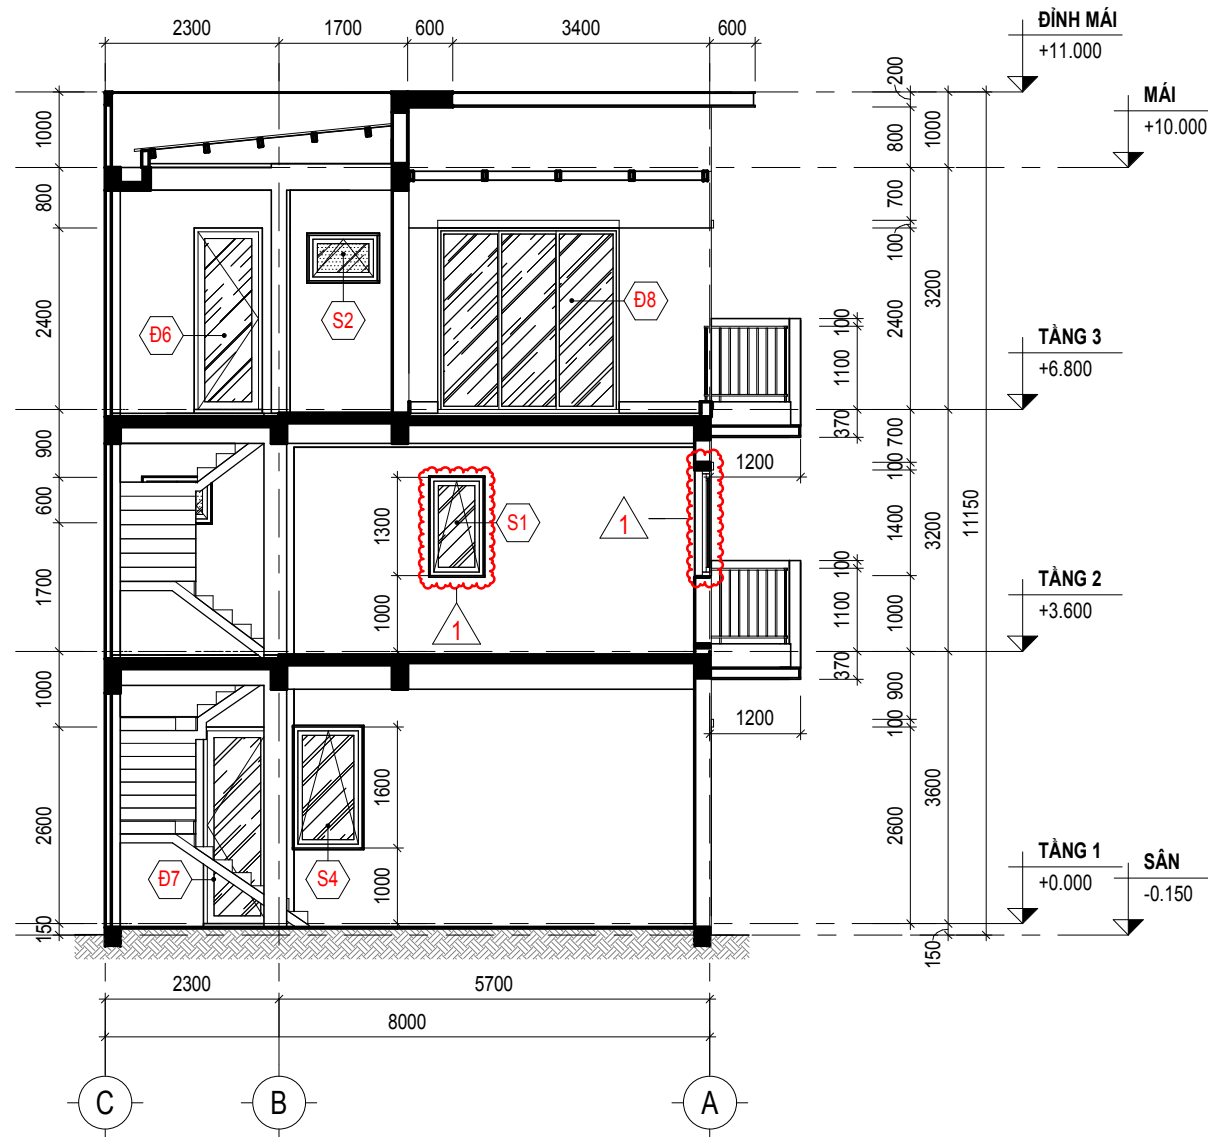

**MẶT CẮT 2-2**  
TỶ LỆ 1:100

**GHI CHÚ:**

- CÁC ĐƠN VỊ THI CÔNG PHẢI PHỐI HỢP BẢN VẼ CỦA TẤT CẢ CÁC BỘ MÔN KHÁC NẾU THẤY SỰ KHÁC BIỆT PHẢI BẢO CHO ĐƠN VỊ THIẾT KẾ XỬ LÝ.
- KHI XỬ LÝ SỰ KHÁC BIỆT, PHẢI THỰC HIỆN ƯU TIÊN THEO THỨ TỰ GIỮA CÁC BỘ MÔN: KIẾN TRÚC → KẾT CẤU / BỘ MÔN KHÁC; HOẶC ƯU TIÊN TRONG CÙNG BỘ MÔN: CHI TIẾT → TỔNG THỂ
- CÁC SỐ LIỆU KÍCH THƯỚC PHẢI ĐƯỢC KIỂM TRA THỰC TẾ TẠI CÔNG TRÌNH, NẾU THẤY SỰ KHÁC BIỆT SO VỚI BẢN VẼ THI PHẢI BẢO CHO ĐƠN VỊ THIẾT KẾ.

| HIỆU CHỈNH: |            |                           |
|-------------|------------|---------------------------|
| REV         | NGÀY       | NỘI DUNG                  |
| 1           | 22/09/2024 | ĐIỀU CHỈNH CỬA ĐI, CỬA SỐ |

**CHỦ ĐẦU TƯ:**  
CÔNG TY TNHH ĐẦU TƯ  
**PHÚ VIỆT TÍN**  
ĐỊA CHỈ: LÔ 18-19 QUỐC LỘ 1A, XÃ DẦU GIẤY,  
TỈNH ĐỒNG NAI, VIỆT NAM

**CTHĐT:** ĐẶNG PHƯỚC BÌNH

**ĐƠN VỊ THIẾT KẾ:**  
CÔNG TY CỔ PHẦN TƯ VẤN THIẾT KẾ  
**BASE ARC**  
ĐỊA CHỈ: 138 ĐIỆN BIÊN PHỦ, PHƯỜNG TÂN ĐỊNH,  
TP. HỒ CHÍ MINH, VIỆT NAM

**TỔNG GIÁM ĐỐC:** TRẦN ĐỨC AN

**CHỦ NHIỆM DỰ ÁN:**

KTS. NGUYỄN THÀNH THÁI

**CHỦ TRÌ THIẾT KẾ:**

KTS. NGUYỄN THÀNH THÁI

**THIẾT KẾ:**

KTS. LÊ ĐÌNH TÂM

**KIỂM TRA:**

KTS. NGUYỄN ĐỨC THÁI

**DỰ ÁN:**

KHU DÂN CƯ A1-C1 (ĐÔ THỊ DẦU GIẤY)

ĐỊA ĐIỂM: XÃ DẦU GIẤY, TỈNH ĐỒNG NAI

**CÔNG TRÌNH:**

NHÀ Ở THƯƠNG MẠI LIÊN KẾ

**HẠNG MỤC:**

MẪU NHÀ T3-2b

**TÊN BẢN VẼ:**

MẶT CẮT

**MỤC ĐÍCH PHÁT HÀNH:**


|                                     |                          |
|-------------------------------------|--------------------------|
| <input type="checkbox"/>            | BẢN VẼ MỜI THẦU          |
| <input type="checkbox"/>            | THIẾT KẾ CƠ SỞ           |
| <input checked="" type="checkbox"/> | THIẾT KẾ BẢN VẼ THI CÔNG |
| <input type="checkbox"/>            | BẢN VẼ HOÀN CÔNG         |

**HOÀN THÀNH** 07/2025


**TỶ LỆ** NTS

**SỐ HIỆU BẢN VẼ** A04-02

BỘ TRÍ BẠC CẤP SÂN SAU  
THEO CAO ĐỘ THỰC TẾ  
CHIỀU RỘNG BẠC 250mm  
CAO ĐỘ BẠC 150-180mm

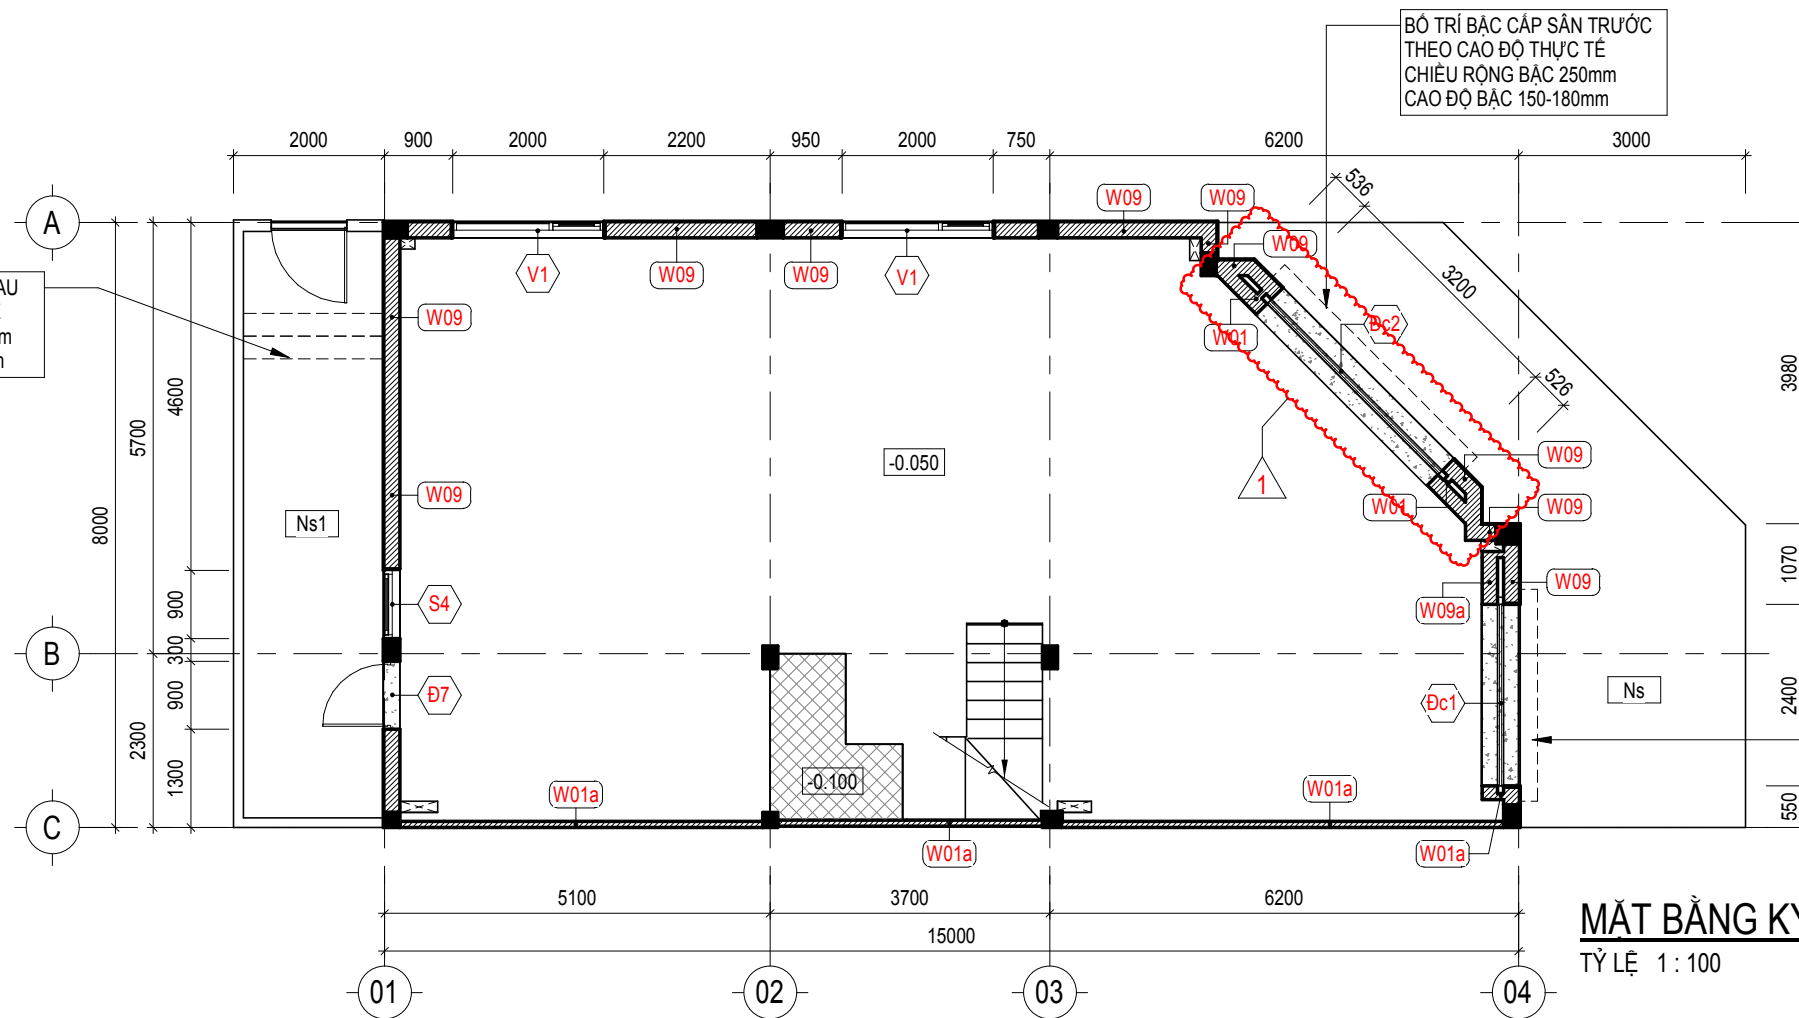

**MẶT BẰNG KÝ HIỆU TẦNG 1**  
TỶ LỆ 1 : 100

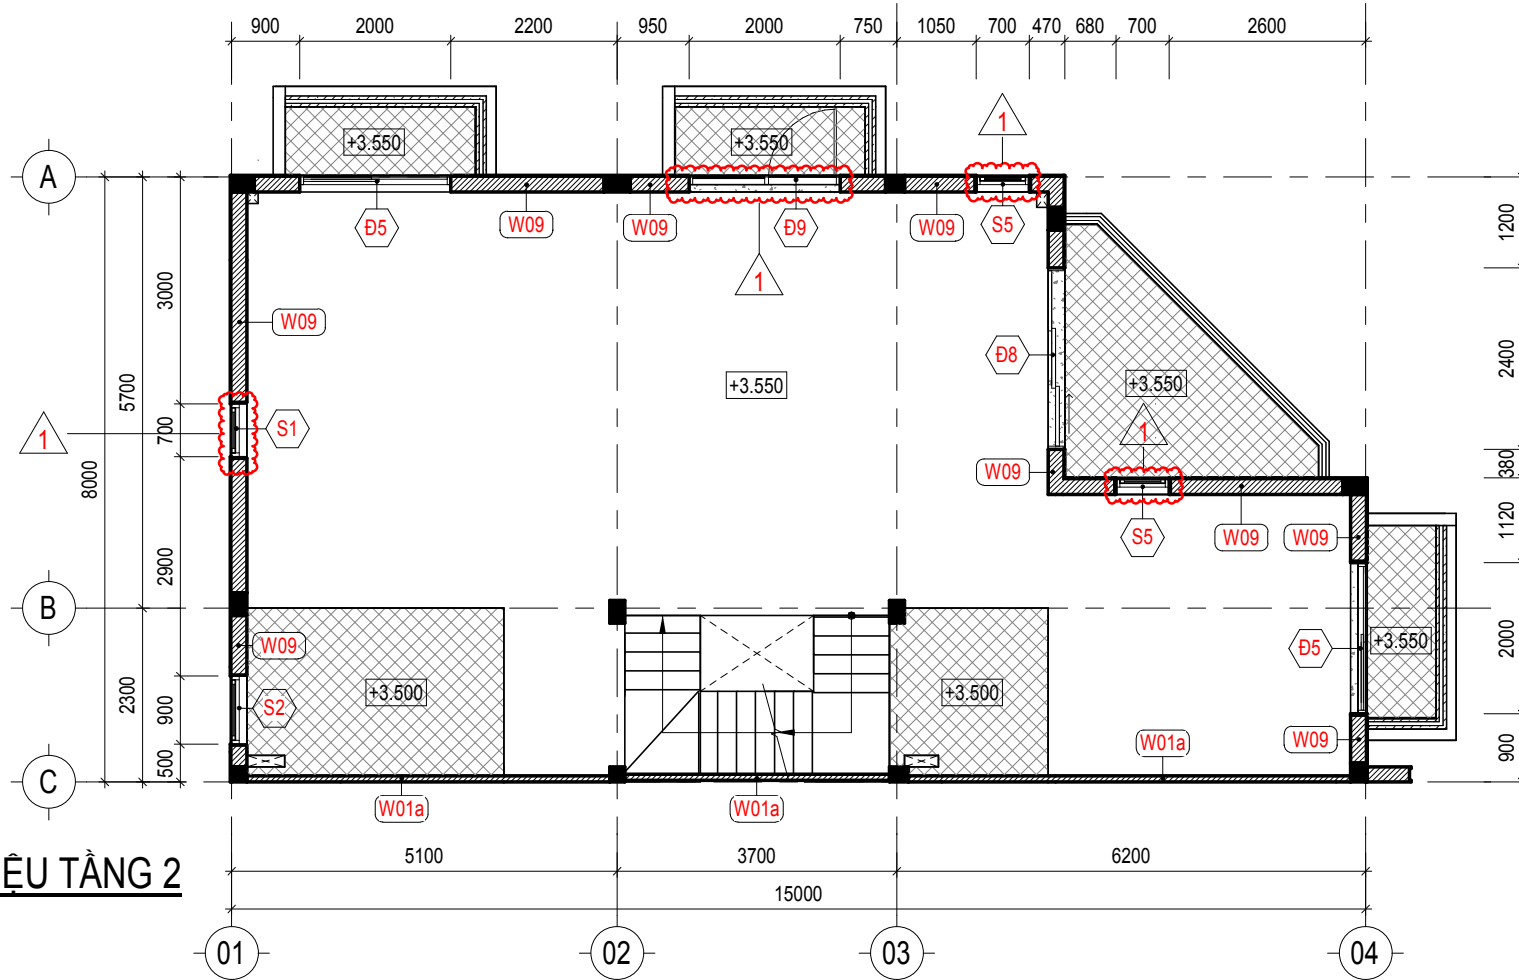

**MẶT BẰNG KÝ HIỆU TẦNG 2**  
TỶ LỆ 1 : 100

**GHI CHÚ:**

- SÂN HẠ COTE
- LÁT ĐÁ GRANIT ĐEN
- LEN GẠCH GẠCH CERAMIC CAO 100mm (BAN CÔNG)

**GHI CHÚ:**

- CÁC ĐƠN VỊ THI CÔNG PHẢI PHỐI HỢP BẢN VẼ CỦA TẤT CẢ CÁC BỘ MÔN KHÁC NẾU THẤY SỰ KHÁC BIỆT PHẢI BẢO CHO ĐƠN VỊ THIẾT KẾ XỬ LÝ.
- KHI XỬ LÝ SỰ KHÁC BIỆT, PHẢI THỰC HIỆN ƯU TIÊN THEO THỨ TỰ GIỮA CÁC BỘ MÔN: KIẾN TRÚC → KẾT CẤU / BỘ MÔN KHÁC; HOẶC ƯU TIÊN TRONG CÙNG BỘ MÔN: CHI TIẾT → TỔNG THỂ
- CÁC SỐ LIỆU KÍCH THƯỚC PHẢI ĐƯỢC KIỂM TRA THỰC TẾ TẠI CÔNG TRÌNH, NẾU THẤY SỰ KHÁC BIỆT SƠ VỚI BẢN VẼ THI PHẢI BẢO CHO ĐƠN VỊ THIẾT KẾ.

**HIỆU CHỈNH:**

| REV | NGÀY       | NỘI DUNG                  |
|-----|------------|---------------------------|
| 1   | 22/09/2024 | ĐIỀU CHỈNH CỬA ĐI, CỬA SỐ |

**CHỦ ĐẦU TƯ:**

CÔNG TY TNHH ĐẦU TƯ

**PHÚ VIỆT TÍN**

ĐỊA CHỈ: LÔ 18-19 QUỐC LỘ 1A, XÃ DẦU GIẤY,  
TỈNH ĐỒNG NAI, VIỆT NAM

**CHỦ ĐẦU TƯ:**

ĐẶNG PHƯỚC BÌNH

**ĐƠN VỊ THIẾT KẾ:**

CÔNG TY CỔ PHẦN TƯ VẤN THIẾT KẾ

**BASE ARC**

ĐỊA CHỈ: 138 ĐIỆN BIÊN PHỦ, PHƯỜNG TÂN ĐỊNH,  
TP. HỒ CHÍ MINH, VIỆT NAM

**TỔNG GIÁM ĐỐC:**

TRẦN ĐỨC AN

**CHỦ NHIỆM DỰ ÁN:**

KTS. NGUYỄN THÀNH THÁI

**CHỦ TRÌ THIẾT KẾ:**

KTS. NGUYỄN THÀNH THÁI

**THIẾT KẾ:**

KTS. LÊ ĐÌNH TÂM

**KIỂM TRA:**

KTS. NGUYỄN ĐỨC THÁI

**DỰ ÁN:**

KHU DÂN CƯ A1-C1 (ĐÔ THỊ DẦU GIẤY)

ĐỊA ĐIỂM: XÃ DẦU GIẤY, TỈNH ĐỒNG NAI

**CÔNG TRÌNH:**

NHÀ Ở THƯƠNG MẠI LIÊN KẾ

**HẠNG MỤC:**

MẪU NHÀ T3-2b

**TÊN BẢN VẼ:**

MẶT BẰNG KÝ HIỆU TẦNG 1, TẦNG 2


**MỤC ĐÍCH PHÁT HÀNH:**

|                                                              |
|--------------------------------------------------------------|
| BẢN VẼ MỜI THẦU                                              |
| THIẾT KẾ CƠ SỞ                                               |
| <input checked="" type="checkbox"/> THIẾT KẾ BẢN VẼ THI CÔNG |
| BẢN VẼ HOÀN CÔNG                                             |


HOÀN THÀNH 07/2025

TỶ LỆ NTS

SỐ HIỆU BẢN VẼ A05-01

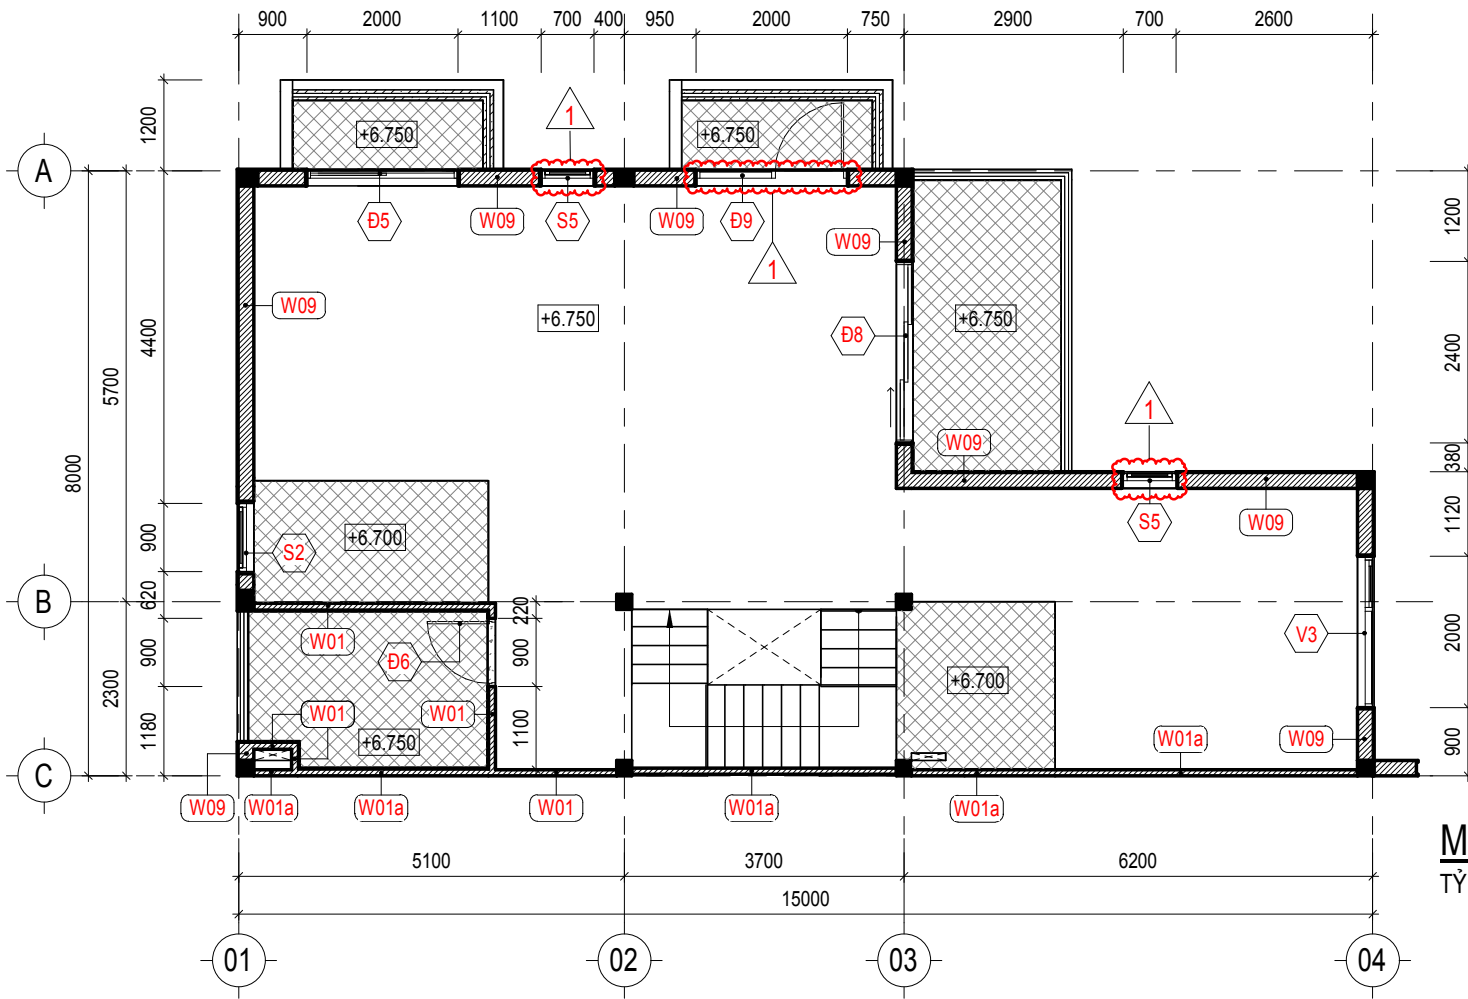

**MẶT BẰNG KÝ HIỆU TẦNG 3**  
TỶ LỆ 1 : 100

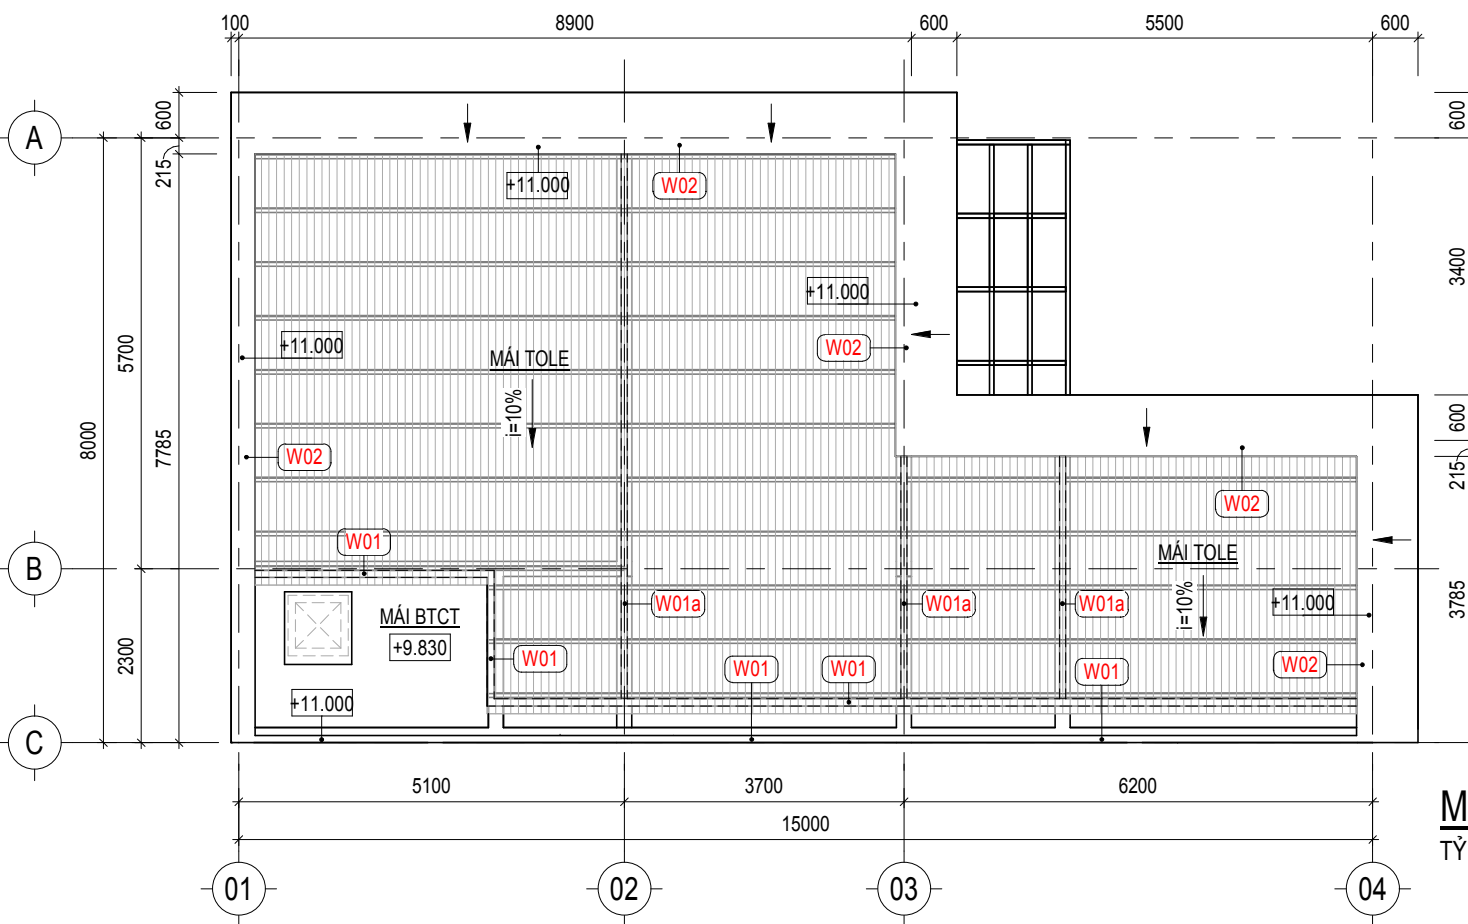

**MẶT BẰNG KÝ HIỆU MÁI**  
TỶ LỆ 1 : 100

**GHI CHÚ:**

- SÀN HẠ COTE
- LÁT ĐÁ GRANIT ĐEN
- LEN GẠCH GẠCH CERAMIC CAO 100mm (BAN CÔNG)

**GHI CHÚ:**

- CÁC ĐƠN VỊ THI CÔNG PHẢI PHỐI HỢP BẢN VẼ CỦA TẤT CẢ CÁC BỘ MÔN KHÁC NẾU THẤY SỰ KHÁC BIỆT PHẢI BẢO CHO ĐƠN VỊ THIẾT KẾ ĐỂ XỬ LÝ.
- KHI XỬ LÝ SỰ KHÁC BIỆT, PHẢI THỰC HIỆN ƯU TIÊN THEO THỨ TỰ GIỮA CÁC BỘ MÔN: KIẾN TRÚC → KẾT CẤU / BỘ MÔN KHÁC; HOẶC ƯU TIÊN TRONG CÙNG BỘ MÔN: CHI TIẾT → TỔNG THỂ
- CÁC SỐ LIỆU KÍCH THƯỚC PHẢI ĐƯỢC KIỂM TRA THỰC TẾ TẠI CÔNG TRÌNH, NẾU THẤY SỰ KHÁC BIỆT SƠ VỚI BẢN VẼ THI PHẢI BẢO CHO ĐƠN VỊ THIẾT KẾ.

**HIỆU CHỈNH:**

| REV | NGÀY       | NỘI DUNG                  |
|-----|------------|---------------------------|
| 1   | 22/09/2024 | ĐIỀU CHỈNH CỬA ĐI, CỬA SỐ |

**CHỦ ĐẦU TƯ:**

CÔNG TY TNHH ĐẦU TƯ

**PHÚ VIỆT TÍN**

ĐỊA CHỈ: LÔ 18-19 QUỐC LỘ 1A, XÃ DẦU GIẤY,  
TỈNH ĐỒNG NAI, VIỆT NAM

**CHỦ ĐẦU TƯ:**

ĐẶNG PHƯỚC BÌNH

**ĐƠN VỊ THIẾT KẾ:**

CÔNG TY CỔ PHẦN TƯ VẤN THIẾT KẾ

**BASE ARC**

ĐỊA CHỈ: 138 ĐIỆN BIÊN PHỦ, PHƯỜNG TÂN ĐỊNH,  
TP. HỒ CHÍ MINH, VIỆT NAM

**TỔNG GIÁM ĐỐC:**

TRẦN ĐỨC AN

**CHỦ NHIỆM DỰ ÁN:**

KTS. NGUYỄN THÀNH THÁI

**CHỦ TRÌ THIẾT KẾ:**

KTS. NGUYỄN THÀNH THÁI

**THIẾT KẾ:**

KTS. LÊ ĐÌNH TÂM

**KIỂM TRA:**

KTS. NGUYỄN ĐỨC THÁI

**DỰ ÁN:**

KHU DÂN CƯ A1-C1 (ĐÔ THỊ DẦU GIẤY)

ĐỊA ĐIỂM: XÃ DẦU GIẤY, TỈNH ĐỒNG NAI

**CÔNG TRÌNH:**

NHÀ Ở THƯƠNG MẠI LIÊN KẾ

**HẠNG MỤC:**

MẪU NHÀ T3-2b

**TÊN BẢN VẼ:**

MẶT BẰNG KÝ HIỆU TẦNG 3, MÁI




**MỤC ĐÍCH PHÁT HÀNH:**

|                                                              |
|--------------------------------------------------------------|
| BẢN VẼ MỜI THẦU                                              |
| THIẾT KẾ CƠ SỞ                                               |
| <input checked="" type="checkbox"/> THIẾT KẾ BẢN VẼ THI CÔNG |
| BẢN VẼ HOÀN CÔNG                                             |


HOÀN THÀNH 07/2025

TỶ LỆ NTS


SỐ HIỆU BẢN VẼ A05-02

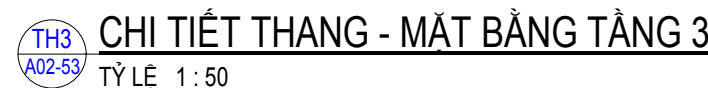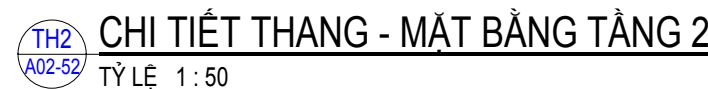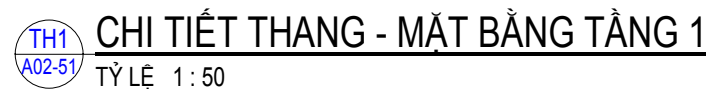


|  |        |
|--|--------|
|  | A06-01 |
|--|--------|

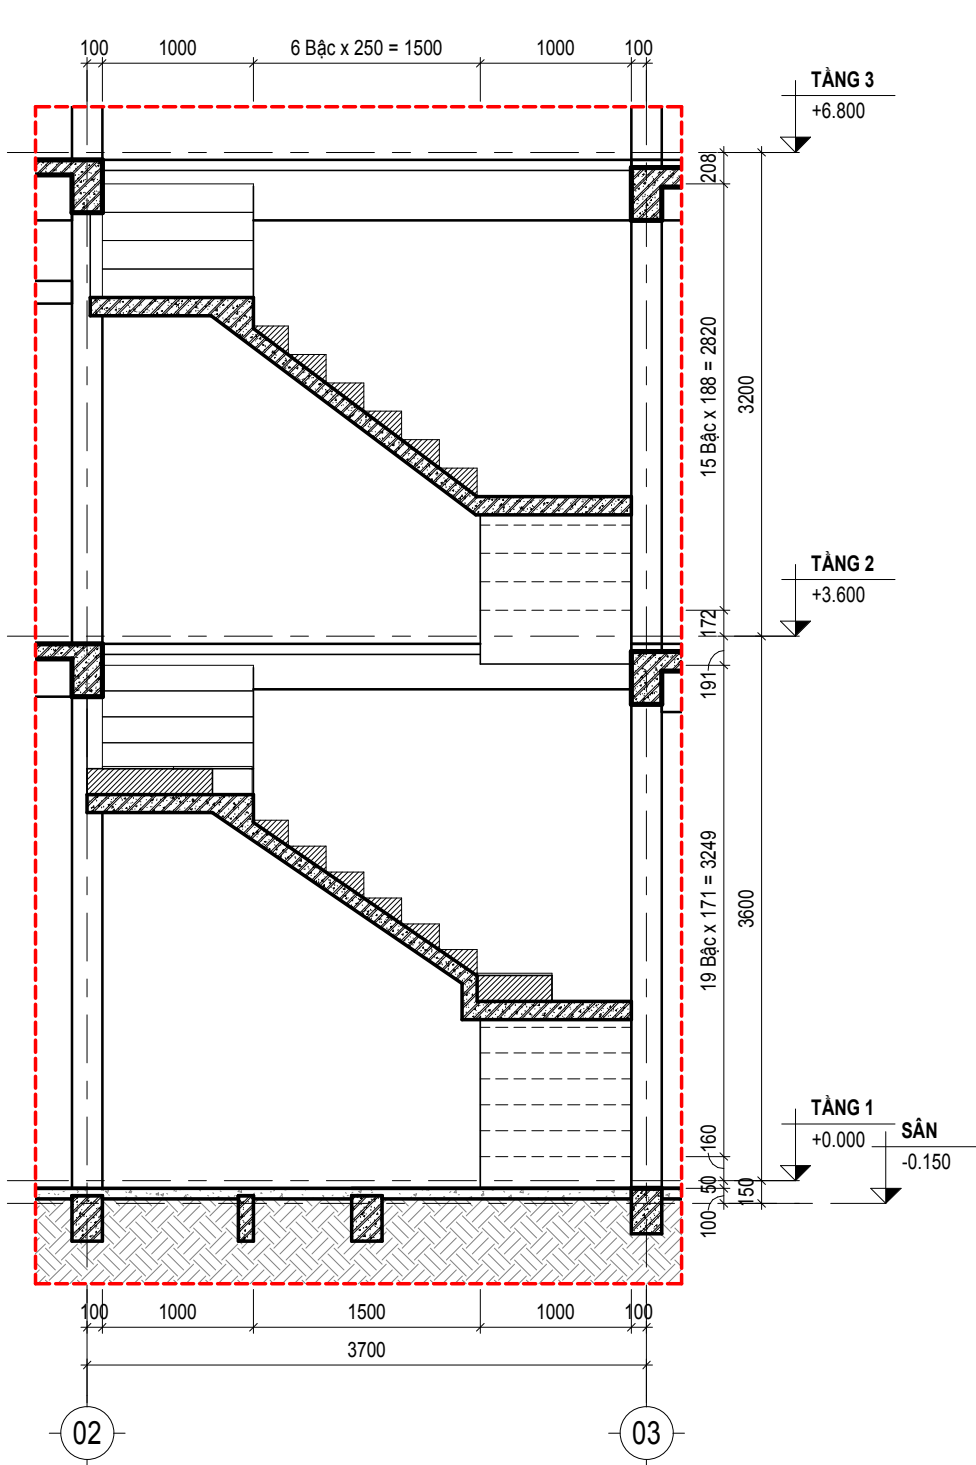

04 CHI TIẾT THANG - MẶT CẮT 04  
TỶ LỆ 1 : 50

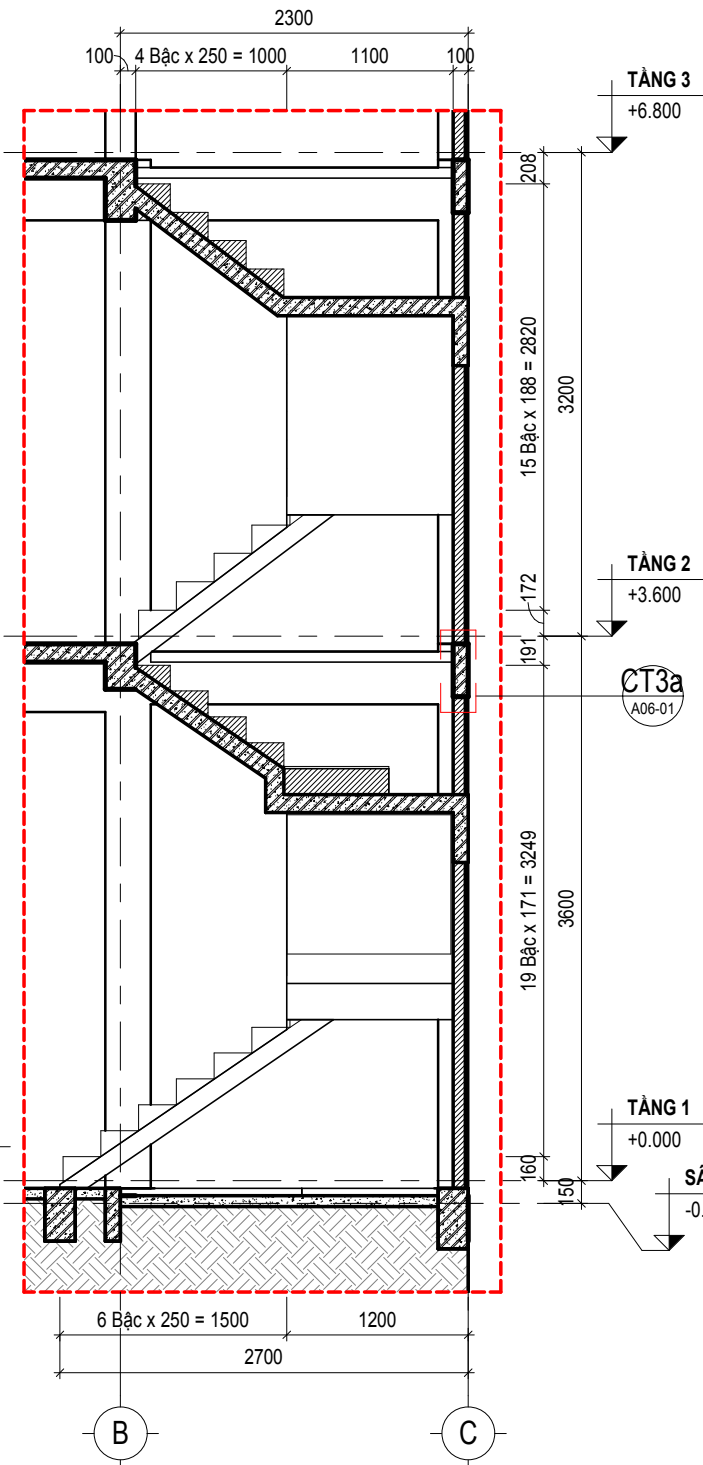

05 CHI TIẾT THANG - MẶT CẮT 5  
TỶ LỆ 1 : 50

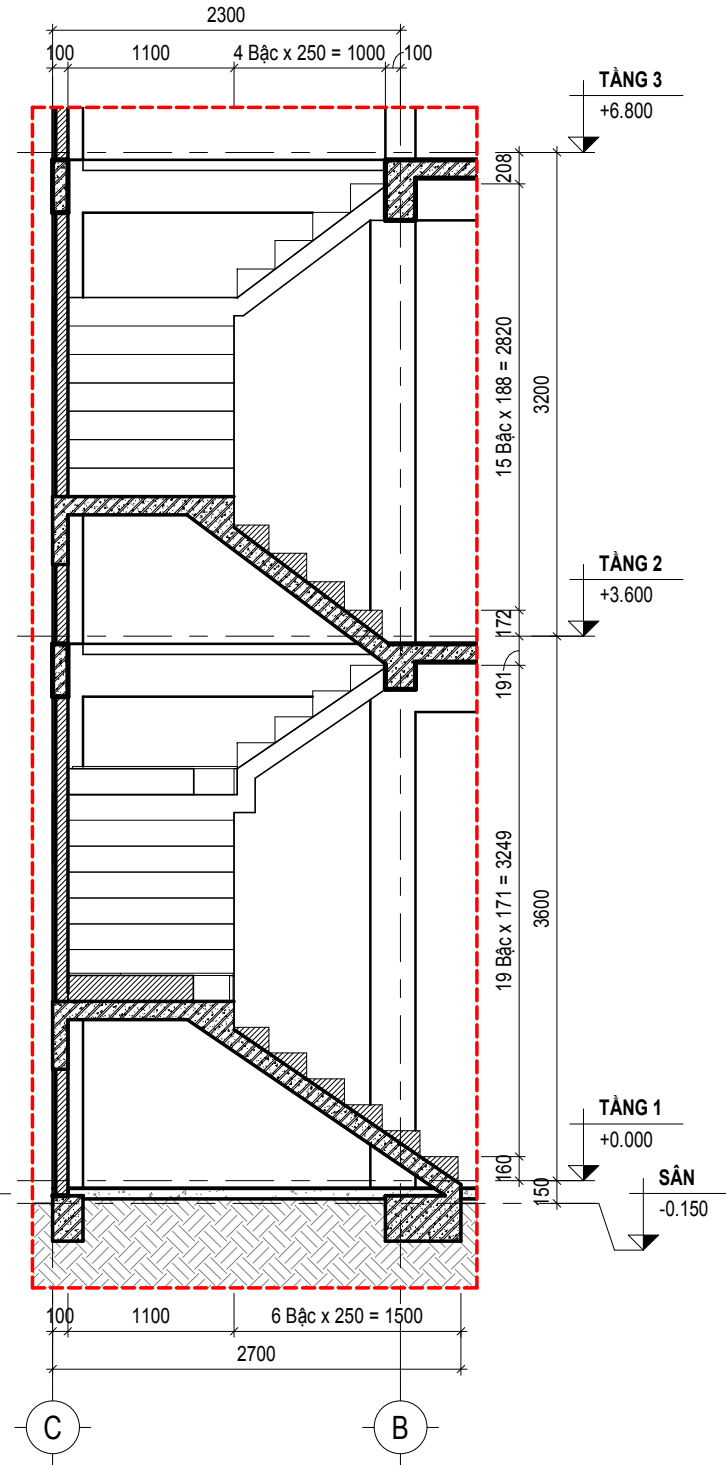

06 CHI TIẾT THANG - MẶT CẮT 6  
TỶ LỆ 1 : 50

GHI CHÚ:  
- CÁC ĐƠN VỊ THI CÔNG PHẢI PHỐI HỢP BẢN VẼ CỦA TẤT CẢ CÁC BỘ MÔN KHÁC NẾU THẤY SỰ KHÁC BIỆT PHẢI BÁO CHO ĐƠN VỊ THIẾT KẾ XỬ LÝ.  
- KHI XỬ LÝ SỰ KHÁC BIỆT, PHẢI THỰC HIỆN ƯU TIÊN THEO THỨ TỰ GIỮA CÁC BỘ MÔN: KIẾN TRÚC → KẾT CẤU / BỘ MÔN KHÁC; HOẶC ƯU TIÊN TRONG CÙNG BỘ MÔN: CHI TIẾT → TỔNG THỂ  
- CÁC SỐ LIỆU KÍCH THƯỚC PHẢI ĐƯỢC KIỂM TRA THỰC TẾ TẠI CÔNG TRÌNH, NẾU THẤY SỰ KHÁC BIỆT SƠ VỚI BẢN VẼ THI PHẢI BÁO CHO ĐƠN VỊ THIẾT KẾ.

HIỆU CHỈNH:  
REV NGÀY NỘI DUNG

CHỦ ĐẦU TƯ:  
CÔNG TY TNHH ĐẦU TƯ  
**PHÚ VIỆT TÍN**  
ĐỊA CHỈ: LÔ 18-19 QUỐC LỘ 1A, XÃ DẦU GIẤY,  
TỈNH ĐỒNG NAI, VIỆT NAM

CTHĐT: ĐẶNG PHƯỚC BÌNH

ĐƠN VỊ THIẾT KẾ:  
CÔNG TY CỔ PHẦN TƯ VẤN THIẾT KẾ  
**BASE ARC**  
ĐỊA CHỈ: 138 ĐIỆN BIÊN PHỦ, PHƯỜNG TÂN ĐỊNH,  
TP. HỒ CHÍ MINH, VIỆT NAM

TỔNG GIÁM ĐỐC: TRẦN ĐỨC AN

CHỦ NHIỆM DỰ ÁN:

KTS. NGUYỄN THÀNH THÁI

CHỦ TRÌ THIẾT KẾ:

KTS. NGUYỄN THÀNH THÁI

THIẾT KẾ:

KTS. LÊ ĐÌNH TÂM

KIỂM TRA:

KTS. NGUYỄN ĐỨC THÁI

DỰ ÁN:

KHU DÂN CƯ A1-C1 (ĐÔ THỊ DẦU GIẤY)

ĐỊA ĐIỂM: XÃ DẦU GIẤY, TỈNH ĐỒNG NAI

CÔNG TRÌNH:

NHÀ Ở THƯƠNG MẠI LIÊN KẾ

HẠNG MỤC:

MẪU NHÀ T3-2b

TÊN BẢN VẼ:

CHI TIẾT THANG (TT)

MỤC ĐÍCH PHÁT HÀNH:

BẢN VẼ MỜI THẦU

THIẾT KẾ CƠ SỞ


THIẾT KẾ BẢN VẼ THI CÔNG

BẢN VẼ HOÀN CÔNG

HOÀN THÀNH 07/2025

TỶ LỆ NTS


SỐ HIỆU BẢN VẼ A06-02

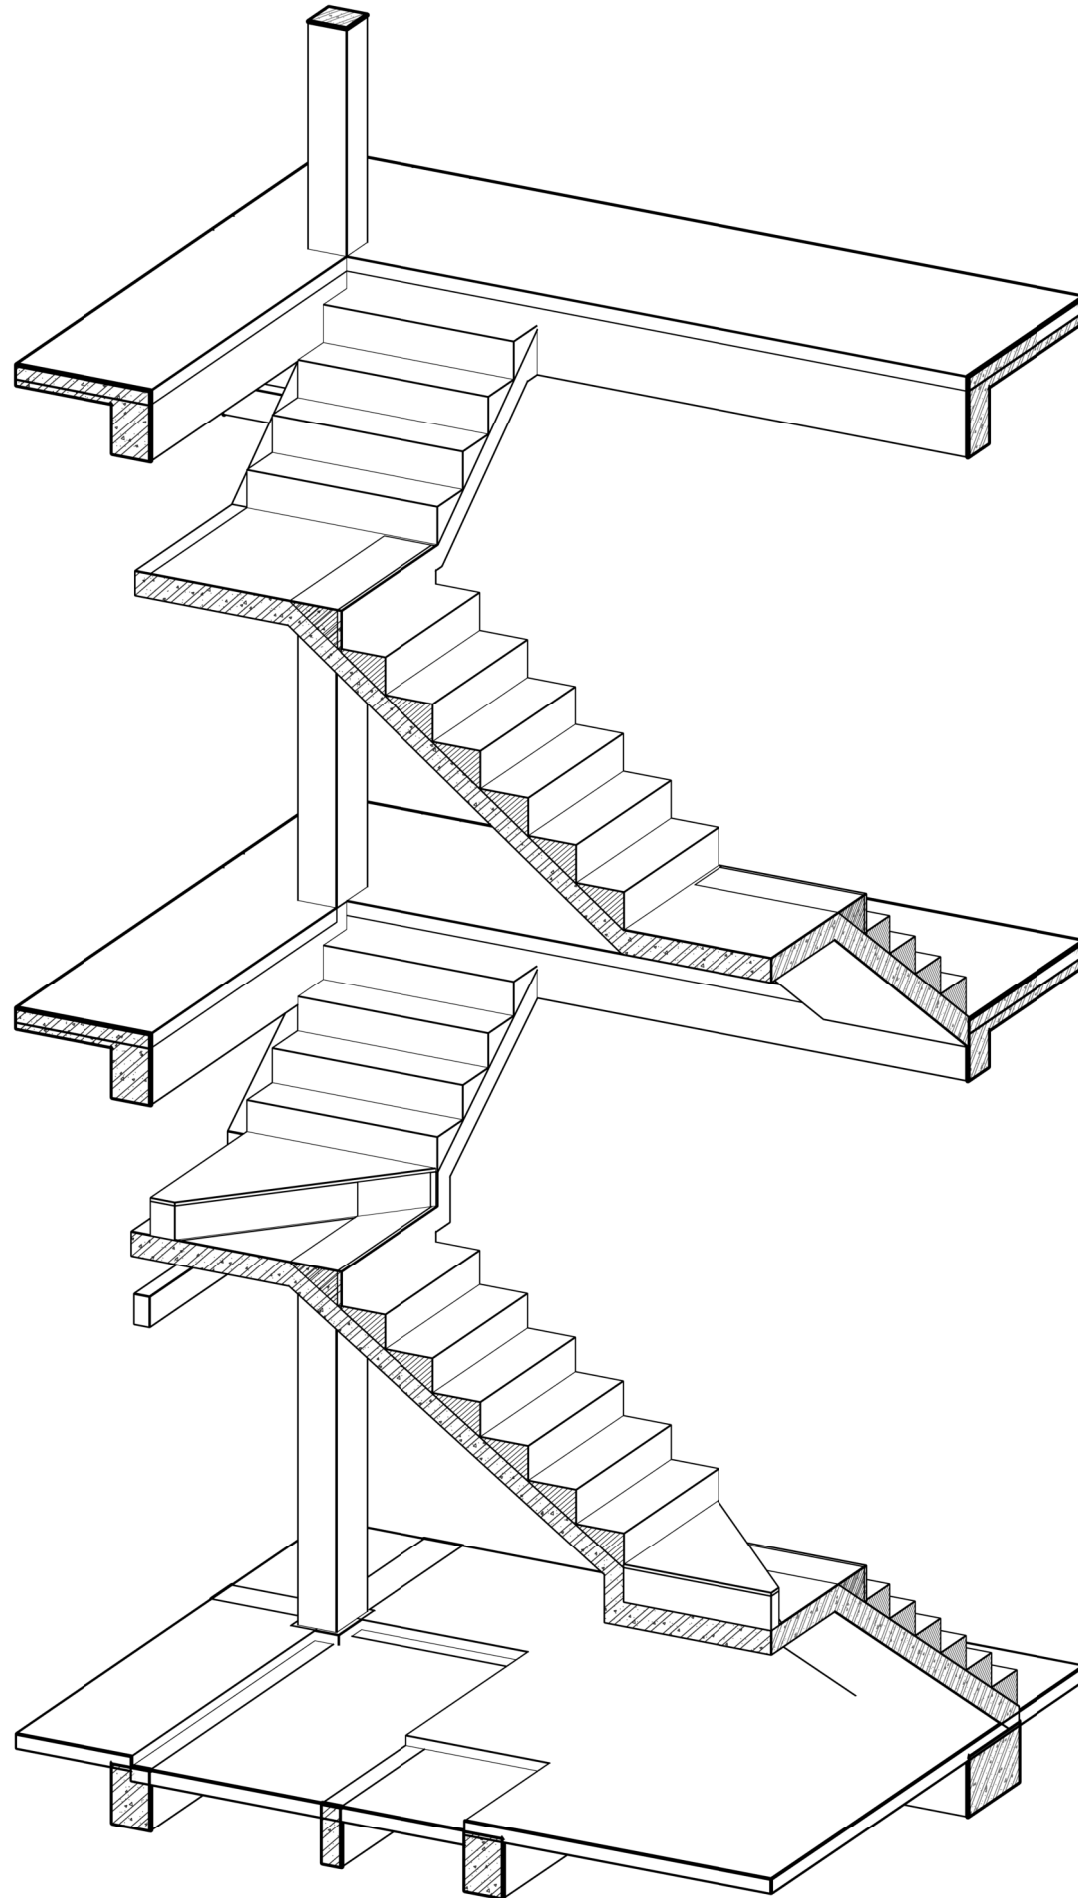


3D - CẦU THANG

|   |                          |                 |
|---|--------------------------|-----------------|
| GHI CHÚ:<br>- CÁC ĐƠN VỊ THI CÔNG PHẢI PHỐI HỢP BẢN VẼ CỦA TẤT CẢ CÁC BỘ MÔN<br>KHÁC NẾU THẤY SỰ KHÁC BIỆT PHẢI BÁO CHO ĐƠN VỊ THIẾT KẾ XỬ LÝ.<br>- KHI XỬ LÝ SỰ KHÁC BIỆT, PHẢI THỰC HIỆN ƯU TIÊN THEO THỨ TỰ GIỮA CÁC<br>BỘ MÔN: KIẾN TRÚC → KẾT CẤU / BỘ MÔN KHÁC; HOẶC ƯU TIÊN TRONG CÙNG<br>BỘ MÔN: CHI TIẾT → TỔNG THỂ<br>- CÁC SỐ LƯU KỊCH THUỘC PHẢI ĐƯỢC KIỂM TRA THỰC TẾ TẠI CÔNG TRÌNH,<br>NẾU THẤY SỰ KHÁC BIỆT SƠ VỚI BẢN VẼ THI PHẢI BÁO CHO ĐƠN VỊ THIẾT KẾ. |                          |                 |
| HIỆU CHỈNH:   |                          |                 |
| REV   | NGÀY                     | NỘI DUNG        |
|   |                          |                 |
| CHỦ ĐẦU TƯ:<br>CÔNG TY TNHH ĐẦU TƯ<br><b>PHÚ VIỆT TÍN</b><br>ĐỊA CHỈ: LÔ 18-19 QUỐC LỘ 1A, XÃ DẦU GIẤY,<br>TỈNH ĐỒNG NAI, VIỆT NAM   |                          |                 |
|   |                          |                 |
| CTHĐT.V:   |                          | ĐẠNG PHƯỚC BÌNH |
| ĐƠN VỊ THIẾT KẾ:<br>CÔNG TY CỔ PHẦN TƯ VẤN THIẾT KẾ<br><b>BASE ARC</b><br>ĐỊA CHỈ: 138 ĐIỆN BIÊN PHỦ, PHƯỜNG TÂN ĐỊNH,<br>TP. HỒ CHÍ MINH, VIỆT NAM   |                          |                 |
|   |                          |                 |
| TỔNG GIÁM ĐỐC:   |                          | TRẦN ĐỨC AN     |
| CHỦ NHIỆM DỰ ÁN:   |                          |                 |
| KTS. NGUYỄN THÀNH THÁI   |                          |                 |
| CHỦ TRÌ THIẾT KẾ:   |                          |                 |
| KTS. NGUYỄN THÀNH THÁI   |                          |                 |
| THIẾT KẾ:   |                          |                 |
| KTS. LÊ ĐÌNH TÂM   |                          |                 |
| KIỂM TRA:   |                          |                 |
| KTS. NGUYỄN ĐỨC THÁI   |                          |                 |
| DỰ ÁN:<br>KHU DÂN CƯ A1-C1 (ĐÔ THỊ DẦU GIẤY)<br>ĐỊA ĐIỂM: XÃ DẦU GIẤY, TỈNH ĐỒNG NAI   |                          |                 |
| CÔNG TRÌNH:<br><br>NHÀ Ở THƯƠNG MẠI LIÊN KẾ   |                          |                 |
| HẠNG MỤC:<br><br>MẪU NHÀ T3-2b   |                          |                 |
| TÊN BẢN VẼ:<br><br>3D CẦU THANG   |                          |                 |
| MỤC ĐÍCH PHÁT HÀNH:   |                          |                 |
|   | BẢN VẼ MỜI THẦU          |                 |
|   | THIẾT KẾ CƠ SỞ           |                 |
| ✓   | THIẾT KẾ BẢN VẼ THI CÔNG |                 |
|   | BẢN VẼ HOÀN CÔNG         |                 |
| HOÀN THÀNH   |                          | 07/2025         |
| TỶ LỆ   |                          | NTS             |
| SỐ HIỆU BẢN VẼ   |                          | A06-03          |




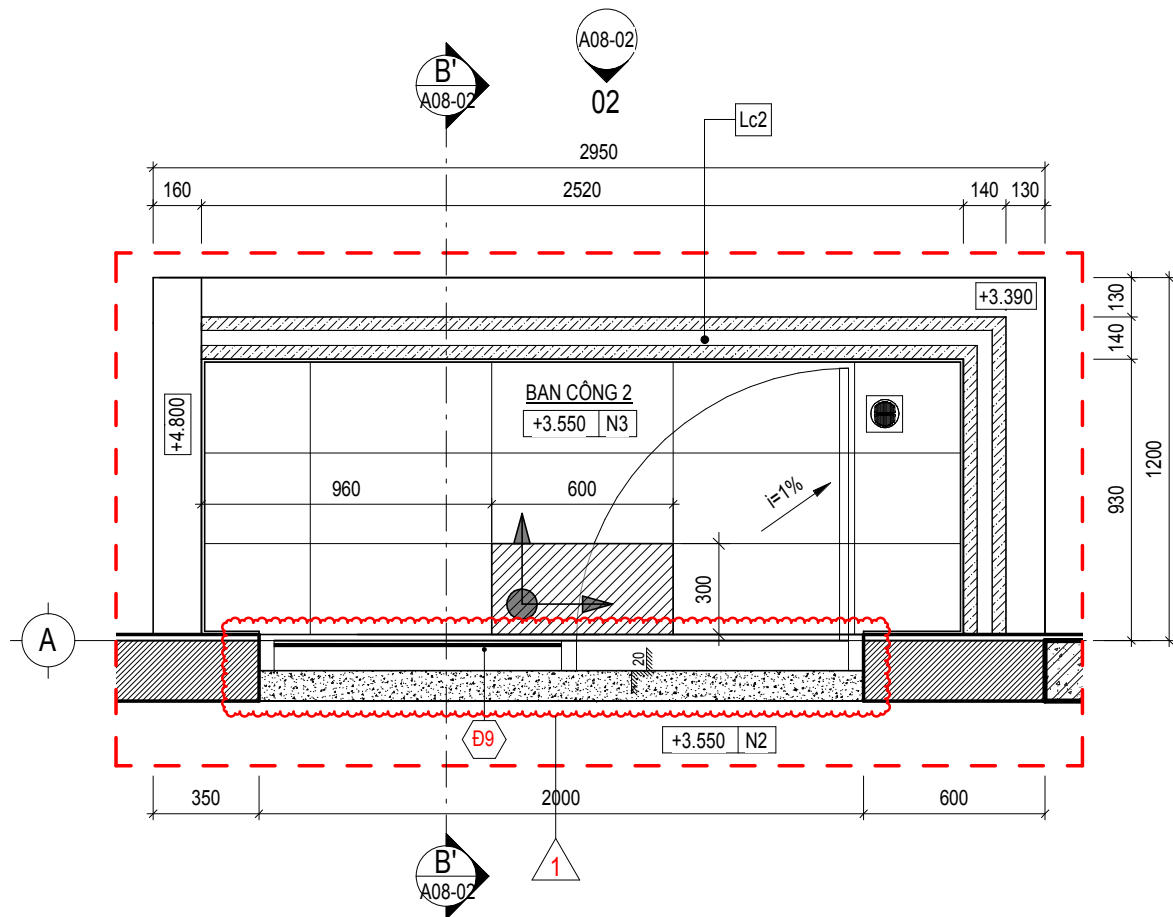

CT BAN CÔNG 2 (ĐIỂN HÌNH) - MẶT BẰNG  
TỶ LỆ 1:25

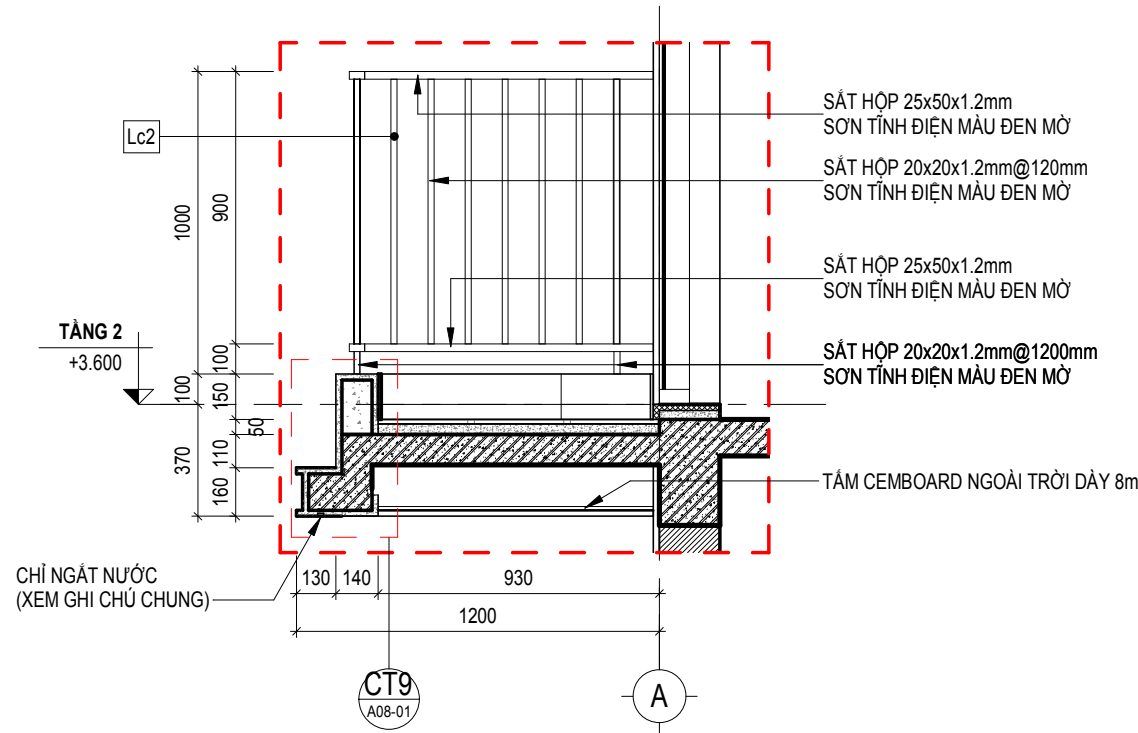

LAN CAN Lc2 (ĐIỂN HÌNH) - MC B'  
TỶ LỆ 1:25

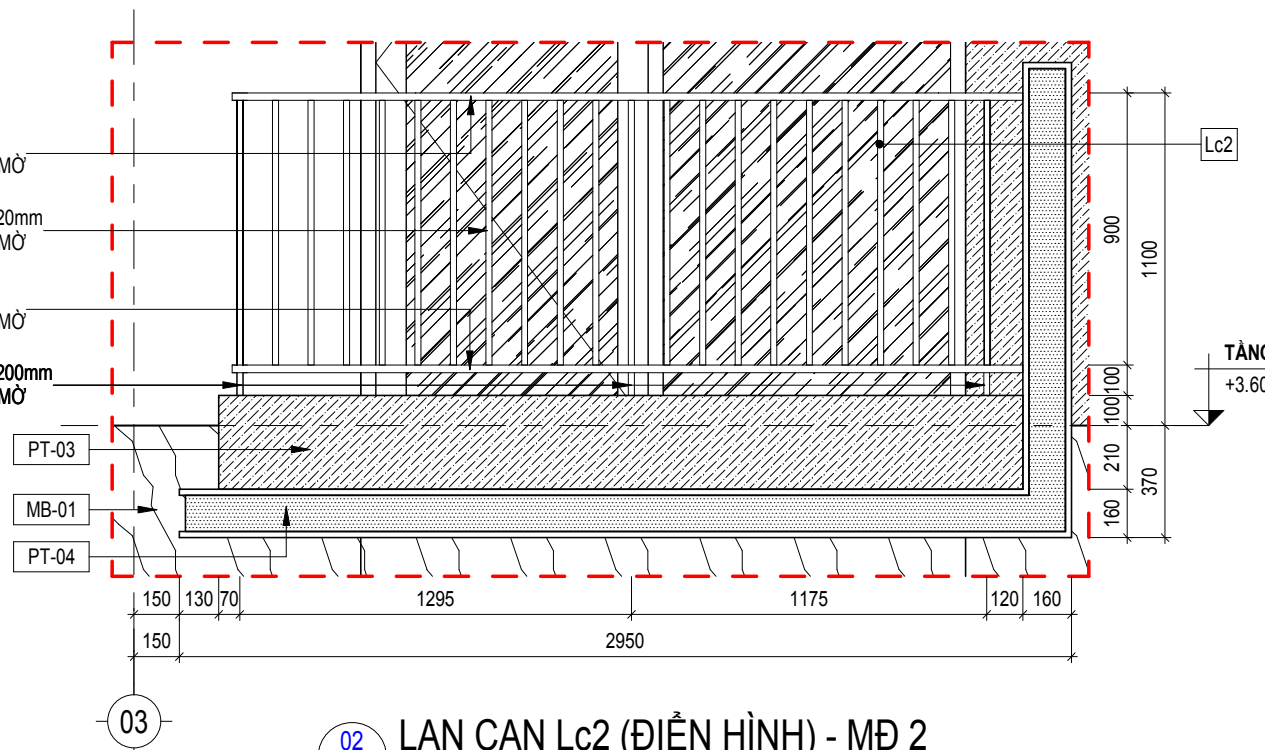

LAN CAN Lc2 (ĐIỂN HÌNH) - MĐ 2  
TỶ LỆ 1:25

GHI CHÚ:  
- CÁC ĐƠN VỊ THI CÔNG PHẢI PHỐI HỢP BẢN VẼ CỦA TẤT CẢ CÁC BỘ MÔN KHÁC NẾU THẤY SỰ KHÁC BIỆT PHẢI BẢO CHỨNG CHO ĐƠN VỊ THIẾT KẾ XỬ LÝ.  
- KHI XỬ LÝ SỰ KHÁC BIỆT, PHẢI THỰC HIỆN ƯU TIÊN THEO THỨ TỰ GIỮA CÁC BỘ MÔN: KIẾN TRÚC → KẾT CẤU / BỘ MÔN KHÁC; HOẶC ƯU TIÊN TRONG CÙNG BỘ MÔN: CHI TIẾT → TỔNG THỂ  
- CÁC SỐ LƯU KỊCH THUỘC PHẢI ĐƯỢC KIỂM TRA THỰC TẾ TẠI CÔNG TRÌNH, NẾU THẤY SỰ KHÁC BIỆT SƠ VỚI BẢN VẼ THI PHẢI BẢO CHỨNG CHO ĐƠN VỊ THIẾT KẾ.

HIỆU CHỈNH:  
REV NGÀY NỘI DUNG  
1 22/09/2024 ĐIỀU CHỈNH CỬA ĐI, CỬA SỔ

CHỦ ĐẦU TƯ:  
CÔNG TY TNHH ĐẦU TƯ  
**PHÚ VIỆT TÍN**  
ĐỊA CHỈ: LÔ 18-19 QUỐC LỘ 1A, XÃ DẦU GIẤY,  
TỈNH ĐỒNG NAI, VIỆT NAM

CTHĐT: ĐẶNG PHƯỚC BÌNH

ĐƠN VỊ THIẾT KẾ:  
CÔNG TY CỔ PHẦN TƯ VẤN THIẾT KẾ  
**BASE ARC**  
ĐỊA CHỈ: 138 ĐIỆN BIÊN PHỦ, PHƯỜNG TÂN ĐỊNH,  
TP. HỒ CHÍ MINH, VIỆT NAM

TỔNG GIÁM ĐỐC: TRẦN ĐỨC AN

CHỦ NHIỆM DỰ ÁN:

KTS. NGUYỄN THÀNH THÁI

CHỦ TRÌ THIẾT KẾ:

KTS. NGUYỄN THÀNH THÁI

THIẾT KẾ:

KTS. LÊ ĐÌNH TÂM

KIỂM TRA:

KTS. NGUYỄN ĐỨC THÁI

DỰ ÁN:

KHU DÂN CƯ A1-C1 (ĐÔ THỊ DẦU GIẤY)

ĐỊA ĐIỂM: XÃ DẦU GIẤY, TỈNH ĐỒNG NAI

CÔNG TRÌNH:

NHÀ Ở THƯƠNG MẠI LIÊN KẾ

HẠNG MỤC:

MẪU NHÀ T3-2b

TÊN BẢN VẼ:

CHI TIẾT BAN CÔNG 2

MỤC ĐÍCH PHÁT HÀNH:

BẢN VẼ MỜI THẦU

THIẾT KẾ CƠ SỞ


THIẾT KẾ BẢN VẼ THI CÔNG

BẢN VẼ HOÀN CÔNG


HOÀN THÀNH 07/2025

TỶ LỆ NTS


SỐ HIỆU BẢN VẼ A08-02

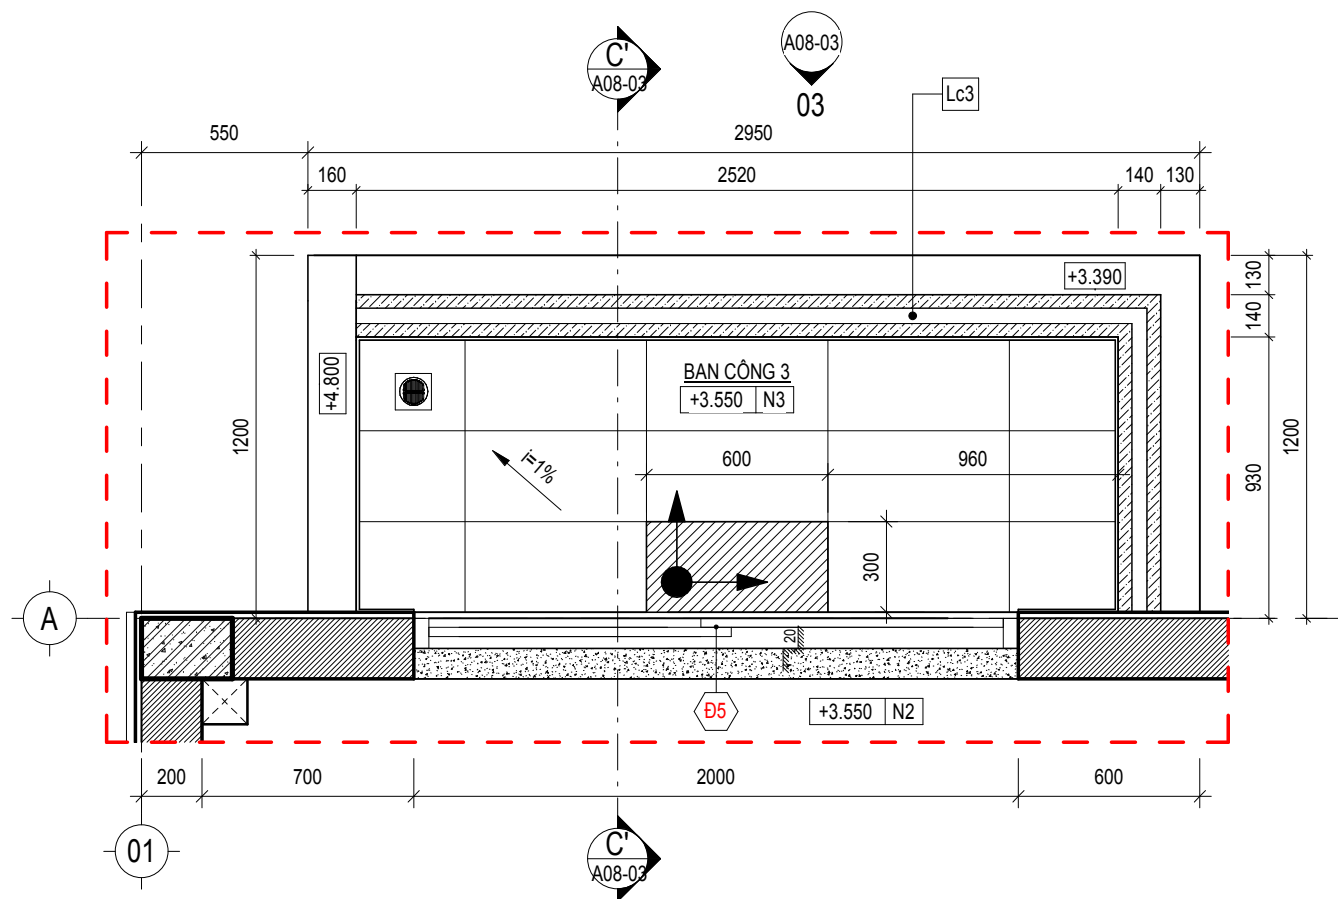

BC3 CT BAN CÔNG 3 (ĐIỂN HÌNH) - MẶT BẰNG  
TỶ LỆ 1 : 25

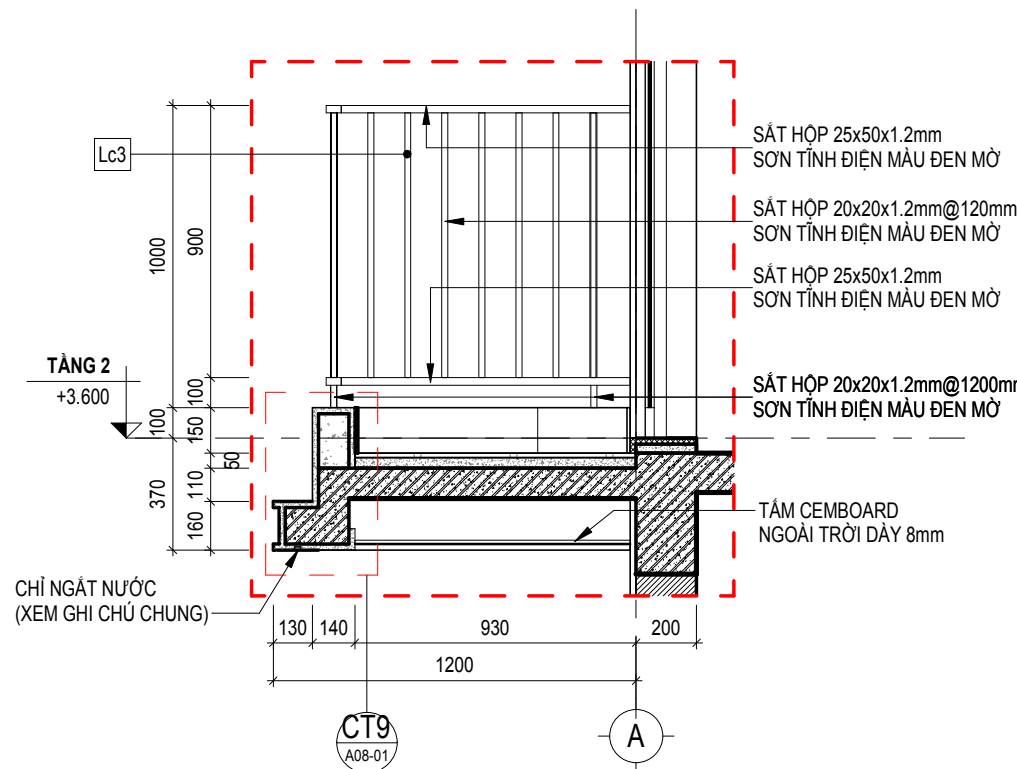

C' LAN CAN Lc3 (ĐIỂN HÌNH) - MC C'  
TỶ LỆ 1 : 25

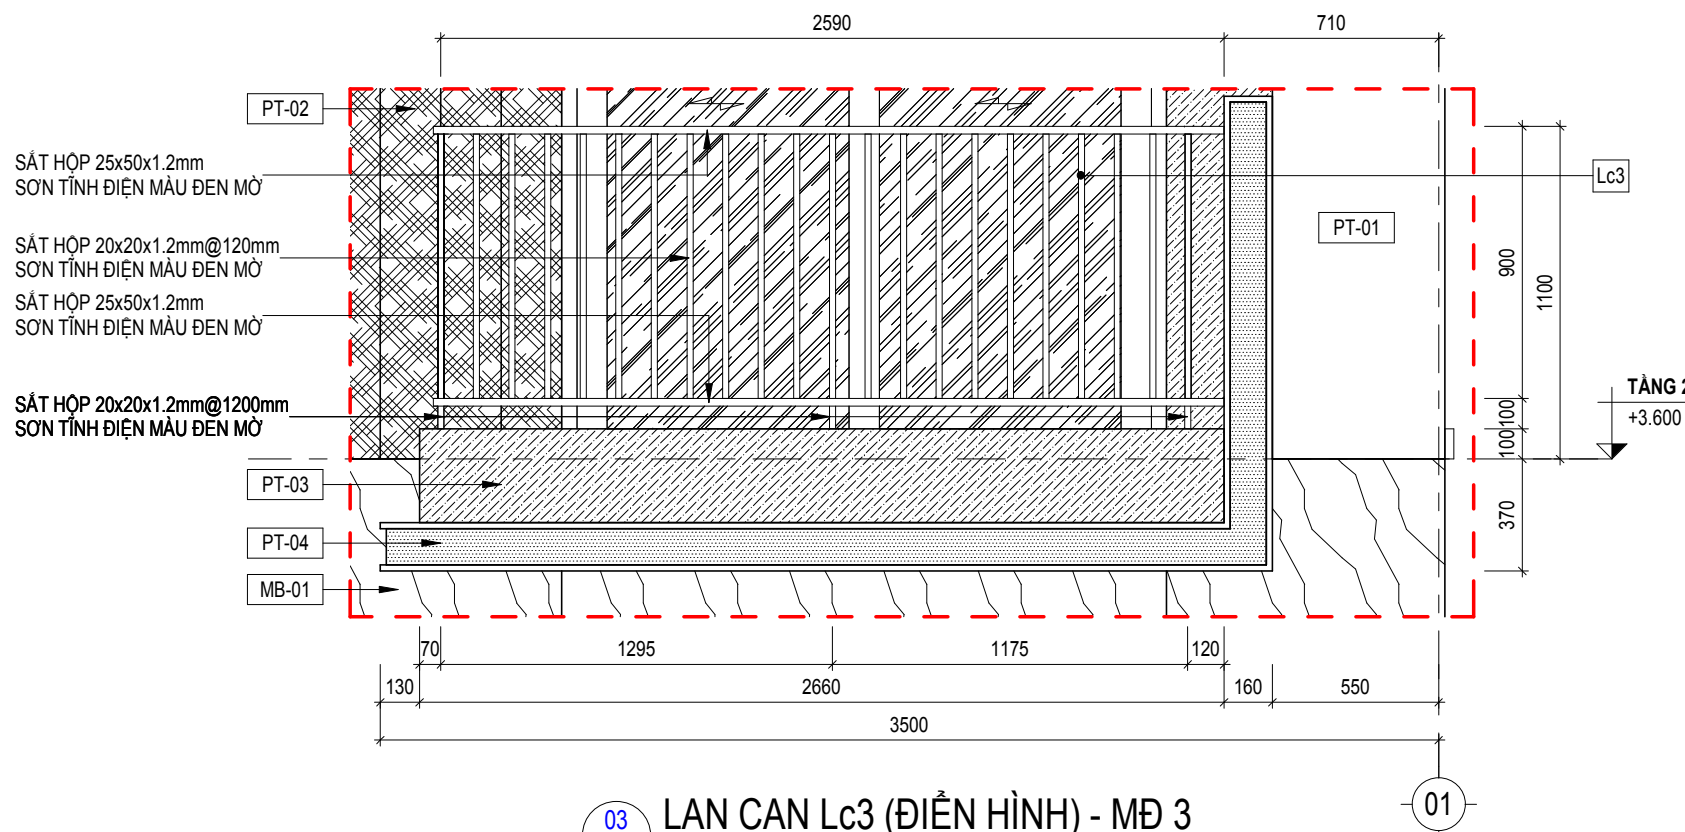

03 LAN CAN Lc3 (ĐIỂN HÌNH) - MĐ 3  
TỶ LỆ 1 : 25

GHI CHÚ:  
- CÁC ĐƠN VỊ THI CÔNG PHẢI PHỐI HỢP BẢN VẼ CỦA TẤT CẢ CÁC BỘ MÔN KHÁC NẾU THẤY SỰ KHÁC BIỆT PHẢI BÁO CHO ĐƠN VỊ THIẾT KẾ XỬ LÝ.  
- KHI XỬ LÝ SỰ KHÁC BIỆT, PHẢI THỰC HIỆN ƯU TIÊN THEO THỨ TỰ GIỮA CÁC BỘ MÔN: KIẾN TRÚC → KẾT CẤU / BỘ MÔN KHÁC; HOẶC ƯU TIÊN TRONG CÙNG BỘ MÔN: CHI TIẾT → TỔNG THỂ.  
- CÁC SỐ LƯU KỊCH THUỘC PHẢI ĐƯỢC KIỂM TRA THỰC TẾ TẠI CÔNG TRÌNH, NẾU THẤY SỰ KHÁC BIỆT SƠ VỚI BẢN VẼ THI PHẢI BÁO CHO ĐƠN VỊ THIẾT KẾ.

HIỆU CHỈNH:  
REV NGÀY NỘI DUNG

CHỦ ĐẦU TƯ:  
CÔNG TY TNHH ĐẦU TƯ  
**PHÚ VIỆT TÍN**  
ĐỊA CHỈ: LÔ 18-19 QUỐC LỘ 1A, XÃ DẦU GIẤY,  
TỈNH ĐỒNG NAI, VIỆT NAM

CTHĐT: ĐẶNG PHƯỚC BÌNH

ĐƠN VỊ THIẾT KẾ:  
CÔNG TY CỔ PHẦN TƯ VẤN THIẾT KẾ  
**BASE ARC**  
ĐỊA CHỈ: 138 ĐIỆN BIÊN PHỦ, PHƯỜNG TÂN ĐỊNH,  
TP. HỒ CHÍ MINH, VIỆT NAM

TỔNG GIÁM ĐỐC: TRẦN ĐỨC AN

CHỦ NHIỆM DỰ ÁN:

KTS. NGUYỄN THÀNH THÁI

CHỦ TRÌ THIẾT KẾ:

KTS. NGUYỄN THÀNH THÁI

THIẾT KẾ:

KTS. LÊ ĐÌNH TÂM

KIỂM TRA:

KTS. NGUYỄN ĐỨC THÁI

DỰ ÁN:

KHU DÂN CƯ A1-C1 (ĐÔ THỊ DẦU GIẤY)

ĐỊA ĐIỂM: XÃ DẦU GIẤY, TỈNH ĐỒNG NAI

CÔNG TRÌNH:

NHÀ Ở THƯƠNG MẠI LIÊN KẾ

HẠNG MỤC:

MẪU NHÀ T3-2b

TÊN BẢN VẼ:

CHI TIẾT BAN CÔNG 3

MỤC ĐÍCH PHÁT HÀNH:

BẢN VẼ MỜI THẦU

THIẾT KẾ CƠ SỞ


THIẾT KẾ BẢN VẼ THI CÔNG

BẢN VẼ HOÀN CÔNG


HOÀN THÀNH 07/2025

TỶ LỆ NTS


SỐ HIỆU BẢN VẼ A08-03

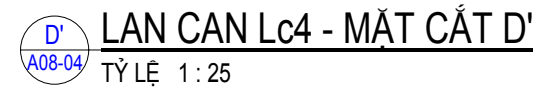

|                |        |
|----------------|--------|
| SỐ HIỆU BẢN VẼ | A08-04 |
|----------------|--------|

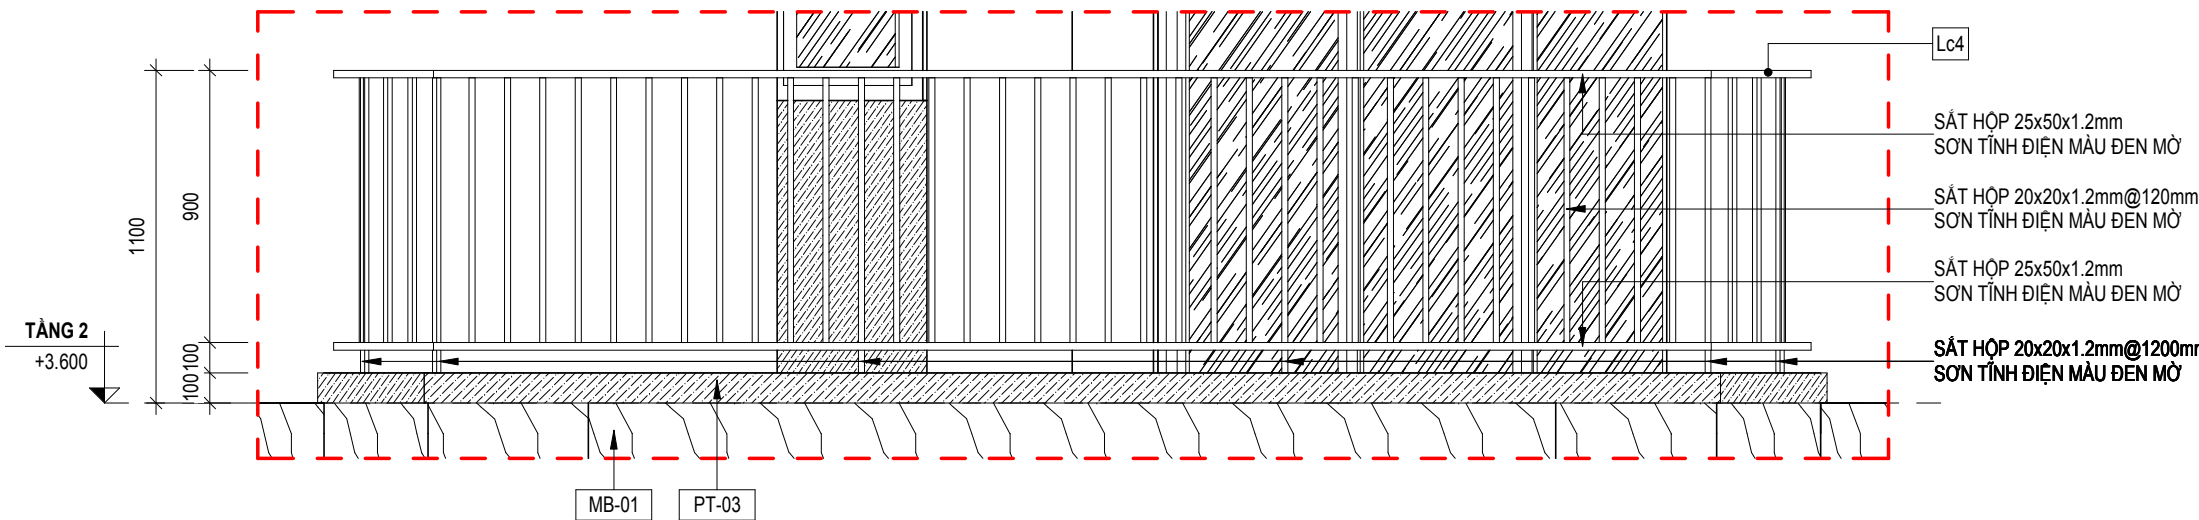

04 LAN CAN Lc4 - MĐ 04  
A08-04 TỶ LỆ 1:25

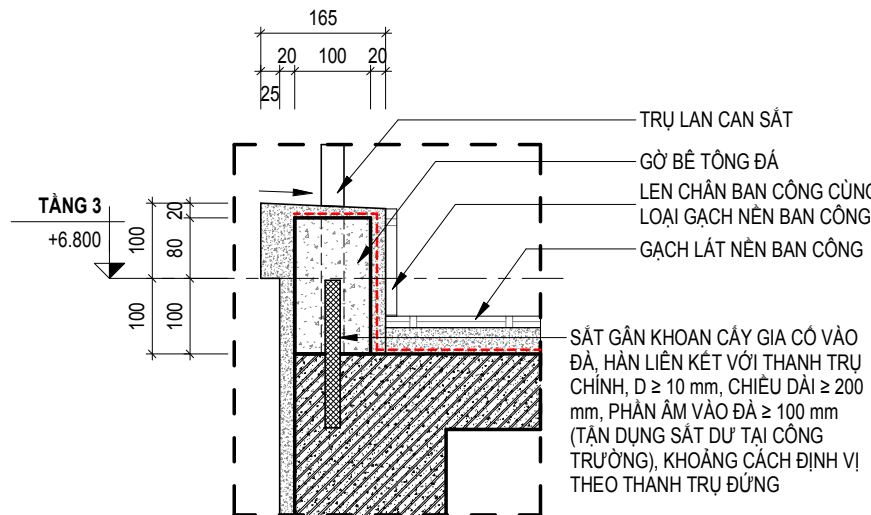

CT11 - CT GỜ CHỈ BAN CÔNG  
A08-04 TỶ LỆ 1:10

GHI CHÚ:  
- CÁC ĐƠN VỊ THI CÔNG PHẢI PHỐI HỢP BẢN VẼ CỦA TẤT CẢ CÁC BỘ MÔN KHÁC NẾU THẤY SỰ KHÁC BIỆT PHẢI BẢO CHO ĐƠN VỊ THIẾT KẾ XỬ LÝ.  
- KHI XỬ LÝ SỰ KHÁC BIỆT, PHẢI THỰC HIỆN ƯU TIÊN THEO THỨ TỰ GIỮA CÁC BỘ MÔN: KIẾN TRÚC → KẾT CẤU / BỘ MÔN KHÁC; HOẶC ƯU TIÊN TRONG CÙNG BỘ MÔN: CHI TIẾT → TỔNG THỂ  
- CÁC SỐ LƯỢNG KÍCH THƯỚC PHẢI ĐƯỢC KIỂM TRA THỰC TẾ TẠI CÔNG TRÌNH, NẾU THẤY SỰ KHÁC BIỆT SƠ VỚI BẢN VẼ THI PHẢI BẢO CHO ĐƠN VỊ THIẾT KẾ.

HIỆU CHỈNH:  
REV NGÀY NỘI DUNG

CHỦ ĐẦU TƯ:  
CÔNG TY TNHH ĐẦU TƯ  
**PHÚ VIỆT TÍN**  
ĐỊA CHỈ: LÔ 18-19 QUỐC LỘ 1A, XÃ DẦU GIẤY,  
TỈNH ĐỒNG NAI, VIỆT NAM

CTHĐT: ĐẶNG PHƯỚC BÌNH

ĐƠN VỊ THIẾT KẾ:  
CÔNG TY CỔ PHẦN TƯ VẤN THIẾT KẾ  
**BASE ARC**  
ĐỊA CHỈ: 138 ĐIỆN BIÊN PHỦ, PHƯỜNG TÂN ĐỊNH,  
TP. HỒ CHÍ MINH, VIỆT NAM

TỔNG GIÁM ĐỐC: TRẦN ĐỨC AN

CHỦ NHIỆM DỰ ÁN:

KTS. NGUYỄN THÀNH THÁI

CHỦ TRÌ THIẾT KẾ:

KTS. NGUYỄN THÀNH THÁI

THIẾT KẾ:

KTS. LÊ ĐÌNH TÂM

KIỂM TRA:

KTS. NGUYỄN ĐỨC THÁI

DỰ ÁN:

KHU DÂN CƯ A1-C1 (ĐÔ THỊ DẦU GIẤY)

ĐỊA ĐIỂM: XÃ DẦU GIẤY, TỈNH ĐỒNG NAI

CÔNG TRÌNH:

NHÀ Ở THƯƠNG MẠI LIÊN KẾ

HẠNG MỤC:

MẪU NHÀ T3-2b

TÊN BẢN VẼ:

CHI TIẾT BAN CÔNG 4 (TT)

MỤC ĐÍCH PHÁT HÀNH:

BẢN VẼ MỜI THẦU

THIẾT KẾ CƠ SỞ


✓ THIẾT KẾ BẢN VẼ THI CÔNG

BẢN VẼ HOÀN CÔNG

HOÀN THÀNH 07/2025

TỶ LỆ NTS

SỐ HIỆU BẢN VẼ A08-05

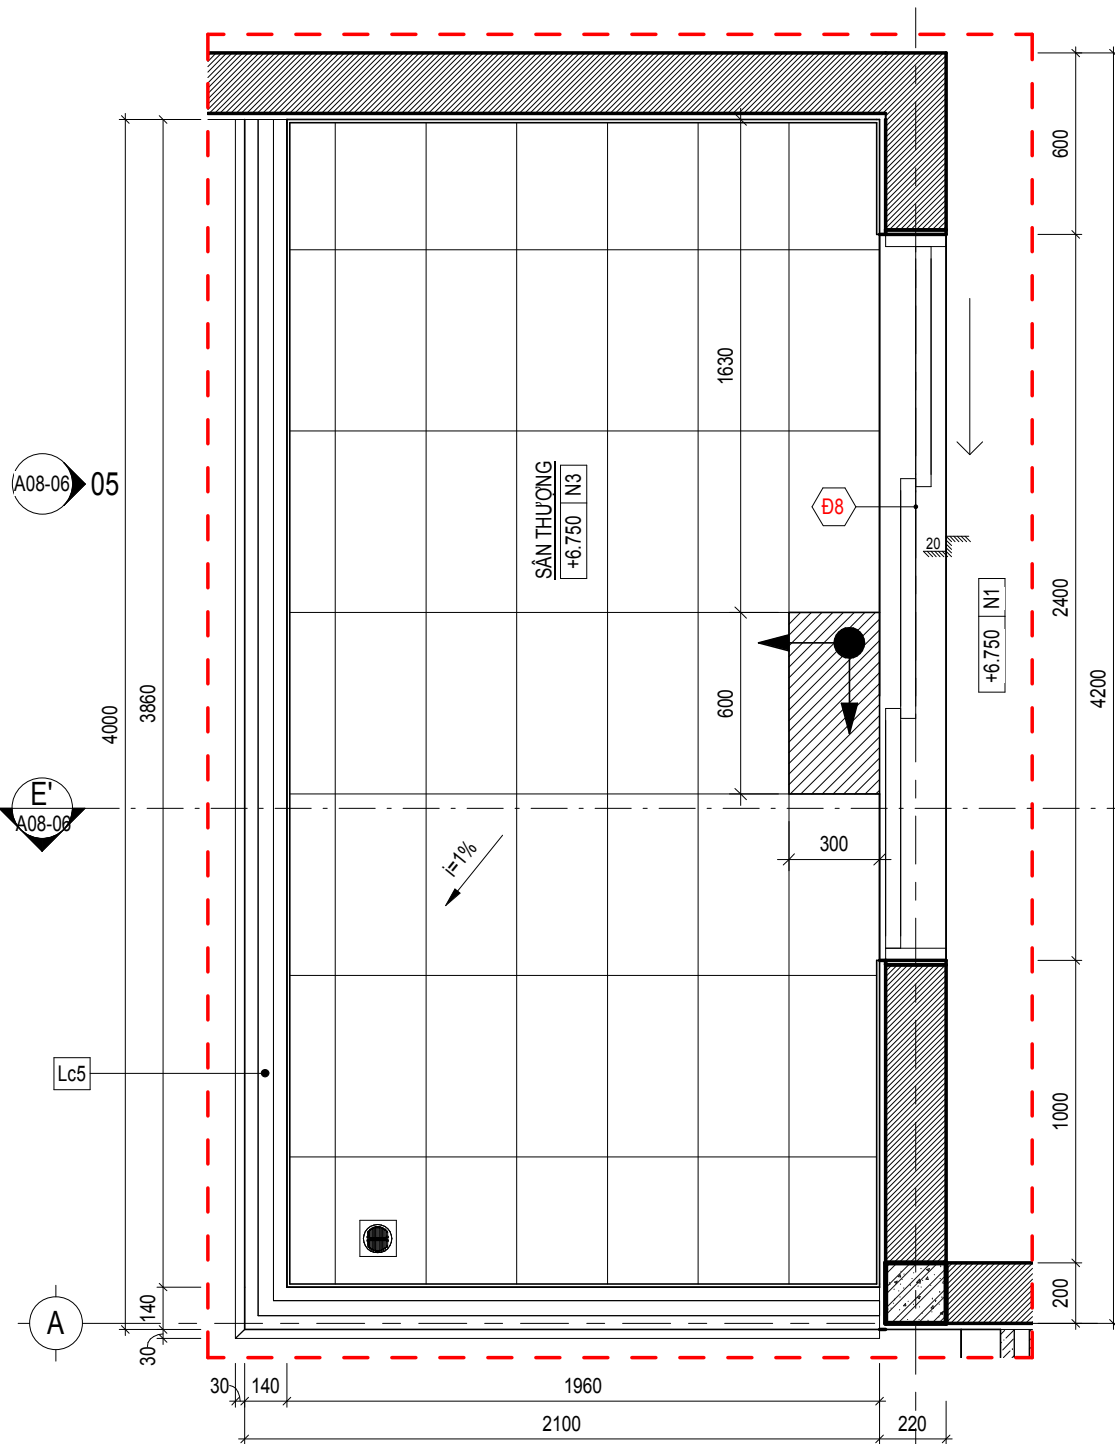


ST  
A02-53 CT SÂN THƯƠNG TẦNG 3 - MẶT BẰNG  
TỶ LỆ 1 : 25

SẮT HỘP 25x50x1.2mm  
SƠN TÍNH ĐIỆN MÀU ĐEN MỜ

SẮT HỘP 20x20x1.2mm@120mm  
SƠN TÍNH ĐIỆN MÀU ĐEN MỜ

SẮT HỘP 25x50x1.2mm  
SƠN TÍNH ĐIỆN MÀU ĐEN MỜ

SẮT HỘP 20x20x1.2mm@1200mm  
SƠN TÍNH ĐIỆN MÀU ĐEN MỜ

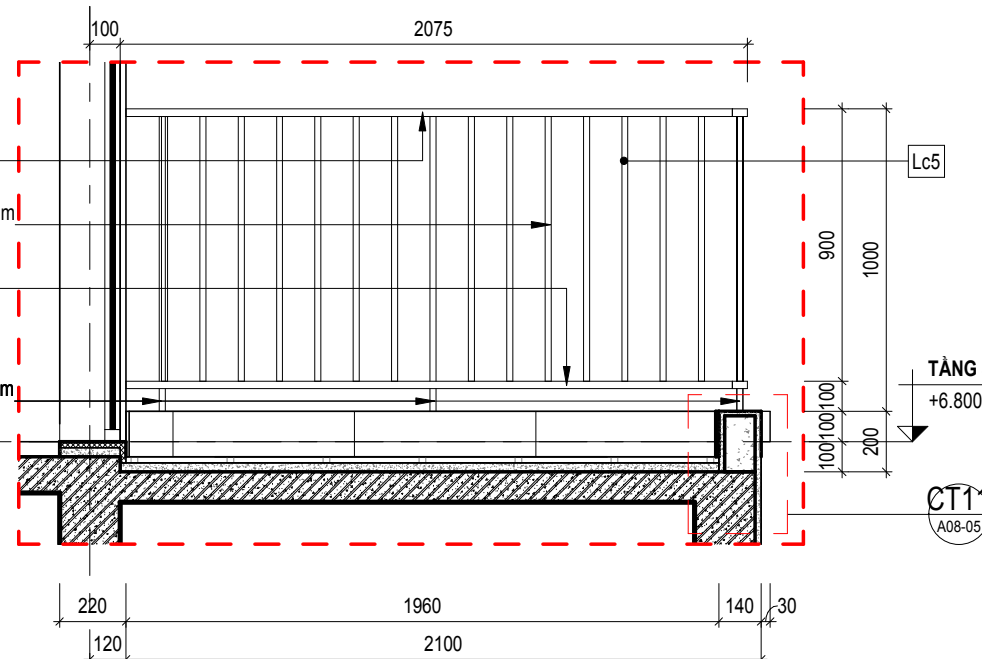

E'  
A08-06 LAN CAN Lc5 - MẶT CẮT E'  
TỶ LỆ 1 : 25


SẮT HỘP 25x50x1.2mm  
SƠN TÍNH ĐIỆN MÀU ĐEN MỜ

SẮT HỘP 20x20x1.2mm@120mm  
SƠN TÍNH ĐIỆN MÀU ĐEN MỜ

SẮT HỘP 25x50x1.2mm  
SƠN TÍNH ĐIỆN MÀU ĐEN MỜ

SẮT HỘP 20x20x1.2mm@1200mm  
SƠN TÍNH ĐIỆN MÀU ĐEN MỜ

05  
A08-06 LAN CAN Lc5 - MẶT ĐỨNG 05  
TỶ LỆ 1 : 25

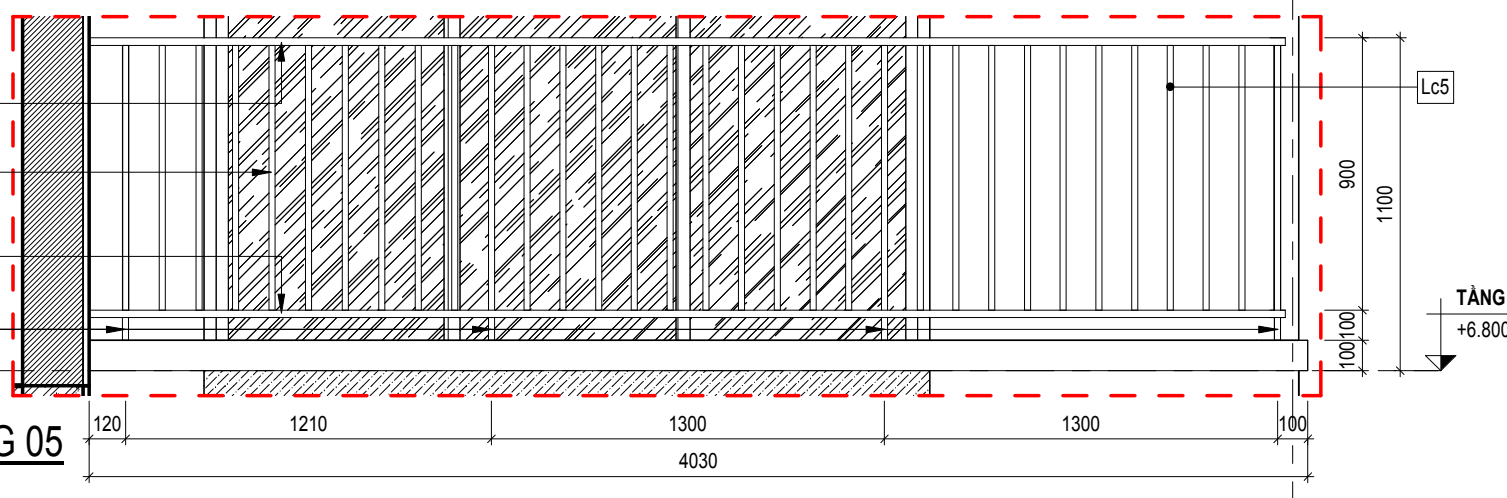

GHI CHÚ:  
- CÁC ĐƠN VỊ THI CÔNG PHẢI PHỐI HỢP BẢN VẼ CỦA TẤT CẢ CÁC BỘ MÔN KHÁC NẾU THẤY SỰ KHÁC BIỆT PHẢI BẢO CHỨNG ĐƠN VỊ THIẾT KẾ ĐỂ XỬ LÝ.  
- KHI XỬ LÝ SỰ KHÁC BIỆT, PHẢI THỰC HIỆN ƯU TIÊN THEO THỨ TỰ GIỮA CÁC BỘ MÔN: KIẾN TRÚC → KẾT CẤU / BỘ MÔN KHÁC; HOẶC ƯU TIÊN TRONG CÙNG BỘ MÔN: CHI TIẾT → TỔNG THỂ  
- CÁC SỐ LIỆU KÍCH THƯỚC PHẢI ĐƯỢC KIỂM TRA THỰC TẾ TẠI CÔNG TRÌNH, NẾU THẤY SỰ KHÁC BIỆT SƠ VỚI BẢN VẼ THI PHẢI BẢO CHỨNG ĐƠN VỊ THIẾT KẾ.

HIỆU CHỈNH:  
REV NGÀY NỘI DUNG

CHỦ ĐẦU TƯ:  
CÔNG TY TNHH ĐẦU TƯ  
**PHÚ VIỆT TÍN**  
ĐỊA CHỈ: LÔ 18-19 QUỐC LỘ 1A, XÃ DẦU GIẤY,  
TỈNH ĐỒNG NAI, VIỆT NAM

CTHĐT V: ĐẶNG PHƯỚC BÌNH

ĐƠN VỊ THIẾT KẾ:  
CÔNG TY CỔ PHẦN TƯ VẤN THIẾT KẾ  
**BASE ARC**  
ĐỊA CHỈ: 138 ĐIỆN BIÊN PHỦ, PHƯỜNG TÂN ĐỊNH,  
TP. HỒ CHÍ MINH, VIỆT NAM

TỔNG GIÁM ĐỐC: TRẦN ĐỨC AN

CHỦ NHIỆM DỰ ÁN:

KTS. NGUYỄN THÀNH THÁI

CHỦ TRÌ THIẾT KẾ:

KTS. NGUYỄN THÀNH THÁI

THIẾT KẾ:

KTS. LÊ ĐÌNH TÂM

KIỂM TRA:

KTS. NGUYỄN ĐỨC THÁI

DỰ ÁN:

KHU DÂN CƯ A1-C1 (ĐÔ THỊ DẦU GIẤY)

ĐỊA ĐIỂM: XÃ DẦU GIẤY, TỈNH ĐỒNG NAI

CÔNG TRÌNH:

NHÀ Ở THƯƠNG MẠI LIÊN KẾ

HẠNG MỤC:

MẪU NHÀ T3-2b

TÊN BẢN VẼ:

CHI TIẾT SÂN THƯƠNG TẦNG 3

MỤC ĐÍCH PHÁT HÀNH:

BẢN VẼ MỜI THẦU

THIẾT KẾ CƠ SỞ




THIẾT KẾ BẢN VẼ THI CÔNG

BẢN VẼ HOÀN CÔNG


HOÀN THÀNH 07/2025

TỶ LỆ NTS

SỐ HIỆU BẢN VẼ A08-06

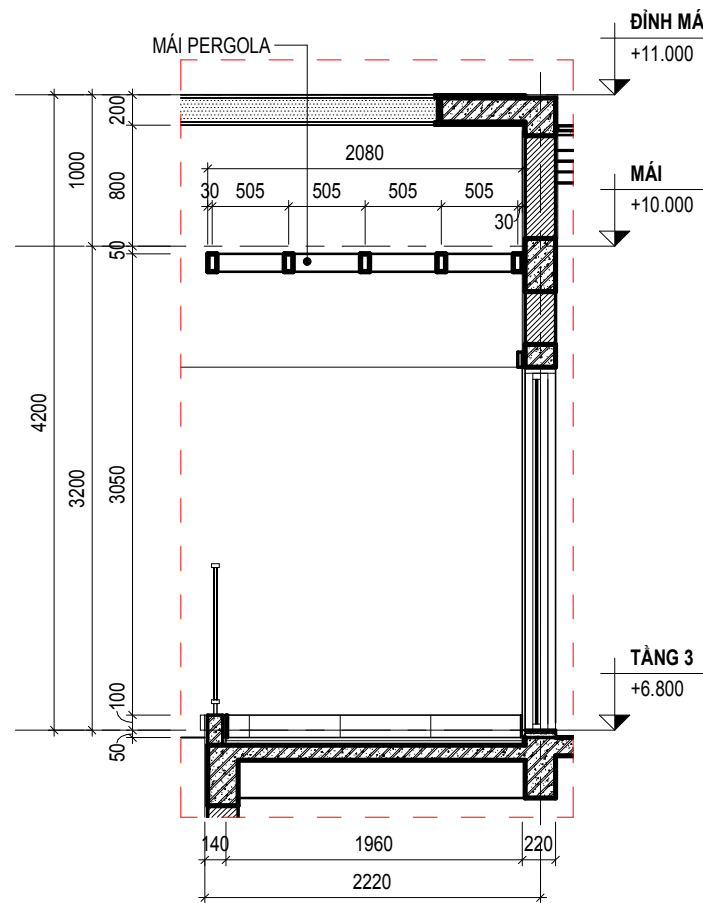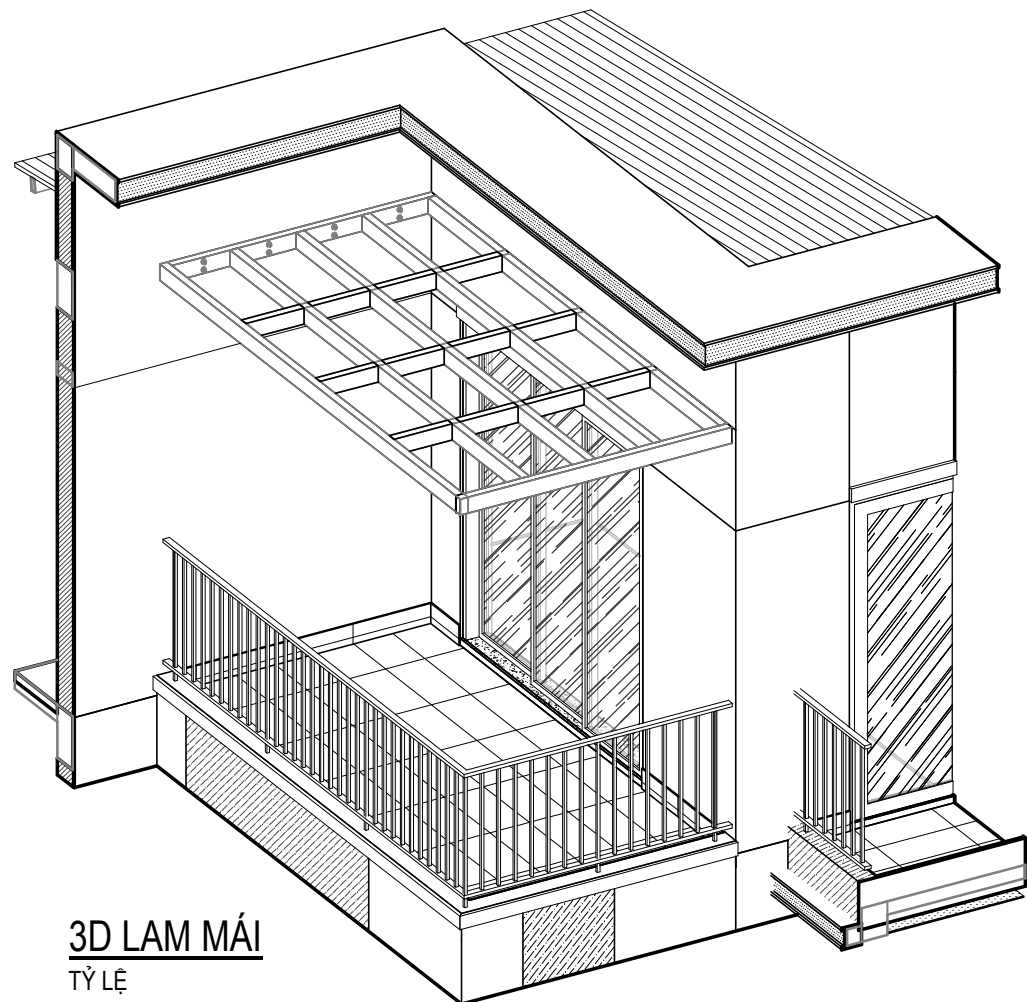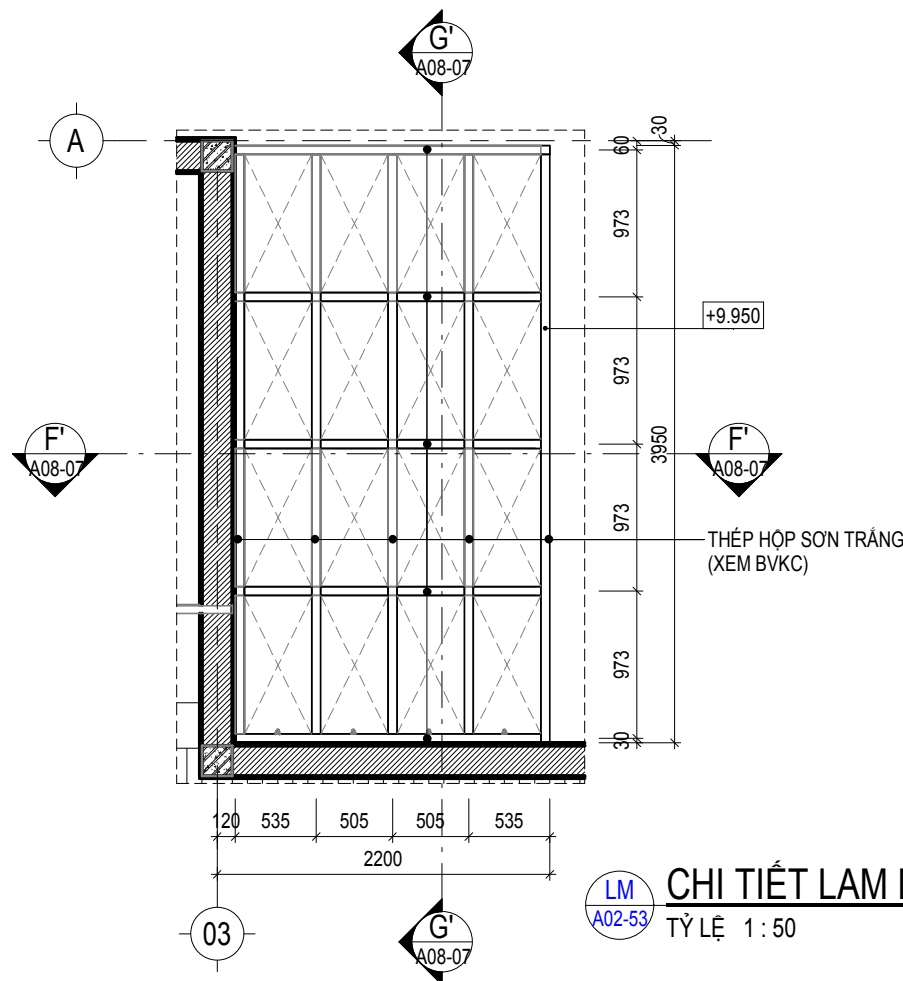

CHI TIẾT LAM MÁI - MẶT CẮT F' - 03  
TỶ LỆ 1:50

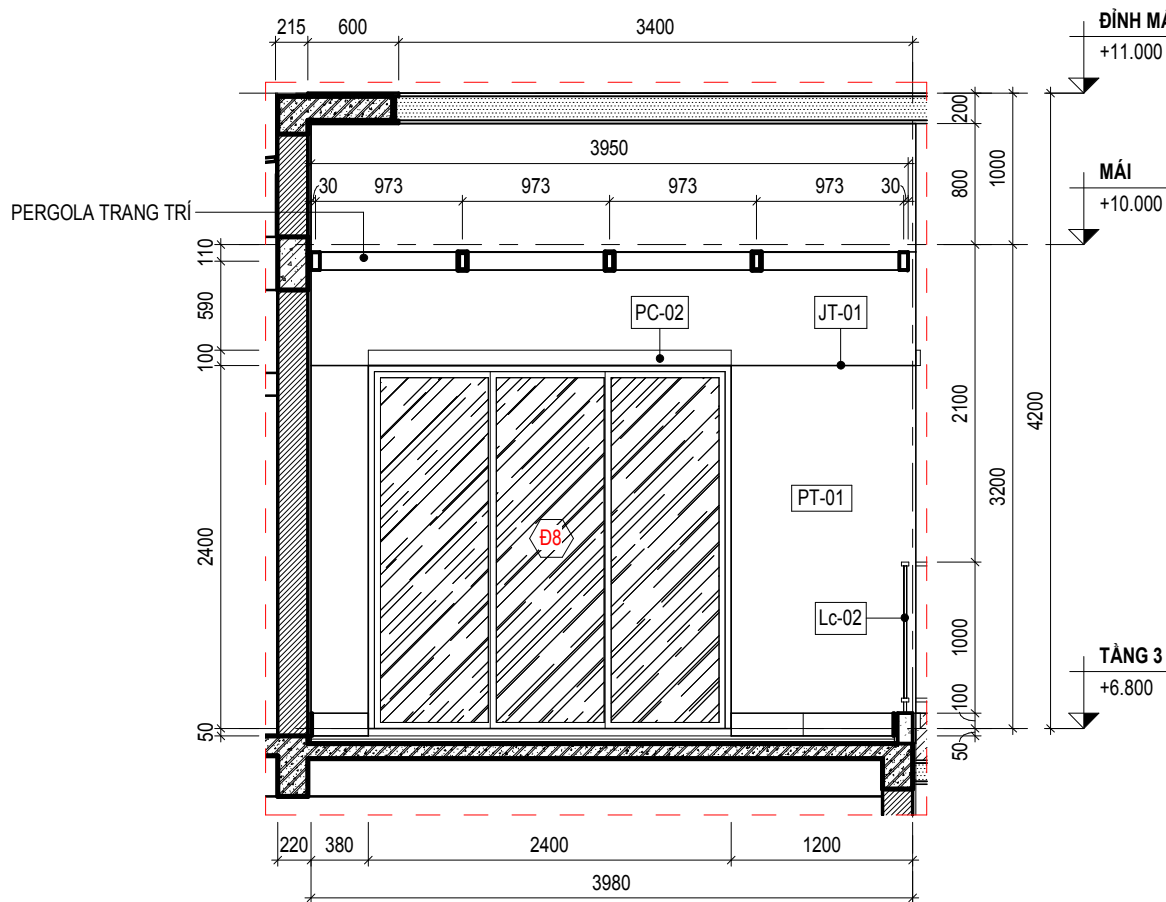

CHI TIẾT LAM MÁI - MẶT CẮT G' - 03  
TỶ LỆ 1:50

GHI CHÚ:  
- CÁC ĐƠN VỊ THI CÔNG PHẢI PHỐI HỢP BẢN VẼ CỦA TẤT CẢ CÁC BỘ MÔN KHÁC NẾU THẤY SỰ KHÁC BIỆT PHẢI BÁO CHO ĐƠN VỊ THIẾT KẾ XỬ LÝ.  
- KHI XỬ LÝ SỰ KHÁC BIỆT, PHẢI THỰC HIỆN ƯU TIÊN THEO THỨ TỰ GIỮA CÁC BỘ MÔN: KIẾN TRÚC → KẾT CẤU / BỘ MÔN KHÁC; HOẶC ƯU TIÊN TRONG CÙNG BỘ MÔN: CHI TIẾT → TỔNG THỂ  
- CÁC SỐ LIỆU KÍCH THƯỚC PHẢI ĐƯỢC KIỂM TRA THỰC TẾ TẠI CÔNG TRÌNH, NẾU THẤY SỰ KHÁC BIỆT SƠ VỚI BẢN VẼ THI PHẢI BÁO CHO ĐƠN VỊ THIẾT KẾ.

HIỆU CHỈNH:  
REV NGÀY NỘI DUNG

CHỦ ĐẦU TƯ:  
CÔNG TY TNHH ĐẦU TƯ  
**PHÚ VIỆT TÍN**  
ĐỊA CHỈ: LÔ 18-19 QUỐC LỘ 1A, XÃ DẦU GIẤY,  
TỈNH ĐỒNG NAI, VIỆT NAM

CTHĐT V: ĐẶNG PHƯỚC BÌNH

ĐƠN VỊ THIẾT KẾ:  
CÔNG TY CỔ PHẦN TƯ VẤN THIẾT KẾ  
**BASE ARC**  
ĐỊA CHỈ: 138 ĐIỆN BIÊN PHỦ, PHƯỜNG TÂN ĐỊNH,  
TP. HỒ CHÍ MINH, VIỆT NAM

TỔNG GIÁM ĐỐC: TRẦN ĐỨC AN

CHỦ NHIỆM DỰ ÁN:

KTS. NGUYỄN THÀNH THÁI

CHỦ TRÌ THIẾT KẾ:

KTS. NGUYỄN THÀNH THÁI

THIẾT KẾ:

KTS. LÊ ĐÌNH TÂM

KIỂM TRA:

KTS. NGUYỄN ĐỨC THÁI

DỰ ÁN:

KHU DÂN CƯ A1-C1 (ĐÔ THỊ DẦU GIẤY)

ĐỊA ĐIỂM: XÃ DẦU GIẤY, TỈNH ĐỒNG NAI

CÔNG TRÌNH:

NHÀ Ở THƯƠNG MẠI LIÊN KẾ

HẠNG MỤC:

MẪU NHÀ T3-2b

TÊN BẢN VẼ:

CHI TIẾT LAM MÁI TẦNG 3

MỤC ĐÍCH PHÁT HÀNH:

BẢN VẼ MỜI THẦU

THIẾT KẾ CƠ SỞ


THIẾT KẾ BẢN VẼ THI CÔNG

BẢN VẼ HOÀN CÔNG


HOÀN THÀNH 07/2025

TỶ LỆ NTS


SỐ HIỆU BẢN VẼ A08-07

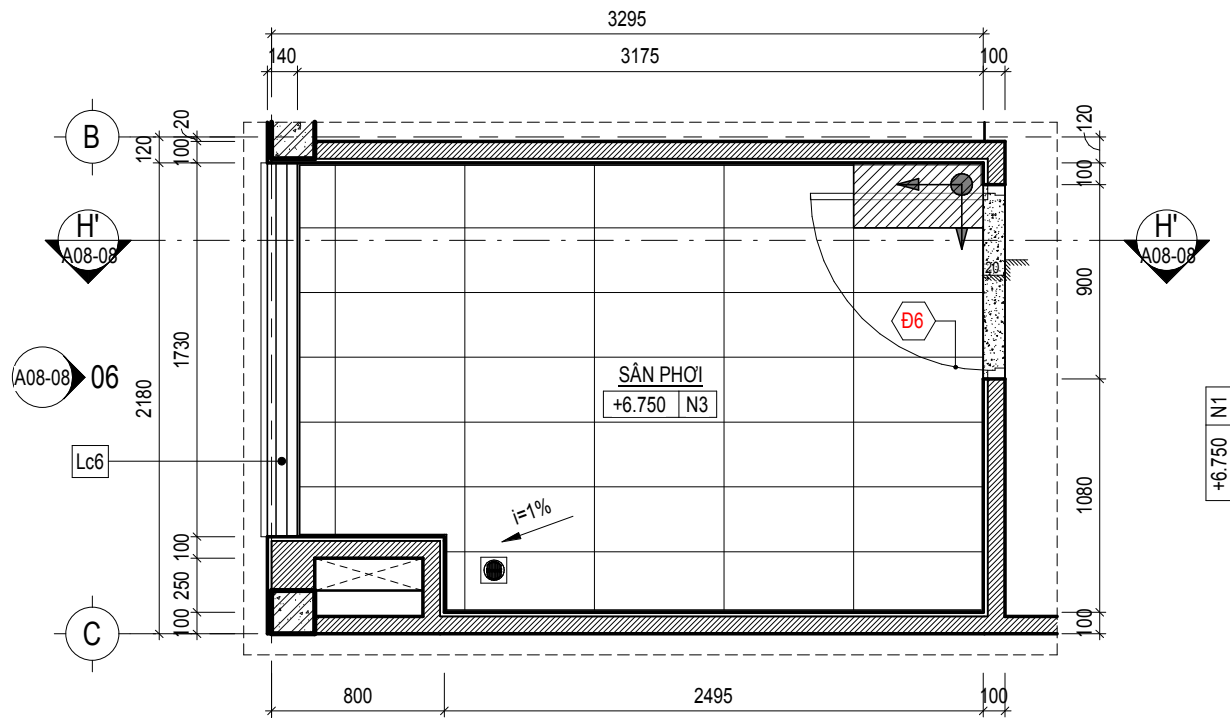


CT SÂN PHƠI TẦNG 3 - MẶT BẰNG  
TỶ LỆ 1 : 35

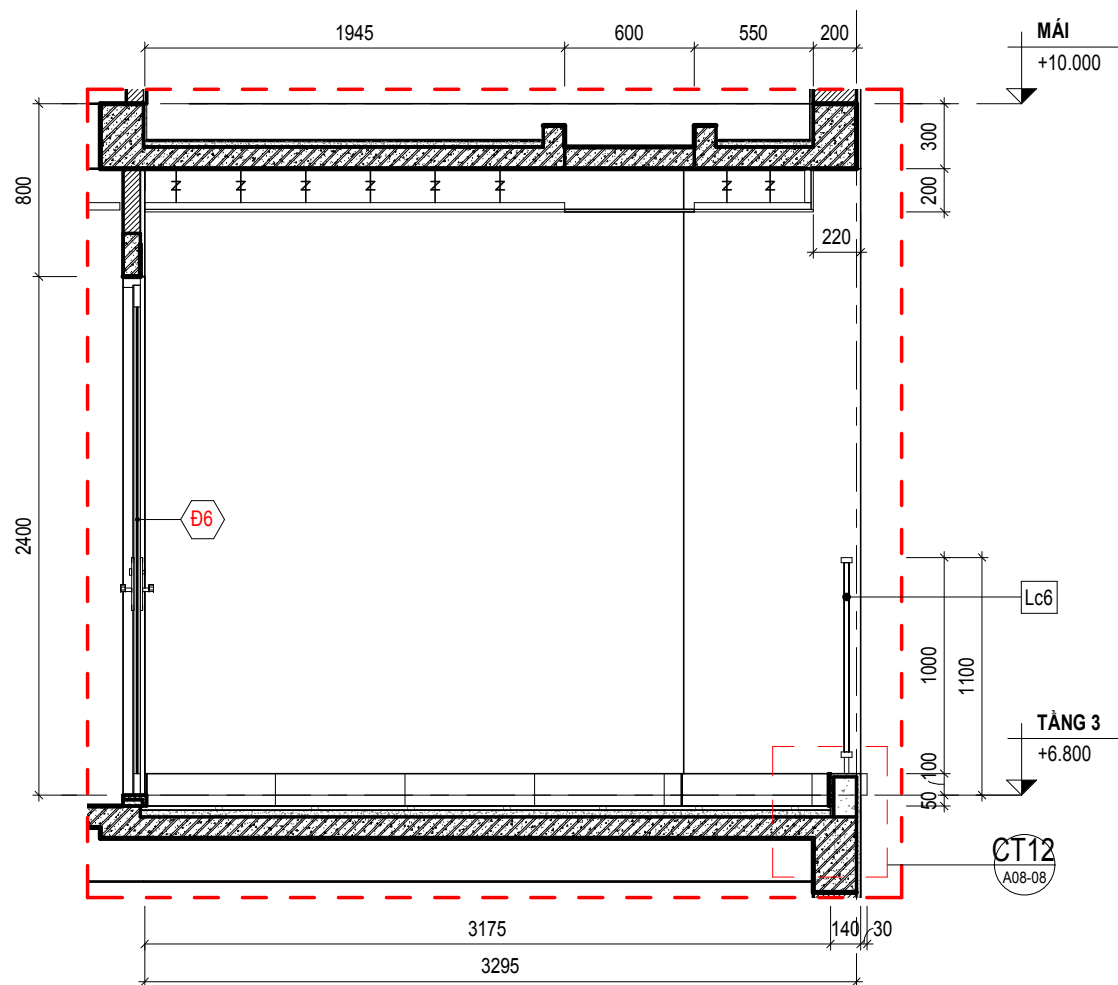

CT SÂN PHƠI TẦNG 3 - MẶT CẮT H'  
TỶ LỆ 1 : 35

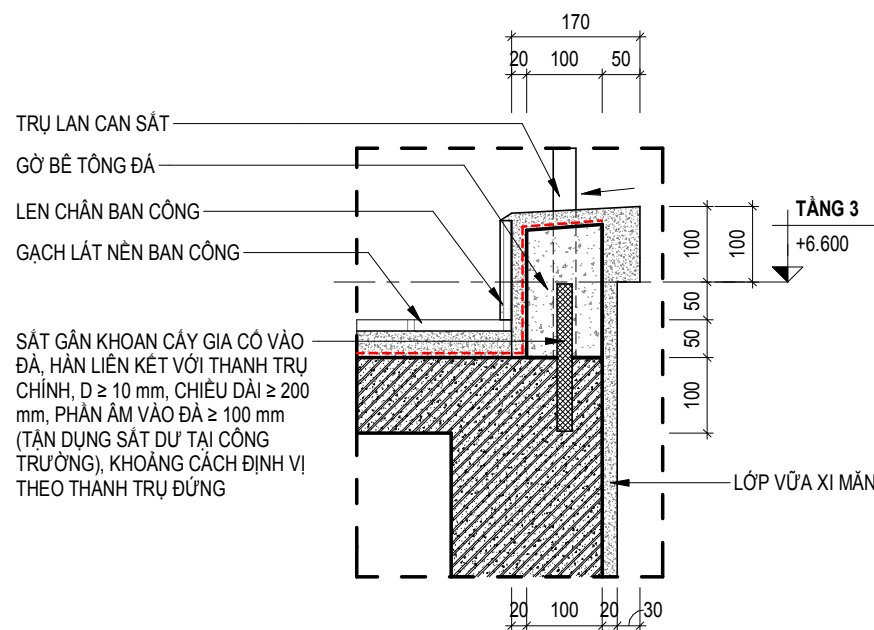

CT12 - CT GỜ CHỈ SÂN PHƠI  
TỶ LỆ 1 : 10

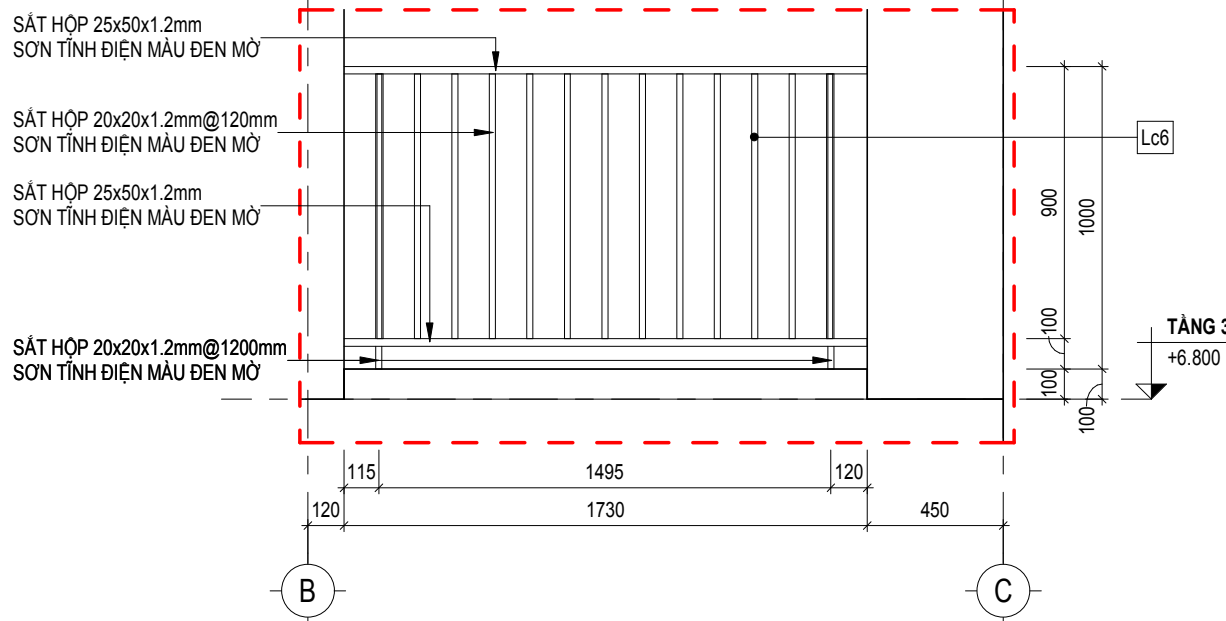

LAN CAN Lc6 - MẶT ĐỨNG 06  
TỶ LỆ 1 : 25

GHI CHÚ:  
- CÁC ĐƠN VỊ THI CÔNG PHẢI PHỐI HỢP BẢN VẼ CỦA TẤT CẢ CÁC BỘ MÔN KHÁC NẾU THẤY SỰ KHÁC BIỆT PHẢI BẢO CHO ĐƠN VỊ THIẾT KẾ XỬ LÝ.  
- KHI XỬ LÝ SỰ KHÁC BIỆT, PHẢI THỰC HIỆN ƯU TIÊN THEO THỨ TỰ GIỮA CÁC BỘ MÔN: KIẾN TRÚC → KẾT CẤU / BỘ MÔN KHÁC; HOẶC ƯU TIÊN TRONG CÙNG BỘ MÔN: CHI TIẾT → TỔNG THỂ.  
- CÁC SỐ LƯU KỊCH THUỘC PHẢI ĐƯỢC KIỂM TRA THỰC TẾ TẠI CÔNG TRÌNH, NẾU THẤY SỰ KHÁC BIỆT SƠ VỚI BẢN VẼ THI PHẢI BẢO CHO ĐƠN VỊ THIẾT KẾ.

HIỆU CHỈNH:  
REV NGÀY NỘI DUNG

CHỦ ĐẦU TƯ:  
CÔNG TY TNHH ĐẦU TƯ  
**PHÚ VIỆT TÍN**  
ĐỊA CHỈ: LÔ 18-19 QUỐC LỘ 1A, XÃ DẦU GIẤY,  
TỈNH ĐỒNG NAI, VIỆT NAM

CTHĐT: ĐẶNG PHƯỚC BÌNH

ĐƠN VỊ THIẾT KẾ:  
CÔNG TY CỔ PHẦN TƯ VẤN THIẾT KẾ  
**BASE ARC**  
ĐỊA CHỈ: 138 ĐIỆN BIÊN PHỦ, PHƯỜNG TÂN ĐỊNH,  
TP. HỒ CHÍ MINH, VIỆT NAM

TỔNG GIÁM ĐỐC: TRẦN ĐỨC AN

CHỦ NHIỆM DỰ ÁN:

KTS. NGUYỄN THÀNH THÁI

CHỦ TRÌ THIẾT KẾ:

KTS. NGUYỄN THÀNH THÁI

THIẾT KẾ:

KTS. LÊ ĐÌNH TÂM

KIỂM TRA:

KTS. NGUYỄN ĐỨC THÁI

DỰ ÁN:

KHU DÂN CƯ A1-C1 (ĐÔ THỊ DẦU GIẤY)

ĐỊA ĐIỂM: XÃ DẦU GIẤY, TỈNH ĐỒNG NAI

CÔNG TRÌNH:

NHÀ Ở THƯƠNG MẠI LIÊN KẾ

HẠNG MỤC:

MẪU NHÀ T3-2b

TÊN BẢN VẼ:

CHI TIẾT SÂN PHƠI TẦNG 3

MỤC ĐÍCH PHÁT HÀNH:

BẢN VẼ MỜI THẦU

THIẾT KẾ CƠ SỞ


THIẾT KẾ BẢN VẼ THI CÔNG

BẢN VẼ HOÀN CÔNG

HOÀN THÀNH 07/2025

TỶ LỆ NTS

SỐ HIỆU BẢN VẼ A08-08


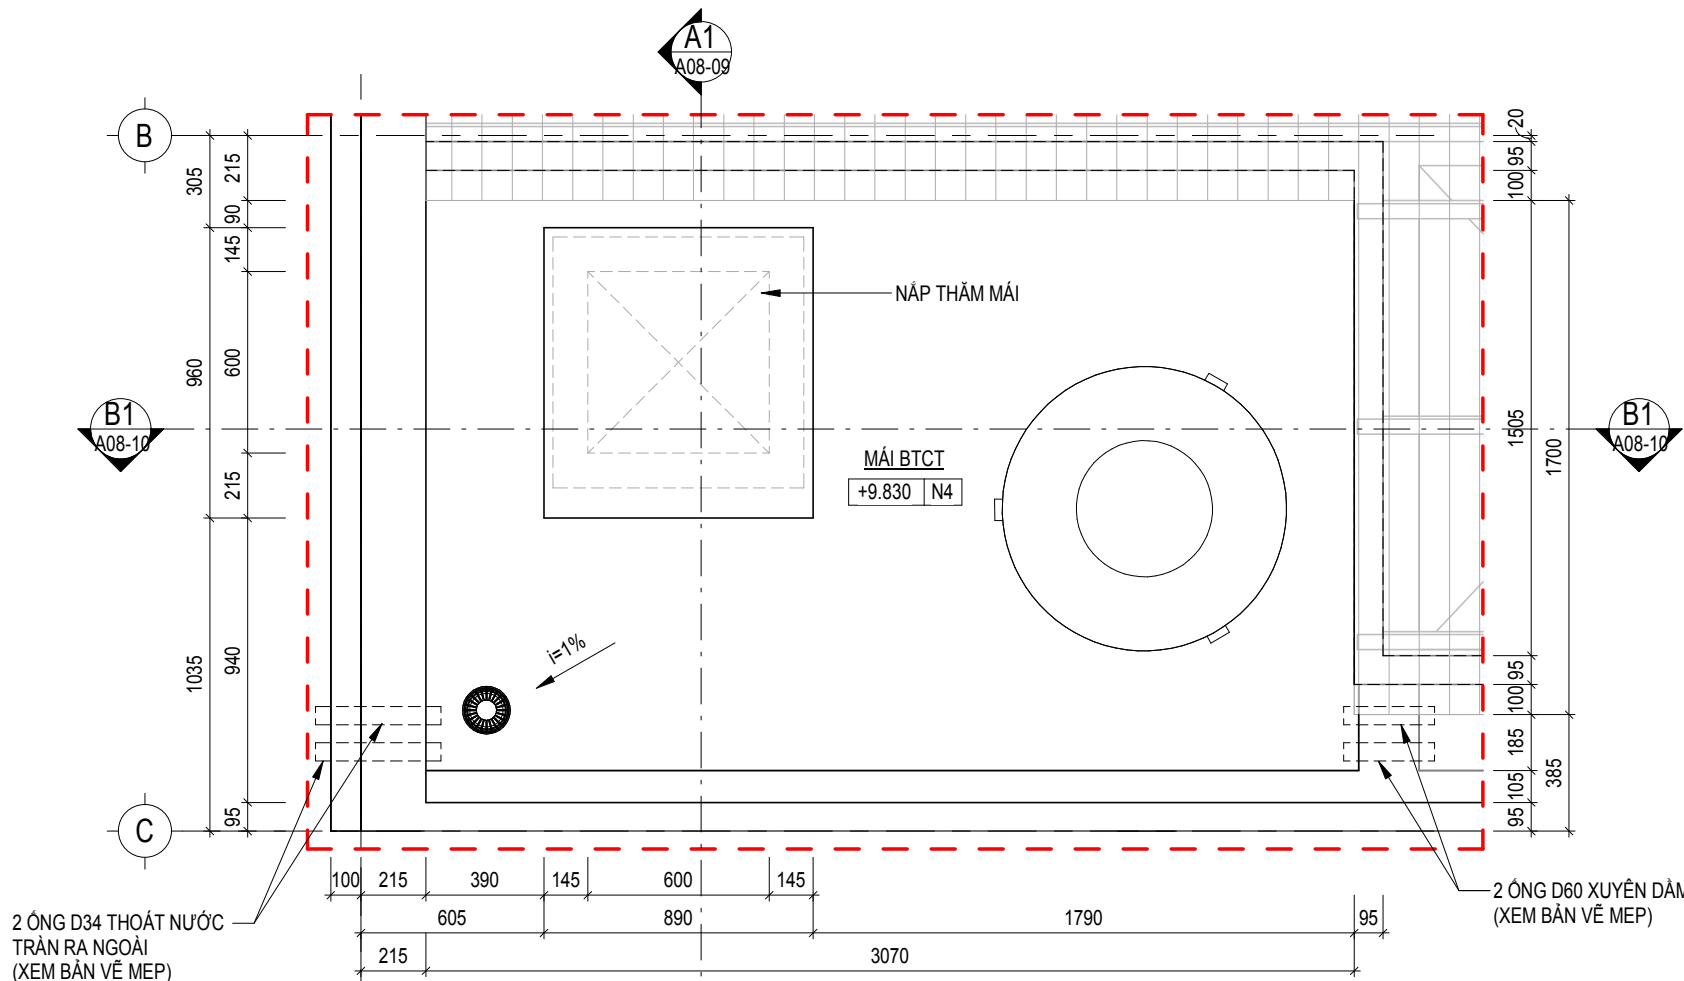


CHI TIẾT NẮP THẢM MÁI - MẶT BẰNG

TỶ LỆ 1 : 25

CT13 - LIÊN KẾT BẢN LỀ NẮP THẢM MÁI

TỶ LỆ 1 : 5

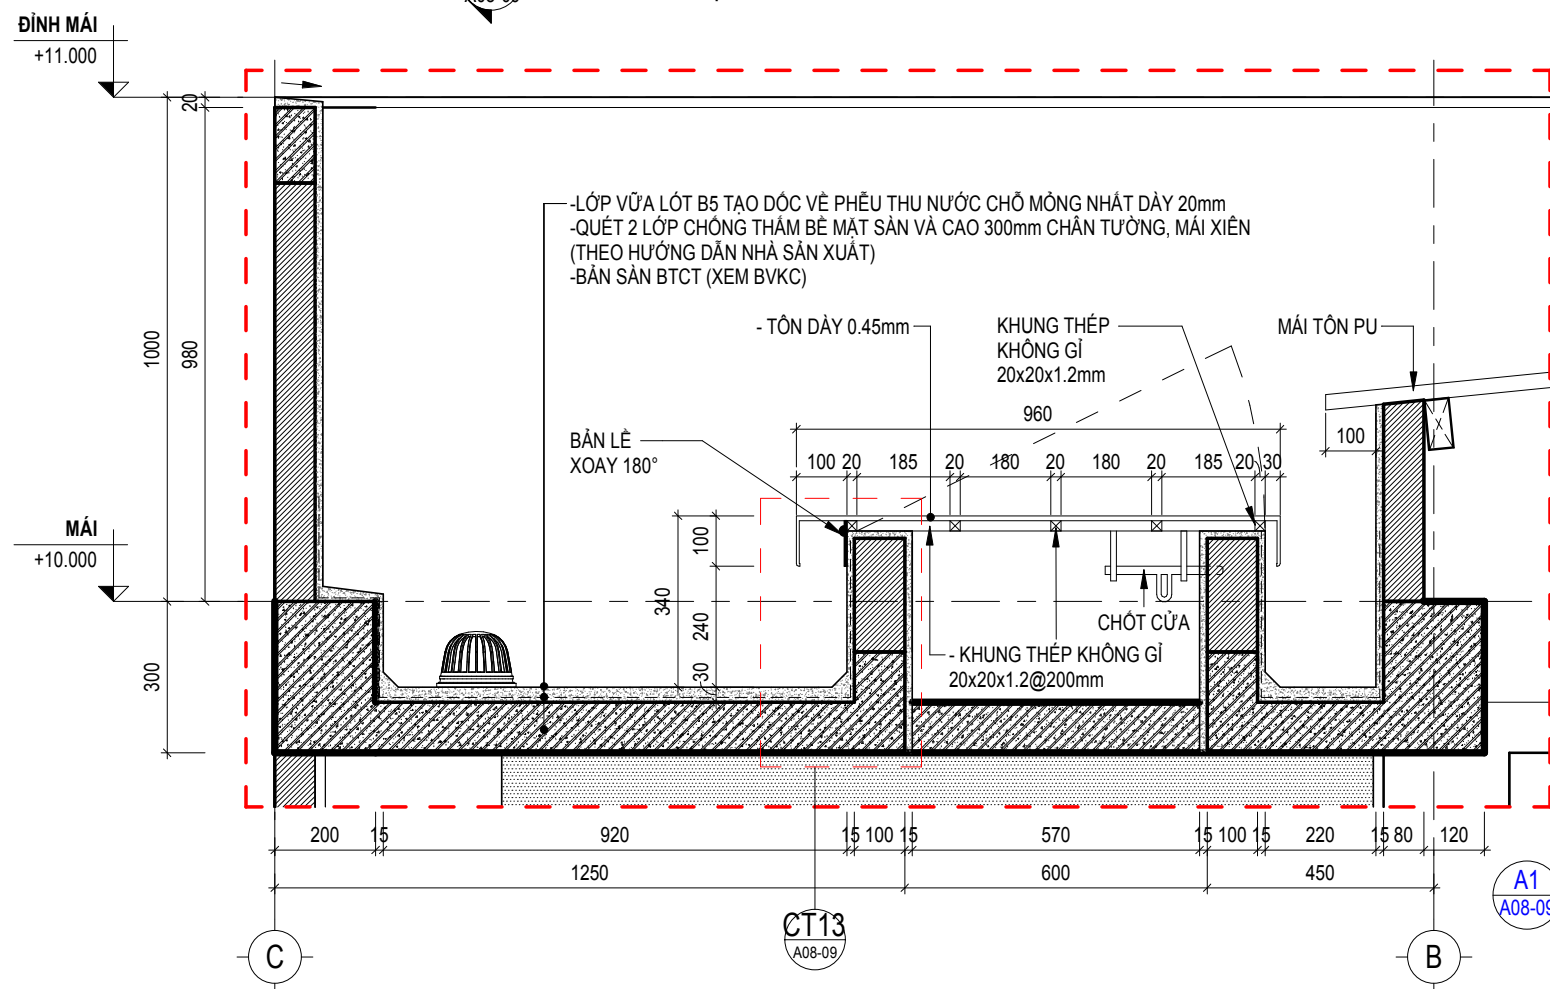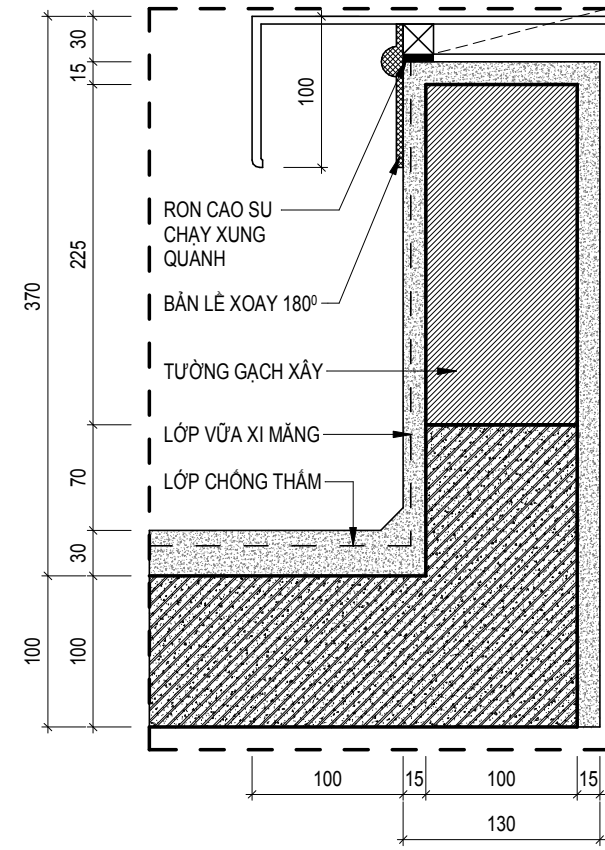

CHI TIẾT NẮP THẢM MÁI - MẶT CẮT A1

TỶ LỆ 1 : 15

GHI CHÚ:  
- CÁC ĐƠN VỊ THI CÔNG PHẢI PHỐI HỢP BẢN VẼ CỦA TẤT CẢ CÁC BỘ MÔN KHÁC NẾU THẤY SỰ KHÁC BIỆT PHẢI BẢO CHỨNG CHO ĐƠN VỊ THIẾT KẾ XỬ LÝ.  
- KHI XỬ LÝ SỰ KHÁC BIỆT, PHẢI THỰC HIỆN ƯU TIÊN THEO THỨ TỰ GIỮA CÁC BỘ MÔN: KIẾN TRÚC → KẾT CẤU / BỘ MÔN KHÁC, HOẶC ƯU TIÊN TRONG CÙNG BỘ MÔN: CHI TIẾT → TỔNG THỂ  
- CÁC SỐ LIỆU KÍCH THƯỚC PHẢI ĐƯỢC KIỂM TRA THỰC TẾ TẠI CÔNG TRÌNH, NẾU THẤY SỰ KHÁC BIỆT SƠ VỚI BẢN VẼ THI PHẢI BẢO CHỨNG ĐƠN VỊ THIẾT KẾ.

HIỆU CHỈNH:  
REV NGÀY NỘI DUNG

CHỦ ĐẦU TƯ:  
CÔNG TY TNHH ĐẦU TƯ  
**PHÚ VIỆT TÍN**  
ĐỊA CHỈ: LÔ 18-19 QUỐC LỘ 1A, XÃ DẦU GIẤY,  
TỈNH ĐỒNG NAI, VIỆT NAM

CTHĐT: ĐẶNG PHƯỚC BÌNH

ĐƠN VỊ THIẾT KẾ:  
CÔNG TY CỔ PHẦN TƯ VẤN THIẾT KẾ  
**BASE ARC**  
ĐỊA CHỈ: 138 ĐIỆN BIÊN PHỦ, PHƯỜNG TÂN ĐỊNH,  
TP. HỒ CHÍ MINH, VIỆT NAM

TỔNG GIÁM ĐỐC: TRẦN ĐỨC AN

CHỦ NHIỆM DỰ ÁN:

KTS. NGUYỄN THÀNH THÁI

CHỦ TRÌ THIẾT KẾ:

KTS. NGUYỄN THÀNH THÁI

THIẾT KẾ:

KTS. LÊ ĐÌNH TÂM

KIỂM TRA:

KTS. NGUYỄN ĐỨC THÁI

DỰ ÁN:

KHU DÂN CƯ A1-C1 (ĐÔ THỊ DẦU GIẤY)

ĐỊA ĐIỂM: XÃ DẦU GIẤY, TỈNH ĐỒNG NAI

CÔNG TRÌNH:

NHÀ Ở THƯƠNG MẠI LIÊN KẾ

HẠNG MỤC:

MẪU NHÀ T3-2b

TÊN BẢN VẼ:

CHI TIẾT NẮP THẢM MÁI, SENO

MỤC ĐÍCH PHÁT HÀNH:

BẢN VẼ MỜI THẦU

THIẾT KẾ CƠ SỞ

THIẾT KẾ BẢN VẼ THI CÔNG


BẢN VẼ HOÀN CÔNG

HOÀN THÀNH 07/2025

TỶ LỆ NTS


SỐ HIỆU BẢN VẼ A08-09

BỐ TRÍ BẠC CẤP SÂN SAU  
THEO CAO ĐỘ THỰC TẾ  
CHIỀU RỘNG BẠC 250mm  
CAO ĐỘ BẠC 150-180mm

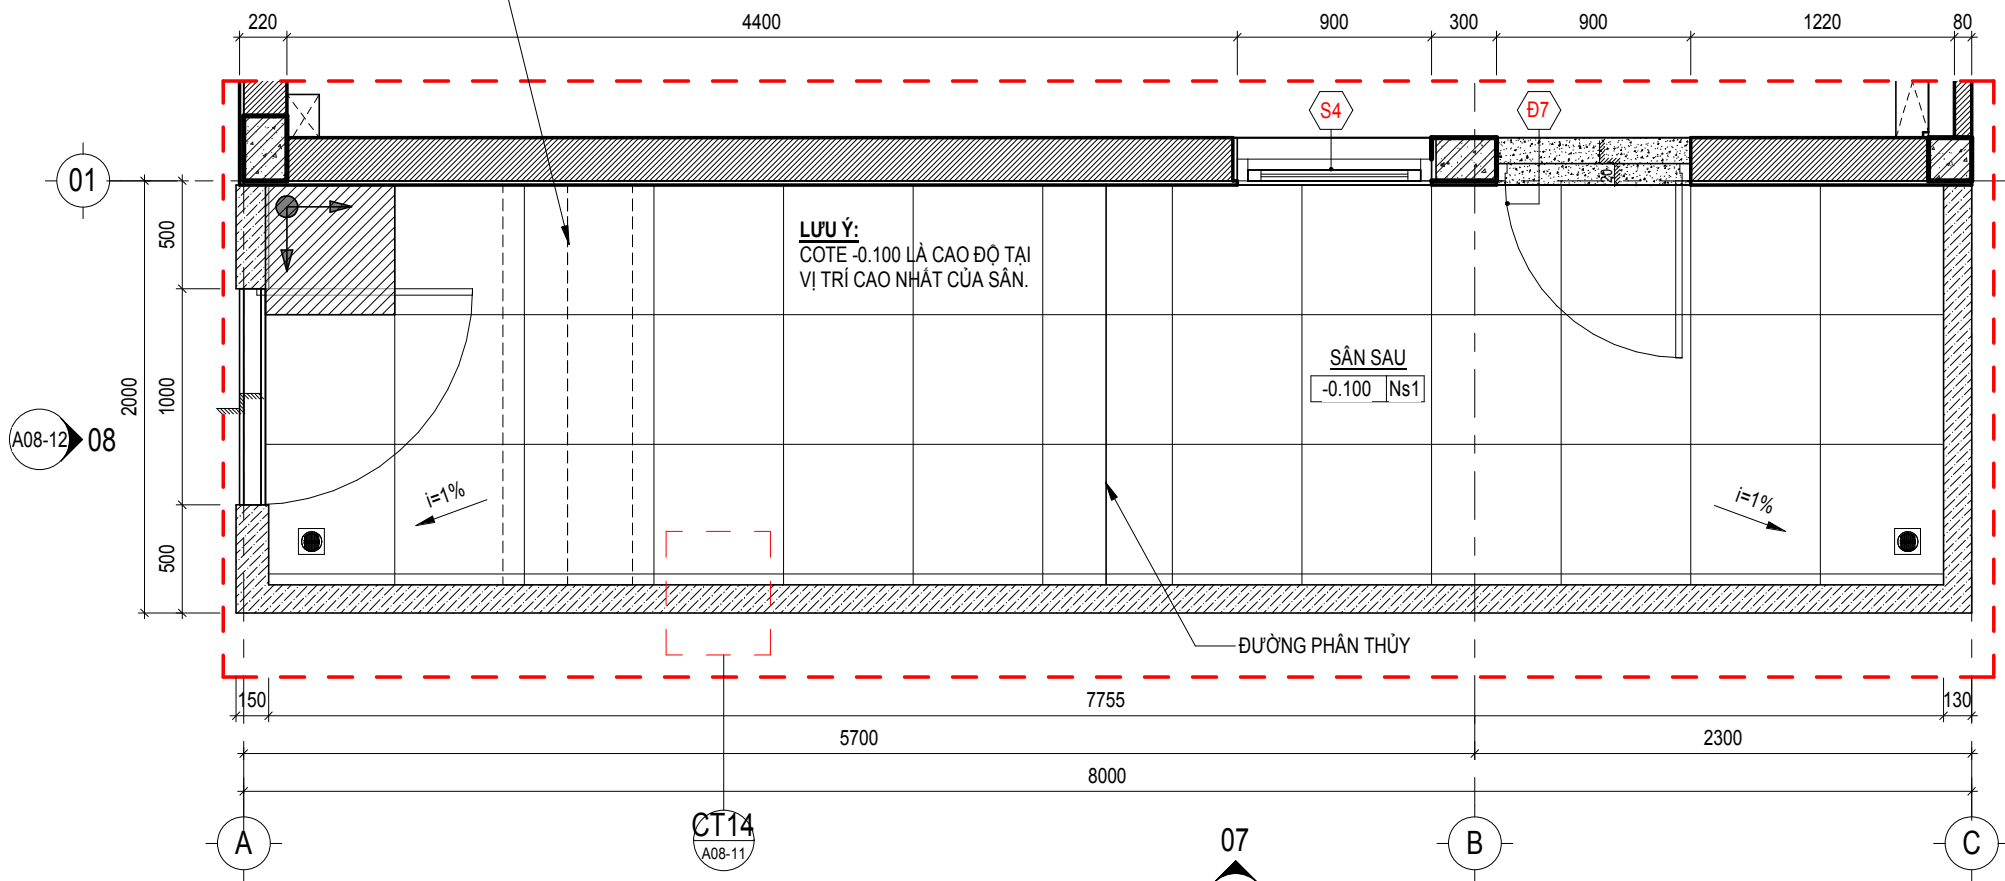

SS  
A02-51 CHI TIẾT SÂN SAU - MẶT BẰNG  
TỶ LỆ 1:35

CT14  
A08-11 CT14 - ĐÌNH TƯỜNG RÀO  
TỶ LỆ 1:5

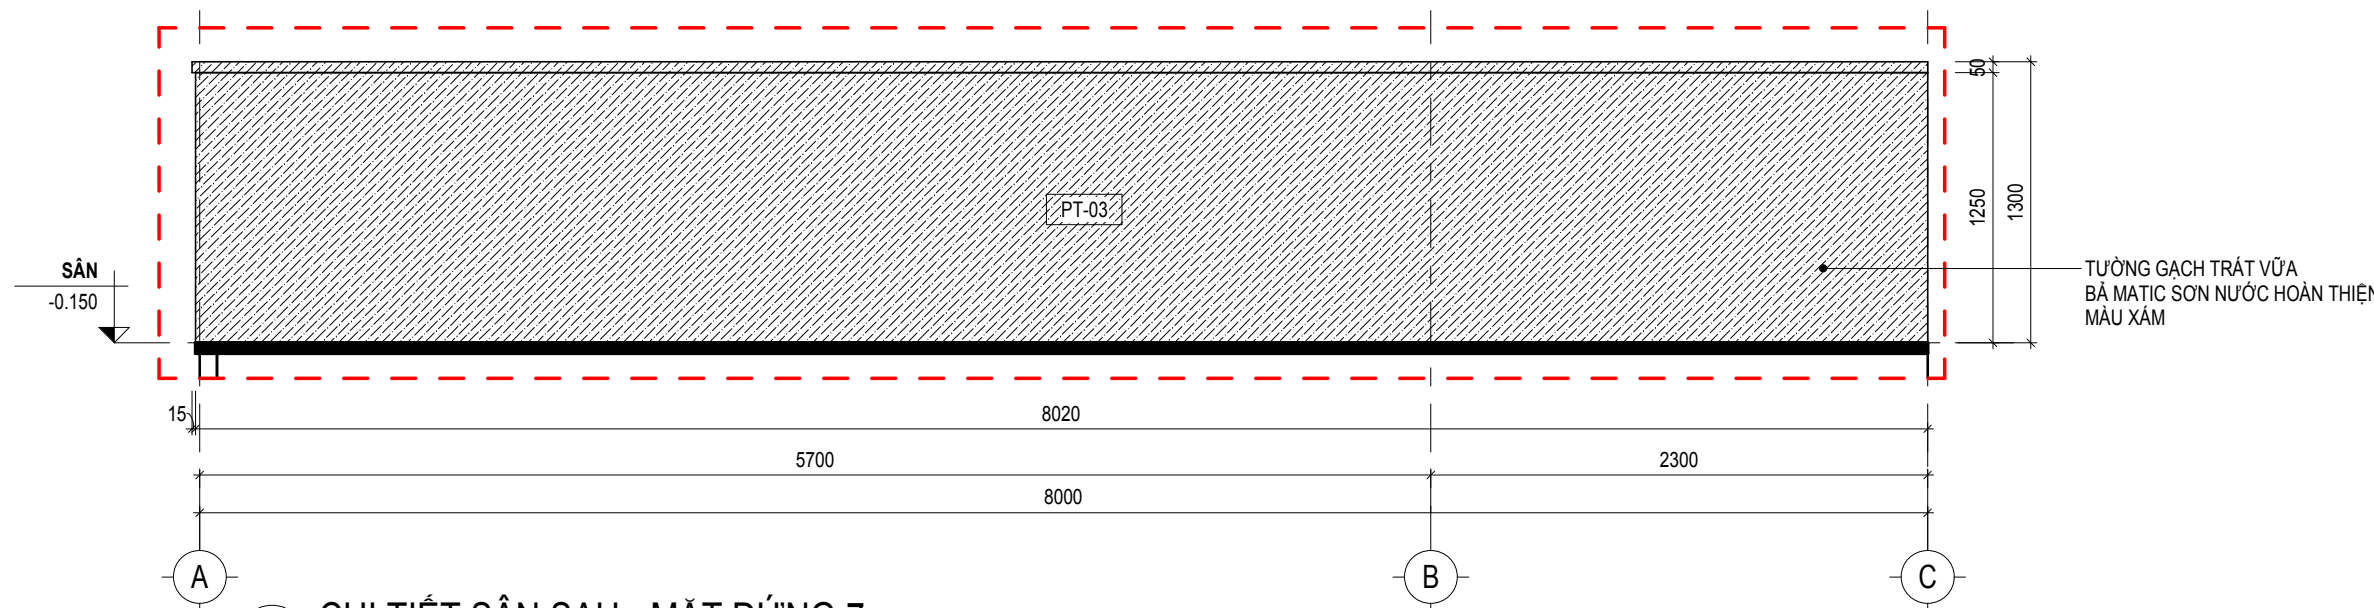

07  
A08-11 CHI TIẾT SÂN SAU - MẶT ĐỨNG 7  
TỶ LỆ 1:35

GHI CHÚ:  
- CÁC ĐƠN VỊ THI CÔNG PHẢI PHỐI HỢP BẢN VẼ CỦA TẤT CẢ CÁC BỘ MÔN  
KHÁC NẾU THẤY SỰ KHÁC BIỆT PHẢI BẢO CHỨNG ĐƠN VỊ THIẾT KẾ XỬ LÝ.  
- KHI XỬ LÝ SỰ KHÁC BIỆT, PHẢI THỰC HIỆN ƯU TIÊN THEO THỨ TỰ GIỮA CÁC  
BỘ MÔN: KIẾN TRÚC → KẾT CẤU / BỘ MÔN KHÁC; HOẶC ƯU TIÊN TRONG CÙNG  
BỘ MÔN: CHI TIẾT → TỔNG THỂ  
- CÁC SỐ LIỆU KÍCH THƯỚC PHẢI ĐƯỢC KIỂM TRA THỰC TẾ TẠI CÔNG TRÌNH,  
NẾU THẤY SỰ KHÁC BIỆT SƠ VỚI BẢN VẼ THI PHẢI BẢO CHỨNG ĐƠN VỊ THIẾT KẾ.

HIỆU CHỈNH:  
REV NGÀY NỘI DUNG

CHỦ ĐẦU TƯ:  
CÔNG TY TNHH ĐẦU TƯ  
**PHÚ VIỆT TÍN**  
ĐỊA CHỈ: LÔ 18-19 QUỐC LỘ 1A, XÃ DẦU GIẤY,  
TỈNH ĐỒNG NAI, VIỆT NAM

CHỦ ĐẦU TƯ:  
ĐẶNG PHƯỚC BÌNH

ĐƠN VỊ THIẾT KẾ:  
CÔNG TY CỔ PHẦN TƯ VẤN THIẾT KẾ  
**BASE ARC**  
ĐỊA CHỈ: 138 ĐIỆN BIÊN PHỦ, PHƯỜNG TÂN ĐỊNH,  
TP. HỒ CHÍ MINH, VIỆT NAM

TỔNG GIÁM ĐỐC: TRẦN ĐỨC AN

CHỦ NHIỆM DỰ ÁN:

KTS. NGUYỄN THÀNH THÁI

CHỦ TRÌ THIẾT KẾ:

KTS. NGUYỄN THÀNH THÁI

THIẾT KẾ:

KTS. LÊ ĐÌNH TÂM

KIỂM TRA:

KTS. NGUYỄN ĐỨC THÁI

DỰ ÁN:

KHU DÂN CƯ A1-C1 (ĐÔ THỊ DẦU GIẤY)

ĐỊA ĐIỂM: XÃ DẦU GIẤY, TỈNH ĐỒNG NAI

CÔNG TRÌNH:

NHÀ Ở THƯƠNG MẠI LIÊN KẾ

HẠNG MỤC:

MẪU NHÀ T3-2b

TÊN BẢN VẼ:

CHI TIẾT HÀNG RÀO SAU NHÀ

MỤC ĐÍCH PHÁT HÀNH:

BẢN VẼ MỜI THẦU

THIẾT KẾ CƠ SỞ

THIẾT KẾ BẢN VẼ THI CÔNG


BẢN VẼ HOÀN CÔNG

HOÀN THÀNH 07/2025

TỶ LỆ NTS

SỐ HIỆU BẢN VẼ A08-11

**GHI CHÚ:**  
H: CAO ĐỘ HÀNG RÀO TỪ COTE SÂN ĐẾN COTE TẦNG 1 THEO THỰC TẾ

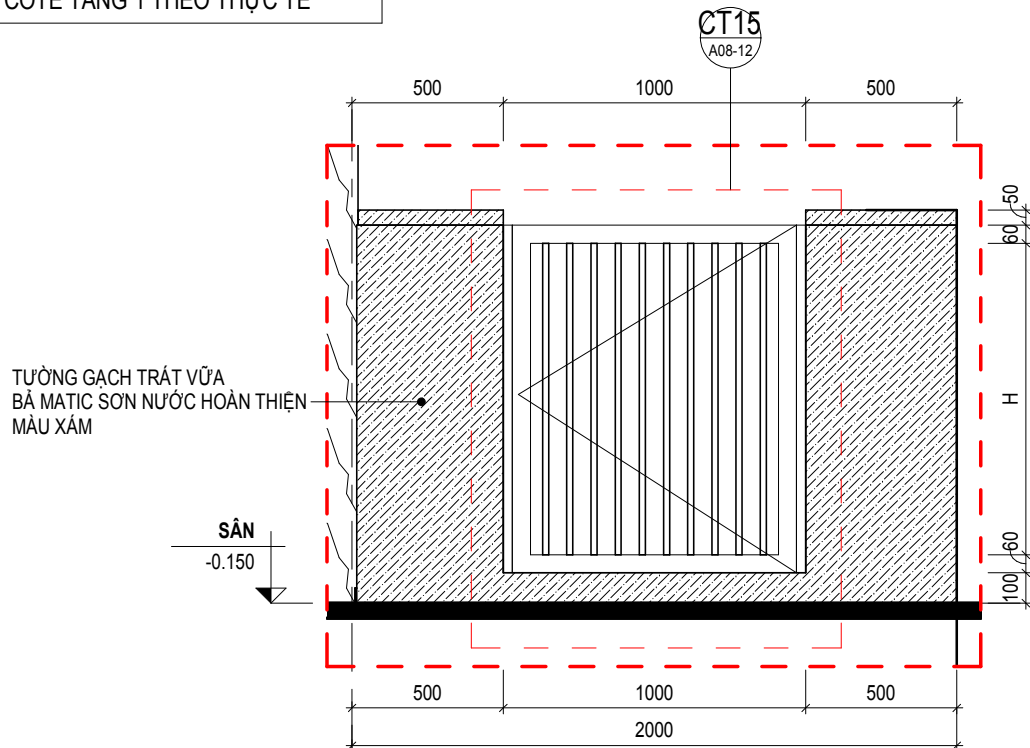

TƯỜNG GẠCH TRÁT VỮA  
BẢ MATIC SƠN NƯỚC HOÀN THIỆN  
MÀU XÁM

SÂN  
-0.150


01 08 A08-11 CHI TIẾT SÂN SAU - MẶT ĐỨNG 8  
TỶ LỆ 1 : 25

KHÓA - CHÓT NGANG  
SẮT TRÒN ĐẶC D14mm  
DÀI 120mm, CAO ĐỘ  
LẤP ĐẶT H = 1000mm

SẮT HỘP 20x20x1.2mm  
SƠN TÍNH ĐIỆN HOÀN THIỆN

SẮT HỘP 30x60x1.2mm  
SƠN TÍNH ĐIỆN HOÀN THIỆN

CHÓT ĐỨNG SẮT TRÒN ĐẶC  
D16mm CAO 500mm

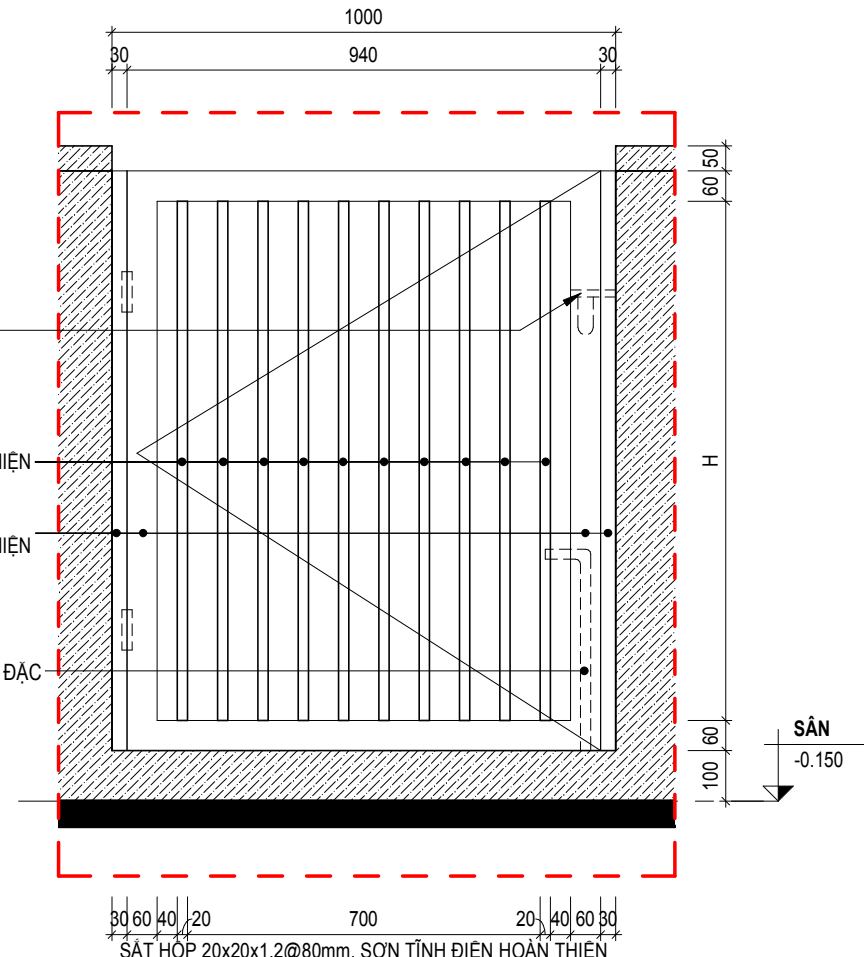

SÂN  
-0.150

CT15 A08-12 CT15 - CHI TIẾT CỔNG RÀO  
TỶ LỆ 1 : 15

**GHI CHÚ:**  
- CÁC ĐƠN VỊ THI CÔNG PHẢI PHỐI HỢP BẢN VẼ CỦA TẤT CẢ CÁC BỘ MÔN KHÁC NẾU THẤY SỰ KHÁC BIỆT PHẢI BẢO CHO ĐƠN VỊ THIẾT KẾ XỬ LÝ.  
- KHI XỬ LÝ SỰ KHÁC BIỆT, PHẢI THỰC HIỆN ƯU TIÊN THEO THỨ TỰ GIỮA CÁC BỘ MÔN: KIẾN TRÚC → KẾT CẤU / BỘ MÔN KHÁC; HOẶC ƯU TIÊN TRONG CÙNG BỘ MÔN: CHI TIẾT → TỔNG THỂ  
- CÁC SỐ LIỆU KÍCH THƯỚC PHẢI ĐƯỢC KIỂM TRA THỰC TẾ TẠI CÔNG TRÌNH, NẾU THẤY SỰ KHÁC BIỆT SƠ VỚI BẢN VẼ THI PHẢI BẢO CHO ĐƠN VỊ THIẾT KẾ.

**HIỆU CHỈNH:**

| REV | NGÀY | NỘI DUNG |
|-----|------|----------|
|-----|------|----------|

**CHỦ ĐẦU TƯ:**  
CÔNG TY TNHH ĐẦU TƯ  
**PHÚ VIỆT TÍN**  
ĐỊA CHỈ: LÔ 18-19 QUỐC LỘ 1A, XÃ DẦU GIẤY,  
TỈNH ĐỒNG NAI, VIỆT NAM

**CTHĐT:** ĐẶNG PHƯỚC BÌNH

**ĐƠN VỊ THIẾT KẾ:**  
CÔNG TY CỔ PHẦN TƯ VẤN THIẾT KẾ  
**BASE ARC**  
ĐỊA CHỈ: 138 ĐIỆN BIÊN PHỦ, PHƯỜNG TÂN ĐỊNH,  
TP. HỒ CHÍ MINH, VIỆT NAM

**TỔNG GIÁM ĐỐC:** TRẦN ĐỨC AN

**CHỦ NHIỆM DỰ ÁN:**

KTS. NGUYỄN THÀNH THÁI

**CHỦ TRÌ THIẾT KẾ:**

KTS. NGUYỄN THÀNH THÁI

**THIẾT KẾ:**

KTS. LÊ ĐÌNH TÂM

**KIỂM TRA:**

KTS. NGUYỄN ĐỨC THÁI

**DỰ ÁN:**

KHU DÂN CƯ A1-C1 (ĐÔ THỊ DẦU GIẤY)

ĐỊA ĐIỂM: XÃ DẦU GIẤY, TỈNH ĐỒNG NAI

**CÔNG TRÌNH:**

NHÀ Ở THƯƠNG MẠI LIÊN KẾ

**HẠNG MỤC:**

MẪU NHÀ T3-2b

**TÊN BẢN VẼ:**

CHI TIẾT HÀNG RÀO SAU NHÀ (TT)













**MỤC ĐÍCH PHÁT HÀNH:**

|                                     |                          |
|-------------------------------------|--------------------------|
| <input type="checkbox"/>            | BẢN VẼ MỜI THẦU          |
| <input type="checkbox"/>            | THIẾT KẾ CƠ SỞ           |
| <input checked="" type="checkbox"/> | THIẾT KẾ BẢN VẼ THI CÔNG |
| <input type="checkbox"/>            | BẢN VẼ HOÀN CÔNG         |

**HOÀN THÀNH** 07/2025


**TỶ LỆ** NTS

**SỐ HIỆU BẢN VẼ** A08-12
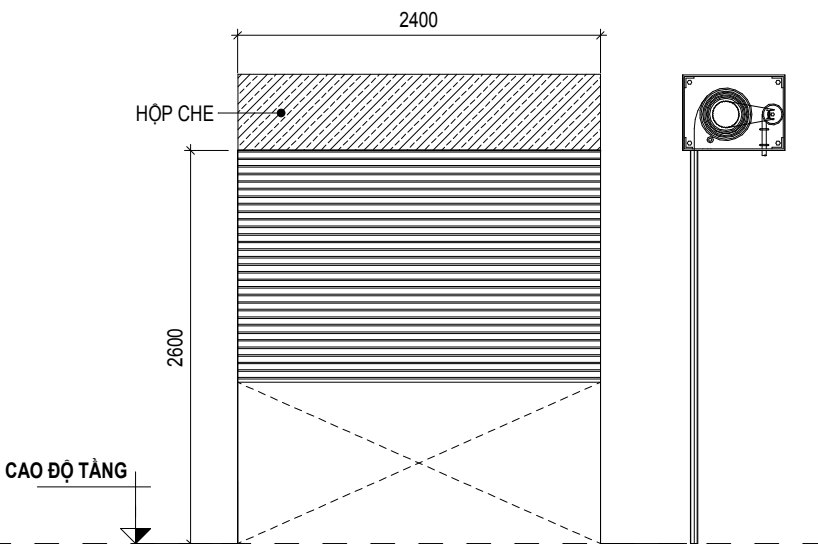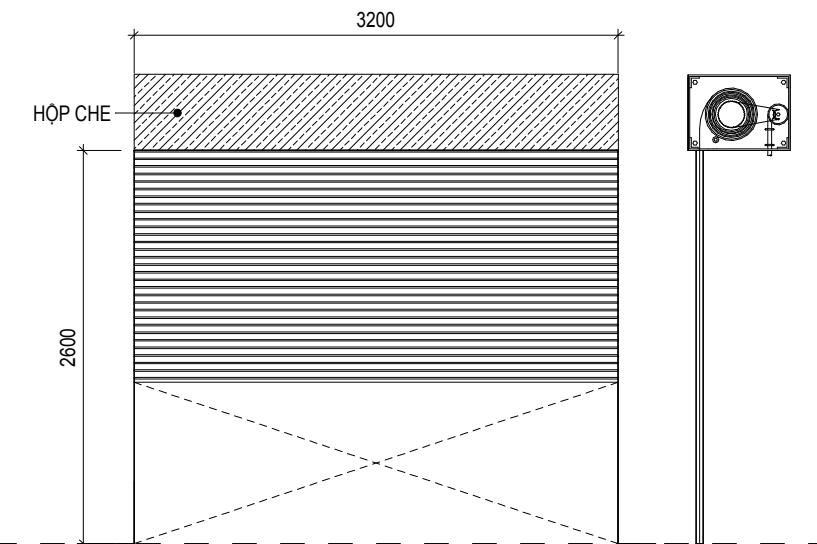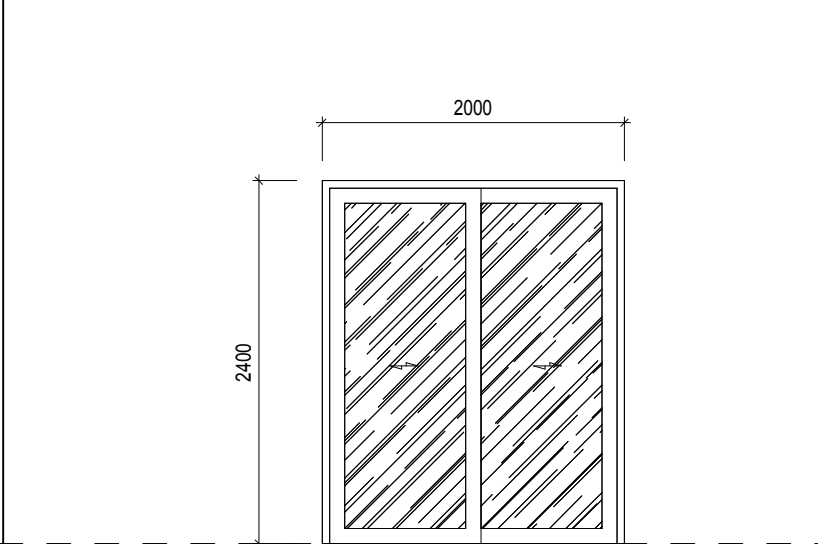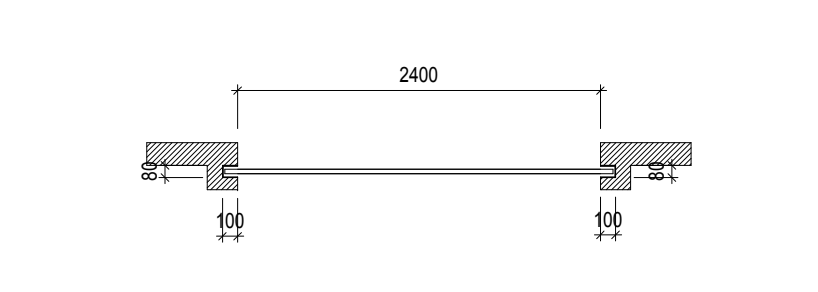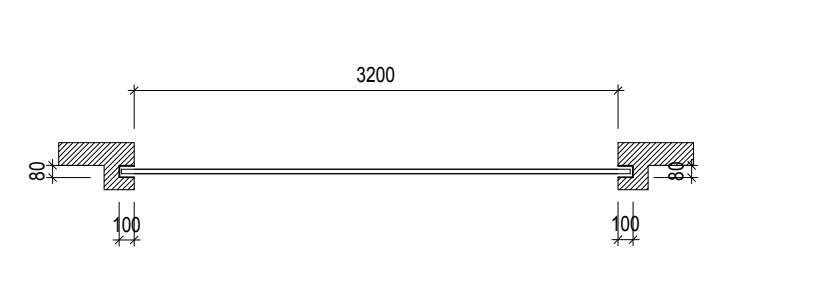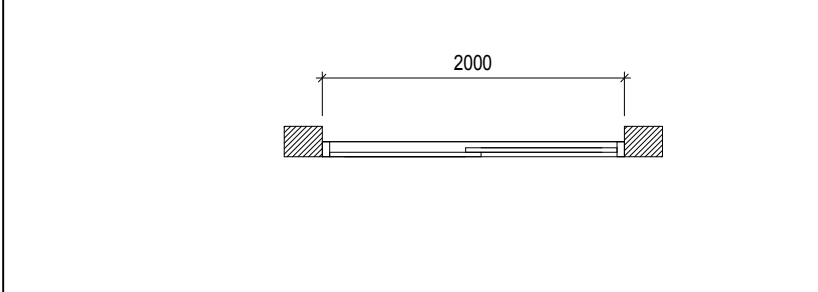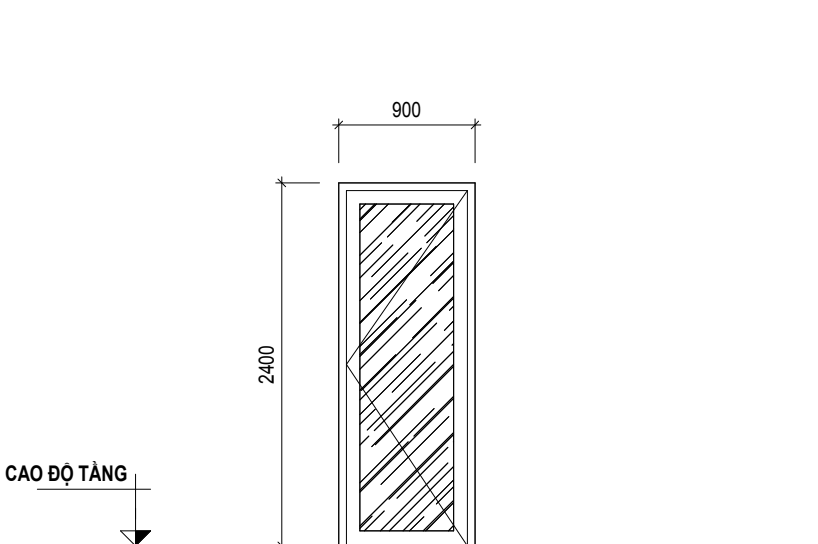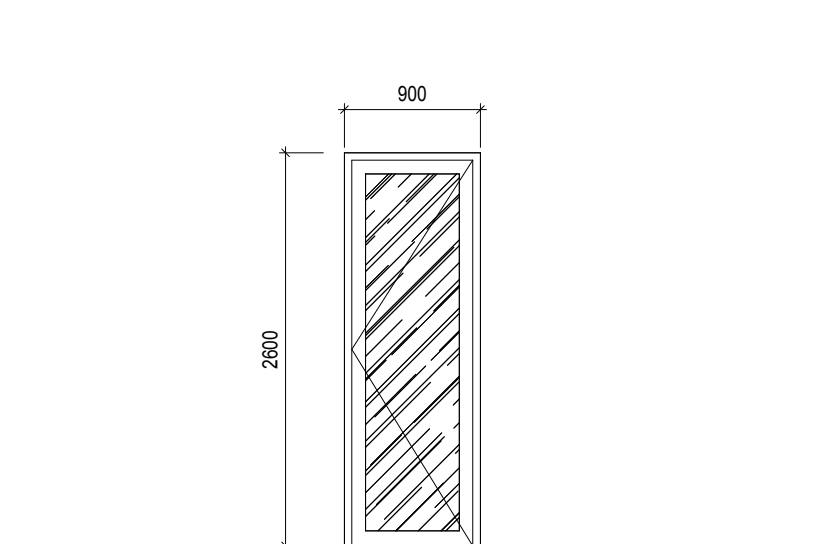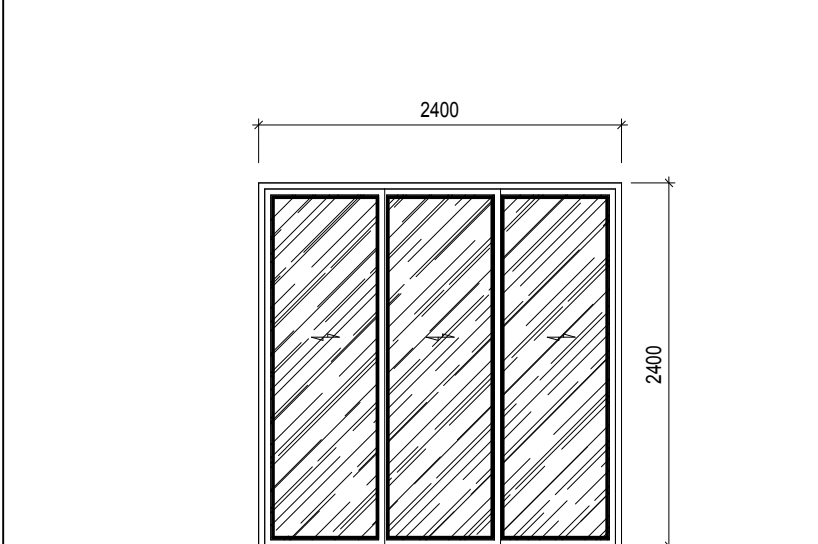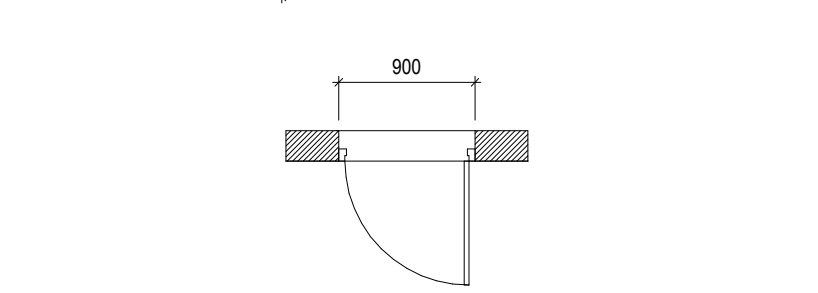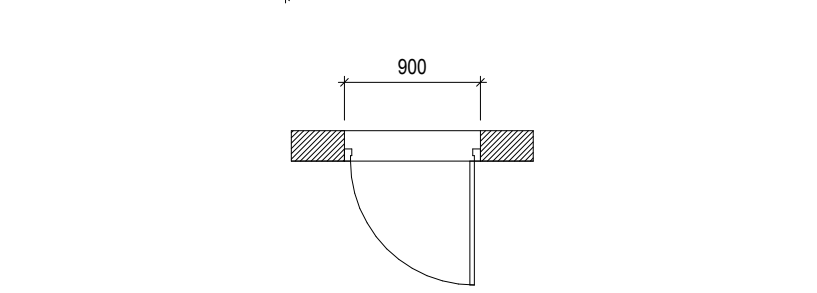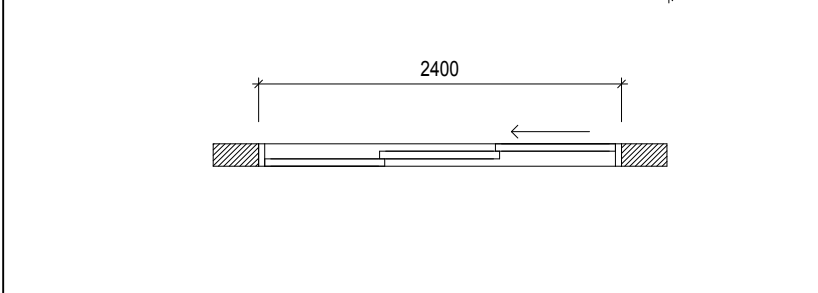
|                                                                                     |   |                                                                                      |   |                                                                                       |   |
|-------------------------------------------------------------------------------------|---|--------------------------------------------------------------------------------------|---|---------------------------------------------------------------------------------------|---|
|     |   |     |   |     |   |
|    |   |    |   |    |   |
| Đc1                                                                                 | -QUY CÁCH:CỬA CUỐN TỰ ĐỘNG KÈM PHỤ KIỆN<br>-VẬT LIỆU:LÁ NHÔM<br>-MÀU SẮC:CĐT LỰA CHỌN                                     | Đc2                                                                                  | -QUY CÁCH:CỬA CUỐN TỰ ĐỘNG KÈM PHỤ KIỆN<br>-VẬT LIỆU:LÁ NHÔM<br>-MÀU SẮC:CĐT LỰA CHỌN                                     | Đ5                                                                                    | -QUY CÁCH:CỬA ĐI TRƯỢT 2 CẢNH VÀ PHỤ KIỆN ĐI KÈM<br>-VẬT LIỆU:HỆ NHÔM DÂY 1.2mm, KÍNH CƯỜNG LỰC DÂY 8mm<br>-MÀU SẮC:MÀU XĂM. |
|                                                                                     | -VỊ TRÍ:TẦNG 1<br>-KÍCH THƯỚC:2400 x 2600<br>-SỐ LƯỢNG: 1 BỘ                                                              |                                                                                      | -VỊ TRÍ:TẦNG 1<br>-KÍCH THƯỚC:3200 x 2600<br>-SỐ LƯỢNG: 1 BỘ                                                              |                                                                                       | -VỊ TRÍ:BAN CÔNG VÀ SÂN THƯỢNG TẦNG 2 VÀ TẦNG 3<br>-KÍCH THƯỚC:2000 x 2400<br>-SỐ LƯỢNG: 5 BỘ                                |
|  |   |  |   |  |   |
|  |   |  |   |  |   |
| Đ6                                                                                  | -QUY CÁCH:CỬA ĐI MỞ 1 CẢNH VÀ PHỤ KIỆN ĐI KÈM<br>-VẬT LIỆU:HỆ NHÔM DÂY 1.2mm, KÍNH CƯỜNG LỰC DÂY 8mm<br>-MÀU SẮC:MÀU XĂM. | Đ7                                                                                   | -QUY CÁCH:CỬA ĐI MỞ 1 CẢNH VÀ PHỤ KIỆN ĐI KÈM<br>-VẬT LIỆU:HỆ NHÔM DÂY 1.2mm, KÍNH CƯỜNG LỰC DÂY 8mm<br>-MÀU SẮC:MÀU XĂM. | Đ8                                                                                    | -QUY CÁCH:CỬA TRƯỢT 3 CẢNH KÈM PHỤ KIỆN<br>-VẬT LIỆU:HỆ NHÔM DÂY 1.2mm, KÍNH CƯỜNG LỰC DÂY 8mm<br>-MÀU SẮC:CĐT LỰA CHỌN      |
|                                                                                     | -VỊ TRÍ:SÂN PHOI TẦNG 3<br>-KÍCH THƯỚC:900 x 2400<br>-SỐ LƯỢNG: 1 BỘ                                                      |                                                                                      | -VỊ TRÍ:SÂN SAU TẦNG 1<br>-KÍCH THƯỚC:900 x 2600<br>-SỐ LƯỢNG: 1 BỘ                                                       |                                                                                       | -VỊ TRÍ:BAN CÔNG TẦNG 2 VÀ SÂN THƯỢNG TẦNG 3<br>-KÍCH THƯỚC:2400 x 2400<br>-SỐ LƯỢNG: 2 BỘ                                   |

|   |          |
|---|----------|
| GHI CHÚ:<br>- CÁC ĐƠN VỊ THI CÔNG PHẢI PHỐI HỢP BẢN VẼ CỦA TẤT CẢ CÁC BỘ MÔN KHÁC NẾU THẤY SỰ KHÁC BIỆT PHẢI BẢO CHO ĐƠN VỊ THIẾT KẾ XỬ LÝ.<br>- KHI XỬ LÝ SỰ KHÁC BIỆT, PHẢI THỰC HIỆN ƯU TIÊN THEO THỨ TỰ GIỮA CÁC BỘ MÔN: KIẾN TRÚC → KẾT CẤU / BỘ MÔN KHÁC; HOẶC ƯU TIÊN TRONG CÙNG BỘ MÔN: CHI TIẾT → TỔNG THỂ<br>- CÁC SỐ LƯU KÍCH THƯỚC PHẢI ĐƯỢC KIỂM TRA THỰC TẾ TẠI CÔNG TRÌNH, NẾU THẤY SỰ KHÁC BIỆT SƠ VỚI BẢN VẼ THI PHẢI BẢO CHO ĐƠN VỊ THIẾT KẾ. |          |
| HIỆU CHỈNH:   |          |
| REV   | NỘI DUNG |
|   |          |
| CHỦ ĐẦU TƯ:<br>CÔNG TY TNHH ĐẦU TƯ<br><b>PHÚ VIỆT TÍN</b><br>ĐỊA CHỈ: LÔ 18-19 QUỐC LỘ 1A, XÃ DẦU GIẤY, TỈNH ĐỒNG NAI, VIỆT NAM   |          |
|   |          |
| CĐT/ĐTV: ĐẶNG PHƯỚC BÌNH   |          |
| ĐƠN VỊ THIẾT KẾ:<br>CÔNG TY CỔ PHẦN TƯ VẤN THIẾT KẾ<br><b>BASE ARC</b><br>ĐỊA CHỈ: 138 ĐIỆN BIÊN PHỦ, PHƯỜNG TÂN ĐỊNH, TP. HỒ CHÍ MINH, VIỆT NAM   |          |
|   |          |
| TỔNG GIÁM ĐỐC: TRẦN ĐỨC AN   |          |
| CHỦ NHIỆM DỰ ÁN:   |          |
| KTS. NGUYỄN THÀNH THÁI   |          |
| CHỦ TRÌ THIẾT KẾ:   |          |
| KTS. NGUYỄN THÀNH THÁI   |          |
| THIẾT KẾ:   |          |
| KTS. LÊ ĐÌNH TÂM   |          |
| KIỂM TRA:   |          |
| KTS. NGUYỄN ĐỨC THÁI   |          |
| DỰ ÁN:<br>KHU DÂN CƯ A1-C1 (ĐÔ THỊ DẦU GIẤY)<br>ĐỊA ĐIỂM: XÃ DẦU GIẤY, TỈNH ĐỒNG NAI   |          |
| CÔNG TRÌNH:<br><br>NHÀ Ở THƯƠNG MẠI LIÊN KẾ   |          |
| HẠNG MỤC:<br><br>MẪU NHÀ T3-2b   |          |
| TÊN BẢN VẼ:<br><br>CHI TIẾT CỬA ĐI   |          |
| MỤC ĐÍCH PHÁT HÀNH:   |          |
| BẢN VẼ MỜI THẦU   |          |
| THIẾT KẾ CƠ SỞ   |          |
| ✓ THIẾT KẾ BẢN VẼ THI CÔNG   |          |
| BẢN VẼ HOÀN CÔNG   |          |
| HOÀN THÀNH   | 07/2025  |
| TỶ LỆ   | NTS      |
| SỐ HIỆU BẢN VẼ   | A08-51   |



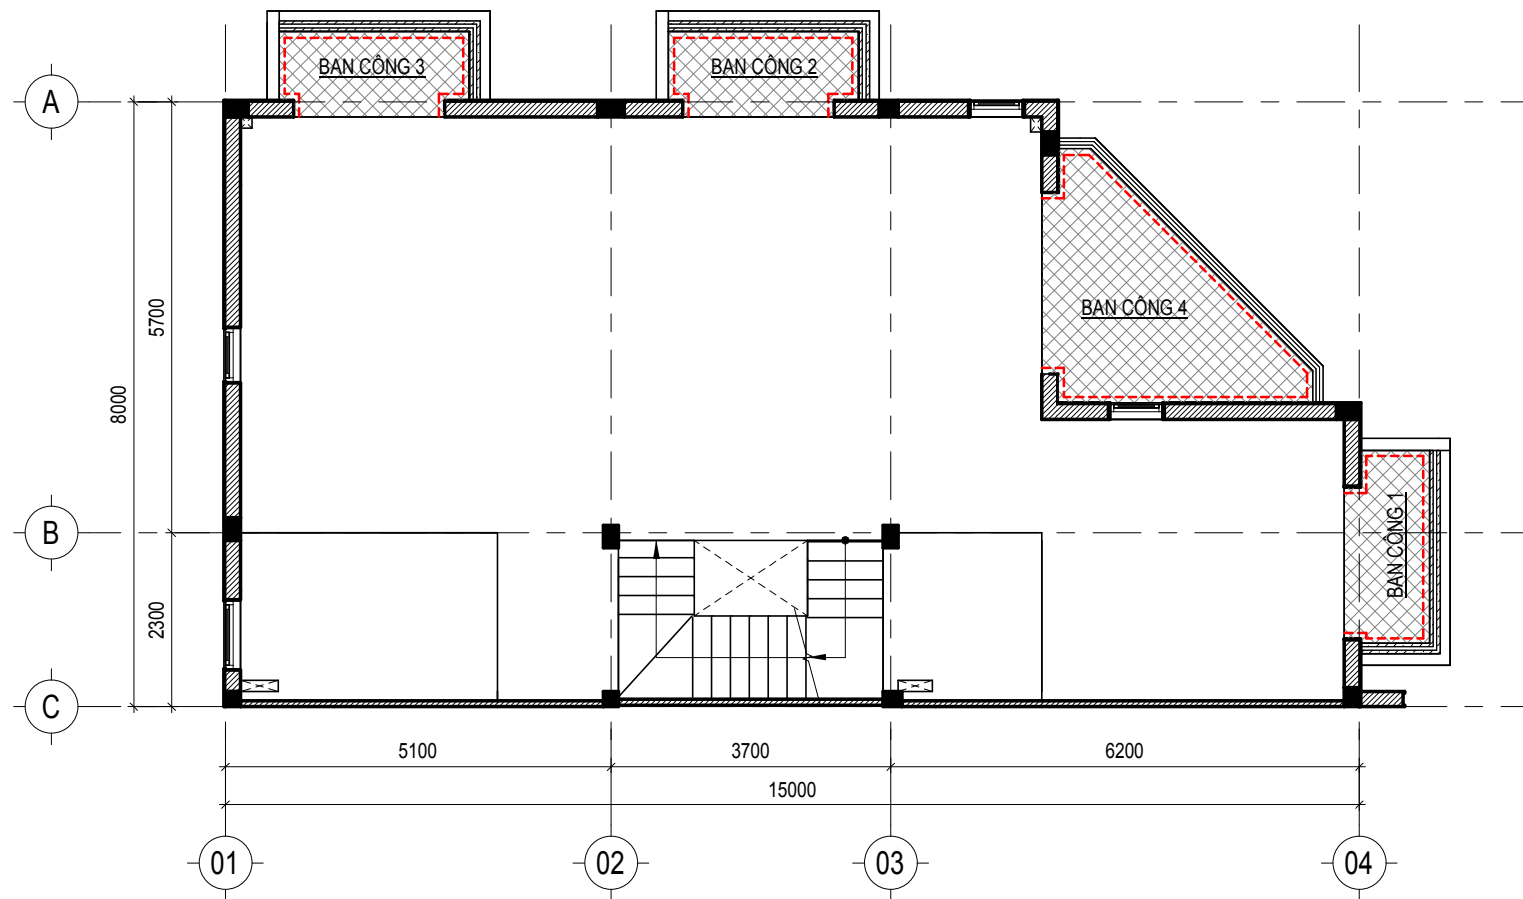

## MẶT BẰNG CHỐNG THẨM TẦNG 2

TỶ LỆ 1 : 100

|  |                                              |
|--|----------------------------------------------|
|  | KHU VỰC CHỐNG THẨM SÀN                       |
|  | KHU VỰC CHỐNG THẨM CUỘN CHÂN TƯỜNG LÊN 300mm |

GHI CHÚ:  
- CÁC ĐƠN VỊ THI CÔNG PHẢI PHỐI HỢP BẢN VẼ CỦA TẤT CẢ CÁC BỘ MÔN KHÁC NẾU THẤY SỰ KHÁC BIỆT PHẢI BÁO CHO ĐƠN VỊ THIẾT KẾ ĐỂ XỬ LÝ.  
- KHI XỬ LÝ SỰ KHÁC BIỆT, PHẢI THỰC HIỆN ƯU TIÊN THEO THỨ TỰ GIỮA CÁC BỘ MÔN: KIẾN TRÚC → KẾT CẤU / BỘ MÔN KHÁC; HOẶC ƯU TIÊN TRONG CÙNG BỘ MÔN: CHI TIẾT → TỔNG THỂ  
- CÁC SỐ LƯU KÍCH THƯỚC PHẢI ĐƯỢC KIỂM TRA THỰC TẾ TẠI CÔNG TRÌNH, NẾU THẤY SỰ KHÁC BIỆT SƠ VỚI BẢN VẼ THI PHẢI BÁO CHO ĐƠN VỊ THIẾT KẾ.

### HIỆU CHỈNH:

| REV | NGÀY | NỘI DUNG |
|-----|------|----------|
|-----|------|----------|

### CHỦ ĐẦU TƯ:

CÔNG TY TNHH ĐẦU TƯ

**PHÚ VIỆT TÍN**

ĐỊA CHỈ: LÔ 18-19 QUỐC LỘ 1A, XÃ DẦU GIẤY,  
TỈNH ĐỒNG NAI, VIỆT NAM

### CHỦ ĐẦU TƯ:

ĐẶNG PHƯỚC BÌNH

### ĐƠN VỊ THIẾT KẾ:

CÔNG TY CỔ PHẦN TƯ VẤN THIẾT KẾ

**BASE ARC**

ĐỊA CHỈ: 138 ĐIỆN BIÊN PHỦ, PHƯỜNG TÂN ĐỊNH,  
TP. HỒ CHÍ MINH, VIỆT NAM

### TỔNG GIÁM ĐỐC:

TRẦN ĐỨC AN

### CHỦ NHIỆM DỰ ÁN:

KTS. NGUYỄN THÀNH THÁI

### CHỦ TRÌ THIẾT KẾ:

KTS. NGUYỄN THÀNH THÁI

### THIẾT KẾ:

KTS. LÊ ĐÌNH TÂM

### KIỂM TRA:

KTS. NGUYỄN ĐỨC THÁI

### DỰ ÁN:

KHU DÂN CƯ A1-C1 (ĐÔ THỊ DẦU GIẤY)

ĐỊA ĐIỂM: XÃ DẦU GIẤY, TỈNH ĐỒNG NAI

### CÔNG TRÌNH:

NHÀ Ở THƯƠNG MẠI LIÊN KẾ

### HẠNG MỤC:

MẪU NHÀ T3-2b

### TÊN BẢN VẼ:

MẶT BẰNG CHỐNG THẨM TẦNG 2


### MỤC ĐÍCH PHÁT HÀNH:

|                                     |                          |
|-------------------------------------|--------------------------|
| <input type="checkbox"/>            | BẢN VẼ MỜI THẦU          |
| <input type="checkbox"/>            | THIẾT KẾ CƠ SỞ           |
| <input checked="" type="checkbox"/> | THIẾT KẾ BẢN VẼ THI CÔNG |
| <input type="checkbox"/>            | BẢN VẼ HOÀN CÔNG         |

HOÀN THÀNH 07/2025


TỶ LỆ NTS

SỐ HIỆU BẢN VẼ A10-01

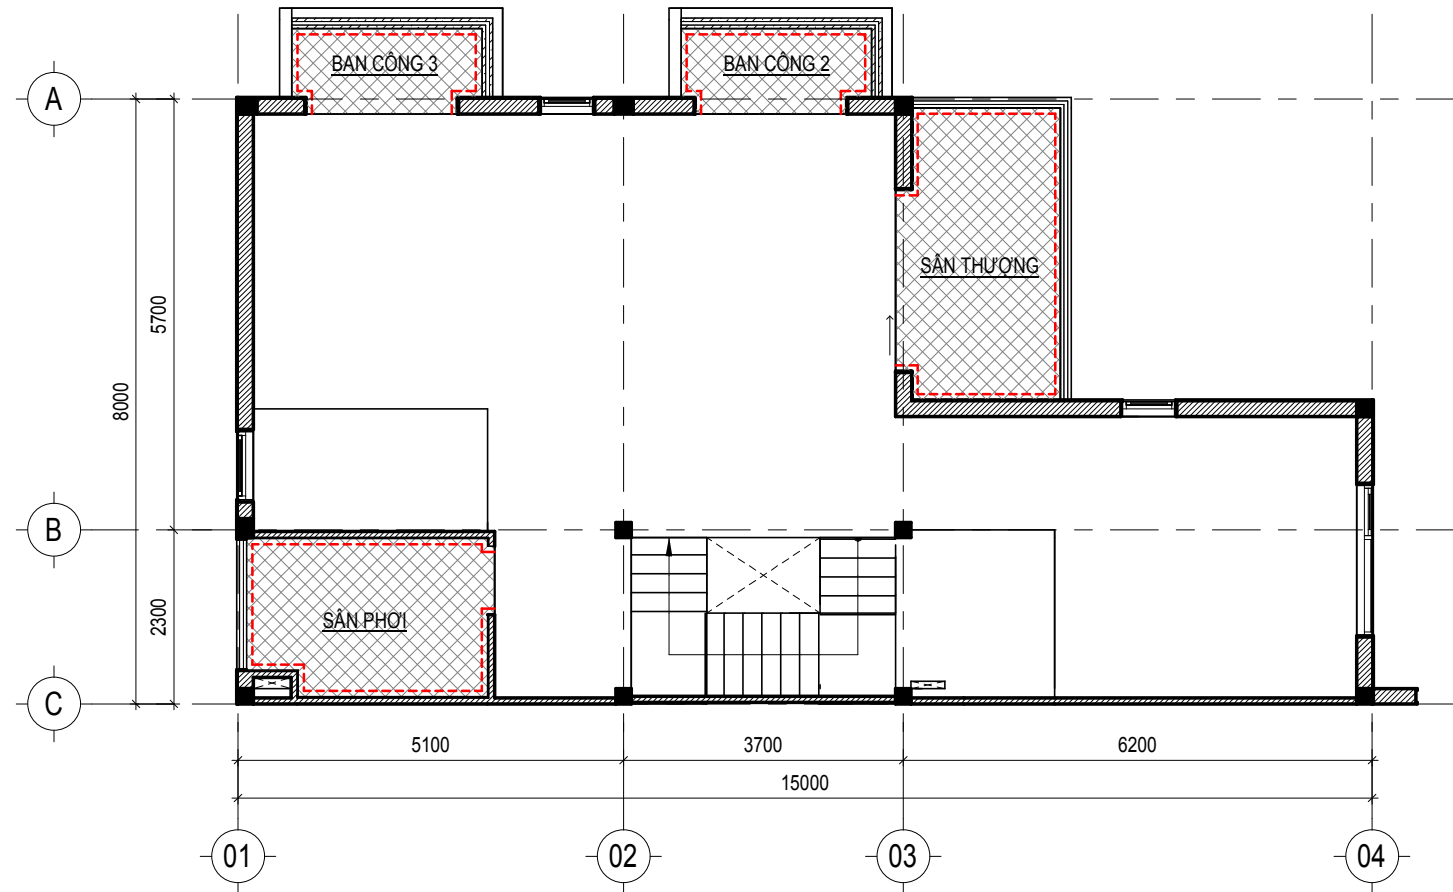

**MẶT BẰNG CHỐNG THẨM TẦNG 3**

TỶ LỆ 1 : 100

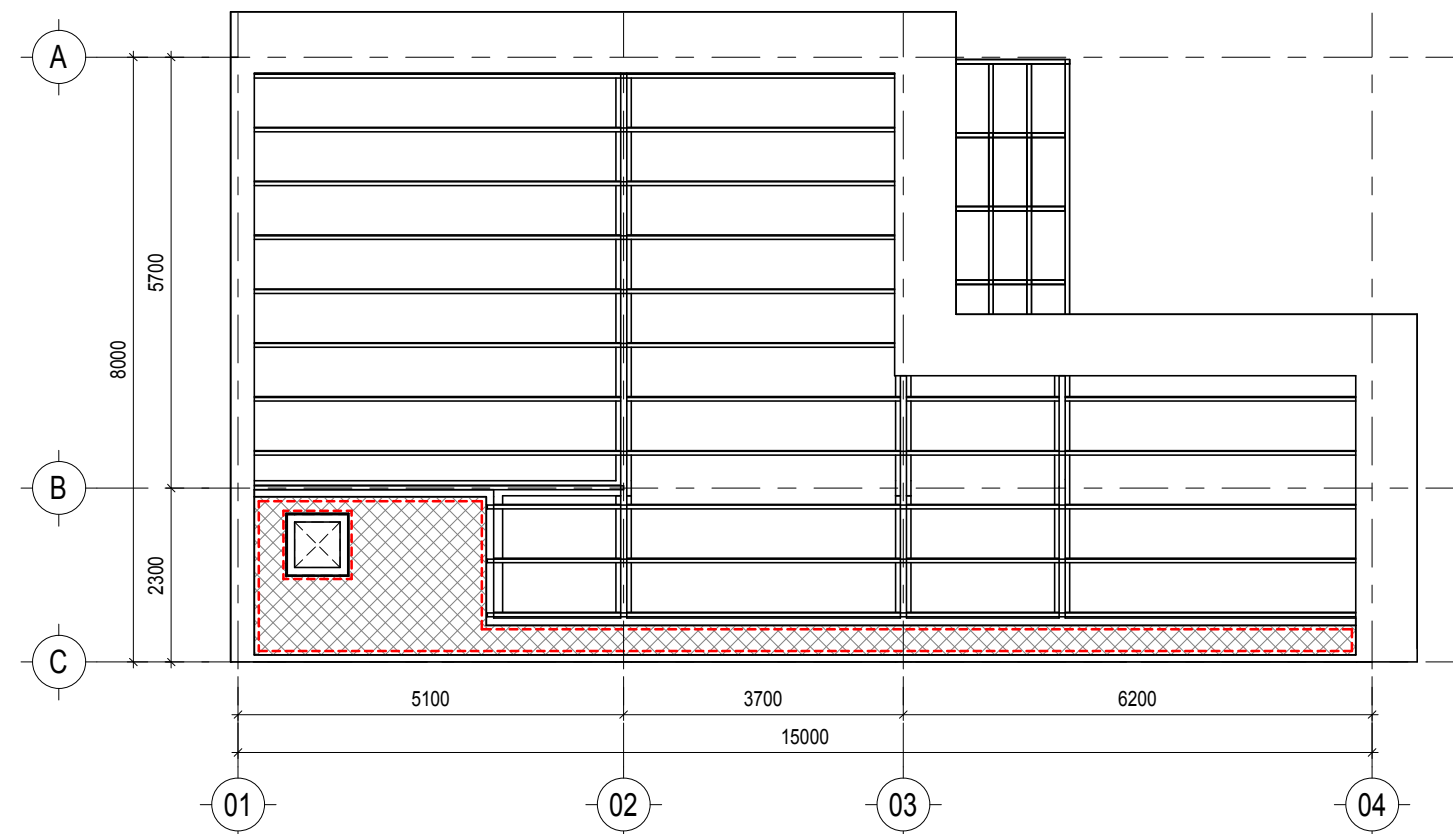

**MẶT BẰNG CHỐNG THẨM MÁI**

TỶ LỆ 1 : 100

|  |                                              |
|--|----------------------------------------------|
|  | KHU VỰC CHỐNG THẨM SÀN                       |
|  | KHU VỰC CHỐNG THẨM CUỘN CHÂN TƯỜNG LÊN 300mm |

GHI CHÚ:  
- CÁC ĐƠN VỊ THI CÔNG PHẢI PHỐI HỢP BẢN VẼ CỦA TẤT CẢ CÁC BỘ MÔN KHÁC NẾU THẤY SỰ KHÁC BIỆT PHẢI BẢO CHỒI ĐƠN VỊ THIẾT KẾ ĐỂ XỬ LÝ.  
- KHI XỬ LÝ SỰ KHÁC BIỆT, PHẢI THỰC HIỆN ƯU TIÊN THEO THỨ TỰ GIỮA CÁC BỘ MÔN: KIẾN TRÚC → KẾT CẤU / BỘ MÔN KHÁC; HOẶC ƯU TIÊN TRONG CÙNG BỘ MÔN: CHI TIẾT → TỔNG THỂ  
- CÁC SỐ LƯỢNG KÍCH THƯỚC PHẢI ĐƯỢC KIỂM TRA THỰC TẾ TẠI CÔNG TRÌNH, NẾU THẤY SỰ KHÁC BIỆT SƠ VỚI BẢN VẼ THI PHẢI BẢO CHỒI ĐƠN VỊ THIẾT KẾ.

HIỆU CHỈNH:

| REV | NGÀY | NỘI DUNG |
|-----|------|----------|
|-----|------|----------|

CHỦ ĐẦU TƯ:  
CÔNG TY TNHH ĐẦU TƯ  
**PHÚ VIỆT TÍN**  
ĐỊA CHỈ: LÔ 18-19 QUỐC LỘ 1A, XÃ DẦU GIẤY,  
TỈNH ĐỒNG NAI, VIỆT NAM

CTHĐT: ĐẶNG PHƯỚC BÌNH

ĐƠN VỊ THIẾT KẾ:  
CÔNG TY CỔ PHẦN TƯ VẤN THIẾT KẾ  
**BASE ARC**  
ĐỊA CHỈ: 138 ĐIỆN BIÊN PHỦ, PHƯỜNG TÂN ĐỊNH,  
TP. HỒ CHÍ MINH, VIỆT NAM

TỔNG GIÁM ĐỐC: TRẦN ĐỨC AN

CHỦ NHIỆM DỰ ÁN:

KTS. NGUYỄN THÀNH THÁI

CHỦ TRÌ THIẾT KẾ:

KTS. NGUYỄN THÀNH THÁI

THIẾT KẾ:

KTS. LÊ ĐÌNH TÂM

KIỂM TRA:

KTS. NGUYỄN ĐỨC THÁI

DỰ ÁN:

KHU DÂN CƯ A1-C1 (ĐÔ THỊ DẦU GIẤY)

ĐỊA ĐIỂM: XÃ DẦU GIẤY, TỈNH ĐỒNG NAI

CÔNG TRÌNH:

NHÀ Ở THƯƠNG MẠI LIÊN KẾ

HẠNG MỤC:

MẪU NHÀ T3-2b

TÊN BẢN VẼ:

MẶT BẰNG CHỐNG THẨM TẦNG 3, MÁI

MỤC ĐÍCH PHÁT HÀNH:

|                                     |                          |
|-------------------------------------|--------------------------|
| <input type="checkbox"/>            | BẢN VẼ MỜI THẦU          |
| <input type="checkbox"/>            | THIẾT KẾ CƠ SỞ           |
| <input checked="" type="checkbox"/> | THIẾT KẾ BẢN VẼ THI CÔNG |
| <input type="checkbox"/>            | BẢN VẼ HOÀN CÔNG         |

HOÀN THÀNH 07/2025

TỶ LỆ NTS

SỐ HIỆU BẢN VẼ A10-02

# PHẦN KẾT CẤU

## DANH MỤC BẢN VẼ

| <b><u>SỐ HIỆU BẢN VẼ</u></b> | <b><u>TÊN BẢN VẼ</u></b>            |
|------------------------------|-------------------------------------|
| KC-00                        | HỒ SƠ THIẾT KẾ THI CÔNG             |
| KC-01                        | DANH MỤC BẢN VẼ                     |
| KC-02                        | GHI CHÚ CHUNG-01                    |
| KC-03                        | GHI CHÚ CHUNG-02                    |
| KC-04                        | GHI CHÚ CHUNG-03                    |
| KC-05                        | GHI CHÚ CHUNG-04                    |
| KC-06                        | PHẦN MÓNG PHƯƠNG ÁN 1               |
| KC-07                        | MẶT BẰNG BỐ TRÍ MÓNG, THÉP ĐÁY MÓNG |
| KC-08                        | CHI TIẾT MÓNG-01                    |
| KC-09                        | CHI TIẾT MÓNG-02                    |
| KC-10                        | CHI TIẾT MÓNG-03                    |
| KC-11                        | CHI TIẾT MÓNG-04                    |
| KC-12                        | PHẦN MÓNG PHƯƠNG ÁN 2               |
| KC-13                        | MẶT BẰNG BỐ TRÍ MÓNG, THÉP ĐÁY MÓNG |
| KC-14                        | CHI TIẾT MÓNG-01                    |
| KC-15                        | CHI TIẾT MÓNG-02                    |
| KC-16                        | CHI TIẾT MÓNG-03                    |
| KC-17                        | CHI TIẾT MÓNG-04                    |
| KC-18                        | PHẦN KHUNG                          |
| KC-19                        | MẶT BẰNG CỘT CỘT                    |
| KC-20                        | MẶT BẰNG CỘT TẦNG 1, 2              |
| KC-21                        | MẶT BẰNG CỘT TẦNG 3, MÁI            |
| KC-22                        | CHI TIẾT CỘT-01                     |
| KC-23                        | CHI TIẾT CỘT-02                     |
| KC-24                        | CHI TIẾT CỘT-03                     |

## DANH MỤC BẢN VẼ

| <b>SỐ HIỆU BẢN VẼ</b> | <b>TÊN BẢN VẼ</b>                             |
|-----------------------|-----------------------------------------------|
| KC-25                 | MẶT BẰNG VÁCH CHẴN ĐẤT BTCT                   |
| KC-26                 | MẶT BẰNG DẦM SÀN TẦNG 1                       |
| KC-27                 | MẶT BẰNG DẦM SÀN TẦNG 2                       |
| KC-28                 | MẶT BẰNG DẦM SÀN TẦNG 3                       |
| KC-29                 | MẶT BẰNG DẦM SÀN MÁI                          |
| KC-30                 | MẶT BẰNG DẦM SÀN ĐÌNH MÁI, MẶT BẰNG XÀ GỖ MÁI |
| KC-31                 | CHI TIẾT DẦM TẦNG 1-01                        |
| KC-32                 | CHI TIẾT DẦM TẦNG 1-02                        |
| KC-33                 | CHI TIẾT DẦM TẦNG 2-01                        |
| KC-34                 | CHI TIẾT DẦM TẦNG 2-02                        |
| KC-35                 | CHI TIẾT DẦM TẦNG 2-03                        |
| KC-36                 | CHI TIẾT DẦM TẦNG 2-04                        |
| KC-37                 | CHI TIẾT DẦM TẦNG 3-01                        |
| KC-38                 | CHI TIẾT DẦM TẦNG 3-02                        |
| KC-39                 | CHI TIẾT DẦM TẦNG 3-03                        |
| KC-40                 | CHI TIẾT DẦM TẦNG 3-04                        |
| KC-41                 | CHI TIẾT DẦM TẦNG 3-05                        |
| KC-42                 | CHI TIẾT DẦM MÁI                              |
| KC-43                 | MẶT BẰNG THÉP SÀN TẦNG 2                      |
| KC-44                 | MẶT BẰNG THÉP SÀN TẦNG 3                      |
| KC-45                 | MẶT BẰNG THÉP SÀN MÁI, ĐÌNH MÁI               |
| KC-46                 | MẶT BẰNG CẦU THANG                            |
| KC-47                 | CHI TIẾT CẦU THANG-01                         |
| KC-48                 | CHI TIẾT CẦU THANG-02                         |
| KC-49                 | MẶT BẰNG LANH TỔ TẦNG 1                       |
| KC-50                 | MẶT BẰNG LANH TỔ TẦNG 2, TẦNG 3               |
| KC-51                 | MẶT BẰNG VÀ CHI TIẾT LAM MÁI                  |
| KC-52                 | TKT ĐÁY MỎNG                                  |

## DANH MỤC BẢN VẼ

| <b><u>SỐ HIỆU BẢN VẼ</u></b> | <b><u>TÊN BẢN VẼ</u></b> |
|------------------------------|--------------------------|
| <b>KC-53</b>                 | TKT DẦM MÓNG PA1         |
| <b>KC-54</b>                 | TKT CỘT-01               |
| <b>KC-55</b>                 | TKT CỘT-02               |
| <b>KC-56</b>                 | THÔNG KẾ THÉP DẦM-01     |
| <b>KC-57</b>                 | THÔNG KẾ THÉP DẦM-02     |
| <b>KC-58</b>                 | THÔNG KẾ THÉP DẦM-03     |
| <b>KC-59</b>                 | THÔNG KẾ THÉP DẦM-04     |
| <b>KC-60</b>                 | THÔNG KẾ THÉP DẦM-05     |
| <b>KC-61</b>                 | THÔNG KẾ THÉP SÀN        |
| <b>KC-62</b>                 | THÔNG KẾ THÉP CẦU THANG  |

**GHI CHÚ:**

- CÁC ĐƠN VỊ THI CÔNG PHẢI PHỐI HỢP BẢN VẼ CỦA TẤT CẢ CÁC BỘ MÔN KHÁC NHAU THẤY SỰ KHÁC BIỆT PHẢI BẢO CHỘ ĐƠN VỊ THIẾT KẾ BỮ XỬ LÝ.
- KHI XỬ LÝ SỰ KHÁC BIỆT, PHẢI THUẬN HIỆN ƯU TIÊN THEO THỨ TỰ ĐƯA CÁC BỘ MÔN: KIẾN TRÚC > KẾT CẤU / BỘ MÔN KHÁC; HOẶC ƯU TIÊN TRONG CÙNG BỘ MÔN: GIẾT TIẾP > TỒNG THỂ.
- CÁC SƠ LƯỢC THƯỚC PHẢI ĐƯỢC KIỂM TRA THỰC TẾ TẠI CÔNG TRƯỜNG, NẾU THẤY SỰ KHÁC BIỆT SƠ VẼ BÊN VẼ THIẾT KẾ PHẢI BẢO CHỘ ĐƠN VỊ THIẾT KẾ.

HIỆU CHỈNH:

| REV | NGÀY | NỘI DUNG |
|-----|------|----------|
|-----|------|----------|

CHỦ ĐẦU TƯ:

CÔNG TY TNHH ĐẦU TƯ

PHÚ VIỆT TÍN

ĐỊA CHỈ: LÔ 18-19 QUỐC LỘ 1A, XÃ DẦU GIẦY,  
TỈNH ĐỒNG NAI, VIỆT NAM

CTHDTV

ĐẶNG PHƯỚC BÌNH

ĐƠN VỊ THIẾT KẾ:

CÔNG TY CỔ PHẦN TƯ VẤN THIẾT KẾ

BASE ARC

ĐỊA CHỈ: 138 ĐIỆN BIÊN PHỦ, PHƯỜNG TÂN ĐỊNH,  
TP. HỒ CHÍ MINH, VIỆT NAM

TỔNG GIÁM ĐỐC

TRẦN ĐỨC AN

CHỦ NHIỆM DỰ ÁN:

KTS. NGUYỄN THÀNH THÁI

CHỦ TRÌ THIẾT KẾ:

KS. NGÔ TÙNG THÀNH

THIẾT KẾ:

KS. NGUYỄN MINH DUY BẰNG

KIỂM TRA:

KS. NGÔ TÙNG THÀNH

**DỰ ÁN:**

KHU DÂN CƯ A1-C1 (ĐÔ THỊ DẦU GIẦY)

ĐỊA ĐIỂM: XÃ DẦU GIẤY, TỈNH ĐỒNG NAI

CÔNG TRÌNH:

NHÀ Ở THƯỜNG MẠI LIỀN KÈ

HANG MUC:

MẪU NHÀ T3 2b

TÊN BẢN VẼ:

DANH MỤC BẢN VẼ

MỤC ĐÍCH PHÁT HÀNH:

|   |                          |
|---|--------------------------|
|   | BẢN VẼ MỜI THẦU          |
|   | THIẾT KẾ CƠ SỞ           |
| ✓ | THIẾT KẾ BẢN VẼ THI CÔNG |
|   | BẢN VẼ HOÀN CÔNG         |

|                |         |
|----------------|---------|
| HOÀN THÀNH     | 07/2025 |
| TỶ LỆ          | NTS     |
| SỐ HIỆU BẢN VẼ | KC-01   |

1. CHÚ THÍCH CHUNG

- CÁC CHÚ THÍCH SAU ĐÂY ĐƯỢC ÁP DỤNG CHO TẤT CẢ CÁC BẢN VẼ KẾT CẤU CỦA HỢP ĐỒNG NÀY, TRỪ KHI CÓ CHÚ THÍCH KHÁC ĐƯỢC GHI THÊM TRONG BẢN VẼ.
- TOÀN BỘ CÁC KÍCH THƯỚC CÓ ĐƠN VỊ LÀ MILIMET, CÁC CAO ĐỘ TÍNH BẢNG MÉT SO VỚI MỐC CHUẨN CỦA KHU ĐẤT XÂY DỰNG TRỪ KHI CÓ QUY ĐỊNH KHÁC.
- TOÀN BỘ CÁC BẢN VẼ KẾT CẤU PHẢI ĐƯỢC XEM CÙNG VỚI CÁC BẢN VẼ KIẾN TRÚC VÀ CÁC BỘ MÔN KHÁC CÓ LIÊN QUAN.
- TOÀN BỘ CÁC KÍCH THƯỚC TIM, TRỤC VÀ CAO ĐỘ CÁC TẦNG PHẢI ĐƯỢC KIỂM TRA THEO BẢN VẼ KIẾN TRÚC MỚI NHẤT CÓ LIÊN QUAN TRƯỚC KHI TIẾN HÀNH THI CÔNG. NẾU PHÁT HIỆN THẤY BẤT KỲ SỰ SAI KHÁC NÀO PHẢI LẬP TỨC THÔNG BÁO CHO KIẾN TRÚC SƯ VÀ CÁC KỸ SƯ BỘ MÔN.
- TOÀN BỘ CÁC TƯỜNG KHÔNG CHỊU LỰC VÀ CÁC CHI TIẾT KIẾN TRÚC KHÔNG ĐƯỢC THỂ HIỆN Ở CÁC BẢN VẼ KẾT CẤU. ĐỂ XÁC ĐỊNH VỊ TRÍ VÀ CÁC CHI TIẾT ĐÓ CẦN XEM BẢN VẼ KIẾN TRÚC.
- ĐẤT NỀN TẦNG TRỆT, ĐÁY MÓNG PHẢI ĐƯỢC ĐÁM CHẶT BẰNG MÁY ĐÁM CÓ ĐỘ CƠ (HỆ SỐ ĐÁM K = 0.90)
- ĐỘ BÊ TÔNG NỀN TẦNG 1 DÂY 70mm BÊ TÔNG B15 (M200) (SAU KHI THI CÔNG XONG HỆ THỐNG ỒNG KỸ THUẬT)
- TẤT CẢ CÁC BÊ MẶT BÊ TÔNG LIÊN KẾT GIỮA HAI LẦN ĐỒ KHÁC NHAU ĐỀU PHẢI SỬ DỤNG CHẤT PHỤ GIA LIÊN KẾT

2. TIÊU CHUẨN SỬ DỤNG

- TUYÊN TẬP TIÊU CHUẨN VIỆT NAM.
- TCVN 2737-2023. TẢI TRỌNG VÀ TÁC ĐỘNG. TIÊU CHUẨN THIẾT KẾ.
- TCVN 5574-2018. KẾT CẤU BÊ TÔNG VÀ BÊ TÔNG CỐT THÉP. TIÊU CHUẨN THIẾT KẾ.
- TCVN 5575-2024. KẾT CẤU THÉP. TIÊU CHUẨN THIẾT KẾ.
- TCVN 9379-2012: KẾT CẤU XÂY DỰNG VÀ NỀN - NGUYÊN TẮC CƠ BẢN VỀ TÍNH TOÁN.
- TCVN 9362:2012.TIÊU CHUẨN THIẾT KẾ NỀN NHÀ VÀ CÔNG TRÌNH.
- TCVN 1651-1:2018. THÉP CỐT BÊ TÔNG - THÉP THANH TRÒN TRON .
- TCVN 1651-2:2018. THÉP CỐT BÊ TÔNG - THÉP THANH VẠN .
- TCVN 1450-2009. GẠCH RỒNG ĐẤT SÉT NUNG.
- TCVN 1451-1998. GẠCH ĐẤT ĐẤT SÉT NUNG.
- TCVN 4314-2003. VỮA XÂY DỰNG - YẾU CẦU KỸ THUẬT.

3. VẬT LIỆU SỬ DỤNG

3.1 BÊ TÔNG

- CẤU KIỆN CHỊU LỰC MÓNG, CỘT, DẪM, SÀN, CẦU THANG: B20 ;ĐỘ SỤT 14±2cm
- BÊ NƯỚC NGÂM, BÊ TỰ HOẠI, LANH TỎ, Ô VĂNG: B15; ĐỘ SỤT 10±2cm
- BÊ TÔNG LÓT ĐÁ 10x20: B7.5
- GHI CHÚ: ĐỘ SỤT QUI ĐỊNH LÀ ĐỘ SỤT THAM KHẢO CỦA HỖN HỢP BÊ TÔNG TẠI VỊ TRÍ ĐÓ.

3.2 CỐT THÉP:

- THÉP CB400-V (Ø ≥ 10): Rs = 350 MPa
- THÉP CB240-T (Ø < 10): Rs = 210 MPa
- THÉP HỢP MẠ KÉM MẮC THÉP SS400: Rs = 245 MPa

3.3 GẠCH XÂY:

- TRỪ KHI ĐƯỢC QUY ĐỊNH TRONG THIẾT KẾ, TẤT CẢ CÁC LOẠI GẠCH SỬ DỤNG CHO XÂY DỰNG PHẢI ĐẠT CƯỜNG ĐỘ QUY ĐỊNH NHƯ SAU:

- + GẠCH RỒNG >= M50.
- + GẠCH ĐẶC >= M75.
- + GẠCH KHÔNG NUNG XI MĂNG CỐT LIỆU, CƯỜNG ĐỘ CHỊU NÉN M5.0MPa

3.4 VỮA :

- TRỪ KHI ĐƯỢC QUY ĐỊNH TRONG THIẾT KẾ, TẤT CẢ CÁC LOẠI VỮA SỬ DỤNG CHO XÂY DỰNG PHẢI ĐẠT CƯỜNG ĐỘ TỐI THIỂU LÀ M7.5 ( MẮC 75).

4. LỚP BÊ TÔNG BẢO VỆ

- 70mm : CẤU KIỆN MÓNG ĐÚC TRỰC TIẾP TRÊN ĐẤT
- 50mm : CẤU KIỆN MÓNG ĐÚC TRÊN BÊ TÔNG LÓT, COFFA
- HOẶC CẤU KIỆN CÓ PHẦN TIẾP XÚC VỚI ĐẤT
- 30mm : DẪM, ĐÀ, CỘT
- 20mm : SÀN

5. ĐOẠN NỐI CHỒNG VÀ NEO CỐT THÉP


- ĐOẠN NEO 40d: NEO TRONG VÙNG KÉO
- ĐOẠN NEO 30d: NEO TRONG VÙNG NÉN
- CHIỀU DÀI ĐOẠN NỐI CỐT THÉP: 40d
- VỊ TRÍ MÔI NỐI THÉP CHỊU LỰC PHẢI XEN KẾ NHAU, TỶ LỆ THÉP ĐƯỢC NỐI NHƯ SAU:
  - + TẠI VÙNG CHỊU KÉO < 25%
  - + TẠI VÙNG CHỊU NÉN < 50 %
- KHI NỐI CÁC THANH KHÔNG CÙNG ĐƯỜNG KÍNH, CHIỀU DÀI ĐOẠN NỐI CHỒNG LẤY THEO THANH CÓ ĐƯỜNG KÍNH NHỎ NHƯNG KHÔNG ÍT HƠN CHIỀU DÀI NEO CHO THANH ĐƯỜNG KÍNH LỚN
- CÁC QUY ĐỊNH KHÁC TUÂN THEO TIÊU CHUẨN HIỆN HÀNH

6. KÝ HIỆU CHUẨN


|              |                                          |                                       |
|--------------|------------------------------------------|---------------------------------------|
| KÝ HIỆU SÀN  | S 100<br>+3.550                          | CHIỀU DÀY SÀN<br>CAO ĐỘ SÀN           |
|              | LỖ MỞ TẠM THỜI<br>TRÊN TƯỜNG, SÀN & VÁCH |                                       |
| KÝ HIỆU TẦNG | X1-1                                     | KÍCH THƯỚC DẪM<br>ĐOẠN DẪM<br>TÊN DẪM |
|              | CỘT BTCT PHÍA TRÊN SÀN                   |                                       |
|              | CỘT BTCT PHÍA DƯỚI SÀN                   |                                       |

7. CHI TIẾT CẤU TẠO ĐIỂN HÌNH


7.1 CHI TIẾT UỐN THÉP

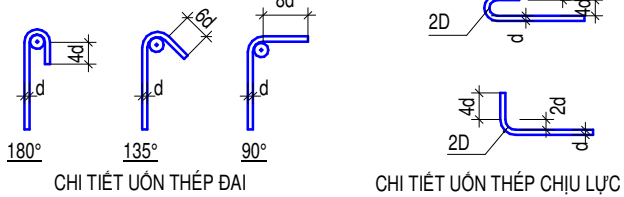

7.2 CHI TIẾT CẤU TẠO ĐAI DẪM, CỘT

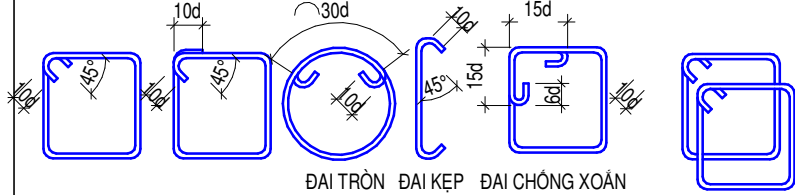

7.3 CHI TIẾT CẤU TẠO TẠI NÚT KHUNG

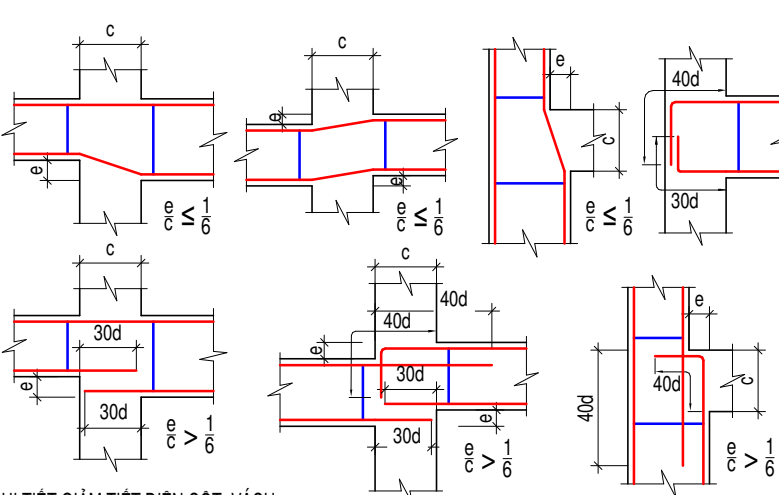


CHI TIẾT GIẢM TIẾT DIỆN CỘT, VÁCH  
- TUÂN THỦ BẢN VẼ CHI TIẾT CỘT VÁCH.  
- TRƯỜNG HỢP BẢN VẼ CHI TIẾT KHÔNG THỂ HIỆN, YẾU CẦU TUÂN THỦ THEO CHỈ DẪN Ở MỤC 5 PHÂN GHI CHÚ CHUNG


7.4 NỐI CỐT THÉP CHO DẪM, CỘT, VÁCH, SÀN

- VỊ TRÍ VÀ CHIỀU DÀI ĐOẠN NỐI CHI TIẾT TRÊN BẢN VẼ. NẾU KHÔNG CÓ CHỈ DẪN NÀO KHÁC CHIỀU DÀI ĐOẠN NỐI ĐƯỢC LẤY THEO MỤC 5 PHÂN GHI CHÚ CHUNG, VỊ TRÍ NỐI THEO HÌNH VẼ SAU:


7.4.1 NỐI CỐT THÉP DẪM

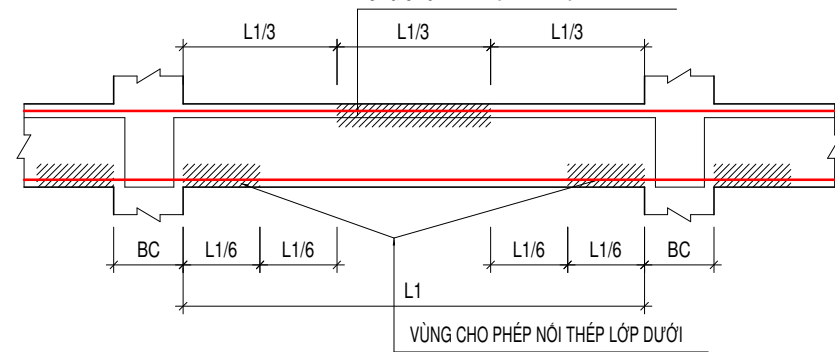


7.4.2 NỐI THÉP SÀN

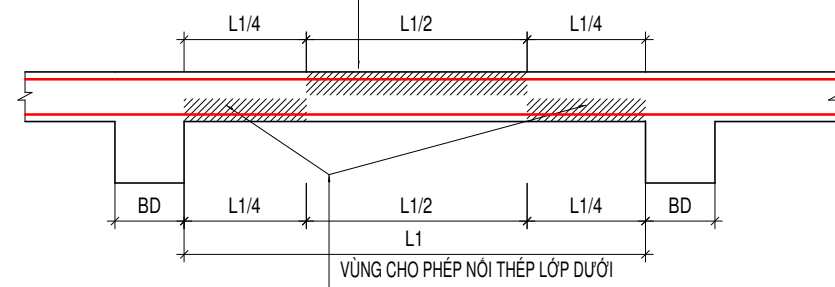


7.5 CHI TIẾT GÓI ĐỖ THÉP MŨ SÀN

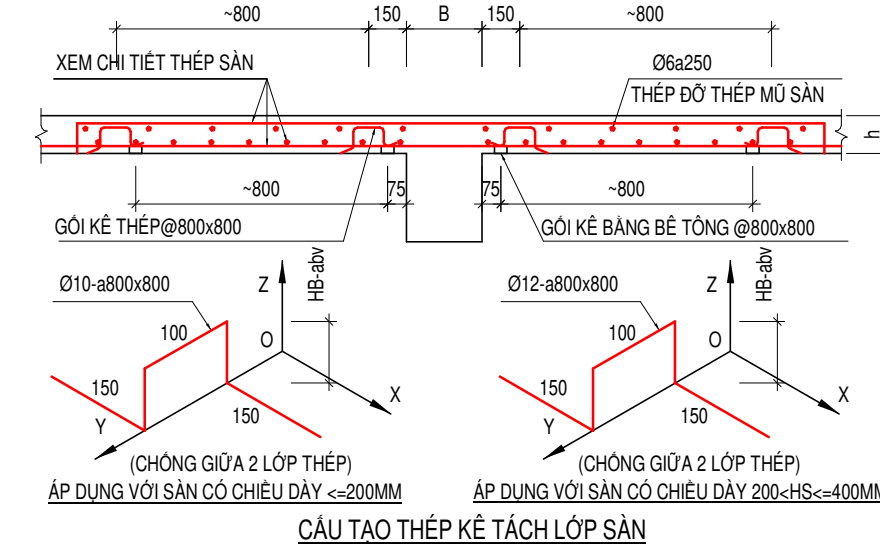

7.6. CẤU TẠO KHU VỰC SÀN HẠ CỘT 30-50MM

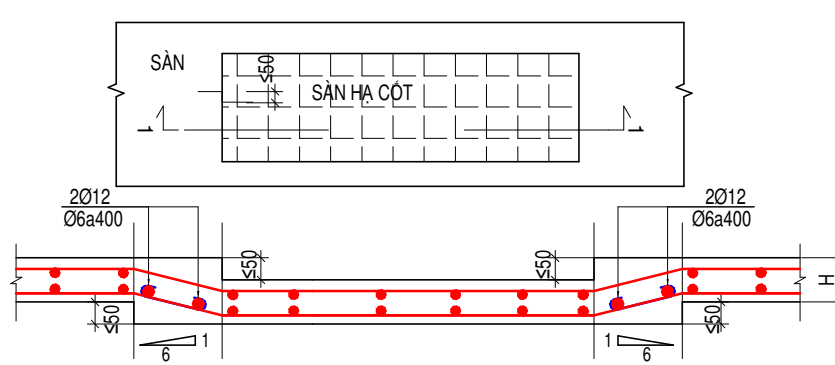

7.7. KÝ HIỆU THÉP SÀN

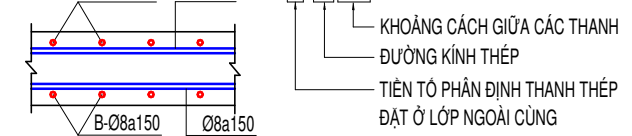

GHI CHÚ:

- CÁC ĐƠN VỊ THI CÔNG PHẢI PHỐI HỢP BẢN VẼ CỦA TẤT CẢ CÁC BỘ MÔN KHÁC NẾU THẤY SỰ KHÁC BIỆT PHẢI BẢO CHO ĐƠN VỊ THIẾT KẾ ĐỂ XỬ LÝ.
- KHI XỬ LÝ SỰ KHÁC BIỆT, PHẢI THỰC HIỆN ƯU TIÊN THEO THỨ TỰ GIỮA CÁC BỘ MÔN: KIẾN TRÚC → KẾT CẤU / BỘ MÔN KHÁC; HOẶC ƯU TIÊN TRONG CÙNG BỘ MÔN: CHI TIẾT → TỔNG THỂ
- CÁC SỐ LIỆU KÍCH THƯỚC PHẢI ĐƯỢC KIỂM TRA THỰC TẾ TẠI CÔNG TRÌNH, NẾU THẤY SỰ KHÁC BIỆT SƠ VỚI BẢN VẼ THÌ PHẢI BẢO CHO ĐƠN VỊ THIẾT KẾ.

HIỆU CHỈNH:

| REV | NGÀY | NỘI DUNG |
|-----|------|----------|
|     |      |          |

CHỦ ĐẦU TƯ:

CÔNG TY TNHH ĐẦU TƯ  
**PHÚ VIỆT TÍN**  
ĐỊA CHỈ: LÔ 18-19 QUỐC LỘ 1A, XÃ DẦU GIẤY,  
TỈNH ĐỒNG NAI, VIỆT NAM

CTHĐTV

ĐẠNG PHƯỚC BÌNH

ĐƠN VỊ THIẾT KẾ:

CÔNG TY CỔ PHẦN TƯ VẤN THIẾT KẾ  
**BASE ARC**  
ĐỊA CHỈ: 138 ĐIỆN BIÊN PHỦ, PHƯỜNG TÂN ĐỊNH,  
TP. HỒ CHÍ MINH, VIỆT NAM

TỔNG GIÁM ĐỐC

TRẦN ĐỨC AN

CHỦ NHIỆM DỰ ÁN:

KTS. NGUYỄN THÀNH THÁI

CHỦ TRÌ THIẾT KẾ:

KS. NGÔ TÙNG THÀNH

THIẾT KẾ:

KS. NGUYỄN MINH DUY BẰNG

KIỂM TRA:

KS. NGÔ TÙNG THÀNH

DỰ ÁN:

KHU DÂN CƯ A1-C1 (ĐÔ THỊ DẦU GIẤY)  
ĐỊA ĐIỂM: XÃ DẦU GIẤY, TỈNH ĐỒNG NAI

CÔNG TRÌNH:

NHÀ Ở THƯƠNG MẠI LIÊN KẾ

HẠNG MỤC:

MẪU NHÀ T3\_2b

TÊN BẢN VẼ:

GHI CHÚ CHUNG-01

MỤC ĐÍCH PHÁT HÀNH:

|                            |         |
|----------------------------|---------|
| BẢN VẼ MỜI THẦU            |         |
| THIẾT KẾ CƠ SỞ             |         |
| ✓ THIẾT KẾ BẢN VẼ THI CÔNG |         |
| BẢN VẼ HOÀN CÔNG           |         |
| HOÀN THÀNH                 | 07/2025 |
| TỶ LỆ                      | NTS     |
| SỐ HIỆU BẢN VẼ             | KC-02   |

ĐAI DẪM CỘT ĐAI DẪM

200


200

Lst

Lst : Khoảng cách từ lớp thép chủ phía đối diện


BỘ SƯNG 2 ĐAI CÁCH KHOẢNG 100mm BÊN TRÊN TIẾT DIỆN CỘT, VỚI  $\varnothing = \varnothing_{\max}$  CỦA THÉP DỌC DẪM

## TRƯỜNG HỢP 1

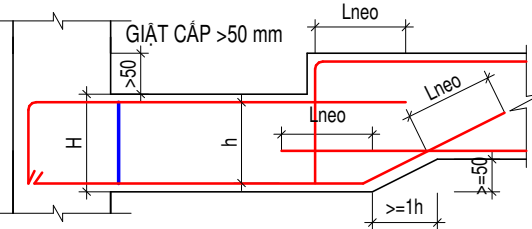


## TRƯỜNG HỢP 2


-KHÍ KHÔNG CÓ BẢN VẼ CHI TIẾT VIỆC HẠ CỘT DẦM KHU VỰC VẾ SINH, BAN CÔNG, LỖ GIA TỬ 30-50MM, VIỆC HẠ CỘT TUẦN THỦ QUY ĐỊNH SAU:  
KHÍ CÁC CẦU KIỂM DẠM CỐ YẾU CẦU HẠ CỘT MẶT TỬ 30-50MM,  
CHO PHÉP THIẾT CHỮ DẦM UỐN CẦU VÙNG HẠ CỘT (TỶ LỆ UỐN 1:6).  
CHÚ Ý XEM KẾT HỢP CÁC BẢN VẼ LIÊN QUAN ĐỂ XÁC ĐỊNH PHẠM VI DẦM HẠ CỘT.

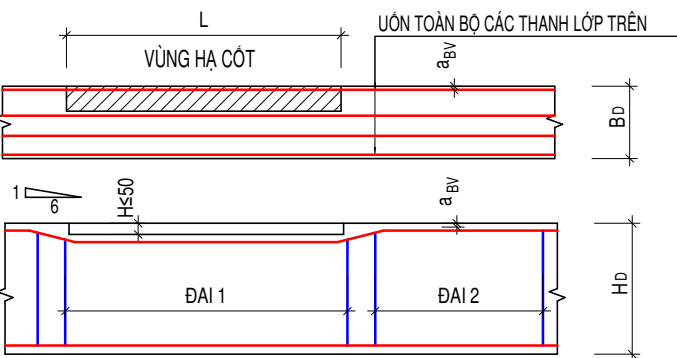


- KHI KHÔNG CÓ BẢN VẼ CHI TIẾT, VIỆC ĐẶT THÉP CÁC DẦM GỖ KHÚC, BẢN SÀN GỖ KHÚC, SÀN CHÉNH CỘT TUẦN THỦ CHỈ DẪN DƯỚI ĐÂY

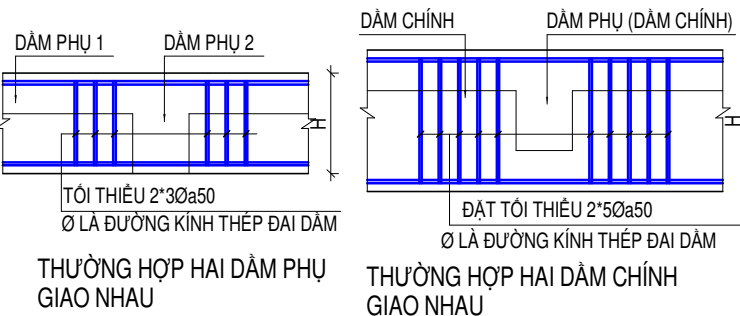

- KHOẢNG CÁCH TỪ MÉP DẦM ĐẾN THANH THÉP SÀN CÙNG PHƯƠNG KHÔNG LỚN HƠN  $A/2$  VÀ 50MM; VỚI A LÀ BƯỚC THÉP SÀN
- CẤU TẠO ĐẶT THÉP MỘT SỐ NÚT GIAO ĐIỂM HÌNH CỦA DẦM NHƯ SAU:

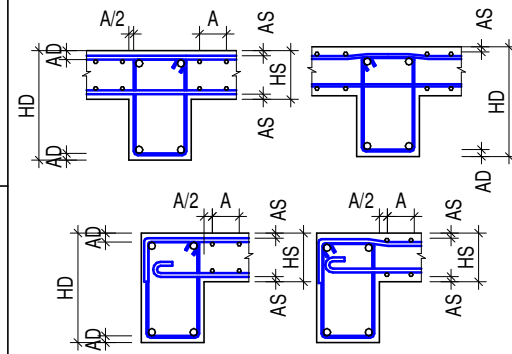


- KHI KHÔNG CÓ BẢN CHI TIẾT, VIỆC ĐẶT THÉP CÁC DÀM GỖ KHÚC, BÀN SÀN GỖ KHÚC, SÀN CHÉNH CỐT TUẦN THỦ CHỈ DẪN DƯỚI ĐÂY

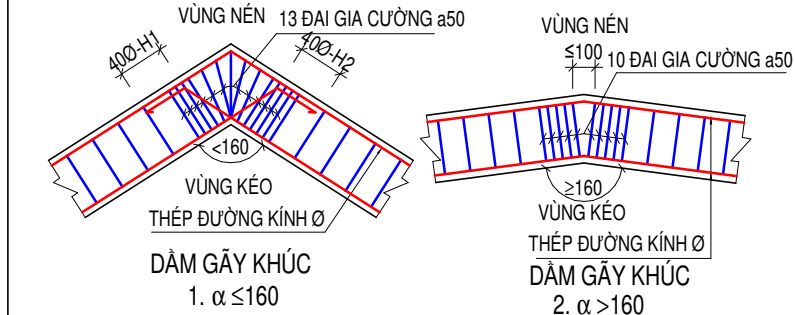

**SÀN GỖ KHÚC**  
1.  $\alpha \leq 160$

**SÀN GỖ KHÚC**  
2.  $\alpha > 160$

## CHI TIẾT HẠ COTE SÀN

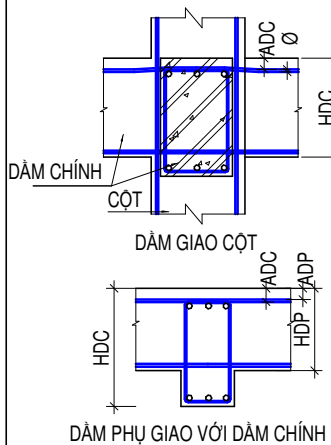

NHÀ THẦU CÓ THỂ LỰA CHỌN 1 TRONG 2 PHƯƠNG ÁN ĐỂ THI CÔNG

\_\_\_\_\_

The diagram shows two cross-sectional views of a slab reinforcement detail. The left view, labeled 'TẠI GÓC' (at the corner), shows a slab with a central rectangular area containing a diagonal cross. The reinforcement consists of two layers of 14mm diameter bars (2 LỚP 2 Ø 14). The top layer is bent up at a 45-degree angle. The bottom layer is bent down at a 45-degree angle. The dimensions are 30D (30 times the bar diameter) for the top and bottom layers, and L < 1000 for the central length. The right view, labeled 'TẠI GIỮA' (at the intermediate support), shows a similar slab with a central rectangular area containing a diagonal cross. The reinforcement consists of two layers of 14mm diameter bars (2 LỚP 2 Ø 14). The top layer is bent up at a 45-degree angle. The bottom layer is bent down at a 45-degree angle. The dimensions are 30D (30 times the bar diameter) for the top and bottom layers, and L < 500 for the central length.

- CÁC ĐƠN VỊ THI CUNG PHẢI PHỐI HỢP BẢN VẼ CỦA TẤT CẢ CÁC BỘ MÔN KHÁC NHU THẤY SỰ KHÁC BIỆT PHẢI BẢO CHỘN ĐƠN VỊ THIẾT KẾ ĐỂ XỬ LÝ.  
- KHI XỬ LÝ SỰ KHÁC BIỆT, PHẢI THU HIỆN VU TIỀN THƯỚC THỨ TƯ GIỮA CÁC BỘ MÔN: KIẾN TRÚC → KẾT CẤU / BỘ MÔN KHÁC; HOẶC VU TIỀN TRONG CÙNG BỘ MÔN: CHI TIẾT → TỔNG THỂ.  
- CÁC SƠ LIỆU KHI THUỐC PHẢI ĐƯỢC KIỂM TRA THUỐC TẾ TÀI CỘNG KINH, NHƯ THẤY SỰ KHÁC BIỆT SƠ VỚI BẢN VẼ PHẢI BẢO CHỘN ĐƠN VỊ THIẾT KẾ.

| REV | NGÀY | NỘI DUNG |
|-----|------|----------|
|-----|------|----------|

PHÚ VIỆT TÍN

ĐỊA CHỈ: LÔ 18-19 QUỐC LỘ 1A, XÃ DẦU GIẦY,  
TỈNH ĐỒNG NAI, VIỆT NAM

ĐẶNG PHƯỚC BÌNH

BASE ARC

ĐỊA CHỈ: 138 ĐIỆN BIÊN PHỦ, PHƯỜNG TÂN ĐỊNH,  
TP. HỒ CHÍ MINH, VIỆT NAM

TRẦN ĐỨC AN

ĐỊA ĐIỂM: XÃ DẦU GIẤY, TỈNH ĐỒNG NAI

NHÀ Ở THƯƠNG MẠI LIỀN KÈ

MẪU NHÀ T3 2b


GHI CHÚ CHUNG-02

|       |     |
|-------|-----|
| TỶ LỆ | NTS |
|-------|-----|

|                |       |
|----------------|-------|
| SỐ HIỆU BẢN VẼ | KC-03 |
|----------------|-------|


## 7.20. CẤU TẠO LỖ XUYÊN DÀM

- KHI KHÔNG CÓ BẢN VẼ CHI TIẾT VIỆC MỜ LỖ TRÊN DÀM TUÂN THỦ THEO CÁC QUY ĐỊNH DƯỚI ĐÂY:
- KHI CÁC LỖ MỜ KHÔNG THEO QUY ĐỊNH PHẢI CÓ SỰ CHẤP THUẬN CỦA KỸ SƯ TƯ VẤN

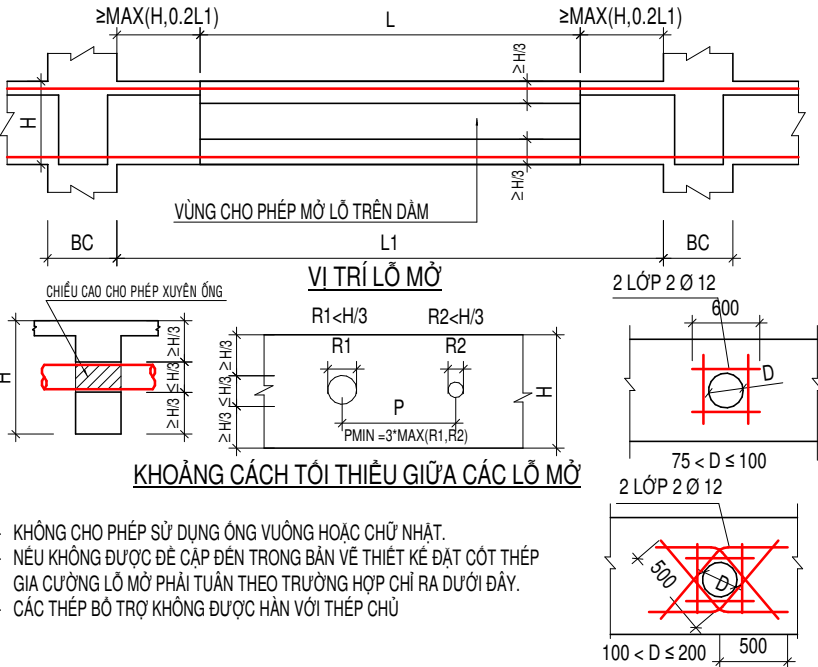


## 8. CHI TIẾT CẤU TẠO KHÁC

### 8.1 CHI TIẾT LIÊN KẾT CỘT - TƯỜNG

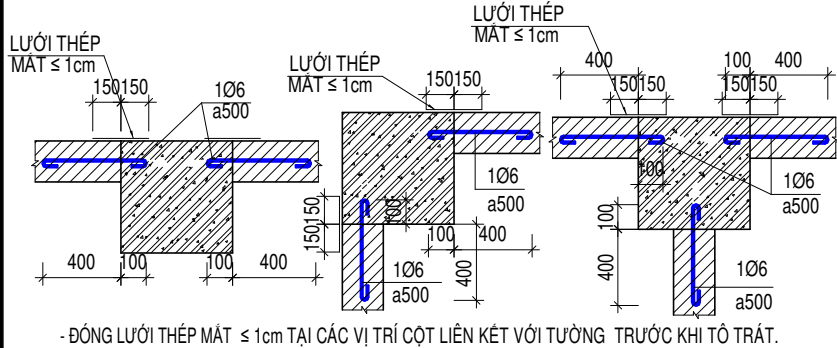

### 8.2 CHI TIẾT GIĂNG ĐÌNH TƯỜNG, GIĂNG NGANG, TRỤ TƯỜNG


- ÁP DỤNG VỚI TƯỜNG CÓ BÊ DÀY B<sub>1</sub> ≥ 150MM
- ÁP DỤNG VỚI TƯỜNG CÓ BÊ DÀY B<sub>1</sub> < 150MM

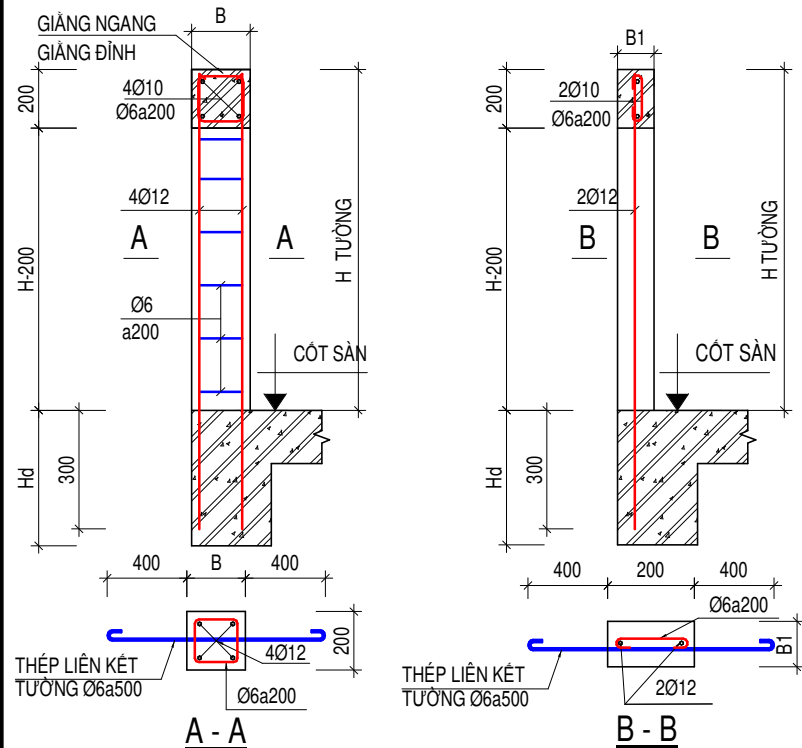

### 8.3 CHI TIẾT BỐ TRỤ TƯỜNG, GIĂNG TƯỜNG :


KHI KHÔNG CÓ BẢN VẼ CHI TIẾT VIỆC BỐ TRỤ TƯỜNG VÀ GIĂNG TƯỜNG TUÂN THỦ QUY ĐỊNH SAU:

- KHI KÍCH THƯỚC MÀNG TƯỜNG XÂY CHÈN KHUNG LỚN YẾU CẦU BỐ TRỤ NHƯ CÁC TRƯỜNG HỢP DƯỚI ĐÂY:

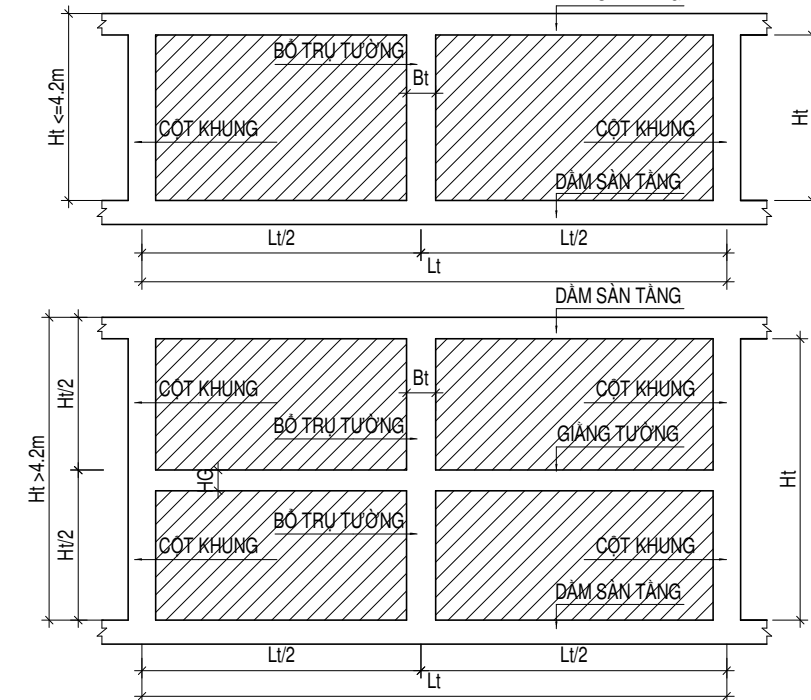


- 4m ≤ L<sub>t</sub> ≤ 7m: VỚI TƯỜNG XÂY CỘ CHIỀU DÀY < 150mm
- 5m ≤ L<sub>t</sub> ≤ 8m: VỚI TƯỜNG XÂY CỘ CHIỀU DÀY ≥ 150mm

KHI KÍCH THƯỚC MÀNG TƯỜNG HỖ LỚN YẾU CẦU BỐ TRỤ VÀ GIĂNG TƯỜNG NHƯ CÁC TRƯỜNG HỢP DƯỚI ĐÂY

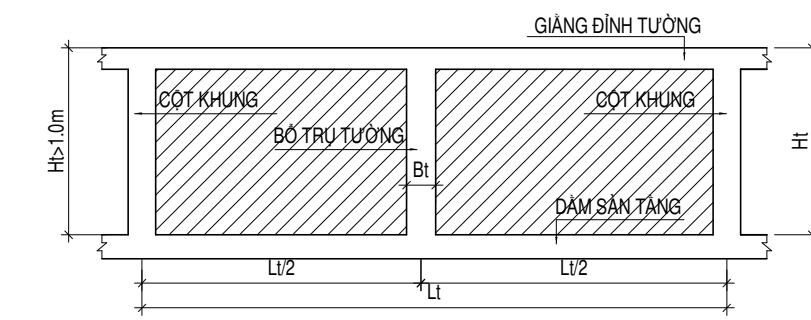


- L<sub>t</sub> > 4m, L<sub>t</sub> < 7m: VỚI TƯỜNG XÂY CỘ CHIỀU DÀY < 150mm
- L<sub>t</sub> > 5m, L<sub>t</sub> < 8m: VỚI TƯỜNG XÂY CỘ CHIỀU DÀY ≥ 150mm

### 8.5 CHI TIẾT XỬ LÝ MÓNG KHÁC CAO ĐỘ GIỮA 2 NHÀ

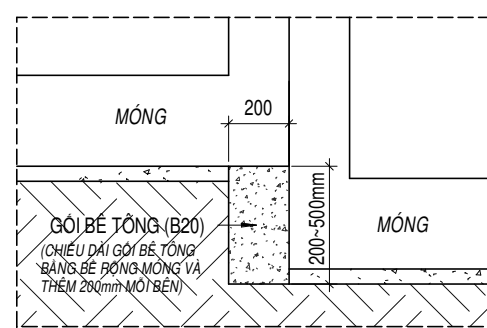

### 8.6 CHI TIẾT CHÈNH CAO ĐỘ GIỮA 2 NHÀ

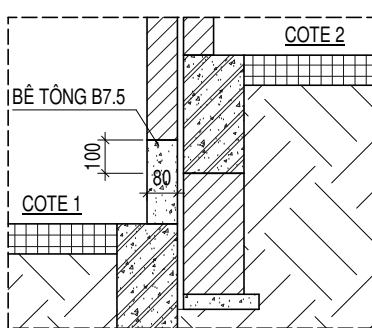

### 8.8 CÔNG TÁC CỘP PHA, ĐÀ GIÁO

- CỘP PHA SÀN VÀ DÀM VỚI KHẨU ĐỘ LỚN HƠN 5M (VỚI CONSOL CHIỀU DÀI VƯỢN LỚN HƠN 2M) PHẢI ĐƯỢC THIẾT KẾ CÓ ĐỘ VÒNG THI CÔNG. TRỊ SỐ ĐỘ VÒNG ĐƯỢC TÍNH THEO CÔNG THỨC:



$$f = \frac{3L}{1000}$$

TRONG ĐÓ: L LÀ KHẨU ĐỘ, TÍNH BẰNG M.

- ĐỐI VỚI CONSOL L = 2L<sub>1</sub> VỚI L<sub>1</sub> LÀ CHIỀU DÀI VƯỢN CỦA CONSOL.
- KHI THẢO DỒ CỘP PHA SÀN, CỘT CHỖNG & ĐÀ GIÁO CẦN TUÂN THỦ NGUYÊN TẮC + GIỮ LẠI TOÀN BỘ (100%) CỘT CHỖNG & ĐÀ GIÁO Ở TẦM SÀN NẾM KẾ DƯỚI TẦM SÀN SÁP ĐỘ BÊ TÔNG.
- THẢO DỒ TỪNG BỘ PHẬN CỘT CHỖNG (50%) CỦA TẦM SÀN DƯỚI NỬA. ĐỐI VỚI CÁC DÀM CÓ NHỊP LỚN HƠN 4M, CẦN GIỮ LẠI CÁC CỘT CHỖNG CÁCH NHAU TỐI ĐA 3M.


### 8.4 QUY ĐỊNH VỀ LANH TÔ

#### MAT CẮT CẤU KIỆN ĐÀ LANH TÔ ĐIỂN HÌNH

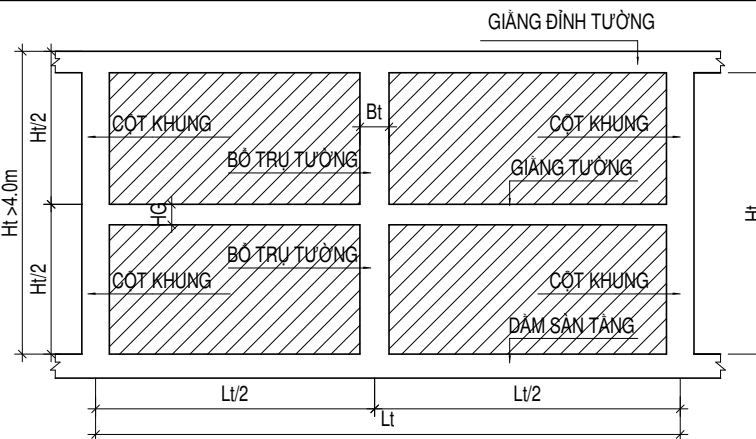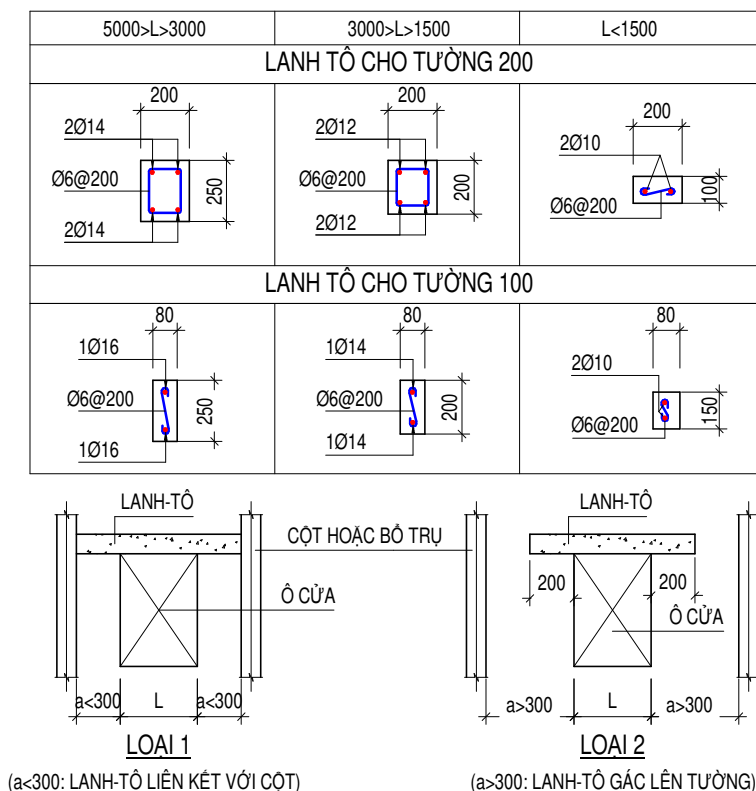


### 8.7 QUY ĐỊNH VỀ KHOAN CÂY THÉP :

- KHI CÁC CẤU KIỆN CỦA CÔNG TRÌNH ĐÀ THI CÔNG CẦN LIÊN KẾT VỚI CÁC CẤU KIỆN MỚI, THI TUÂN THỦ CÁC CHỈ DẪN VÀ BẢN VẼ DƯỚI ĐÂY:
- KHOAN CÂY THÉP BẰNG KEO LIÊN KẾT RAMSET EPON G5 HOẶC LOẠI CÓ CƯỜNG ĐỘ TƯƠNG ĐƯƠNG.
- CHIỀU DÀI ĐOẠN KHOAN CÂY TÙY THEO YẾU CẦU KỸ THUẬT CỦA NHÀ SẢN XUẤT NHƯNG KHÔNG NHỎ HƠN 10D.
- CÁC CHỈ DẪN THI CÔNG KHOAN CÂY CẦN TUÂN THỦ THEO NHÀ SẢN XUẤT.

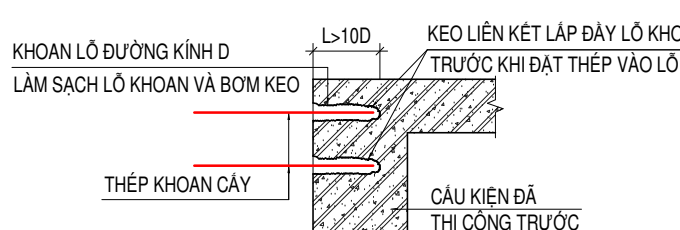

### 8.9 CHI TIẾT SÀN CAO HƠN COTE DÀM

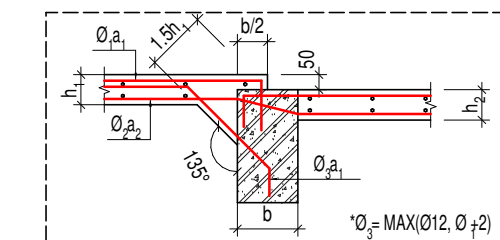

#### GHI CHÚ:

- CÁC ĐƠN VỊ THI CÔNG PHẢI PHỐI HỢP BẢN VẼ CỦA TẤT CẢ CÁC BỘ MÔN KHÁC NẾU THẤY SỰ KHÁC BIỆT PHẢI BẢO CHO ĐƠN VỊ THIẾT KẾ ĐỂ XỬ LÝ.
- KHI XỬ LÝ SỰ KHÁC BIỆT, PHẢI THỰC HIỆN ƯU TIÊN THEO THỨ TỰ GIỮA CÁC BỘ MÔN: KIẾN TRÚC → KẾT CẤU / BỘ MÔN KHÁC; HOẶC ƯU TIÊN TRONG CÙNG BỘ MÔN: CHI TIẾT → TỔNG THỂ
- CÁC SỐ LƯU KÍCH THƯỚC PHẢI ĐƯỢC KIỂM TRA THỰC TẾ TẠI CÔNG TRÌNH, NẾU THẤY SỰ KHÁC BIỆT SỐ VỚI BẢN VẼ THI PHẢI BẢO CHO ĐƠN VỊ THIẾT KẾ.

#### HIỆU CHỈNH:

| REV | NGÀY | NỘI DUNG |
|-----|------|----------|
|-----|------|----------|

#### CHỦ ĐẦU TƯ:

CÔNG TY TNHH ĐẦU TƯ

**PHÚ VIỆT TÍN**

ĐỊA CHỈ: LÔ 18-19 QUỐC LỘ 1A, XÃ DẦU GIẤY, TỈNH ĐỒNG NAI, VIỆT NAM

#### CTHĐT

ĐẶNG PHƯỚC BÌNH

#### ĐƠN VỊ THIẾT KẾ:

CÔNG TY CỔ PHẦN TƯ VẤN THIẾT KẾ

**BASE ARC**

ĐỊA CHỈ: 138 ĐIỆN BIÊN PHỦ, PHƯỜNG TÂN ĐỊNH, TP. HỒ CHÍ MINH, VIỆT NAM

#### TỔNG GIÁM ĐỐC

TRẦN ĐỨC AN

#### CHỦ NHIỆM DỰ ÁN:

KTS. NGUYỄN THÀNH THÁI

#### CHỦ TRÌ THIẾT KẾ:

KS. NGÔ TÙNG THÀNH

#### THIẾT KẾ:

KS. NGUYỄN MINH DUY BẰNG

#### KIỂM TRA:

KS. NGÔ TÙNG THÀNH

#### DỰ ÁN:

KHU DÂN CƯ A1-C1 (ĐÔ THỊ DẦU GIẤY)

ĐỊA ĐIỂM: XÃ DẦU GIẤY, TỈNH ĐỒNG NAI

#### CÔNG TRÌNH:

NHÀ Ở THƯƠNG MẠI LIÊN KẾ

#### HẠNG MỤC:

MẪU NHÀ T3\_2b

#### TÊN BẢN VẼ:

GHI CHÚ CHUNG-03

#### MỤC ĐÍCH PHÁT HÀNH:


|                            |         |
|----------------------------|---------|
| BẢN VẼ MỜI THẦU            |         |
| THIẾT KẾ CƠ SỞ             |         |
| ✓ THIẾT KẾ BẢN VẼ THI CÔNG |         |
| BẢN VẼ HOÀN CÔNG           |         |
| HOÀN THÀNH                 | 07/2025 |
| TỶ LỆ                      | NTS     |
| SỐ HIỆU BẢN VẼ             | KC-04   |



# PHẦN MÓNG PHƯƠNG ÁN 1


ÁP DỤNG CHO CÁC LÔ:

- LK2-26
- LK3-1
- LK4-27
- LK13-28
- LK14A-1
- LK15-28

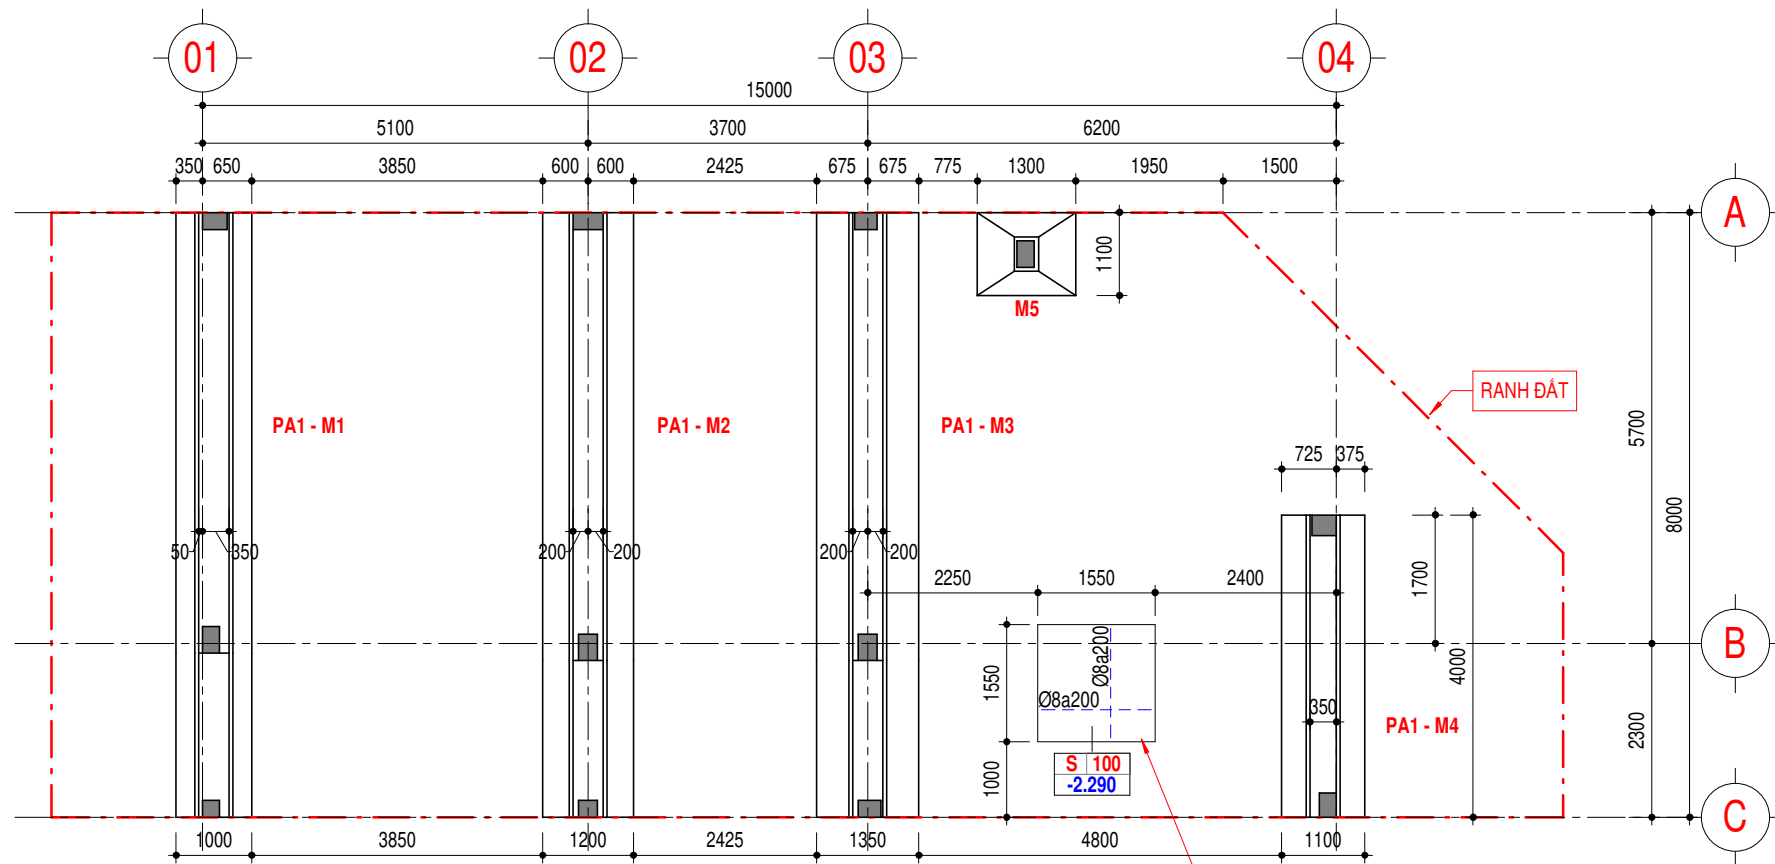

MẶT BẰNG BỐ TRÍ MÓNG

TL 1 : 100

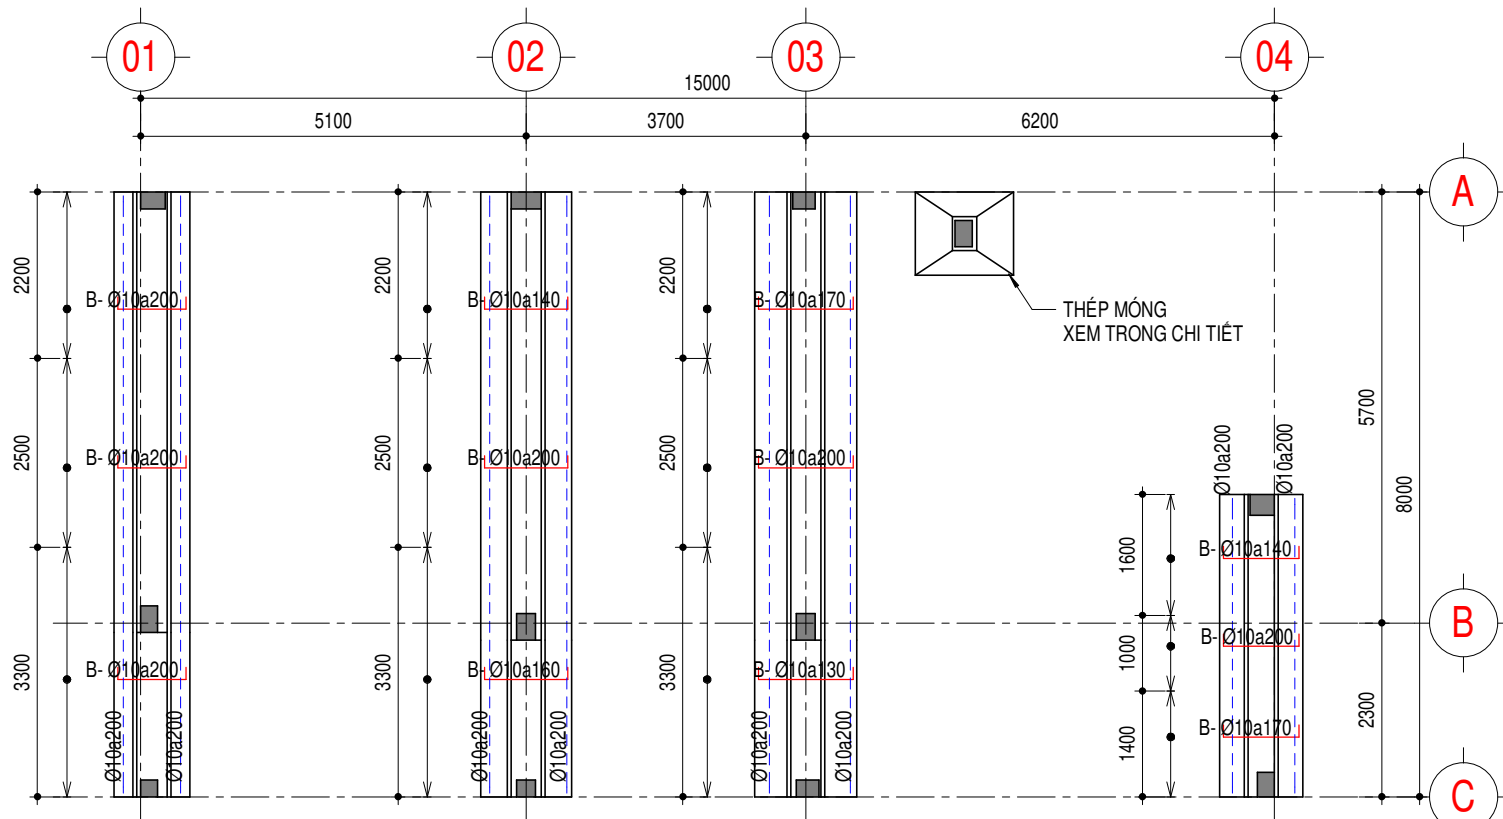

MẶT BẰNG BỐ TRÍ THÉP ĐÁY MÓNG

TL 1 : 100

| CAO ĐỘ HOÀN THIỆN KIẾN TRÚC |         |
|-----------------------------|---------|
| MẶT BẰNG                    | CAO ĐỘ  |
| ĐỈNH Mái                    | +11.000 |
| Mái                         | +10.000 |
| TẦNG 3                      | +6.800  |
| TẦNG 2                      | +3.600  |
| TẦNG 1                      | +0.000  |

|     | CAO ĐỘ (m) | CỘT ĐỊA TẦNG    | MÔ TẢ                              |
|-----|------------|-----------------|------------------------------------|
| LỚP | (±0.000)   | MĐTN            |                                    |
| 1   | (H)        | CAO ĐỘ ĐÁY MÓNG | Sét dẻo thấp, xám nâu đỏ, dẻo mềm  |
| L   |            |                 | Đá bazan                           |
| 1   |            |                 | Sét dẻo thấp, xám nâu đỏ, dẻo cứng |

GHI CHÚ:

- ĐÁY MÓNG PHẢI ĐƯỢC ĐẶT TRÊN LỚP ĐẤT TỰ NHIÊN HIỆN TRẠNG. HỆ SỐ ĐẢM CHẤT K = 0.9.
- NHÀ THẦU CẦN CÓ BIỆN PHÁP BƠM HÚT NƯỚC VÀ CHỐNG ĐỔ VÁCH HỒ ĐÀM BẢO AN TOÀN CHO CÁC CÔNG TRÌNH HIỆN HỮU.
- COTE ±0.000 LÀ CAO ĐỘ THIẾT KẾ KIẾN TRÚC, CAO ĐỘ QUỐC GIA XEM BẢN VẼ KIẾN TRÚC.
- TẤT CẢ CÁC KÍCH THƯỚC KIỂM TRA VÀ XÁC NHẬN TRÊN CÔNG TRƯỜNG.
- KÍCH THƯỚC VÀ VỊ TRÍ CÁC LỖ GEN, MƯƠNG, LAM TRANG TRÍ PHẢI ĐƯỢC KIỂM TRA SO VỚI CÁC BẢN VẼ KIẾN TRÚC, MEP CỎ LIÊN QUAN.
- CÁC VỊ TRÍ ỜNG XUYỀN DÀM XEM BẢN VẼ MEP. CHI TIẾT XUYỀN DÀM XEM BẢN VẼ GHI CHÚ CHUNG.
- KÍCH THƯỚC, CHIỀU SÂU ĐẶT TẤM ĐAN BÊ TỰ HOẠI XEM BẢN VẼ MEP TRƯỚC KHI THI CÔNG. TẤM ĐAN BÊ TỰ HOẠI SỬ DỤNG BÊ TÔNG CỘT THÉP ĐÁ 1x2, CẤP ĐỘ BỀN B15.
- CƯỜNG ĐỘ CHỊU TẢI ĐẤT NỀN:  $R_{dn} = 250 \text{ kN/m}^2$ .
- CAO ĐỘ ĐÁY MÓNG (H) VÀ VỊ TRÍ ÁP DỤNG CHO CÁC LỖ:
  - LK13-28; LK14A-1; LK15-28: H = -1.5m SO VỚI COTE ±0.000
  - LK2-26: H = -1.8m SO VỚI COTE ±0.000
  - LK3-1; LK4-27: H = -2.0m SO VỚI COTE ±0.000

GHI CHÚ:

- CÁC ĐƠN VỊ THI CÔNG PHẢI PHỐI HỢP BẢN VẼ CỦA TẤT CẢ CÁC BỘ MÔN KHÁC NẾU THẤY SỰ KHÁC BIỆT PHẢI BẢO CHO ĐƠN VỊ THIẾT KẾ ĐỂ XỬ LÝ.
- KHI XỬ LÝ SỰ KHÁC BIỆT, PHẢI THỰC HIỆN ƯU TIÊN THEO THỨ TỰ GIỮA CÁC BỘ MÔN: KIẾN TRÚC → KẾT CẤU / BỘ MÔN KHÁC; HOẶC ƯU TIÊN TRONG CÙNG BỘ MÔN: CHI TIẾT → TỔNG THỂ
- CÁC SỐ LIEU KÍCH THƯỚC PHẢI ĐƯỢC KIỂM TRA THỰC TẾ TẠI CÔNG TRÌNH, NẾU THẤY SỰ KHÁC BIỆT SO VỚI BẢN VẼ THI PHẢI BẢO CHO ĐƠN VỊ THIẾT KẾ.

HIỆU CHỈNH:

| REV | NGÀY | NỘI DUNG |
|-----|------|----------|
|-----|------|----------|

CHỦ ĐẦU TƯ:

CÔNG TY TNHH ĐẦU TƯ

**PHÚ VIỆT TÍN**

ĐỊA CHỈ: LÔ 18-19 QUỐC LỘ 1A, XÃ DẦU GIẤY, TỈNH ĐỒNG NAI, VIỆT NAM

CTHĐT

ĐẠNG PHƯỚC BÌNH

ĐƠN VỊ THIẾT KẾ:

CÔNG TY CỔ PHẦN TƯ VẤN THIẾT KẾ

**BASE ARC**

ĐỊA CHỈ: 138 ĐIỆN BIÊN PHỦ, PHƯỜNG TÂN ĐỊNH, TP. HỒ CHÍ MINH, VIỆT NAM

TỔNG GIÁM ĐỐC

TRẦN ĐỨC AN

CHỦ NHIỆM DỰ ÁN:

KTS. NGUYỄN THÀNH THÁI

CHỦ TRÌ THIẾT KẾ:

KS. NGÔ TÙNG THÀNH

THIẾT KẾ:

KS. NGUYỄN MINH DUY BẰNG

KIỂM TRA:

KS. NGÔ TÙNG THÀNH

DỰ ÁN:

KHU DÂN CƯ A1-C1 (ĐÔ THỊ DẦU GIẤY)

ĐỊA ĐIỂM: XÃ DẦU GIẤY, TỈNH ĐỒNG NAI

CÔNG TRÌNH:

NHÀ Ở THƯƠNG MẠI LIÊN KẾ

HẠNG MỤC:


MẪU NHÀ T3\_2b

TÊN BẢN VẼ:

MẶT BẰNG BỐ TRÍ MÓNG, THÉP ĐÁY MÓNG


MỤC ĐÍCH PHÁT HÀNH:

|                                                              |         |
|--------------------------------------------------------------|---------|
| BẢN VẼ MỜI THẦU                                              |         |
| THIẾT KẾ CƠ SỞ                                               |         |
| <input checked="" type="checkbox"/> THIẾT KẾ BẢN VẼ THI CÔNG |         |
| BẢN VẼ HOÀN CÔNG                                             |         |
| HOÀN THÀNH                                                   | 07/2025 |
| TỶ LỆ                                                        | NTS     |
| SỐ HIỆU BẢN VẼ                                               | KC-07   |

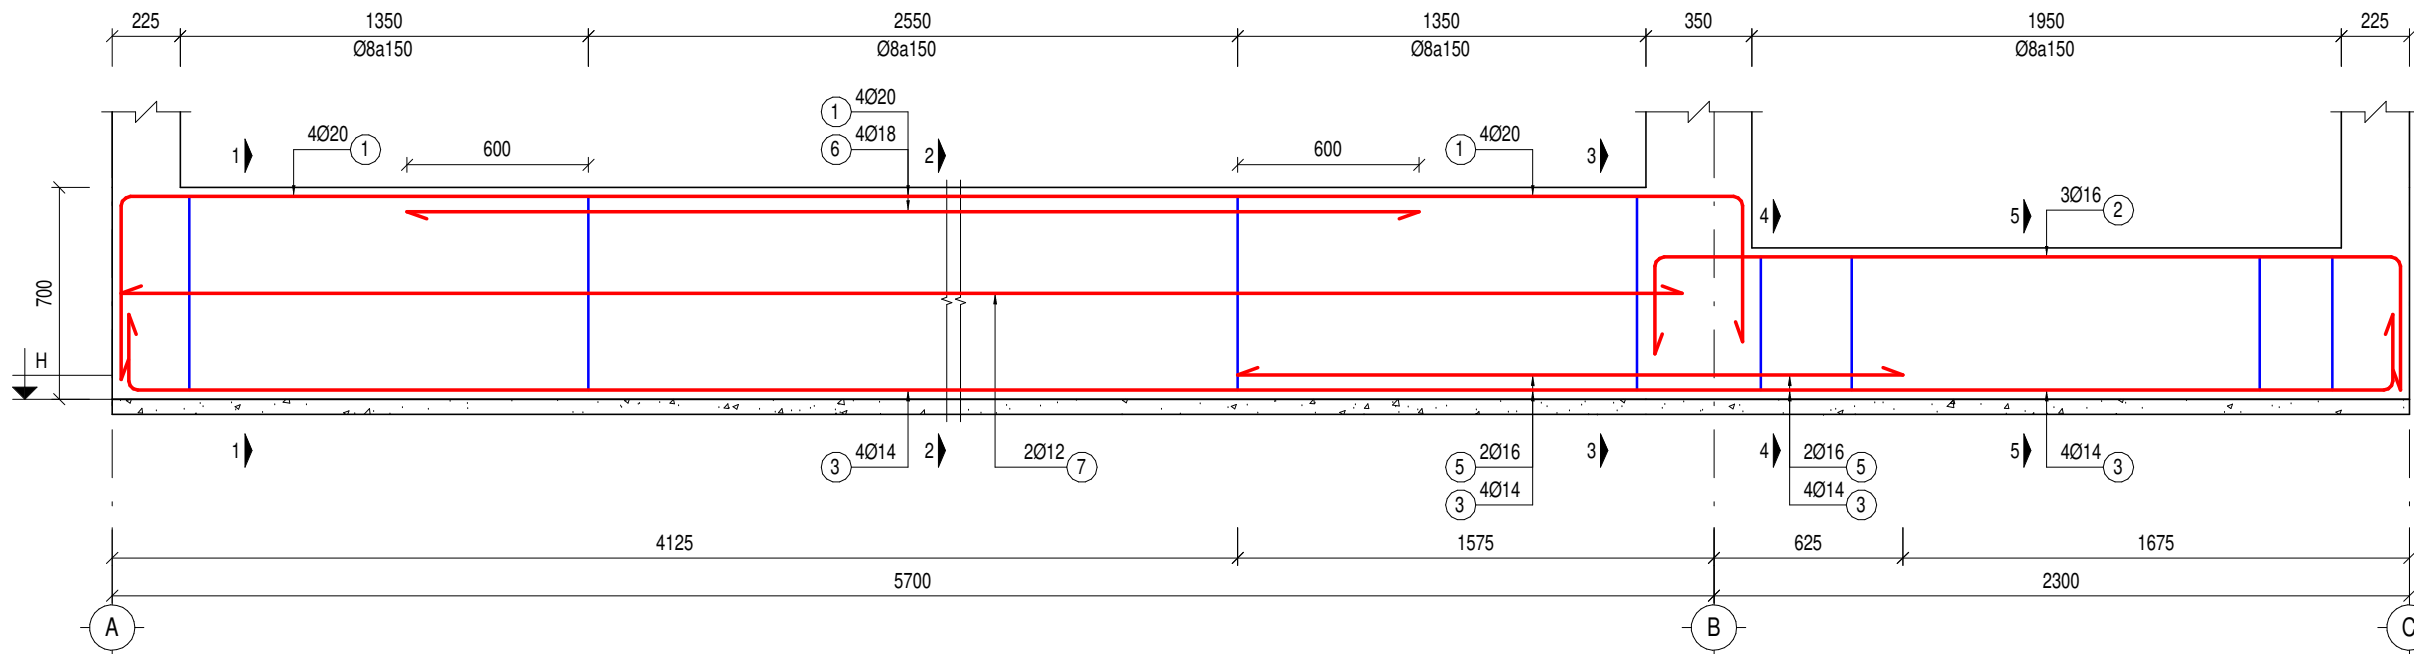


### MÓNG PA1 - M1 (SL=1; L=8000)

TL: 1/25

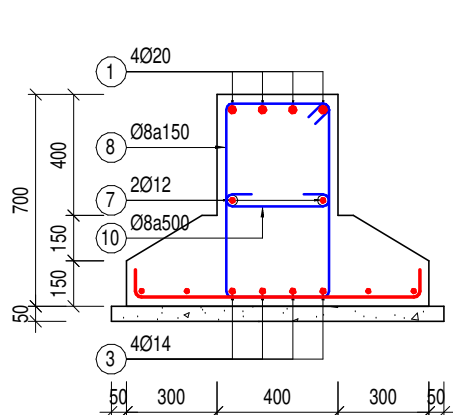


#### MC 1-1

PA1 - M1 (TL: 1/25)

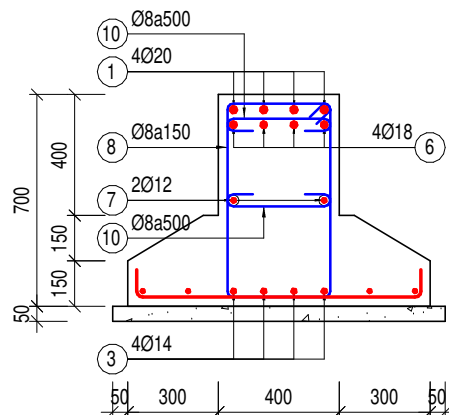


#### MC 2-2

PA1 - M1 (TL: 1/25)

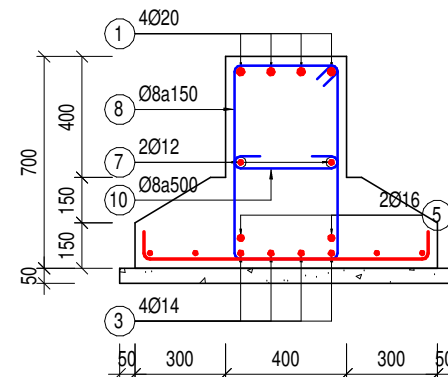


#### MC 3-3

PA1 - M1 (TL: 1/25)

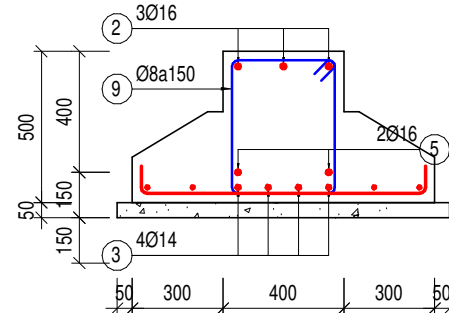

#### MC 4-4

PA1 - M1 (TL: 1/25)

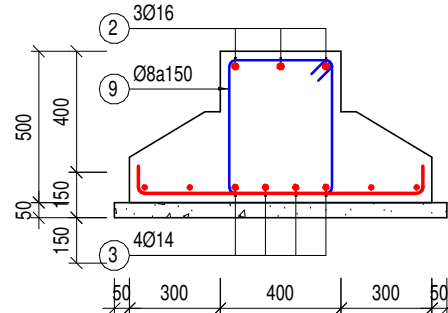

#### MC 5-5

PA1 - M1 (TL: 1/25)

#### GHI CHÚ:

- CÁC ĐƠN VỊ THI CÔNG PHẢI PHỐI HỢP BẢN VẼ CỦA TẤT CẢ CÁC BỘ MÔN KHÁC NẾU THẤY SỰ KHÁC BIỆT PHẢI BẢO CHO ĐƠN VỊ THIẾT KẾ ĐỂ XỬ LÝ.
- KHI XỬ LÝ SỰ KHÁC BIỆT, PHẢI THỰC HIỆN ƯU TIÊN THEO THỨ TỰ GIỮA CÁC BỘ MÔN: KIẾN TRÚC → KẾT CẤU / BỘ MÔN KHÁC; HOẶC ƯU TIÊN TRONG CÙNG BỘ MÔN: CHI TIẾT → TỔNG THỂ.
- CÁC SỐ LIỆU KÍCH THƯỚC PHẢI ĐƯỢC KIỂM TRA THỰC TẾ TẠI CÔNG TRÌNH, NẾU THẤY SỰ KHÁC BIỆT SƠ VỚI BẢN VẼ THI PHẢI BẢO CHO ĐƠN VỊ THIẾT KẾ.

#### HIỆU CHỈNH:

| REV | NGÀY | NỘI DUNG |
|-----|------|----------|
|-----|------|----------|

#### CHỦ ĐẦU TƯ:

CÔNG TY TNHH ĐẦU TƯ

**PHÚ VIỆT TÍN**

ĐỊA CHỈ: LÔ 18-19 QUỐC LỘ 1A, XÃ DẦU GIẤY,  
TỈNH ĐỒNG NAI, VIỆT NAM

#### CTHĐT

ĐẶNG PHƯỚC BÌNH

#### ĐƠN VỊ THIẾT KẾ:

CÔNG TY CỔ PHẦN TƯ VẤN THIẾT KẾ

**BASE ARC**

ĐỊA CHỈ: 138 ĐIỆN BIÊN PHỦ, PHƯỜNG TÂN ĐỊNH,  
TP. HỒ CHÍ MINH, VIỆT NAM

#### TỔNG GIÁM ĐỐC

TRẦN ĐỨC AN

#### CHỦ NHIỆM DỰ ÁN:

KTS. NGUYỄN THÀNH THÁI

#### CHỦ TRÌ THIẾT KẾ:

KS. NGÔ TÙNG THÀNH

#### THIẾT KẾ:

KS. NGUYỄN MINH DUY BẰNG

#### KIỂM TRA:

KS. NGÔ TÙNG THÀNH

#### DỰ ÁN:

KHU DÂN CƯ A1-C1 (ĐÔ THỊ DẦU GIẤY)

ĐỊA ĐIỂM: XÃ DẦU GIẤY, TỈNH ĐỒNG NAI

#### CÔNG TRÌNH:

NHÀ Ở THƯƠNG MẠI LIÊN KẾ

#### HẠNG MỤC:

MẪU NHÀ T3\_2b


#### TÊN BẢN VẼ:

CHI TIẾT MÓNG-01

#### MỤC ĐÍCH PHÁT HÀNH:


|                                     |                          |
|-------------------------------------|--------------------------|
| <input type="checkbox"/>            | BẢN VẼ MỜI THẦU          |
| <input type="checkbox"/>            | THIẾT KẾ CƠ SỞ           |
| <input checked="" type="checkbox"/> | THIẾT KẾ BẢN VẼ THI CÔNG |
| <input type="checkbox"/>            | BẢN VẼ HOÀN CÔNG         |

|                |         |
|----------------|---------|
| HOÀN THÀNH     | 07/2025 |
| TỶ LỆ          | NTS     |
| SỐ HIỆU BẢN VẼ | KC-08   |

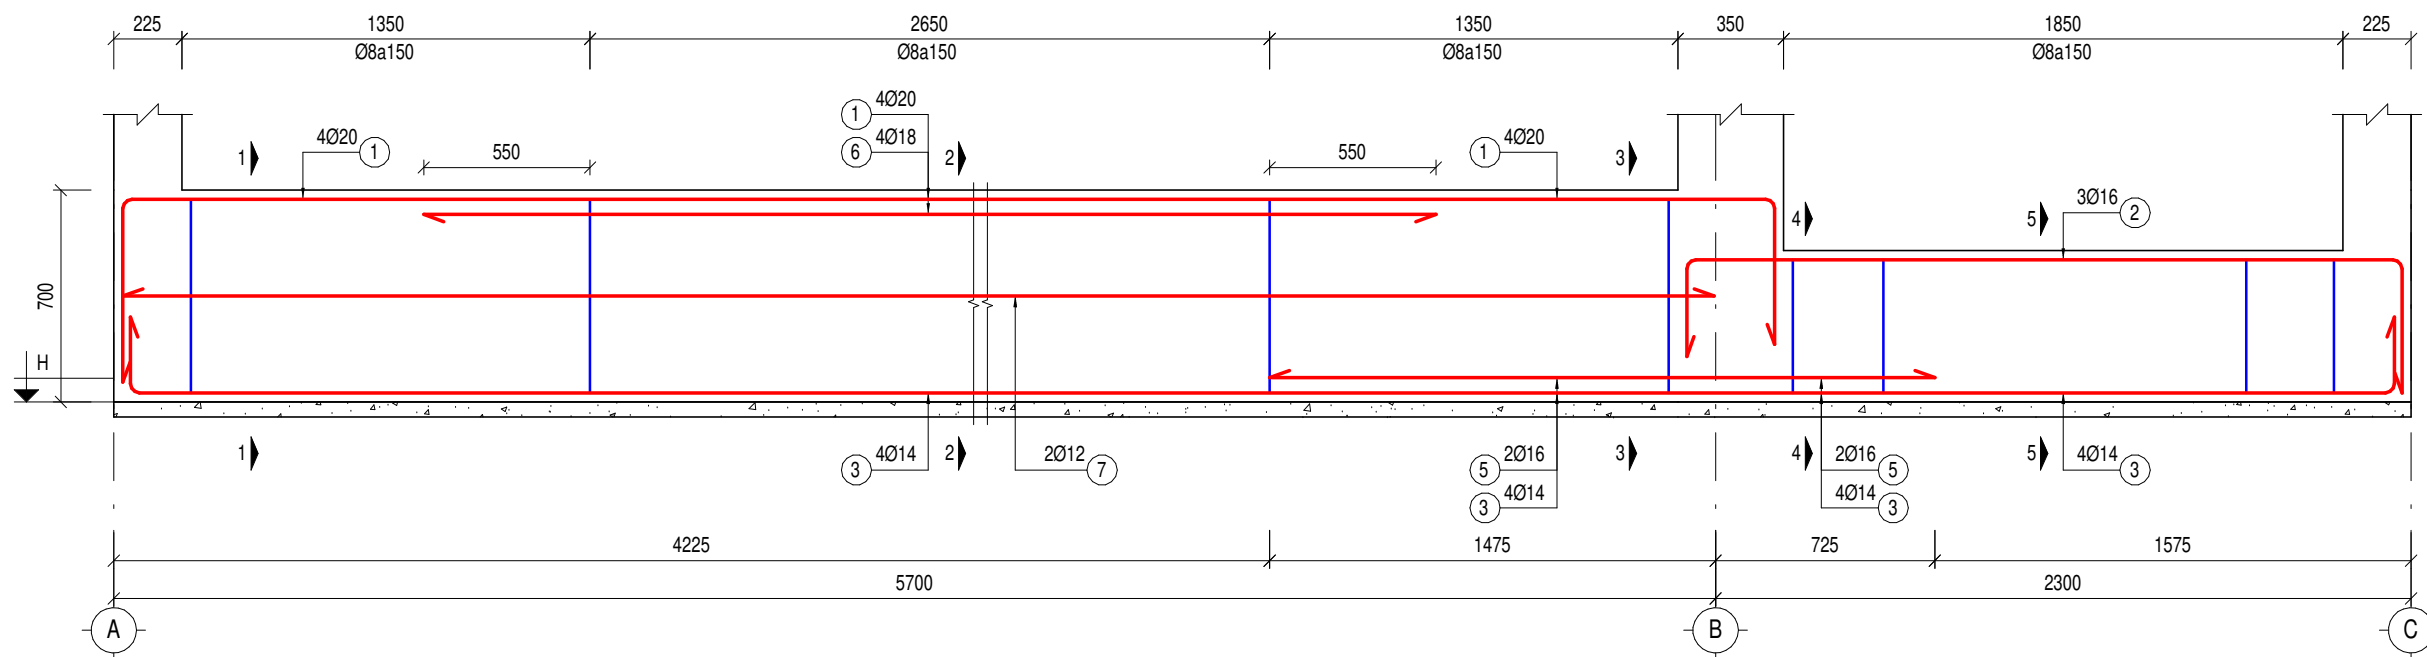


### MÓNG PA1 - M2 (SL=1; L=8000)


TL: 1/25

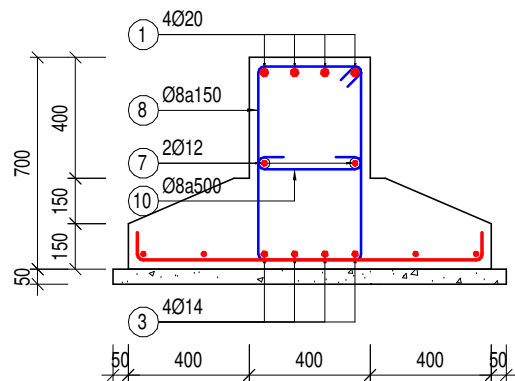


MC 1-1  
PA1 - M2 (TL: 1/25)

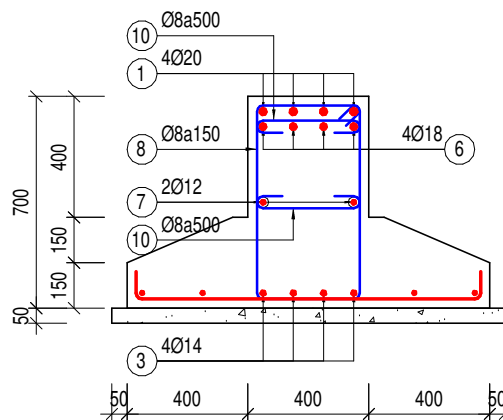


MC 2-2  
PA1 - M2 (TL: 1/25)

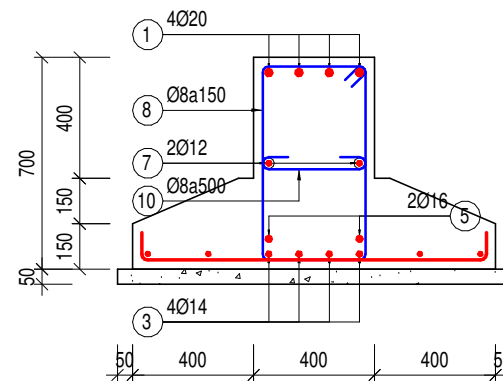

MC 3-3  
PA1 - M2 (TL: 1/25)

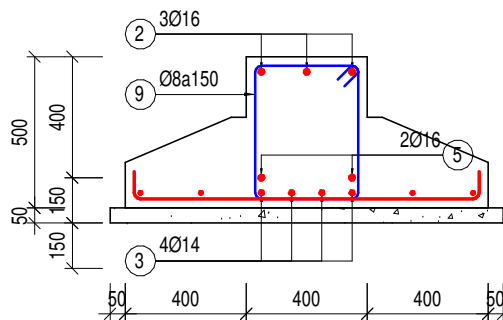

MC 4-4  
PA1 - M2 (TL: 1/25)

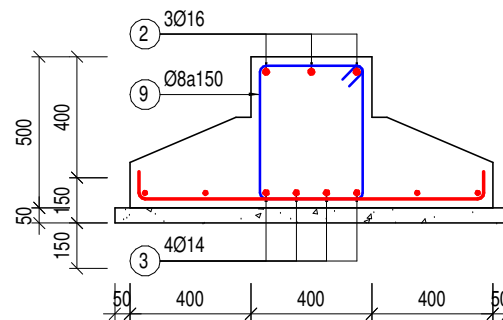

MC 5-5  
PA1 - M2 (TL: 1/25)

#### GHI CHÚ:

- CÁC ĐƠN VỊ THI CÔNG PHẢI HỢP BÀN VẼ CỦA TẤT CẢ CÁC BỘ MÔN KHÁC NẾU THẤY SỰ KHÁC BIỆT PHẢI BẢO CHO ĐƠN VỊ THIẾT KẾ ĐỂ XỬ LÝ.
- KHI XỬ LÝ SỰ KHÁC BIỆT, PHẢI THỰC HIỆN ƯU TIÊN THEO THỨ TỰ GIỮA CÁC BỘ MÔN: KIẾN TRÚC → KẾT CẤU / BỘ MÔN KHÁC; HOẶC ƯU TIÊN TRONG CÙNG BỘ MÔN: CHI TIẾT → TỔNG THỂ.
- CÁC SỐ LIỆU KÍCH THƯỚC PHẢI ĐƯỢC KIỂM TRA THỰC TẾ TẠI CÔNG TRÌNH, NẾU THẤY SỰ KHÁC BIỆT SƠ VỚI BẢN VẼ THI PHẢI BẢO CHO ĐƠN VỊ THIẾT KẾ.

#### HIỆU CHỈNH:

| REV | NGÀY | NỘI DUNG |
|-----|------|----------|
|-----|------|----------|

#### CHỦ ĐẦU TƯ:

CÔNG TY TNHH ĐẦU TƯ

**PHÚ VIỆT TÍN**

ĐỊA CHỈ: LÔ 18-19 QUỐC LỘ 1A, XÃ DẦU GIẤY,  
TỈNH ĐỒNG NAI, VIỆT NAM

CTHĐT

ĐẶNG PHƯỚC BÌNH

#### ĐƠN VỊ THIẾT KẾ:

CÔNG TY CỔ PHẦN TƯ VẤN THIẾT KẾ

**BASE ARC**

ĐỊA CHỈ: 138 ĐIỆN BIÊN PHỦ, PHƯỜNG TÂN ĐỊNH,  
TP. HỒ CHÍ MINH, VIỆT NAM

#### TỔNG GIÁM ĐỐC

TRẦN ĐỨC AN

#### CHỦ NHIỆM DỰ ÁN:

KTS. NGUYỄN THÀNH THÁI

#### CHỦ TRÌ THIẾT KẾ:

KS. NGÔ TÙNG THÀNH

#### THIẾT KẾ:

KS. NGUYỄN MINH DUY BẰNG

#### KIỂM TRA:

KS. NGÔ TÙNG THÀNH

#### DỰ ÁN:

KHU DÂN CƯ A1-C1 (ĐÔ THỊ DẦU GIẤY)

ĐỊA ĐIỂM: XÃ DẦU GIẤY, TỈNH ĐỒNG NAI

#### CÔNG TRÌNH:

NHÀ Ở THƯƠNG MẠI LIÊN KẾ

#### HẠNG MỤC:

MẪU NHÀ T3\_2b


#### TÊN BẢN VẼ:

CHI TIẾT MÓNG-02

#### MỤC ĐÍCH PHÁT HÀNH:


|                                     |                          |
|-------------------------------------|--------------------------|
| <input type="checkbox"/>            | BẢN VẼ MỜI THẦU          |
| <input type="checkbox"/>            | THIẾT KẾ CƠ SỞ           |
| <input checked="" type="checkbox"/> | THIẾT KẾ BẢN VẼ THI CÔNG |
| <input type="checkbox"/>            | BẢN VẼ HOÀN CÔNG         |

|                |         |
|----------------|---------|
| HOÀN THÀNH     | 07/2025 |
| TỶ LỆ          | NTS     |
| SỐ HIỆU BẢN VẼ | KC-09   |

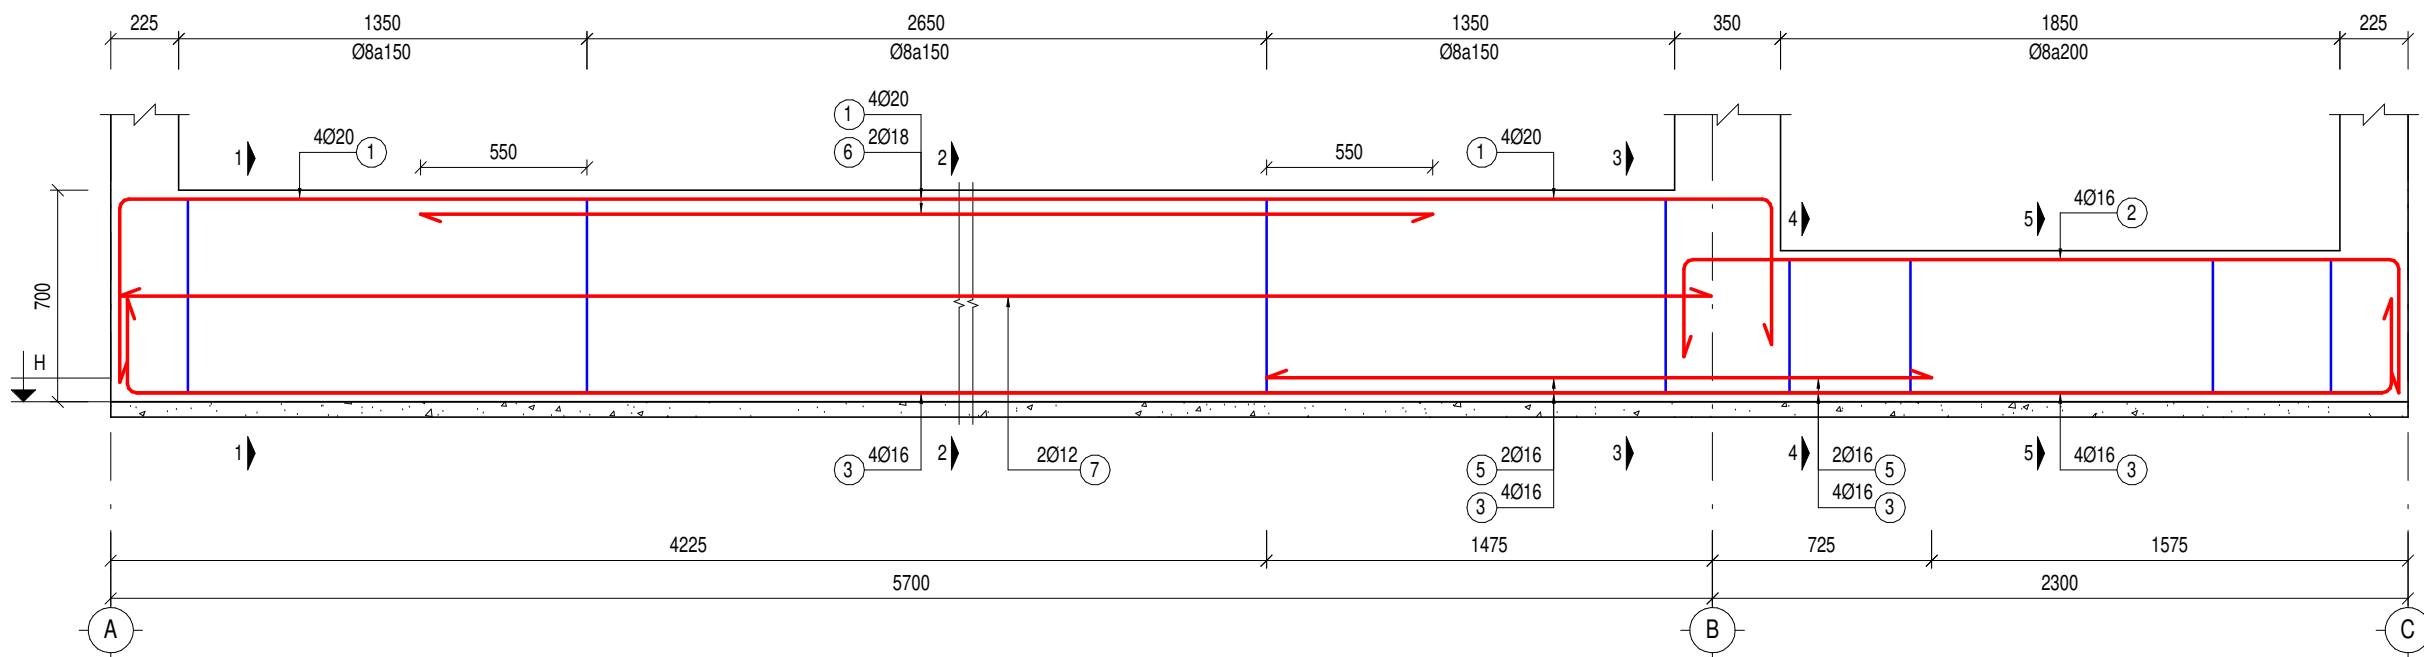


### MÓNG PA1 - M3 (SL=1; L=8000)


TL: 1/25

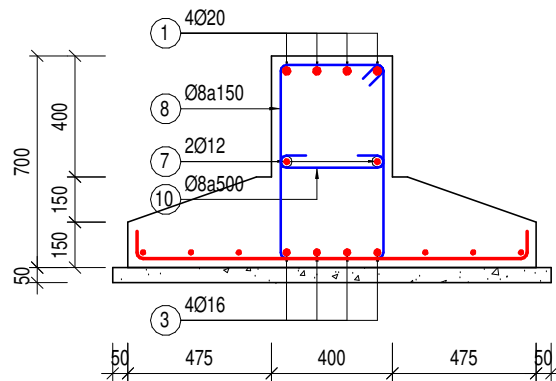


MC 1-1  
PA1 - M3 (TL: 1/25)

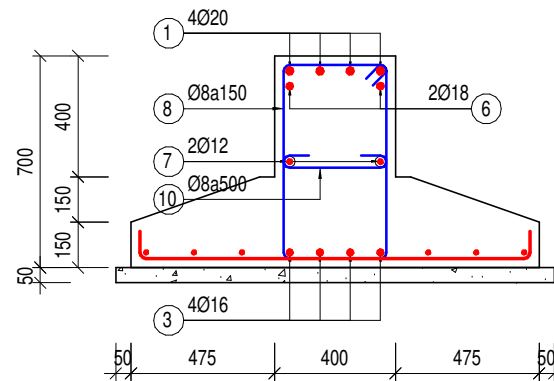


MC 2-2  
PA1 - M3 (TL: 1/25)

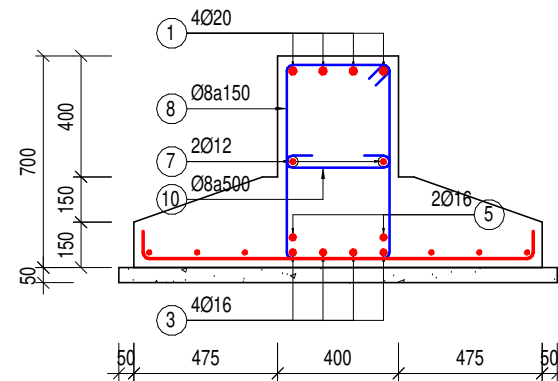

MC 3-3  
PA1 - M3 (TL: 1/25)

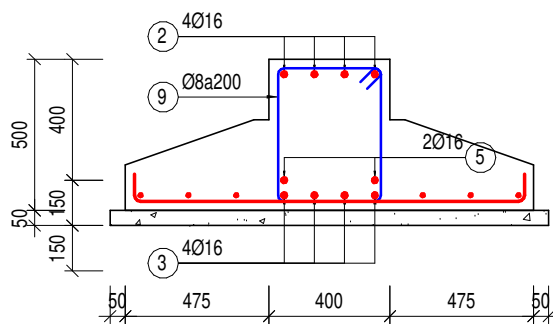

MC 4-4  
PA1 - M3 (TL: 1/25)

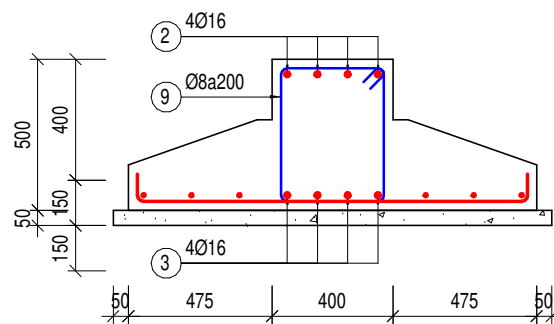

MC 5-5  
PA1 - M3 (TL: 1/25)

#### GHI CHÚ:

- CÁC ĐƠN VỊ THI CÔNG PHẢI HỢP BÀN VẼ CỦA TẤT CẢ CÁC BỘ MÔN KHÁC NẾU THẤY SỰ KHÁC BIỆT PHẢI BẢO CHO ĐƠN VỊ THIẾT KẾ ĐỂ XỬ LÝ.
- KHI XỬ LÝ SỰ KHÁC BIỆT, PHẢI THỰC HIỆN ƯU TIÊN THEO THỨ TỰ GIỮA CÁC BỘ MÔN: KIẾN TRÚC → KẾT CẤU / BỘ MÔN KHÁC; HOẶC ƯU TIÊN TRONG CÙNG BỘ MÔN: CHI TIẾT → TỔNG THỂ.
- CÁC SỐ LƯỢNG KÍCH THƯỚC PHẢI ĐƯỢC KIỂM TRA THỰC TẾ TẠI CÔNG TRÌNH, NẾU THẤY SỰ KHÁC BIỆT SƠ VỚI BẢN VẼ THI PHẢI BẢO CHO ĐƠN VỊ THIẾT KẾ.

#### HIỆU CHỈNH:

| REV | NGÀY | NỘI DUNG |
|-----|------|----------|
|-----|------|----------|

#### CHỦ ĐẦU TƯ:

CÔNG TY TNHH ĐẦU TƯ  
**PHÚ VIỆT TÍN**  
ĐỊA CHỈ: LÔ 18-19 QUỐC LỘ 1A, XÃ DẦU GIẤY,  
TỈNH ĐỒNG NAI, VIỆT NAM

#### CTHĐT

ĐẶNG PHƯỚC BÌNH

#### ĐƠN VỊ THIẾT KẾ:

CÔNG TY CỔ PHẦN TƯ VẤN THIẾT KẾ  
**BASE ARC**  
ĐỊA CHỈ: 138 ĐIỆN BIÊN PHỦ, PHƯỜNG TÂN ĐỊNH,  
TP. HỒ CHÍ MINH, VIỆT NAM

#### TỔNG GIÁM ĐỐC

TRẦN ĐỨC AN

#### CHỦ NHIỆM DỰ ÁN:

KTS. NGUYỄN THÀNH THÁI

#### CHỦ TRÌ THIẾT KẾ:

KS. NGÔ TÙNG THÀNH

#### THIẾT KẾ:

KS. NGUYỄN MINH DUY BẰNG

#### KIỂM TRA:

KS. NGÔ TÙNG THÀNH

#### DỰ ÁN:

KHU DÂN CƯ A1-C1 (ĐÔ THỊ DẦU GIẤY)  
ĐỊA ĐIỂM: XÃ DẦU GIẤY, TỈNH ĐỒNG NAI

#### CÔNG TRÌNH:

NHÀ Ở THƯƠNG MẠI LIÊN KẾ

#### HẠNG MỤC:

MẪU NHÀ T3\_2b

#### TÊN BẢN VẼ:

CHI TIẾT MÓNG-03


#### MỤC ĐÍCH PHÁT HÀNH:

|                                     |                          |
|-------------------------------------|--------------------------|
| <input type="checkbox"/>            | BẢN VẼ MỜI THẦU          |
| <input type="checkbox"/>            | THIẾT KẾ CƠ SỞ           |
| <input checked="" type="checkbox"/> | THIẾT KẾ BẢN VẼ THI CÔNG |
| <input type="checkbox"/>            | BẢN VẼ HOÀN CÔNG         |

HOÀN THÀNH 07/2025


TỶ LỆ NTS

SỐ HIỆU BẢN VẼ KC-10

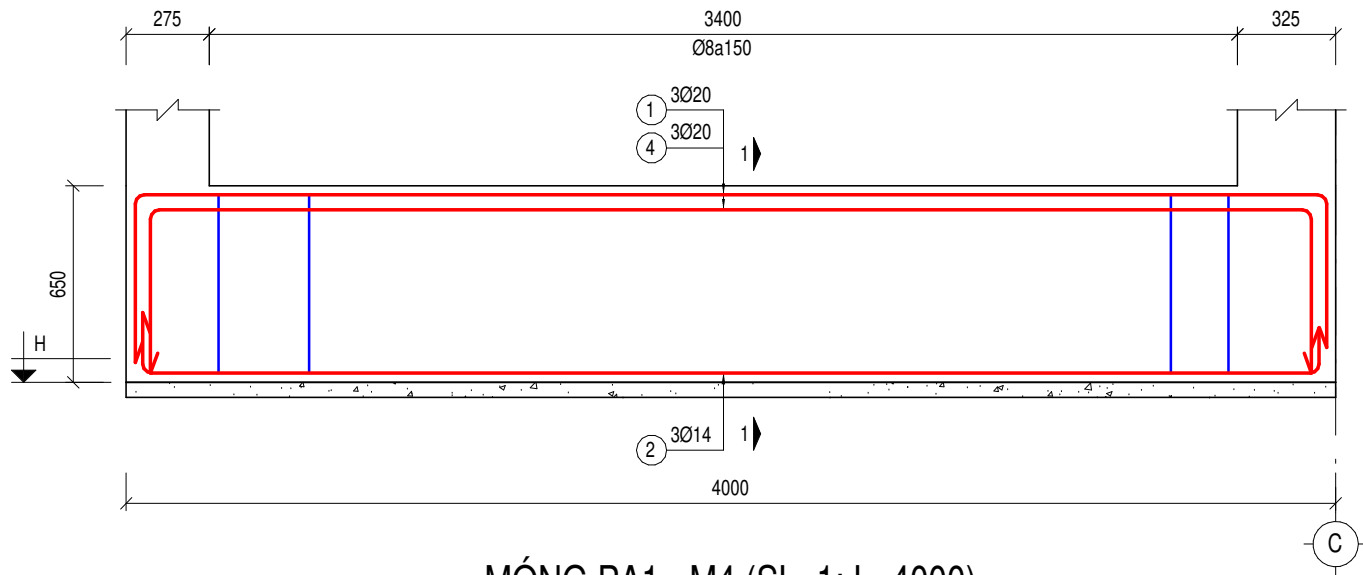


**MÓNG PA1 - M4 (SL=1; L=4000)**

TL: 1/25

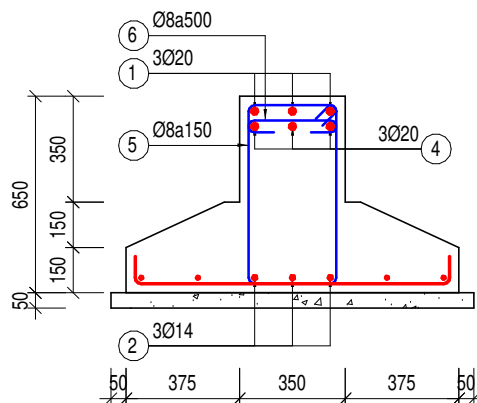


**MÓNG PA1 - M4 (SL=1; L=4000)**

MC 1-1 (TỶ LỆ: 1/25)

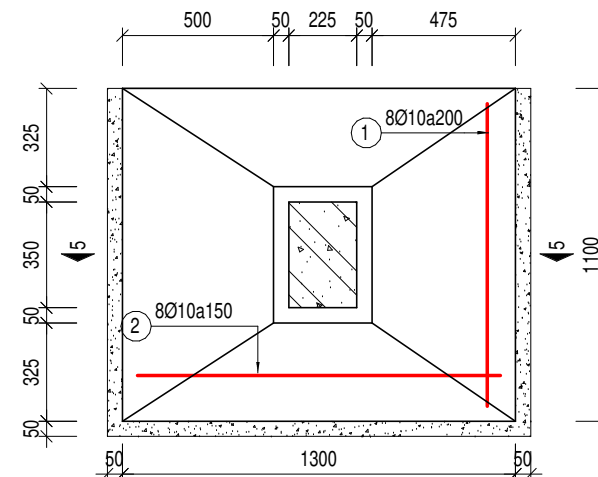

**MÓNG M5 (SL=1)**

TL: 1/25

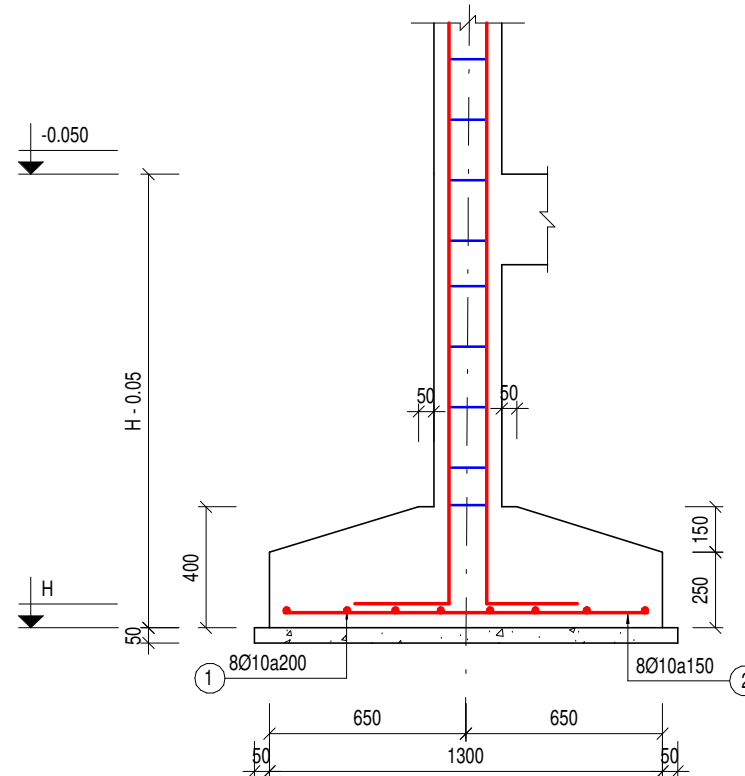

**MC 5-5**

TL: 1/25

**GHI CHÚ:**

- CÁC ĐƠN VỊ THI CÔNG PHẢI PHỐI HỢP BẢN VẼ CỦA TẤT CẢ CÁC BỘ MÔN KHÁC NẾU THẤY SỰ KHÁC BIỆT PHẢI BẢO CHỨNG ĐƠN VỊ THIẾT KẾ ĐỂ XỬ LÝ.
- KHI XỬ LÝ SỰ KHÁC BIỆT, PHẢI THỰC HIỆN ƯU TIÊN THEO THỨ TỰ GIỮA CÁC BỘ MÔN: KIẾN TRÚC → KẾT CẤU / BỘ MÔN KHÁC; HOẶC ƯU TIÊN TRONG CÙNG BỘ MÔN: CHI TIẾT → TỔNG THỂ
- CÁC SỐ LIỆU KÍCH THƯỚC PHẢI ĐƯỢC KIỂM TRA THỰC TẾ TẠI CÔNG TRÌNH, NẾU THẤY SỰ KHÁC BIỆT SƠ VỚI BẢN VẼ THI PHẢI BẢO CHỨNG ĐƠN VỊ THIẾT KẾ.

**HIỆU CHỈNH:**

| REV | NGÀY | NỘI DUNG |
|-----|------|----------|
|-----|------|----------|

**CHỦ ĐẦU TƯ:**

CÔNG TY TNHH ĐẦU TƯ

**PHÚ VIỆT TÍN**

ĐỊA CHỈ: LÔ 18-19 QUỐC LỘ 1A, XÃ DẦU GIẤY,  
TỈNH ĐỒNG NAI, VIỆT NAM

**CTHĐT**

ĐẶNG PHƯỚC BÌNH

**ĐƠN VỊ THIẾT KẾ:**

CÔNG TY CỔ PHẦN TƯ VẤN THIẾT KẾ

**BASE ARC**

ĐỊA CHỈ: 138 ĐIỆN BIÊN PHỦ, PHƯỜNG TÂN ĐỊNH,  
TP. HỒ CHÍ MINH, VIỆT NAM

**TỔNG GIÁM ĐỐC**

TRẦN ĐỨC AN

**CHỦ NHIỆM DỰ ÁN:**

KTS. NGUYỄN THÀNH THÁI

**CHỦ TRÌ THIẾT KẾ:**

KS. NGÔ TÙNG THÀNH

**THIẾT KẾ:**

KS. NGUYỄN MINH DUY BẰNG

**KIỂM TRA:**

KS. NGÔ TÙNG THÀNH

**DỰ ÁN:**

KHU DÂN CƯ A1-C1 (ĐÔ THỊ DẦU GIẤY)

ĐỊA ĐIỂM: XÃ DẦU GIẤY, TỈNH ĐỒNG NAI

**CÔNG TRÌNH:**

NHÀ Ở THƯƠNG MẠI LIÊN KẾ

**HẠNG MỤC:**

MẪU NHÀ T3\_2b

**TÊN BẢN VẼ:**

CHI TIẾT MÓNG-04

**MỤC ĐÍCH PHÁT HÀNH:**


|                                     |                          |
|-------------------------------------|--------------------------|
| <input type="checkbox"/>            | BẢN VẼ MỜI THẦU          |
| <input type="checkbox"/>            | THIẾT KẾ CƠ SỞ           |
| <input checked="" type="checkbox"/> | THIẾT KẾ BẢN VẼ THI CÔNG |
| <input type="checkbox"/>            | BẢN VẼ HOÀN CÔNG         |

|                |         |
|----------------|---------|
| HOÀN THÀNH     | 07/2025 |
| TỶ LỆ          | NTS     |
| SỐ HIỆU BẢN VẼ | KC-11   |

# PHẦN MÓNG PHƯƠNG ÁN 2


ÁP DỤNG CHO CÁC LÔ:

- LK4-1

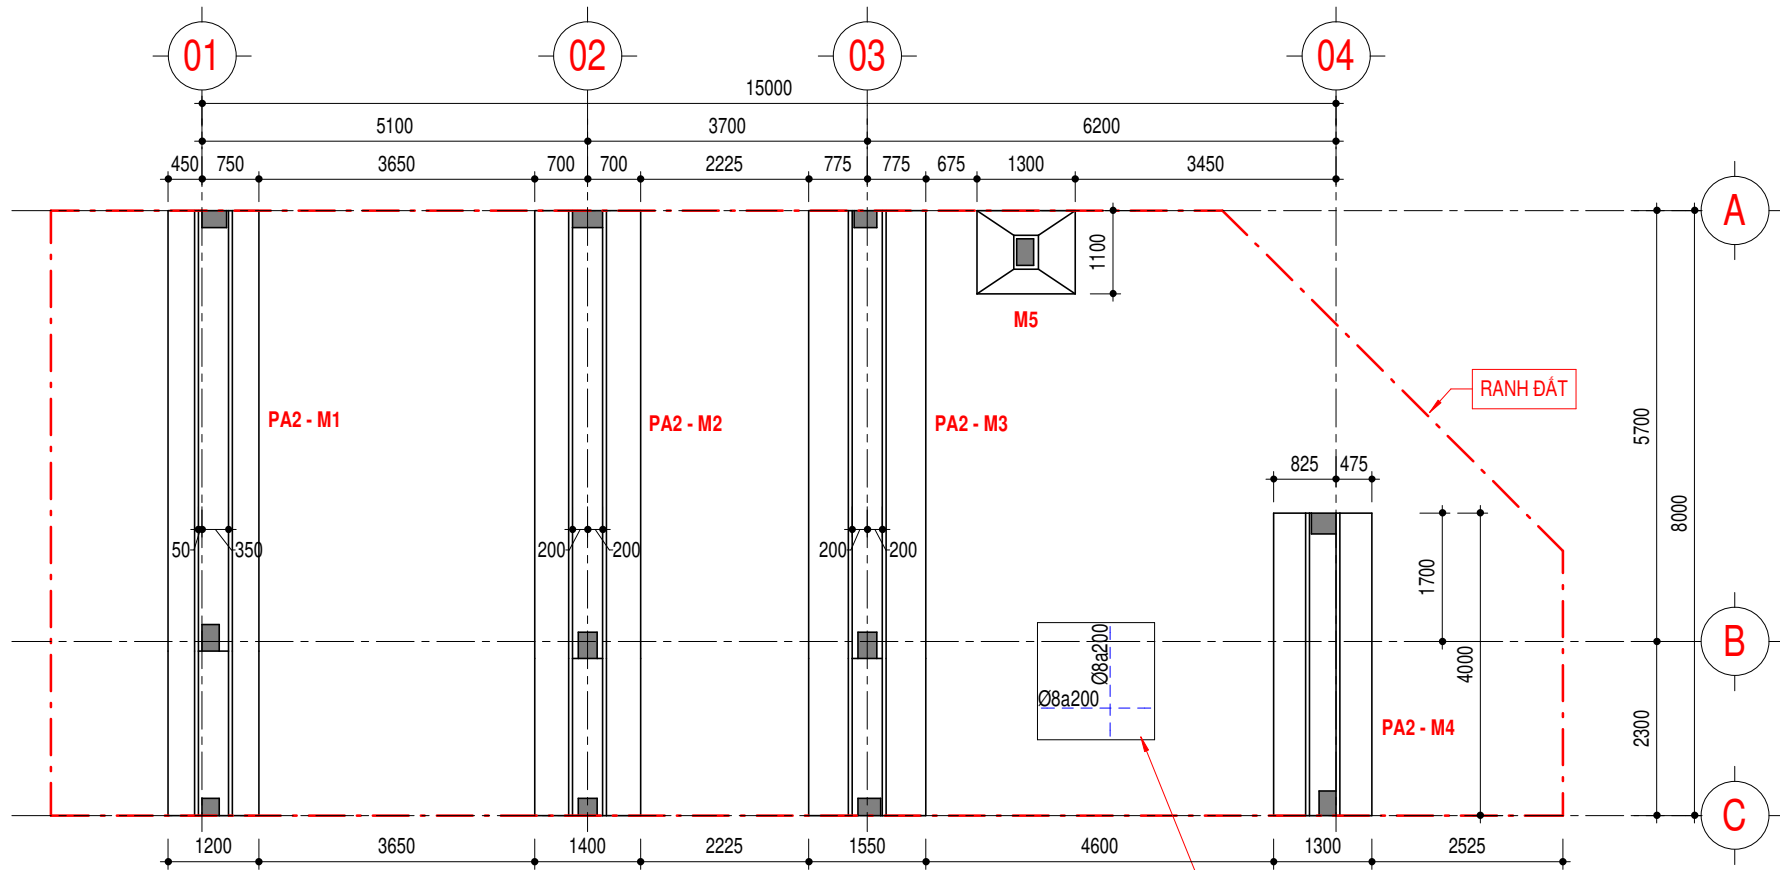

MẶT BẰNG BỐ TRÍ MÓNG

TL 1:100

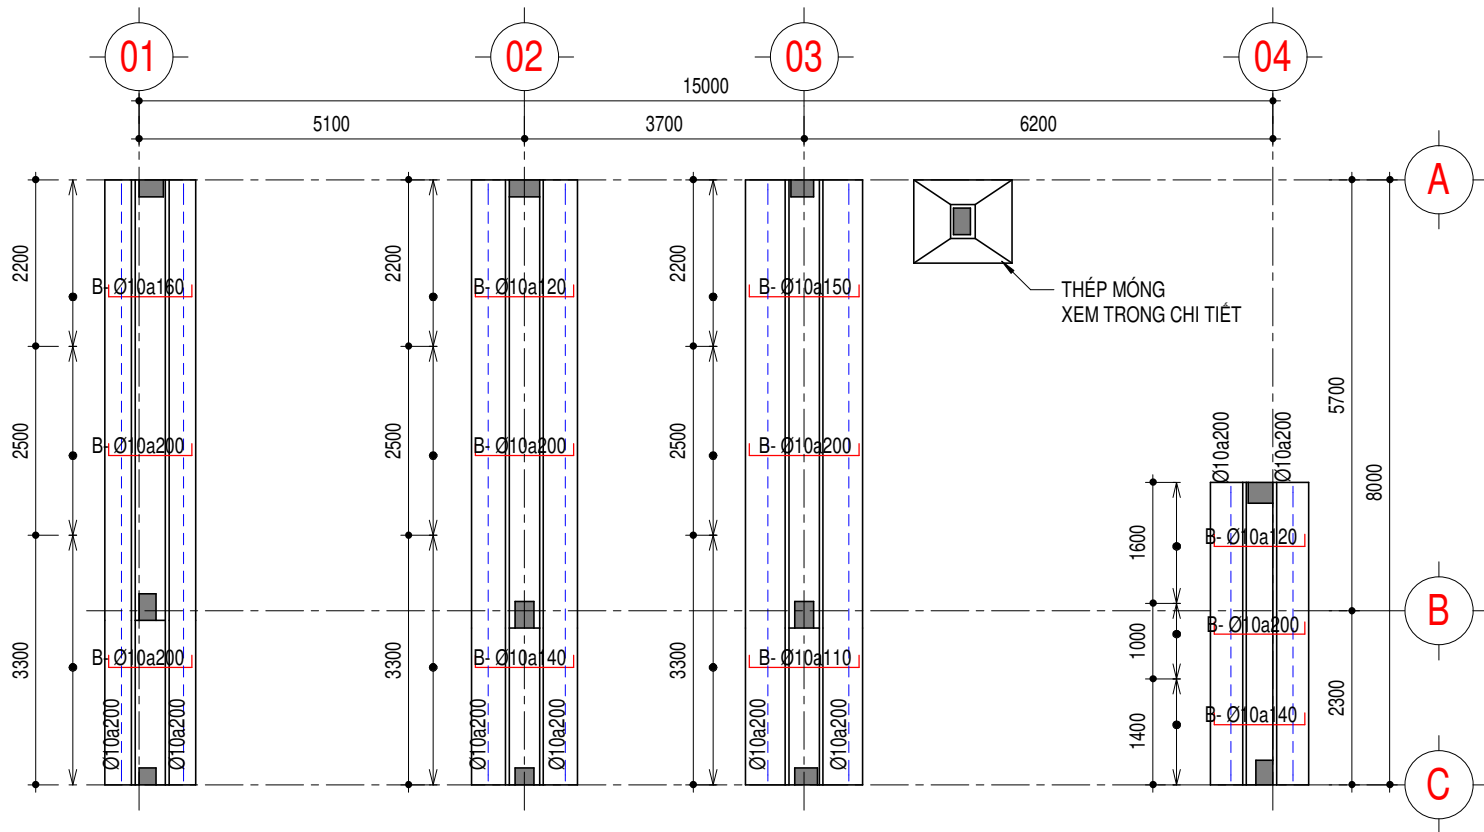

MẶT BẰNG BỐ TRÍ THÉP ĐÁY MÓNG

TL 1:100

| CAO ĐỘ HOÀN THIỆN KIẾN TRÚC |         |
|-----------------------------|---------|
| MẶT BẰNG                    | CAO ĐỘ  |
| ĐỈNH Mái                    | +11.000 |
| Mái                         | +10.000 |
| TẦNG 3                      | +6.800  |
| TẦNG 2                      | +3.600  |
| TẦNG 1                      | +0.000  |

|     | CAO ĐỘ (m) | CỘT ĐỊA TẦNG    | MÔ TẢ                              |
|-----|------------|-----------------|------------------------------------|
| LỚP | (±0.000)   | MĐTN            |                                    |
| 1   | (H)        | CAO ĐỘ ĐÁY MÓNG | Sét dẻo thấp, xám nâu đỏ, dẻo mềm  |
| L   |            |                 | Đá bazan                           |
| 1   |            |                 | Sét dẻo thấp, xám nâu đỏ, dẻo cứng |

GHI CHÚ:

- ĐÁY MÓNG PHẢI ĐƯỢC ĐẶT TRÊN LỚP ĐẤT TỰ NHIÊN HIỆN TRẠNG, HỆ SỐ ĐÁM CHẶT  $K = 0.9$ .
- NHÀ THẦU CẦN CÓ BIỆN PHÁP BƠM HÚT NƯỚC VÀ CHỒNG ĐỖ VÁCH HỒ ĐÀO ĐẢM BẢO AN TOÀN CHO CÁC CÔNG TRÌNH HIỆN HỮU.
- COTE ±0.000 LÀ CAO ĐỘ THIẾT KẾ KIẾN TRÚC, CAO ĐỘ QUỐC GIA XEM BẢN VẼ KIẾN TRÚC.
- TẤT CẢ CÁC KÍCH THƯỚC ĐƯỢC KIỂM TRA VÀ XÁC NHẬN TRÊN CÔNG TRƯỜNG.
- KÍCH THƯỚC VÀ VỊ TRÍ CÁC LỖ GEN, MƯƠNG, LAM TRANG TRÍ PHẢI ĐƯỢC KIỂM TRA SO VỚI CÁC BẢN VẼ KIẾN TRÚC, MEP CÓ LIÊN QUAN.
- CÁC VỊ TRÍ ỐNG XUYÊN DÀM XEM BẢN VẼ MEP. CHI TIẾT XUYÊN DÀM XEM BẢN VẼ GHI CHÚ CHUNG.
- KÍCH THƯỚC, CHIỀU SÂU ĐẶT TẦM ĐÀN BÊ TỰ HOẠI XEM BẢN VẼ MEP TRƯỚC KHI THI CÔNG. TẦM ĐÀN BÊ TỰ HOẠI SỬ DỤNG BÊ TÔNG CỐT THÉP ĐÁ 1x2, CẤP ĐỘ BÊ B15.
- CƯỜNG ĐỘ CHỊU TẢI ĐẤT NỀN:  $R_{dn} = 250 \text{ kN/m}^2$ .
- CAO ĐỘ ĐÁY MÓNG (H) VÀ VỊ TRÍ ÁP DỤNG CHO CÁC LỖ:
- LK4-1:  $H = -3.0\text{m}$  SO VỚI COTE ±0.000

GHI CHÚ:

- CÁC ĐƠN VỊ THI CÔNG PHẢI PHỐI HỢP BẢN VẼ CỦA TẤT CẢ CÁC BỘ MÔN KHÁC NẾU THẤY SỰ KHÁC BIỆT PHẢI BẢO CHO ĐƠN VỊ THIẾT KẾ XỬ LÝ.
- KHI XỬ LÝ SỰ KHÁC BIỆT, PHẢI THỰC HIỆN ƯU TIÊN THEO THỨ TỰ GIỮA CÁC BỘ MÔN: KIẾN TRÚC → KẾT CẤU / BỘ MÔN KHÁC; HOẶC ƯU TIÊN TRONG CÙNG BỘ MÔN: CHI TIẾT → TỔNG THỂ.
- CÁC SỐ LIEU KÍCH THƯỚC PHẢI ĐƯỢC KIỂM TRA THỰC TẾ TẠI CÔNG TRÌNH, NẾU THẤY SỰ KHÁC BIỆT SO VỚI BẢN VẼ THI PHẢI BẢO CHO ĐƠN VỊ THIẾT KẾ.

HIỆU CHỈNH:

| REV | NGÀY | NỘI DUNG |
|-----|------|----------|
|-----|------|----------|

CHỦ ĐẦU TƯ:

CÔNG TY TNHH ĐẦU TƯ

**PHÚ VIỆT TÍN**

ĐỊA CHỈ: LÔ 18-19 QUỐC LỘ 1A, XÃ DẦU GIẤY, TỈNH ĐỒNG NAI, VIỆT NAM

CTHĐT

ĐẠNG PHƯỚC BÌNH

ĐƠN VỊ THIẾT KẾ:

CÔNG TY CỔ PHẦN TƯ VẤN THIẾT KẾ

**BASE ARC**

ĐỊA CHỈ: 138 ĐIỆN BIÊN PHỦ, PHƯỜNG TÂN ĐỊNH, TP. HỒ CHÍ MINH, VIỆT NAM

TỔNG GIÁM ĐỐC

TRẦN ĐỨC AN

CHỦ NHIỆM DỰ ÁN:

KTS. NGUYỄN THÀNH THÁI

CHỦ TRÌ THIẾT KẾ:

KS. NGÔ TÙNG THÀNH

THIẾT KẾ:

KS. NGUYỄN MINH DUY BẰNG

KIỂM TRA:

KS. NGÔ TÙNG THÀNH

DỰ ÁN:

KHU DÂN CƯ A1-C1 (ĐÔ THỊ DẦU GIẤY)

ĐỊA ĐIỂM: XÃ DẦU GIẤY, TỈNH ĐỒNG NAI

CÔNG TRÌNH:

NHÀ Ở THƯƠNG MẠI LIÊN KẾ

HẠNG MỤC:


MẪU NHÀ T3\_2b

TÊN BẢN VẼ:

MẶT BẰNG BỐ TRÍ MÓNG, THÉP ĐÁY MÓNG


MỤC ĐÍCH PHÁT HÀNH:

|                            |         |
|----------------------------|---------|
| BẢN VẼ MỜI THẦU            |         |
| THIẾT KẾ CƠ SỞ             |         |
| ✓ THIẾT KẾ BẢN VẼ THI CÔNG |         |
| BẢN VẼ HOÀN CÔNG           |         |
| HOÀN THÀNH                 | 07/2025 |
| TỶ LỆ                      | NTS     |
| SỐ HIỆU BẢN VẼ             | KC-13   |

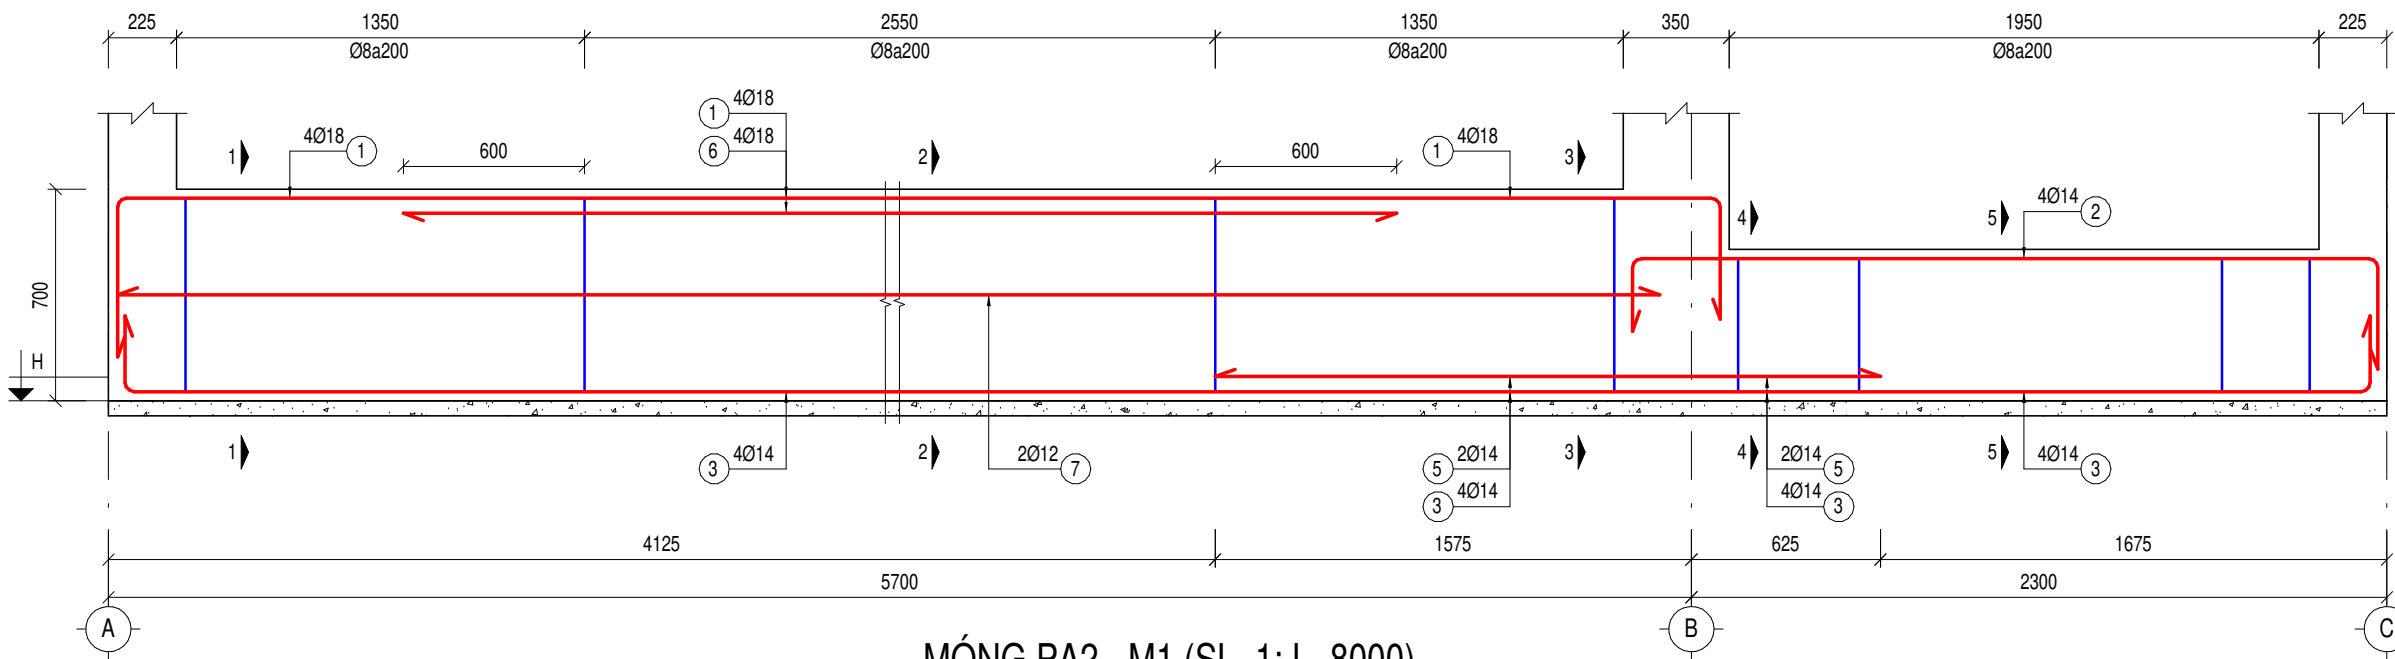


**MÓNG PA2 - M1 (SL=1; L=8000)**

TL: 1/25

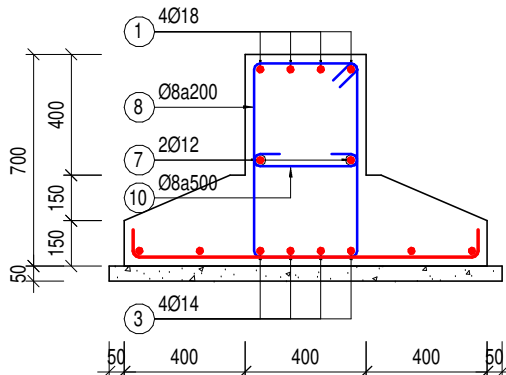


**MC 1-1**

PA2 - M1 (TL: 1/25)

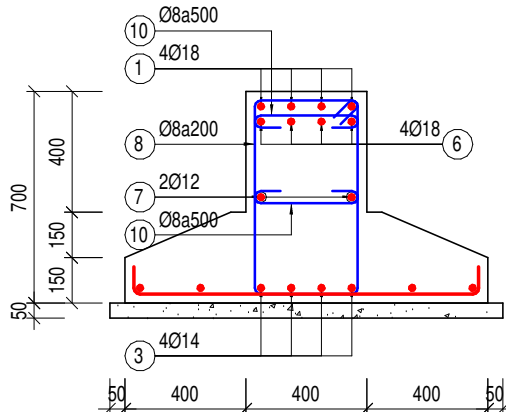


**MC 2-2**

PA2 - M1 (TL: 1/25)

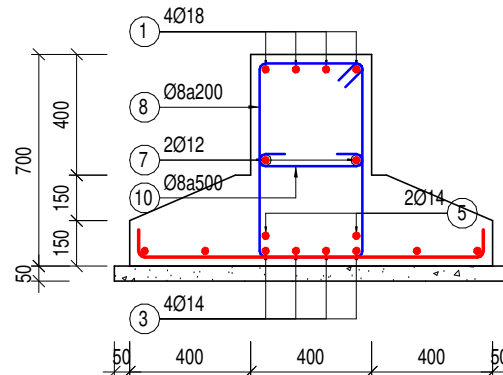


**MC 3-3**

PA2 - M1 (TL: 1/25)

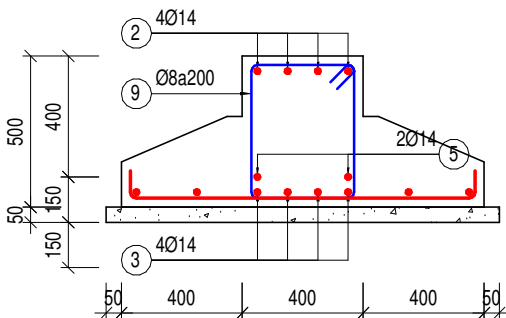

**MC 4-4**

PA2 - M1 (TL: 1/25)

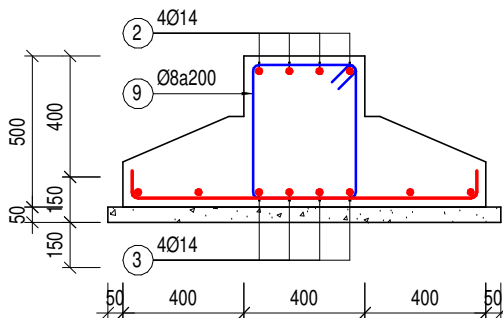

**MC 5-5**

PA2 - M1 (TL: 1/25)

**GHI CHÚ:**

- CÁC ĐƠN VỊ THI CÔNG PHẢI PHỐI HỢP BẢN VẼ CỦA TẤT CẢ CÁC BỘ MÔN KHÁC NẾU THẤY SỰ KHÁC BIỆT PHẢI BẢO CHO ĐƠN VỊ THIẾT KẾ XỬ LÝ.  
- KHI XỬ LÝ SỰ KHÁC BIỆT, PHẢI THỰC HIỆN ƯU TIÊN THEO THỨ TỰ GIỮA CÁC BỘ MÔN: KIẾN TRÚC → KẾT CẤU / BỘ MÔN KHÁC; HOẶC ƯU TIÊN TRONG CÙNG BỘ MÔN: CHI TIẾT → TỔNG THỂ.  
- CÁC SỐ LIỆU KÍCH THƯỚC PHẢI ĐƯỢC KIỂM TRA THỰC TẾ TẠI CÔNG TRÌNH, NẾU THẤY SỰ KHÁC BIỆT SƠ VỚI BẢN VẼ THI PHẢI BẢO CHO ĐƠN VỊ THIẾT KẾ.

**HIỆU CHỈNH:**

| REV | NGÀY | NỘI DUNG |
|-----|------|----------|
|-----|------|----------|

**CHỦ ĐẦU TƯ:**

CÔNG TY TNHH ĐẦU TƯ

**PHÚ VIỆT TÍN**

ĐỊA CHỈ: LÔ 18-19 QUỐC LỘ 1A, XÃ DẦU GIẤY,  
TỈNH ĐỒNG NAI, VIỆT NAM

**CTHĐT**

ĐẶNG PHƯỚC BÌNH

**ĐƠN VỊ THIẾT KẾ:**

CÔNG TY CỔ PHẦN TƯ VẤN THIẾT KẾ

**BASE ARC**

ĐỊA CHỈ: 138 ĐIỆN BIÊN PHỦ, PHƯỜNG TÂN ĐỊNH,  
TP. HỒ CHÍ MINH, VIỆT NAM

**TỔNG GIÁM ĐỐC**

TRẦN ĐỨC AN

**CHỦ NHIỆM DỰ ÁN:**

KTS. NGUYỄN THÀNH THÁI

**CHỦ TRÌ THIẾT KẾ:**

KS. NGÔ TÙNG THÀNH

**THIẾT KẾ:**

KS. NGUYỄN MINH DUY BẰNG

**KIỂM TRA:**

KS. NGÔ TÙNG THÀNH

**DỰ ÁN:**

KHU DÂN CƯ A1-C1 (ĐÔ THỊ DẦU GIẤY)

ĐỊA ĐIỂM: XÃ DẦU GIẤY, TỈNH ĐỒNG NAI

**CÔNG TRÌNH:**

NHÀ Ở THƯƠNG MẠI LIÊN KẾ

**HẠNG MỤC:**

MẪU NHÀ T3\_2b

**TÊN BẢN VẼ:**

CHI TIẾT MÓNG-01


**MỤC ĐÍCH PHÁT HÀNH:**

|                                     |                          |
|-------------------------------------|--------------------------|
| <input type="checkbox"/>            | BẢN VẼ MỜI THẦU          |
| <input type="checkbox"/>            | THIẾT KẾ CƠ SỞ           |
| <input checked="" type="checkbox"/> | THIẾT KẾ BẢN VẼ THI CÔNG |
| <input type="checkbox"/>            | BẢN VẼ HOÀN CÔNG         |

HOÀN THÀNH 07/2025


TỶ LỆ NTS

SỐ HIỆU BẢN VẼ KC-14

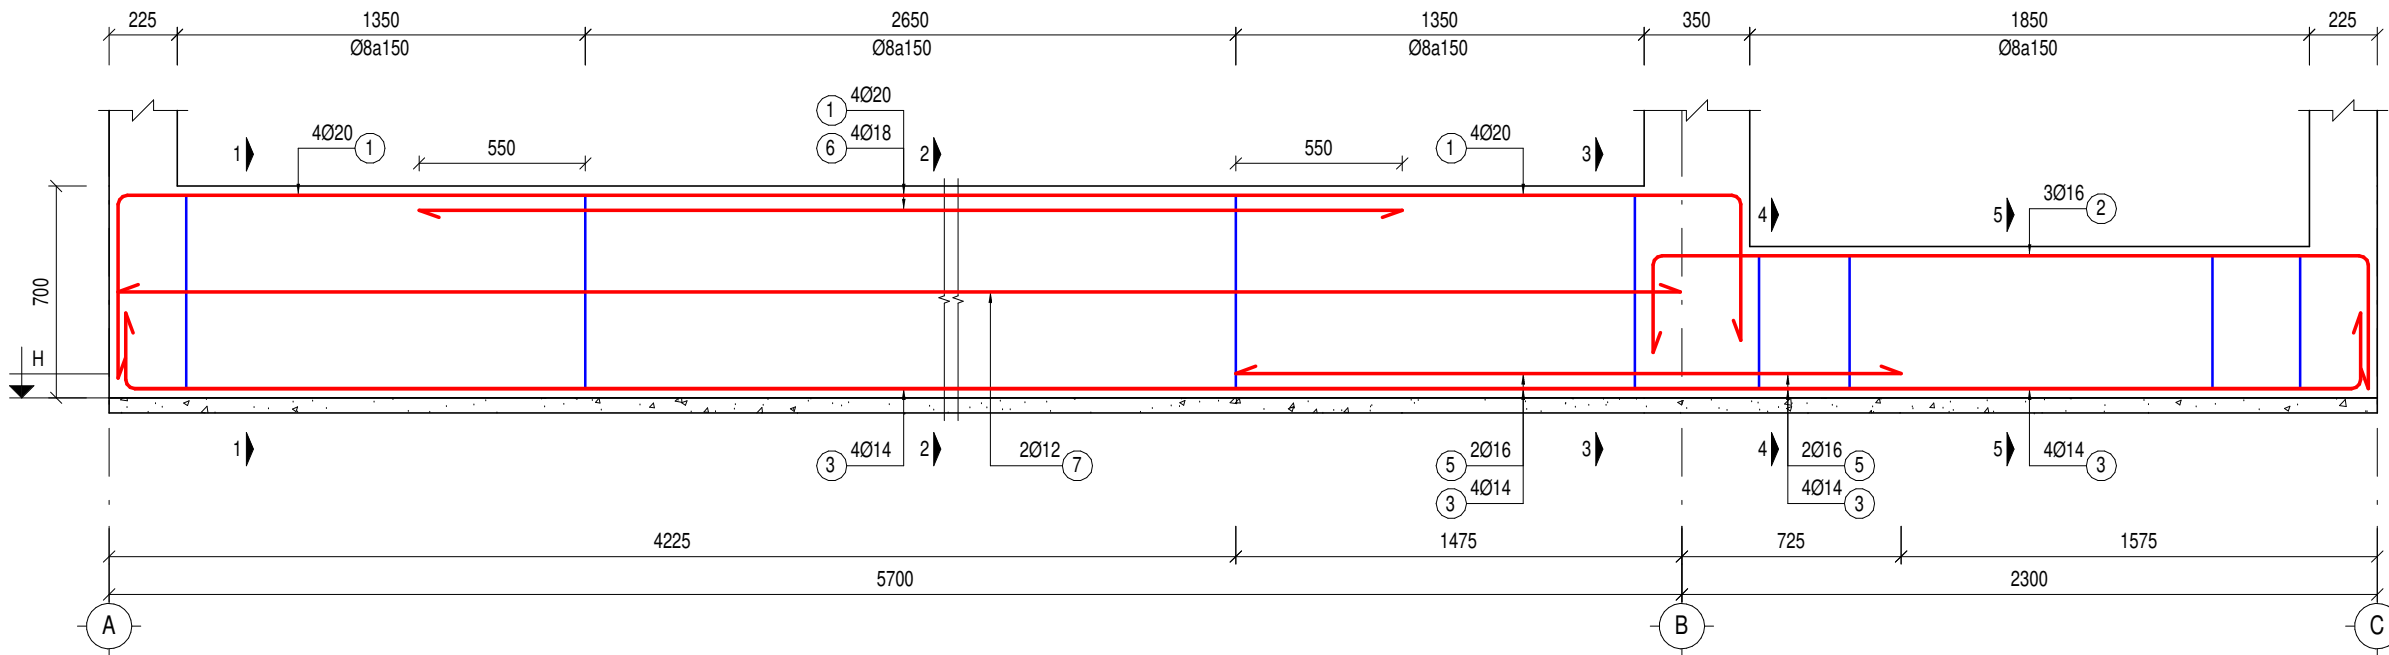


### MÓNG PA2 - M2 (SL=1; L=8000)


TL: 1/25

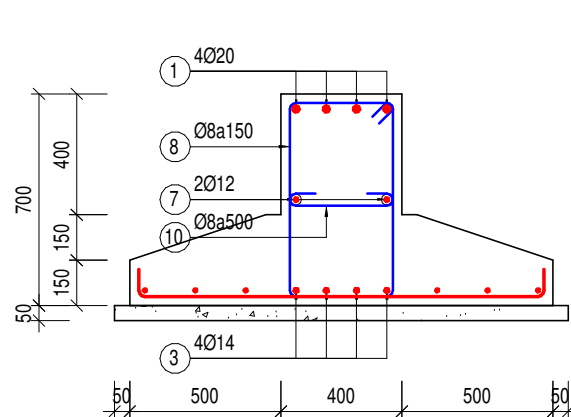


MC 1-1  
PA2 - M2 (TL: 1/25)

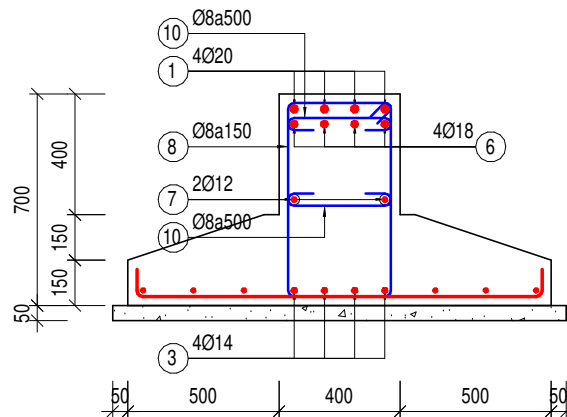


MC 2-2  
PA2 - M2 (TL: 1/25)

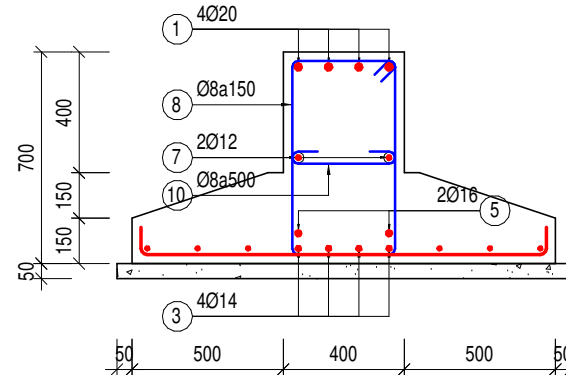

MC 3-3  
PA2 - M2 (TL: 1/25)

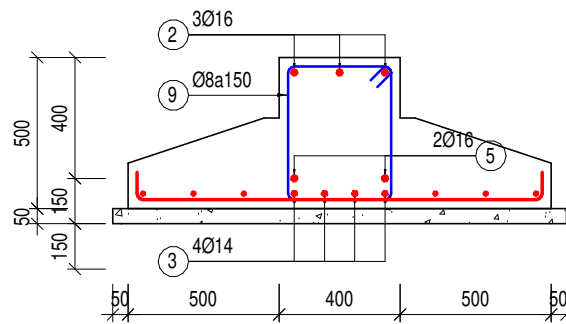

MC 4-4  
PA2 - M2 (TL: 1/25)

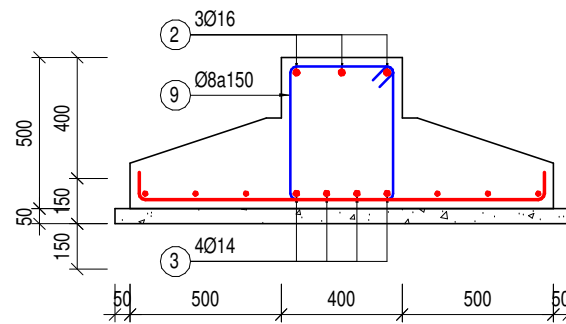

MC 5-5  
PA2 - M2 (TL: 1/25)

#### GHI CHÚ:

- CÁC ĐƠN VỊ THI CÔNG PHẢI HỢP BÀN VẼ CỦA TẤT CẢ CÁC BỘ MÔN KHÁC NẾU THẤY SỰ KHÁC BIỆT PHẢI BẢO CHO ĐƠN VỊ THIẾT KẾ ĐỂ XỬ LÝ.
- KHI XỬ LÝ SỰ KHÁC BIỆT, PHẢI THỰC HIỆN ƯU TIÊN THEO THỨ TỰ GIỮA CÁC BỘ MÔN: KIẾN TRÚC → KẾT CẤU / BỘ MÔN KHÁC; HOẶC ƯU TIÊN TRONG CÙNG BỘ MÔN: CHI TIẾT → TỔNG THỂ.
- CÁC SỐ LIỆU KÍCH THƯỚC PHẢI ĐƯỢC KIỂM TRA THỰC TẾ TẠI CÔNG TRÌNH, NẾU THẤY SỰ KHÁC BIỆT SƠ VỚI BẢN VẼ THI PHẢI BẢO CHO ĐƠN VỊ THIẾT KẾ.

#### HIỆU CHỈNH:

| REV | NGÀY | NỘI DUNG |
|-----|------|----------|
|-----|------|----------|

#### CHỦ ĐẦU TƯ:

CÔNG TY TNHH ĐẦU TƯ  
**PHÚ VIỆT TÍN**  
ĐỊA CHỈ: LÔ 18-19 QUỐC LỘ 1A, XÃ DẦU GIẤY,  
TỈNH ĐỒNG NAI, VIỆT NAM

#### CTHĐT

ĐẶNG PHƯỚC BÌNH

#### ĐƠN VỊ THIẾT KẾ:

CÔNG TY CỔ PHẦN TƯ VẤN THIẾT KẾ  
**BASE ARC**  
ĐỊA CHỈ: 138 ĐIỆN BIÊN PHỦ, PHƯỜNG TÂN ĐỊNH,  
TP. HỒ CHÍ MINH, VIỆT NAM

#### TỔNG GIÁM ĐỐC

TRẦN ĐỨC AN

#### CHỦ NHIỆM DỰ ÁN:

KTS. NGUYỄN THÀNH THÁI

#### CHỦ TRÌ THIẾT KẾ:

KS. NGÔ TÙNG THÀNH

#### THIẾT KẾ:

KS. NGUYỄN MINH DUY BẰNG

#### KIỂM TRA:

KS. NGÔ TÙNG THÀNH

#### DỰ ÁN:

KHU DÂN CƯ A1-C1 (ĐÔ THỊ DẦU GIẤY)  
ĐỊA ĐIỂM: XÃ DẦU GIẤY, TỈNH ĐỒNG NAI

#### CÔNG TRÌNH:

NHÀ Ở THƯƠNG MẠI LIÊN KẾ

#### HẠNG MỤC:

MẪU NHÀ T3\_2b


#### TÊN BẢN VẼ:

CHI TIẾT MÓNG-02

#### MỤC ĐÍCH PHÁT HÀNH:


|                                     |                          |
|-------------------------------------|--------------------------|
| <input type="checkbox"/>            | BẢN VẼ MỜI THẦU          |
| <input type="checkbox"/>            | THIẾT KẾ CƠ SỞ           |
| <input checked="" type="checkbox"/> | THIẾT KẾ BẢN VẼ THI CÔNG |
| <input type="checkbox"/>            | BẢN VẼ HOÀN CÔNG         |

|                |         |
|----------------|---------|
| HOÀN THÀNH     | 07/2025 |
| TỶ LỆ          | NTS     |
| SỐ HIỆU BẢN VẼ | KC-15   |

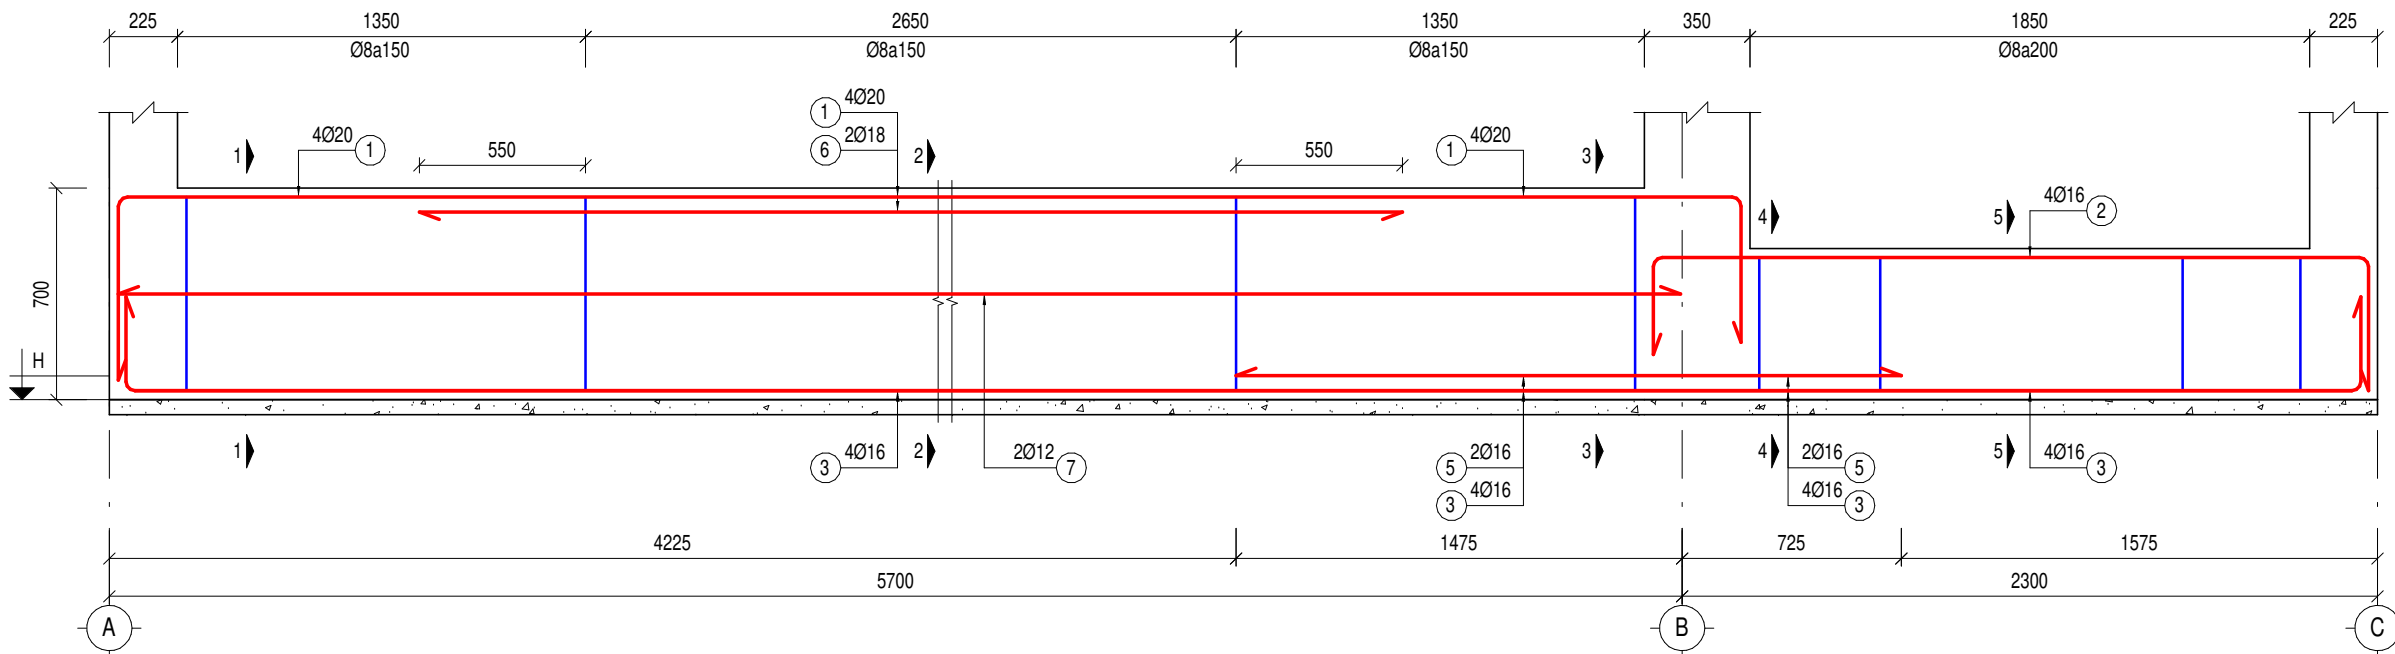


### MÓNG PA2 - M3 (SL=1; L=8000)

TL: 1/25

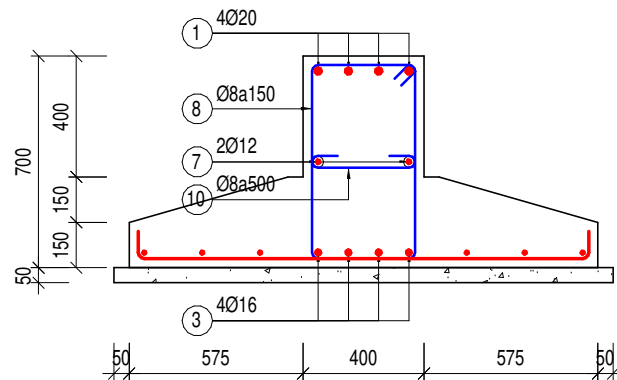


#### MC 1-1

PA2 - M3 (TL: 1/25)

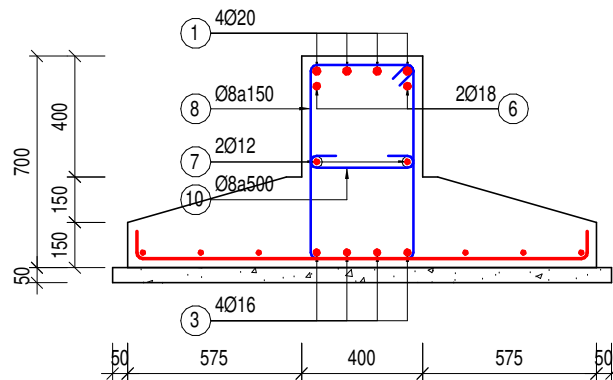


#### MC 2-2

PA2 - M3 (TL: 1/25)

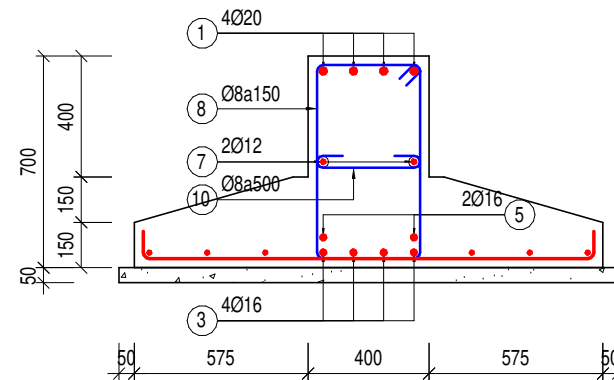


#### MC 3-3

PA2 - M3 (TL: 1/25)

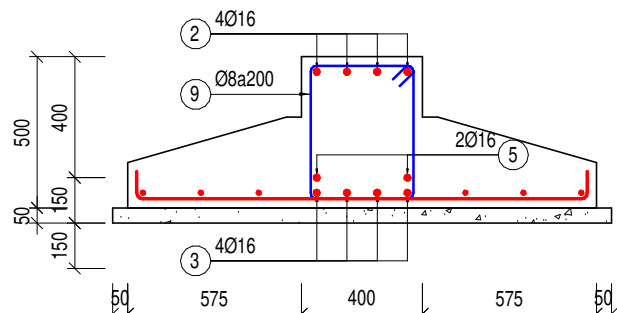

#### MC 4-4

PA2 - M3 (TL: 1/25)

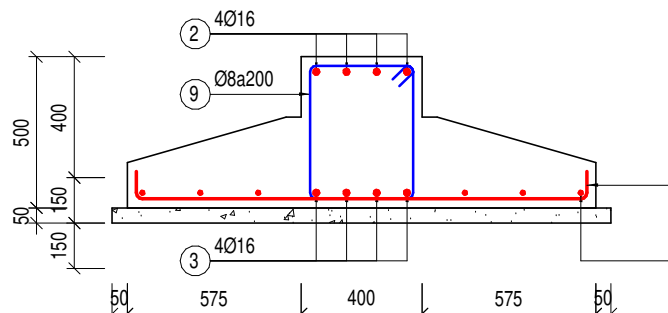

#### MC 5-5

PA2 - M3 (TL: 1/25)

#### GHI CHÚ:

- CÁC ĐƠN VỊ THI CÔNG PHẢI PHỐI HỢP BẢN VẼ CỦA TẤT CẢ CÁC BỘ MÔN KHÁC NẾU THẤY SỰ KHÁC BIỆT PHẢI BẢO CHỨ ĐƠN VỊ THIẾT KẾ ĐỂ XỬ LÝ.
- KHI XỬ LÝ SỰ KHÁC BIỆT, PHẢI THỰC HIỆN ƯU TIÊN THEO THỨ TỰ GIỮA CÁC BỘ MÔN: KIẾN TRÚC → KẾT CẤU / BỘ MÔN KHÁC; HOẶC ƯU TIÊN TRONG CÙNG BỘ MÔN: CHI TIẾT → TỔNG THỂ
- CÁC SỐ LIỆU KỊCH THUỘC PHẢI ĐƯỢC KIỂM TRA THỰC TẾ TẠI CÔNG TRÌNH, NẾU THẤY SỰ KHÁC BIỆT SƠ VỚI BẢN VẼ THI PHẢI BẢO CHỨ ĐƠN VỊ THIẾT KẾ.

#### HIỆU CHỈNH:

| REV | NGÀY | NỘI DUNG |
|-----|------|----------|
|-----|------|----------|

#### CHỦ ĐẦU TƯ:

CÔNG TY TNHH ĐẦU TƯ

**PHÚ VIỆT TÍN**

ĐỊA CHỈ: LÔ 18-19 QUỐC LỘ 1A, XÃ DẦU GIẤY,  
TỈNH ĐỒNG NAI, VIỆT NAM

CTHĐT

ĐẶNG PHƯỚC BÌNH

#### ĐƠN VỊ THIẾT KẾ:

CÔNG TY CỔ PHẦN TƯ VẤN THIẾT KẾ

**BASE ARC**

ĐỊA CHỈ: 138 ĐIỆN BIÊN PHỦ, PHƯỜNG TÂN ĐỊNH,  
TP. HỒ CHÍ MINH, VIỆT NAM

#### TỔNG GIÁM ĐỐC

TRẦN ĐỨC AN

#### CHỦ NHIỆM DỰ ÁN:

KTS. NGUYỄN THÀNH THÁI

#### CHỦ TRÌ THIẾT KẾ:

KS. NGÔ TÙNG THÀNH

#### THIẾT KẾ:

KS. NGUYỄN MINH DUY BẰNG

#### KIỂM TRA:

KS. NGÔ TÙNG THÀNH

#### DỰ ÁN:

KHU DÂN CƯ A1-C1 (ĐÔ THỊ DẦU GIẤY)

ĐỊA ĐIỂM: XÃ DẦU GIẤY, TỈNH ĐỒNG NAI

#### CÔNG TRÌNH:

NHÀ Ở THƯƠNG MẠI LIÊN KẾ

#### HẠNG MỤC:

MẪU NHÀ T3\_2b

#### TÊN BẢN VẼ:

CHI TIẾT MÓNG-03

#### MỤC ĐÍCH PHÁT HÀNH:

|                                     |                          |
|-------------------------------------|--------------------------|
| <input type="checkbox"/>            | BẢN VẼ MỜI THẦU          |
| <input type="checkbox"/>            | THIẾT KẾ CƠ SỞ           |
| <input checked="" type="checkbox"/> | THIẾT KẾ BẢN VẼ THI CÔNG |
| <input type="checkbox"/>            | BẢN VẼ HOÀN CÔNG         |

HOÀN THÀNH


07/2025

TỶ LỆ

NTS


SỐ HIỆU BẢN VẼ

KC-16

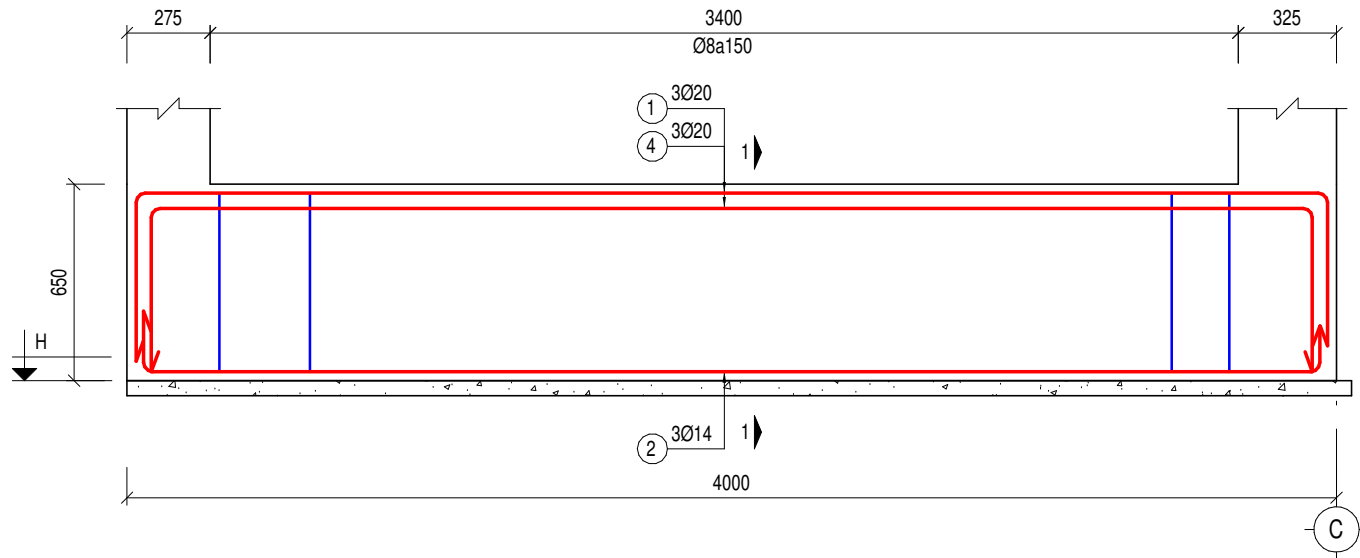


**MÓNG PA2 - M4 (SL=1; L=4000)**

TL: 1/25

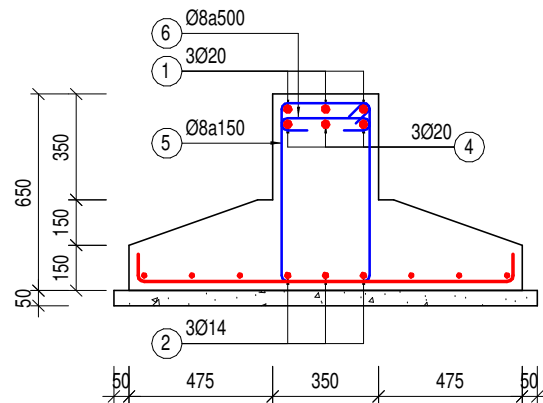


**MÓNG PA2 - M4 (SL=1; L=4000)**

MC 1-1 (TỶ LỆ: 1/25)

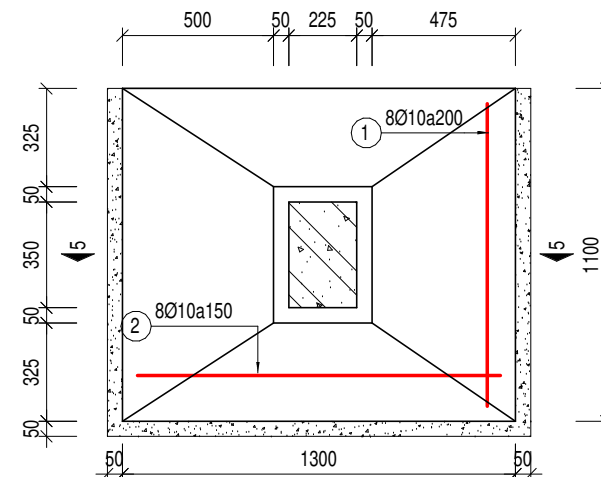

**MÓNG M5 (SL=1)**

TL: 1/25

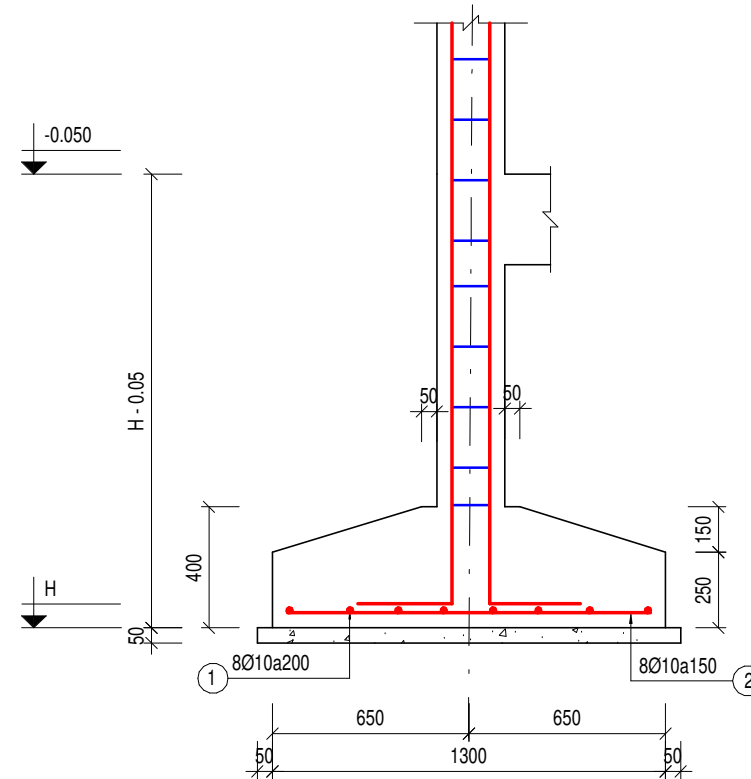

**MC 5-5**

TL: 1/25

**GHI CHÚ:**

- CÁC ĐƠN VỊ THI CÔNG PHẢI PHỐI HỢP BẢN VẼ CỦA TẤT CẢ CÁC BỘ MÔN KHÁC NẾU THẤY SỰ KHÁC BIỆT PHẢI BÁO CHO ĐƠN VỊ THIẾT KẾ ĐỂ XỬ LÝ.
- KHI XỬ LÝ SỰ KHÁC BIỆT, PHẢI THỰC HIỆN ƯU TIÊN THEO THỨ TỰ GIỮA CÁC BỘ MÔN: KIẾN TRÚC → KẾT CẤU / BỘ MÔN KHÁC; HOẶC ƯU TIÊN TRONG CÙNG BỘ MÔN: CHI TIẾT → TỔNG THỂ
- CÁC SỐ LIỆU KÍCH THƯỚC PHẢI ĐƯỢC KIỂM TRA THỰC TẾ TẠI CÔNG TRÌNH, NẾU THẤY KHÁC BIỆT SƠ VỚI BẢN VẼ THI PHẢI BÁO CHO ĐƠN VỊ THIẾT KẾ.

**HIỆU CHỈNH:**

| REV | NGÀY | NỘI DUNG |
|-----|------|----------|
|-----|------|----------|

**CHỦ ĐẦU TƯ:**

CÔNG TY TNHH ĐẦU TƯ

**PHÚ VIỆT TÍN**

ĐỊA CHỈ: LÔ 18-19 QUỐC LỘ 1A, XÃ DẦU GIẤY,  
TỈNH ĐỒNG NAI, VIỆT NAM

CTHĐT

ĐẶNG PHƯỚC BÌNH

**ĐƠN VỊ THIẾT KẾ:**

CÔNG TY CỔ PHẦN TƯ VẤN THIẾT KẾ

**BASE ARC**

ĐỊA CHỈ: 138 ĐIỆN BIÊN PHỦ, PHƯỜNG TÂN ĐỊNH,  
TP. HỒ CHÍ MINH, VIỆT NAM

**TỔNG GIÁM ĐỐC**

TRẦN ĐỨC AN

**CHỦ NHIỆM DỰ ÁN:**

KTS. NGUYỄN THÀNH THÁI

**CHỦ TRÌ THIẾT KẾ:**

KS. NGÔ TÙNG THÀNH

**THIẾT KẾ:**

KS. NGUYỄN MINH DUY BẰNG

**KIỂM TRA:**

KS. NGÔ TÙNG THÀNH

**DỰ ÁN:**

KHU DÂN CƯ A1-C1 (ĐÔ THỊ DẦU GIẤY)

ĐỊA ĐIỂM: XÃ DẦU GIẤY, TỈNH ĐỒNG NAI

**CÔNG TRÌNH:**

NHÀ Ở THƯƠNG MẠI LIÊN KẾ

**HẠNG MỤC:**

MẪU NHÀ T3\_2b

**TÊN BẢN VẼ:**

CHI TIẾT MÓNG-04

**MỤC ĐÍCH PHÁT HÀNH:**

|                                     |                          |
|-------------------------------------|--------------------------|
| <input type="checkbox"/>            | BẢN VẼ MỜI THẦU          |
| <input type="checkbox"/>            | THIẾT KẾ CƠ SỞ           |
| <input checked="" type="checkbox"/> | THIẾT KẾ BẢN VẼ THI CÔNG |
| <input type="checkbox"/>            | BẢN VẼ HOÀN CÔNG         |

HOÀN THÀNH 07/2025

TỶ LỆ NTS

SỐ HIỆU BẢN VẼ KC-17

# PHẦN KHUNG

ÁP DỤNG CHUNG CHO TOÀN BỘ  
CÁC LÔ THUỘC MẪU T3\_2b




| CAO ĐỘ HOÀN THIỆN KIẾN TRÚC |         |
|-----------------------------|---------|
| MẶT BẰNG                    | CAO ĐỘ  |
| ĐÌNH MÃI                    | +11.000 |
| MÃI                         | +10.000 |
| TẦNG 3                      | +6.800  |
| TẦNG 2                      | +3.600  |
| TẦNG 1                      | +0.000  |

**GHI CHÚ:**

1. TẤT CẢ CÁC KÍCH THƯỚC ĐƯỢC KIỂM TRA VÀ XÁC NHẬN TRÊN CÔNG TRƯỜNG
2. KÍCH THƯỚC VÀ VỊ TRÍ CÁC LỖ GEN, MƯƠNG, LAM TRĂNG TRÍ PHẢI ĐƯỢC KIỂM TRA SO VỚI CÁC BẢN VẼ KIẾN TRÚC, MEP CÓ LIÊN QUAN.
3. CÁC VỊ TRÍ ỜNG XUYÊN DÂM XEM BẢN VẼ MEP.


CHI TIẾT XUYÊN DÂM XEM BẢN VẼ GHI CHÚ CHUNG

[illegible]

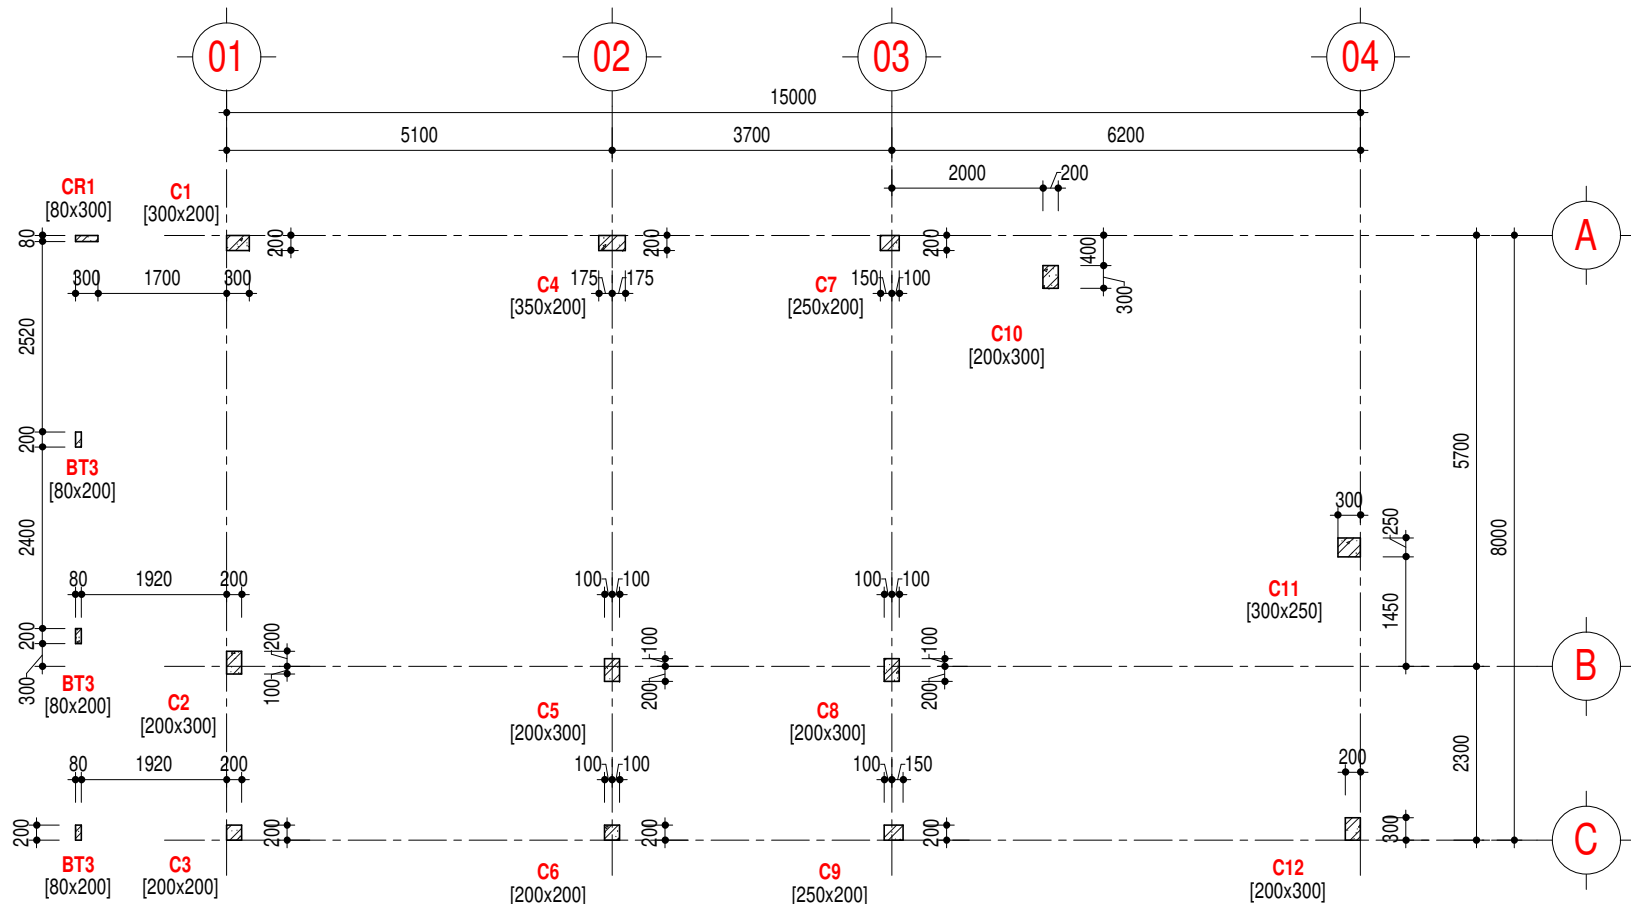

### MẶT BẰNG CỘT TẦNG 1

TL 1 : 100

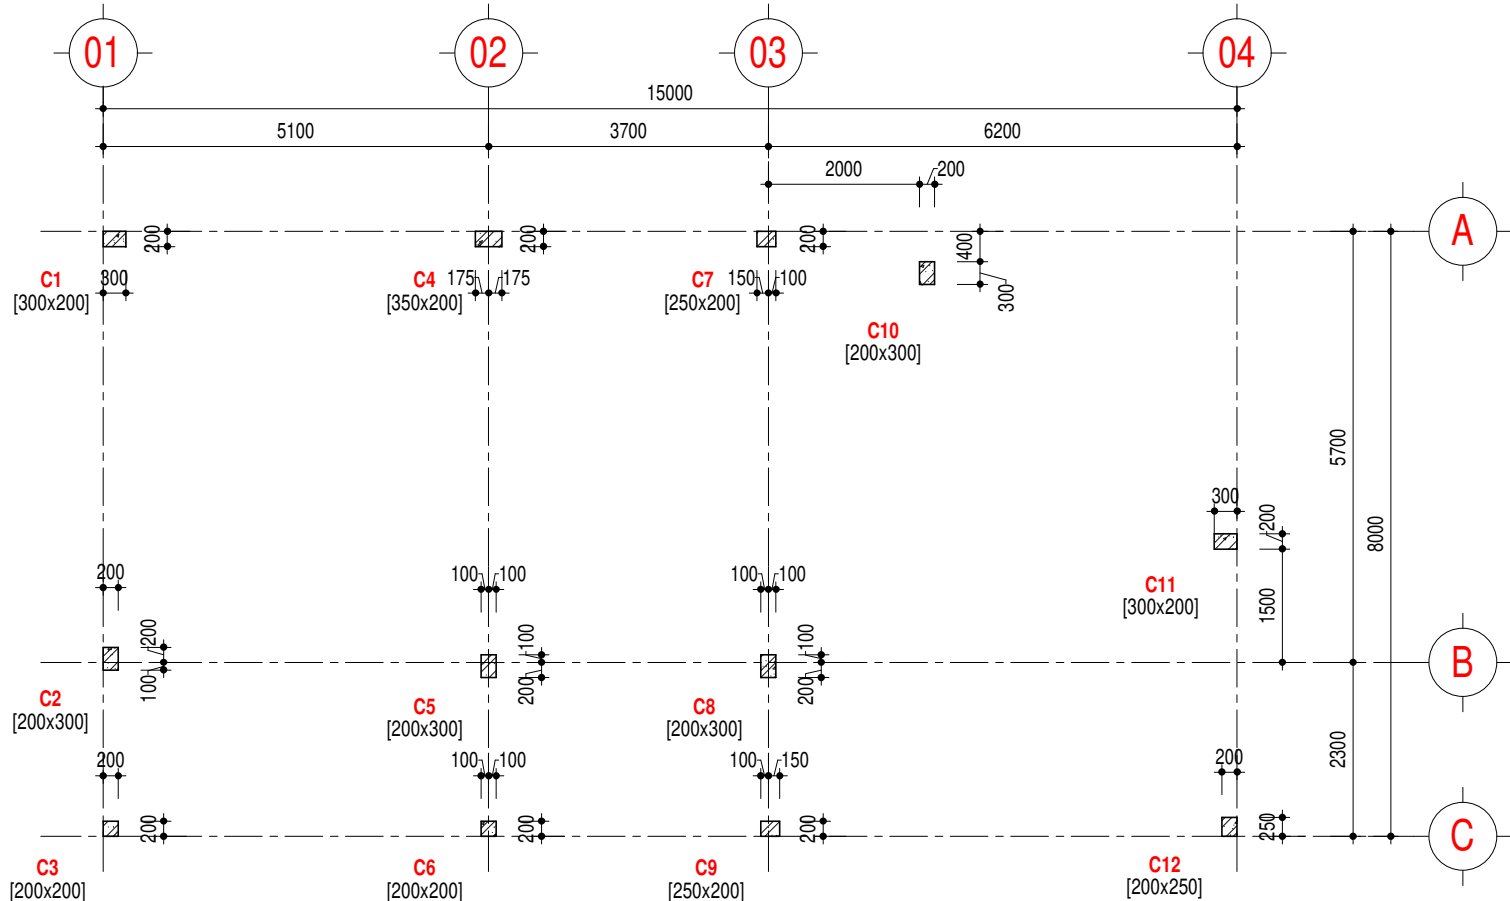

### MẶT BẰNG CỘT TẦNG 2

TL 1 : 100

| CAO ĐỘ HOÀN THIỆN KIẾN TRÚC |         |
|-----------------------------|---------|
| MẶT BẰNG                    | CAO ĐỘ  |
| ĐỈNH MÁI                    | +11.000 |
| MÁI                         | +10.000 |
| TẦNG 3                      | +6.800  |
| TẦNG 2                      | +3.600  |
| TẦNG 1                      | +0.000  |

#### GHI CHÚ:

- TẤT CẢ CÁC KÍCH THƯỚC ĐƯỢC KIỂM TRA VÀ XÁC NHẬN TRÊN CÔNG TRƯỜNG
- KÍCH THƯỚC VÀ VỊ TRÍ CÁC LỖ GEN, MƯƠNG, LAM TRANG TRÍ PHẢI ĐƯỢC KIỂM TRA SÓ VỚI CÁC BẢN VẼ KIẾN TRÚC, MEP CÓ LIÊN QUAN.
- CÁC VỊ TRÍ ỜNG XUYẾN DẪM XEM BẢN VẼ MEP.
- CHI TIẾT XUYẾN DẪM XEM BẢN VẼ GHI CHÚ CHUNG

#### THÔNG KÊ CỘT - TẦNG 1

| CẤU KIỆN | SỐ LƯỢNG |
|----------|----------|
| BT3      | 3        |
| C1       | 1        |
| C2       | 1        |
| C3       | 1        |
| C4       | 1        |
| C5       | 1        |
| C6       | 1        |
| C7       | 1        |
| C8       | 1        |
| C9       | 1        |
| C10      | 1        |
| C11      | 1        |
| C12      | 1        |
| CR1      | 1        |

#### THÔNG KÊ CỘT - TẦNG 2

| CẤU KIỆN | SỐ LƯỢNG |
|----------|----------|
| C1       | 1        |
| C2       | 1        |
| C3       | 1        |
| C4       | 1        |
| C5       | 1        |
| C6       | 1        |
| C7       | 1        |
| C8       | 1        |
| C9       | 1        |
| C10      | 1        |
| C11      | 1        |
| C12      | 1        |

#### GHI CHÚ:

- CÁC ĐƠN VỊ THI CÔNG PHẢI PHỐI HỢP BẢN VẼ CỦA TẤT CẢ CÁC BỘ MÔN KHÁC NẾU THẤY SỰ KHÁC BIỆT PHẢI BẢO CHO ĐƠN VỊ THIẾT KẾ ĐỂ XỬ LÝ.
- KHI XỬ LÝ SỰ KHÁC BIỆT, PHẢI THỰC HIỆN ƯU TIÊN THEO THỨ TỰ GIỮA CÁC BỘ MÔN: KIẾN TRÚC → KẾT CẤU / BỘ MÔN KHÁC; HOẶC ƯU TIÊN TRONG CÙNG BỘ MÔN: CHI TIẾT → TỔNG THỂ
- CÁC SỐ LIEU KÍCH THƯỚC PHẢI ĐƯỢC KIỂM TRA THỰC TẾ TẠI CÔNG TRÌNH, NẾU THẤY SỰ KHÁC BIỆT SÓ VỚI BẢN VẼ THI PHẢI BẢO CHO ĐƠN VỊ THIẾT KẾ.

#### HIỆU CHỈNH:

| REV | NGÀY | NỘI DUNG |
|-----|------|----------|
|-----|------|----------|

#### CHỦ ĐẦU TƯ:

CÔNG TY TNHH ĐẦU TƯ

**PHÚ VIỆT TÍN**

ĐỊA CHỈ: LÔ 18-19 QUỐC LỘ 1A, XÃ DẦU GIẤY, TỈNH ĐỒNG NAI, VIỆT NAM

#### CTHĐT

ĐẶNG PHƯỚC BÌNH

#### ĐƠN VỊ THIẾT KẾ:

CÔNG TY CỔ PHẦN TƯ VẤN THIẾT KẾ

**BASE ARC**

ĐỊA CHỈ: 138 ĐIỆN BIÊN PHỦ, PHƯỜNG TÂN ĐỊNH, TP. HỒ CHÍ MINH, VIỆT NAM

#### TỔNG GIÁM ĐỐC

TRẦN ĐỨC AN

#### CHỦ NHIỆM DỰ ÁN:

KTS. NGUYỄN THÀNH THÁI

#### CHỦ TRÌ THIẾT KẾ:

KS. NGÔ TÙNG THÀNH

#### THIẾT KẾ:

KS. NGUYỄN MINH DUY BẰNG

#### KIỂM TRA:

KS. NGÔ TÙNG THÀNH

#### DỰ ÁN:

KHU DÂN CƯ A1-C1 (ĐÔ THỊ DẦU GIẤY)

ĐỊA ĐIỂM: XÃ DẦU GIẤY, TỈNH ĐỒNG NAI

#### CÔNG TRÌNH:

NHÀ Ở THƯƠNG MẠI LIÊN KẾ

#### HẠNG MỤC:


MẪU NHÀ T3\_2b

#### TÊN BẢN VẼ:

MẶT BẰNG CỘT TẦNG 1, 2


#### MỤC ĐÍCH PHÁT HÀNH:

|                                                              |         |
|--------------------------------------------------------------|---------|
| BẢN VẼ MỜI THẦU                                              |         |
| THIẾT KẾ CƠ SỞ                                               |         |
| <input checked="" type="checkbox"/> THIẾT KẾ BẢN VẼ THI CÔNG |         |
| BẢN VẼ HOÀN CÔNG                                             |         |
| HOÀN THÀNH                                                   | 07/2025 |
| TỶ LỆ                                                        | NTS     |
| SỐ HIỆU BẢN VẼ                                               | KC-20   |

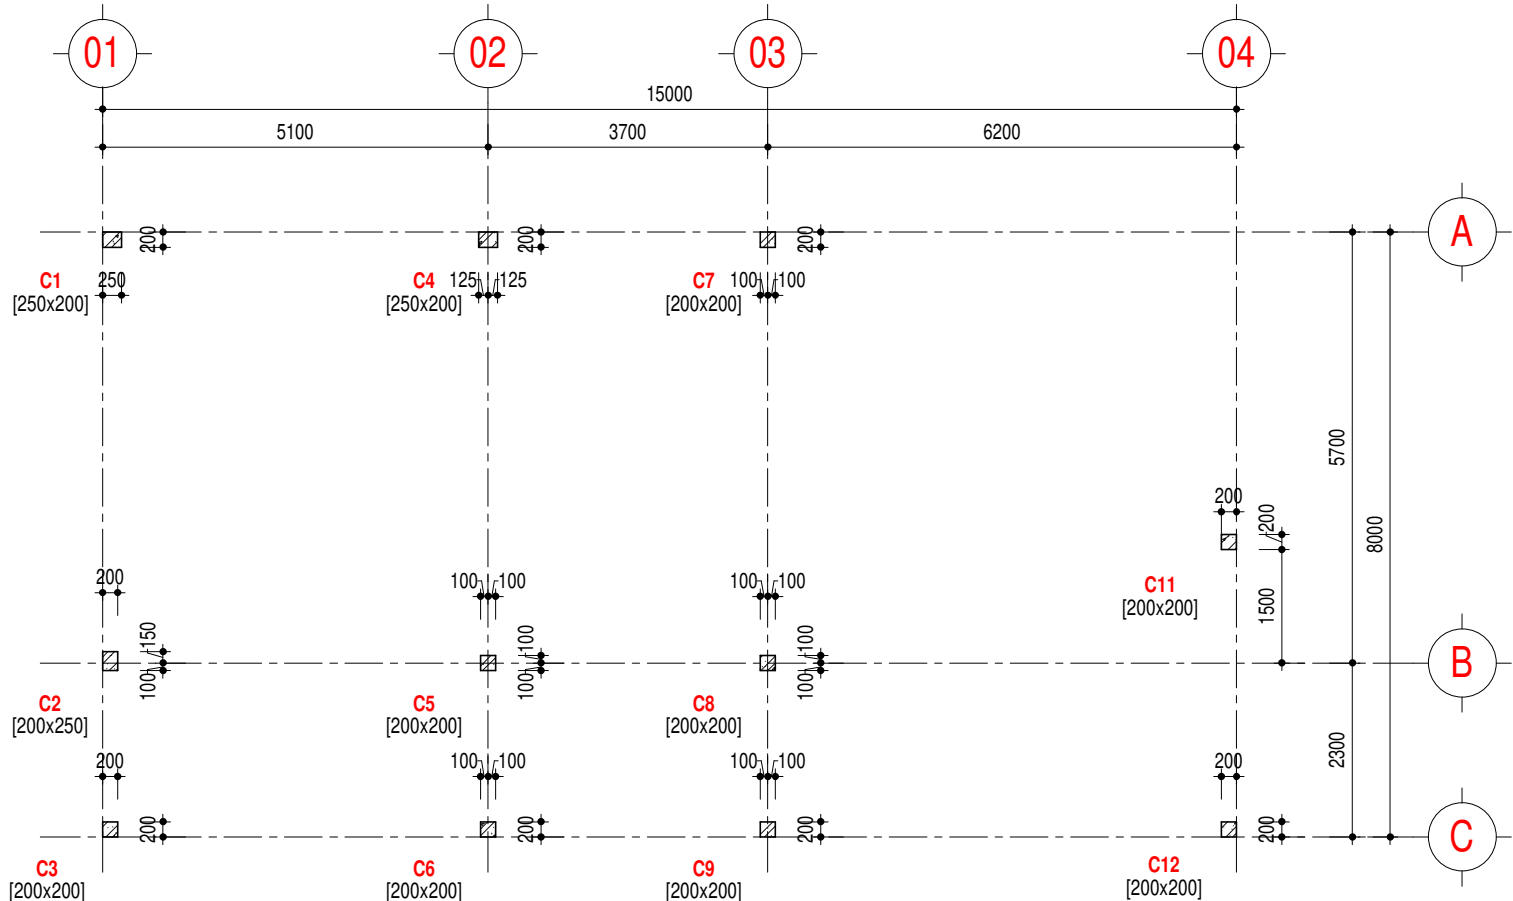

### MẶT BẰNG CỘT TẦNG 3

TL 1 : 100

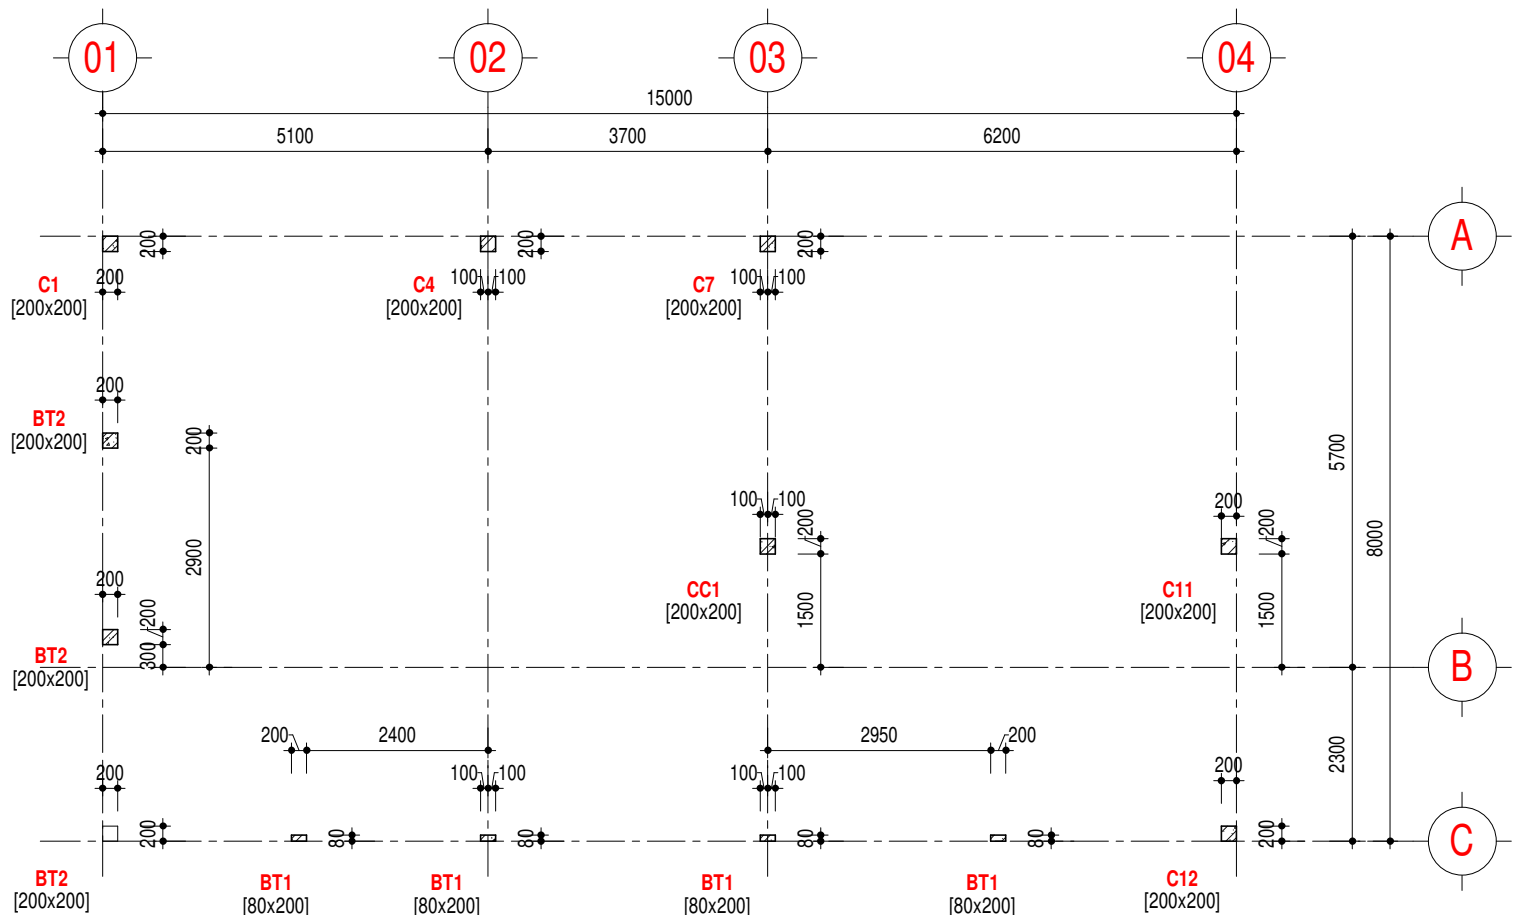

### MẶT BẰNG CỘT MÁI

TL 1 : 100

| THÔNG KÊ CỘT - MÁI |          |
|--------------------|----------|
| CẤU KIỆN           | SỐ LƯỢNG |
| BT1                | 4        |
| BT2                | 3        |
| C1                 | 1        |
| C4                 | 1        |
| C7                 | 1        |
| C11                | 1        |
| C12                | 1        |
| CC1                | 1        |

| THÔNG KÊ CỘT - TẦNG 3 |          |
|-----------------------|----------|
| CẤU KIỆN              | SỐ LƯỢNG |
| C1                    | 1        |
| C2                    | 1        |
| C3                    | 1        |
| C4                    | 1        |
| C5                    | 1        |
| C6                    | 1        |
| C7                    | 1        |
| C8                    | 1        |
| C9                    | 1        |
| C11                   | 1        |
| C12                   | 1        |

| CAO ĐỘ HOÀN THIÊN KIẾN TRÚC |         |
|-----------------------------|---------|
| MẶT BẰNG                    | CAO ĐỘ  |
| ĐÌNH MÁI                    | +11.000 |
| MÁI                         | +10.000 |
| TẦNG 3                      | +6.800  |
| TẦNG 2                      | +3.600  |
| TẦNG 1                      | +0.000  |

#### GHI CHÚ:

- TẤT CẢ CÁC KÍCH THƯỚC ĐƯỢC KIỂM TRA VÀ XÁC NHẬN TRÊN CÔNG TRƯỜNG
- KÍCH THƯỚC VÀ VỊ TRÍ CÁC LỖ GEN, MƯƠNG, LAM TRANG TRÍ PHẢI ĐƯỢC KIỂM TRA SÓ VỚI CÁC BẢN VẼ KIẾN TRÚC, MEP CÓ LIÊN QUAN.
- CÁC VỊ TRÍ ÔNG XUYẾN DÀM XEM BẢN VẼ MEP.
- CHI TIẾT XUYẾN DÀM XEM BẢN VẼ GHI CHÚ CHUNG

#### GHI CHÚ:

- CÁC ĐƠN VỊ THI CÔNG PHẢI PHỐI HỢP BẢN VẼ CỦA TẤT CẢ CÁC BỘ MÔN KHÁC NẾU THẤY SỰ KHÁC BIỆT PHẢI BẢO CHO ĐƠN VỊ THIẾT KẾ ĐỂ XỬ LÝ.
- KHI XỬ LÝ SỰ KHÁC BIỆT, PHẢI THỰC HIỆN ƯU TIÊN THEO THỨ TỰ GIỮA CÁC BỘ MÔN: KIẾN TRÚC → KẾT CẤU / BỘ MÔN KHÁC; HOẶC ƯU TIÊN TRONG CÙNG BỘ MÔN: CHI TIẾT → TỔNG THỂ
- CÁC SỐ LIEU KÍCH THƯỚC PHẢI ĐƯỢC KIỂM TRA THỰC TẾ TẠI CÔNG TRÌNH, NẾU THẤY SỰ KHÁC BIỆT SÓ VỚI BẢN VẼ THI PHẢI BẢO CHO ĐƠN VỊ THIẾT KẾ.

#### HIỆU CHỈNH:

| REV | NGÀY | NỘI DUNG |
|-----|------|----------|
|-----|------|----------|

#### CHỦ ĐẦU TƯ:

CÔNG TY TNHH ĐẦU TƯ

**PHÚ VIỆT TÍN**

ĐỊA CHỈ: LÔ 18-19 QUỐC LỘ 1A, XÃ DẦU GIẤY, TỈNH ĐỒNG NAI, VIỆT NAM

#### CTHĐT

ĐẶNG PHƯỚC BÌNH

#### ĐƠN VỊ THIẾT KẾ:

CÔNG TY CỔ PHẦN TƯ VẤN THIẾT KẾ

**BASE ARC**

ĐỊA CHỈ: 138 ĐIỆN BIÊN PHỦ, PHƯỜNG TÂN ĐỊNH, TP. HỒ CHÍ MINH, VIỆT NAM

#### TỔNG GIÁM ĐỐC

TRẦN ĐỨC AN

#### CHỦ NHIỆM DỰ ÁN:

KTS. NGUYỄN THÀNH THÁI

#### CHỦ TRÌ THIẾT KẾ:

KS. NGÔ TÙNG THÀNH

#### THIẾT KẾ:

KS. NGUYỄN MINH DUY BẰNG

#### KIỂM TRA:

KS. NGÔ TÙNG THÀNH

#### DỰ ÁN:

KHU DÂN CƯ A1-C1 (ĐÔ THỊ DẦU GIẤY)

ĐỊA ĐIỂM: XÃ DẦU GIẤY, TỈNH ĐỒNG NAI

#### CÔNG TRÌNH:

NHÀ Ở THƯƠNG MẠI LIÊN KẾ

#### HẠNG MỤC:

MẪU NHÀ T3\_2b

#### TÊN BẢN VẼ:

MẶT BẰNG CỘT TẦNG 3, MÁI

#### MỤC ĐÍCH PHÁT HÀNH:

|                                     |                          |
|-------------------------------------|--------------------------|
| <input type="checkbox"/>            | BẢN VẼ MỜI THẦU          |
| <input type="checkbox"/>            | THIẾT KẾ CƠ SỞ           |
| <input checked="" type="checkbox"/> | THIẾT KẾ BẢN VẼ THI CÔNG |
| <input type="checkbox"/>            | BẢN VẼ HOÀN CÔNG         |
| HOÀN THÀNH                          | 07/2025                  |
| TỶ LỆ                               | NTS                      |
| SỐ HIỆU BẢN VẼ                      | KC-21                    |

|                               |                                   |                                   |                                   |                                   |                                   |
|-------------------------------|-----------------------------------|-----------------------------------|-----------------------------------|-----------------------------------|-----------------------------------|
| Mái                           |                                   |                                   |                                   |                                   |                                   |
| TẦNG 3<br>h=3.25m<br>+6.750   |                                   |                                   |                                   |                                   |                                   |
| TẦNG 2<br>h=3.2m<br>+3.550    |                                   |                                   |                                   |                                   |                                   |
| TẦNG 1<br>h=3.6m<br>-0.050    |                                   |                                   |                                   |                                   |                                   |
| CỘ CỘT<br>h = H - 0.050m<br>H |                                   |                                   |                                   |                                   |                                   |
|                               | <b>CỘT C1 (SL: 1)</b><br>TL: 1/25 | <b>CỘT C2 (SL: 1)</b><br>TL: 1/25 | <b>CỘT C3 (SL: 1)</b><br>TL: 1/25 | <b>CỘT C4 (SL: 1)</b><br>TL: 1/25 | <b>CỘT C5 (SL: 1)</b><br>TL: 1/25 |

|   |          |
|---|----------|
| GHI CHÚ:<br>- CÁC ĐƠN VỊ THI CÔNG PHẢI PHỐI HỢP BẢN VẼ CỦA TẤT CẢ CÁC BỘ MÔN KHÁC NẾU THẤY SỰ KHÁC BIỆT PHẢI BẢO CHO ĐƠN VỊ THIẾT KẾ ĐỂ XỬ LÝ.<br>- KHI XỬ LÝ SỰ KHÁC BIỆT, PHẢI THỰC HIỆN ƯU TIÊN THEO THỨ TỰ GIỮA CÁC BỘ MÔN: KIẾN TRÚC → KẾT CẤU / BỘ MÔN KHÁC; HOẶC ƯU TIÊN TRONG CÙNG BỘ MÔN: CHI TIẾT → TỔNG THỂ<br>- CÁC SỐ LƯỢNG KỊCH THUỘC PHẢI ĐƯỢC KIỂM TRA THỰC TẾ TẠI CÔNG TRÌNH, NẾU THẤY SỰ KHÁC BIỆT SỐ VỚI BẢN VẼ THI PHẢI BẢO CHO ĐƠN VỊ THIẾT KẾ. |          |
| HIỆU CHỈNH:   |          |
| REV   | NỘI DUNG |
| CHỦ ĐẦU TƯ:   |          |
| CÔNG TY TNHH ĐẦU TƯ   |          |
| <b>PHÚ VIỆT TÍN</b>   |          |
| ĐỊA CHỈ: LÔ 18-19 QUỐC LỘ 1A, XÃ DẦU GIẤY, TỈNH ĐỒNG NAI, VIỆT NAM   |          |
| CĐTĐTV   |          |
| ĐẶNG PHƯỚC BÌNH   |          |
| ĐƠN VỊ THIẾT KẾ:   |          |
| CÔNG TY CỔ PHẦN TƯ VẤN THIẾT KẾ   |          |
| <b>BASE ARC</b>   |          |
| ĐỊA CHỈ: 138 ĐIỆN BIÊN PHỦ, PHƯỜNG TÂN ĐỊNH, TP. HỒ CHÍ MINH, VIỆT NAM   |          |
| TỔNG GIÁM ĐỐC   |          |
| TRẦN ĐỨC AN   |          |
| CHỦ NHIỆM DỰ ÁN:   |          |
| KTS. NGUYỄN THÀNH THÁI   |          |
| CHỦ TRÌ THIẾT KẾ:   |          |
| KS. NGÔ TÙNG THÀNH   |          |
| THIẾT KẾ:   |          |
| KS. NGUYỄN MINH DUY BẰNG   |          |
| KIỂM TRA:   |          |
| KS. NGÔ TÙNG THÀNH   |          |
| DỰ ÁN:   |          |
| KHU DÂN CƯ A1-C1 (ĐÔ THỊ DẦU GIẤY)   |          |
| ĐỊA ĐIỂM: XÃ DẦU GIẤY, TỈNH ĐỒNG NAI   |          |
| CÔNG TRÌNH:   |          |
| NHÀ Ở THƯƠNG MẠI LIÊN KẾ   |          |
| HẠNG MỤC:   |          |
| MẪU NHÀ T3_2b   |          |
| TÊN BẢN VẼ:   |          |
| CHI TIẾT CỘT-01   |          |
| MỤC ĐÍCH PHÁT HÀNH:   |          |
| BẢN VẼ MỜI THẦU   |          |
| THIẾT KẾ CƠ SỞ   |          |
| ✓ THIẾT KẾ BẢN VẼ THI CÔNG   |          |
| BẢN VẼ HOÀN CÔNG   |          |
| HOÀN THÀNH   | 07/2025  |
| TỶ LỆ   | NTS      |
| SỐ HIỆU BẢN VẼ   | KC-22    |

|                          |        |                                        |                                        |                                        |                                        |
|--------------------------|--------|----------------------------------------|----------------------------------------|----------------------------------------|----------------------------------------|
| MÁI                      |        | <p>COTE TỪ +10.050 -&gt; +10.980</p>   |                                        |                                        |                                        |
| TẦNG 3<br>h=3.25m        | +6.750 | <p>COTE TỪ +6.750 -&gt; +10.050</p>    | <p>COTE TỪ +6.750 -&gt; +10.050</p>    | <p>COTE TỪ +6.750 -&gt; +10.050</p>    | <p>COTE TỪ +6.750 -&gt; +10.050</p>    |
| TẦNG 2<br>h=3.2m         | +3.550 | <p>COTE TỪ +3.550 -&gt; +10.050</p>    | <p>COTE TỪ +3.550 -&gt; +10.050</p>    | <p>COTE TỪ +3.550 -&gt; +10.050</p>    | <p>COTE TỪ +3.550 -&gt; +10.050</p>    |
| TẦNG 1<br>h=3.6m         | -0.050 | <p>COTE TỪ -0.050 -&gt; +10.050</p>    | <p>COTE TỪ -0.050 -&gt; +10.050</p>    | <p>COTE TỪ -0.050 -&gt; +10.050</p>    | <p>COTE TỪ -0.050 -&gt; +10.050</p>    |
| CỘ CỘT<br>h = H - 0.050m | H      | <p>COTE TỪ H - 0.050 -&gt; +10.050</p> | <p>COTE TỪ H - 0.050 -&gt; +10.050</p> | <p>COTE TỪ H - 0.050 -&gt; +10.050</p> | <p>COTE TỪ H - 0.050 -&gt; +10.050</p> |
|                          |        | <b>CỘT C6 (SL: 1)</b><br>TL: 1/25      | <b>CỘT C7 (SL: 1)</b><br>TL: 1/25      | <b>CỘT C8 (SL: 1)</b><br>TL: 1/25      | <b>CỘT C9 (SL: 1)</b><br>TL: 1/25      |

**GHI CHÚ:**

- CÁC ĐƠN VỊ THI CÔNG PHẢI PHỐI HỢP BẢN VẼ CỦA TẤT CẢ CÁC BỘ MÔN KHÁC NHU THẤY SỰ KHÁC BIỆT PHẢI BẢO CHỒN ĐƠN VỊ THIẾT KẾ ĐỂ XỬ LÝ.
- KHI XỬ LÝ SỰ KHÁC BIỆT, PHẢI THỰC HIỆN ƯU TIÊN THEO THỨ TỰ LƯU CẤP CÁC BỘ MÔN: KIẾN TRÚC - KẾT CẤU / BỘ MÔN KHÁC; HOẶC ƯU TIÊN TRONG CÙNG BỘ MÔN: CHỈ THIẾT - TÔNG THẠCH.
- CÁC SƠ LƯỢC THƯỚC PHẢI ĐƯỢC KIỂM TRA THỰC TẾ TẠI CÔNG TRÌNH, NHƯ THẤY SỰ KHÁC BIỆT SƠ VẼ BÊN VẼ THIẾT KẾ PHẢI BẢO CHỒN ĐƠN VỊ THIẾT KẾ.

HIỆU CHỈNH:

| REV | NGÀY | NỘI DUNG |
|-----|------|----------|
|-----|------|----------|

CHỦ ĐẦU TƯ:

CÔNG TY TNHH ĐẦU TƯ

PHÚ VIỆT TÍN

ĐỊA CHỈ: LÔ 18-19 QUỐC LỘ 1A, XÃ DẦU GIẦY,  
TỈNH ĐỒNG NAI, VIỆT NAM

CTHDTV

ĐẶNG PHƯỚC BÌNH

ĐƠN VỊ THIẾT KẾ:

CÔNG TY CỔ PHẦN TƯ VẤN THIẾT KẾ

BASE ARC

ĐỊA CHỈ: 138 ĐIỆN BIÊN PHỦ, PHƯỜNG TÂN ĐỊNH,  
TP. HỒ CHÍ MINH, VIỆT NAM

TỔNG GIÁM ĐỐC

TRẦN ĐỨC AN

CHỦ NHIỆM DỰ ÁN:

KTS. NGUYỄN THÀNH THÁI

CHỦ TRÌ THIẾT KẾ:

KS. NGÔ TÙNG THÀNH

THIẾT KẾ:

KS. NGUYỄN MINH DUY BẰNG

KIỂM TRA:

KS. NGÔ TÙNG THÀNH

**DỰ ÁN:**

KHU DÂN CƯ A1-C1 (ĐÔ THỊ DẦU GIẦY)

ĐỊA ĐIỂM: XÃ DẦU GIẤY, TỈNH ĐỒNG NAI

CÔNG TRÌNH:

NHÀ Ở THƯƠNG MẠI LIỀN KÈ

HANG MỤC:

MẪU NHÀ T3 2b

TÊN BẢN VẼ:

CHI TIẾT CỘT-02

MỤC ĐÍCH PHÁT HÀNH:

|                                     |                          |
|-------------------------------------|--------------------------|
| <input type="checkbox"/>            | BẢN VẼ MỜI THẦU          |
| <input type="checkbox"/>            | THIẾT KẾ CƠ SỞ           |
| <input checked="" type="checkbox"/> | THIẾT KẾ BẢN VẼ THI CÔNG |
| <input type="checkbox"/>            | BẢN VẼ HOÀN CÔNG         |

|            |  |
|------------|--|
| HOÀN THÀNH |  |
|------------|--|












|         |
|---------|
| 07/2025 |
|---------|


TỶ LỆ

|     |
|-----|
| NTS |
|-----|

SỐ HIỆU BẢN VẼ


KC-23
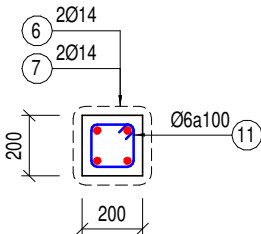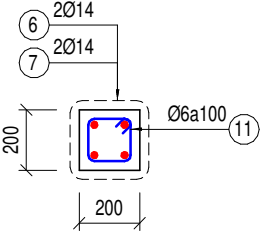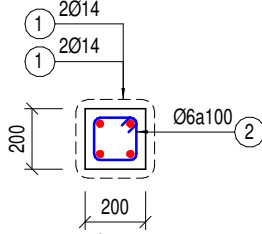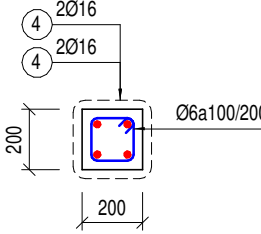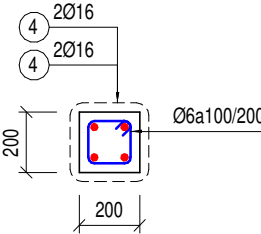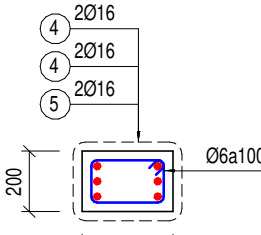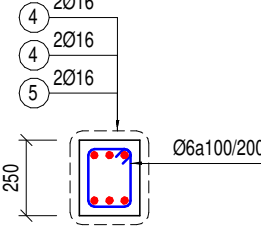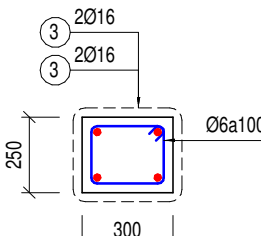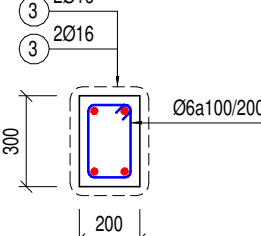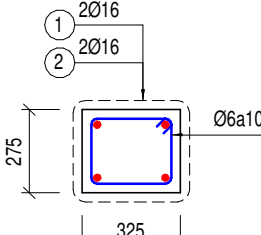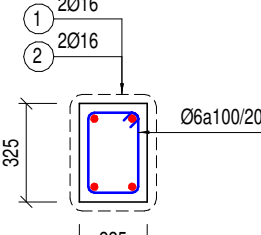
|        |   |   |   |
|--------|---|---|---|
| MÁI    |  <p>COTE TỪ +10.050 -&gt; +10.980</p>                                        |  <p>COTE TỪ +10.000 -&gt; +10.980</p>                                        |  <p>COTE TỪ +10.050 -&gt; +10.980</p> <p><b>COT CC1 (SL: 1)</b><br/>TL: 1/25</p> |
|        |   |   |   |
| TẦNG 3 |  <p>COTE TỪ +6.750 -&gt; +10.050</p>                                         |  <p>COTE TỪ +6.750 -&gt; +10.050</p>                                         |   |
| TẦNG 2 |  <p>COTE TỪ +3.550 -&gt; +10.050</p>                                        |  <p>COTE TỪ +3.550 -&gt; +10.050</p>                                        |   |
| TẦNG 1 |  <p>COTE TỪ -0.050 -&gt; +10.050</p>                                       |  <p>COTE TỪ -0.050 -&gt; +10.050</p>                                       |   |
| CỘ CỘT |  <p>COTE TỪ H -&gt; +10.050</p> <p><b>CỘT C11 (SL: 1)</b><br/>TL: 1/25</p> |  <p>COTE TỪ H -&gt; +10.050</p> <p><b>CỘT C12 (SL: 1)</b><br/>TL: 1/25</p> |   |

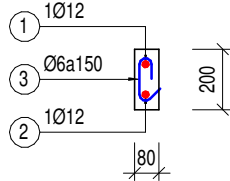


COTE TỪ +10.000 -> +10.980

**BT1 (SL=4)**  
TL: 1/25

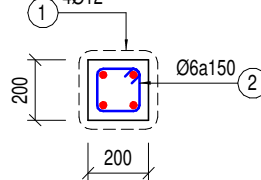


COTE TỪ +10.000 -> +10.980

**CỘT BT2 (SL:3)**  
TL: 1/25

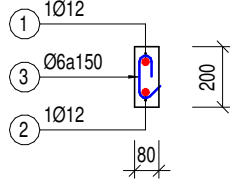

COTE TỪ -0.150 -> +1.130



**BT3 (SL=3)**  
TL: 1/25

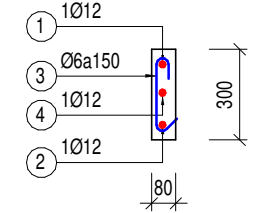


COTE THEO THỰC TẾ -> +1.130

**CỘT CR1 (SL:1)**  
TL: 1/25

|   |          |
|---|----------|
| GHI CHÚ:<br>- CÁC ĐƠN VỊ THI CÔNG PHẢI PHỐI HỢP BẢN VẼ CỦA TẤT CẢ CÁC BỘ MÔN<br>KHÁC NẾU THẤY SỰ KHÁC BIỆT PHẢI BẢO CHO ĐƠN VỊ THIẾT KẾ ĐỂ XỬ LÝ.<br>- KHI XỬ LÝ SỰ KHÁC BIỆT, PHẢI THỰC HIỆN ƯU TIÊN THEO THỨ TỰ GIỮA CÁC<br>BỘ MÔN: KIẾN TRÚC -> KẾT CẤU / BỘ MÔN KHÁC; HOẶC ƯU TIÊN TRONG CÙNG<br>BỘ MÔN: CHI TIẾT -> TỔNG THỂ<br>- CÁC SỐ LIỆU KÍCH THƯỚC PHẢI ĐƯỢC KIỂM TRA THỰC TẾ TẠI CÔNG TRÌNH,<br>NẾU THẤY SỰ KHÁC BIỆT SƠ VỚI BẢN VẼ THI PHẢI BẢO CHO ĐƠN VỊ THIẾT KẾ. |          |
| HIỆU CHỈNH:   |          |
| REV   | NỘI DUNG |
| CHỦ ĐẦU TƯ:   |          |
| CÔNG TY TNHH ĐẦU TƯ   |          |
| PHÚ VIỆT TÍN   |          |
| ĐỊA CHỈ: LÔ 18-19 QUỐC LỘ 1A, XÃ DẦU GIẤY,<br>TỈNH ĐỒNG NAI, VIỆT NAM   |          |
| CĐTĐTV   |          |
| ĐẶNG PHƯỚC BÌNH   |          |
| ĐƠN VỊ THIẾT KẾ:   |          |
| CÔNG TY CỔ PHẦN TƯ VẤN THIẾT KẾ   |          |
| BASE ARC   |          |
| ĐỊA CHỈ: 138 ĐIỆN BIÊN PHỦ, PHƯỜNG TÂN ĐỊNH,<br>TP. HỒ CHÍ MINH, VIỆT NAM   |          |
| TỔNG GIÁM ĐỐC   |          |
| TRẦN ĐỨC AN   |          |
| CHỦ NHIỆM DỰ ÁN:   |          |
| KTS. NGUYỄN THÀNH THÁI   |          |
| CHỦ TRÌ THIẾT KẾ:   |          |
| KS. NGÔ TÙNG THÀNH   |          |
| THIẾT KẾ:   |          |
| KS. NGUYỄN MINH DUY BẰNG   |          |
| KIỂM TRA:   |          |
| KS. NGÔ TÙNG THÀNH   |          |
| DỰ ÁN:   |          |
| KHU DÂN CƯ A1-C1 (ĐÔ THỊ DẦU GIẤY)   |          |
| ĐỊA ĐIỂM: XÃ DẦU GIẤY, TỈNH ĐỒNG NAI   |          |
| CÔNG TRÌNH:   |          |
| NHÀ Ở THƯƠNG MẠI LIÊN KẾ   |          |
| HẠNG MỤC:   |          |
| MẪU NHÀ T3_2b   |          |
| TÊN BẢN VẼ:   |          |
| CHI TIẾT CỘT-03   |          |
| MỤC ĐÍCH PHÁT HÀNH:   |          |
| BẢN VẼ MỜI THẦU   |          |
| THIẾT KẾ CƠ SỞ   |          |
| ✓ THIẾT KẾ BẢN VẼ THI CÔNG   |          |
| BẢN VẼ HOÀN CÔNG   |          |
| HOÀN THÀNH   | 07/2025  |
| TỶ LỆ   | NTS      |
| SỐ HIỆU BẢN VẼ   | KC-24    |

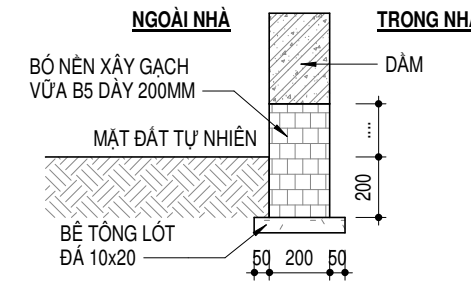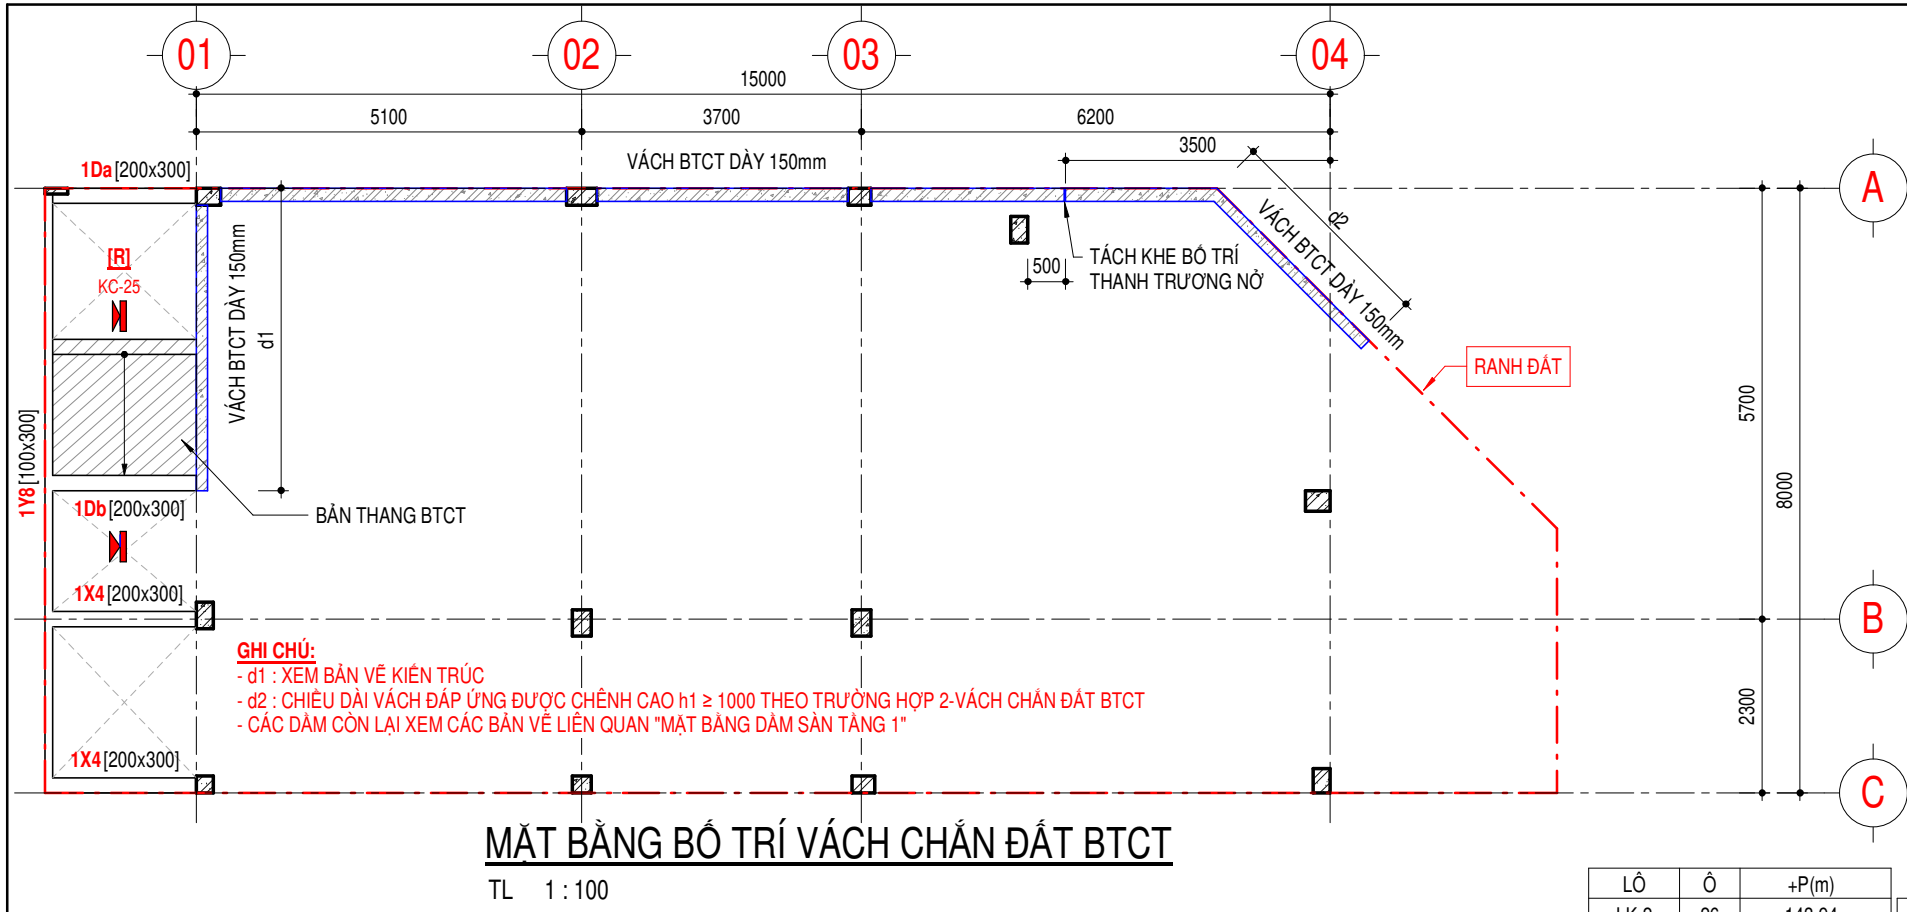

**BÓ NỀN DƯỚI ĐÀ KIỀNG**  
(ÁP DỤNG VỊ TRÍ DẪM BIẾN BAO QUANH NHÀ VÀ KHÔNG THUỘC TRƯỜNG HỢP VÁCH CHẴN ĐẤT BTCT)

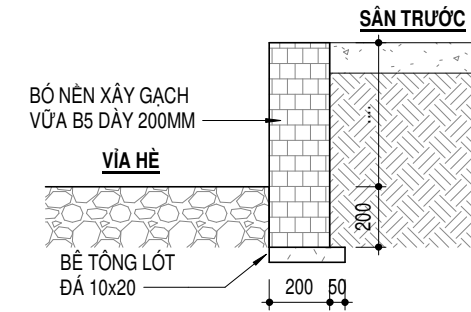

**BÓ NỀN SÀN TRƯỚC**  
(ÁP DỤNG VỊ TRÍ SÀN TRƯỚC, ĐOẠN KHÔNG LÂM VÁCH BTCT)

| LÔ   | Ô  | +P(m)  |
|------|----|--------|
| LK-2 | 26 | 143.94 |
| LK-3 | 1  | 143.96 |
| LK-4 | 1  | 144.50 |
| LK-4 | 27 | 144.50 |

\*CAO TRÌNH +P MANG TÍNH THAM KHẢO, CẦN KIỂM TRA THỰC TẾ TRƯỚC KHI THI CÔNG


| LÔ     | Ô  | +P(m)  |
|--------|----|--------|
| LK-13  | 28 | 165.38 |
| LK-14A | 1  | 165.73 |
| LK-15  | 28 | 169.76 |

\*CAO TRÌNH +P MANG TÍNH THAM KHẢO, CẦN KIỂM TRA THỰC TẾ TRƯỚC KHI THI CÔNG

## VÁCH CHẴN ĐẤT BTCT


### TRƯỜNG HỢP 1

(TRONG NHÀ TIẾP GIÁP VÍA HÈ)

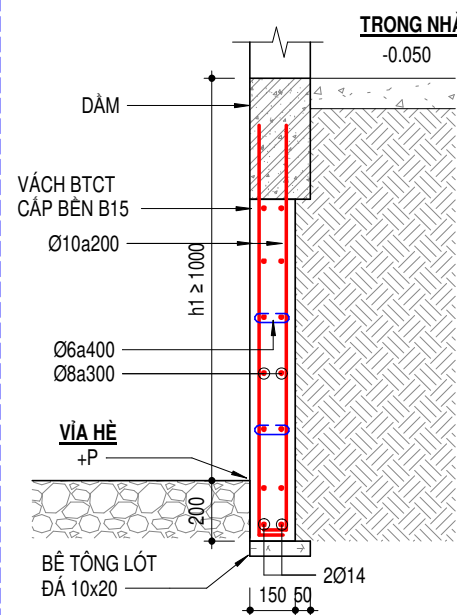





### TRƯỜNG HỢP 2

(SÀN TRƯỚC TIẾP GIÁP VÍA HÈ)

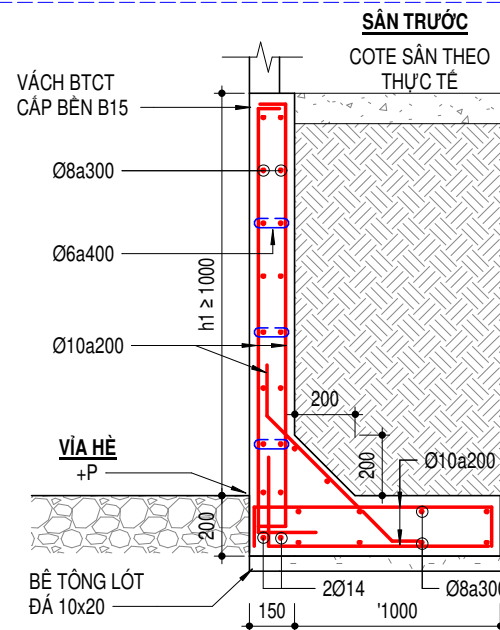

### TRƯỜNG HỢP 3

(TRONG NHÀ TIẾP GIÁP SÀN SAU)

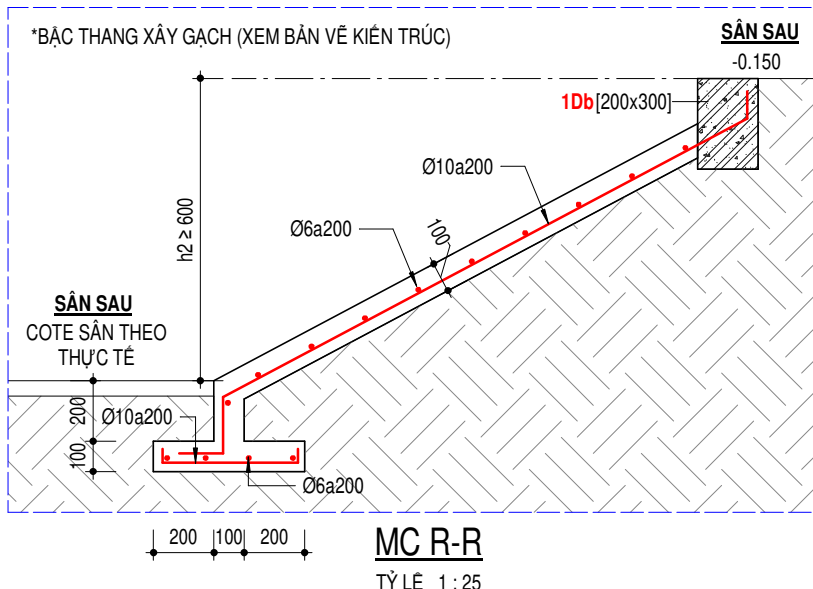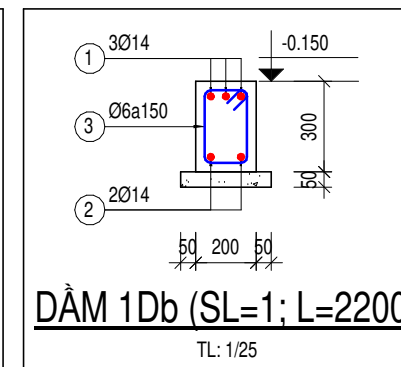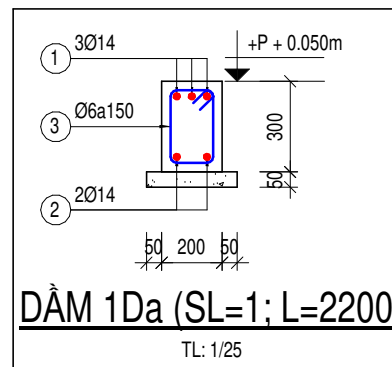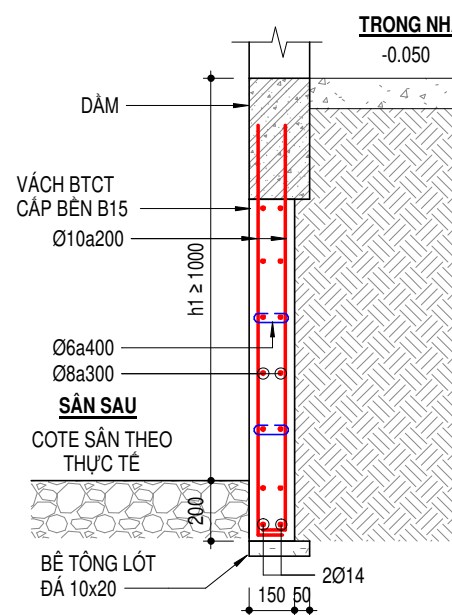

- TẤT CẢ CÁC KÍCH THƯỚC ĐƯỢC KIỂM TRA VÀ XÁC NHẬN TRÊN CÔNG TRƯỜNG.
- KÍCH THƯỚC VÀ VỊ TRÍ CÁC LỖ GEN, MƯƠNG, LAM TRANG TRÍ PHẢI ĐƯỢC KIỂM TRA SO VỚI CÁC BẢN VẼ KIẾN TRÚC, MEP CÓ LIÊN QUAN.
- CÁC VỊ TRÍ ÔNG XUYỀN DẪM XEM BẢN VẼ MEP, CHI TIẾT XUYỀN DẪM XEM BẢN VẼ GHI CHÚ CHUNG.
- NHÀ THẦU PHẢI CÓ BIỆN PHÁP CHỐNG THÂM Ở NHỮNG ĐOẠN MẠCH NGỪNG CỦA VÁCH KHI THI CÔNG.
- ĐOẠN CHÉNH CAO  $h_1 < 1000$  THÌ XÂY GẠCH (XEM CHI TIẾT BÓ NỀN).

GHI CHÚ:

- CÁC ĐƠN VỊ THI CÔNG PHẢI PHỐI HỢP BẢN VẼ CỦA TẤT CẢ CÁC BỘ MÔN KHÁC NẾU THẤY SỰ KHÁC BIỆT PHẢI BẢO CHỨNG ĐƠN VỊ THIẾT KẾ ĐỂ XỬ LÝ.  
- KHI XỬ LÝ SỰ KHÁC BIỆT, PHẢI THỰC HIỆN ƯU TIÊN THEO THỨ TỰ GIỮA CÁC BỘ MÔN: KIẾN TRÚC → KẾT CẤU / BỘ MÔN KHÁC; HOẶC ƯU TIÊN TRONG CÙNG BỘ MÔN: CHI TIẾT → TỔNG THỂ.  
- CÁC SỐ LƯU KỊCH THUỘC PHẢI ĐƯỢC KIỂM TRA THỰC TẾ TẠI CÔNG TRÌNH, NẾU THẤY SỰ KHÁC BIỆT SƠ VỚI BẢN VẼ THI PHẢI BẢO CHỨNG ĐƠN VỊ THIẾT KẾ.

HIỆU CHỈNH:

| REV | NGÀY | NỘI DUNG |
|-----|------|----------|
|-----|------|----------|

CHỦ ĐẦU TƯ:

CÔNG TY TNHH ĐẦU TƯ

**PHÚ VIỆT TÍN**

ĐỊA CHỈ: LÔ 18-19 QUỐC LỘ 1A, XÃ DẦU GIẤY, TỈNH ĐỒNG NAI, VIỆT NAM

CTHĐT

ĐẠNG PHƯỚC BÌNH

ĐƠN VỊ THIẾT KẾ:

CÔNG TY CỔ PHẦN TƯ VẤN THIẾT KẾ

**BASE ARC**

ĐỊA CHỈ: 138 ĐIỆN BIÊN PHỦ, PHƯỜNG TÂN ĐỊNH, TP. HỒ CHÍ MINH, VIỆT NAM

TỔNG GIÁM ĐỐC

TRẦN ĐỨC AN

CHỦ NHIỆM DỰ ÁN:

KTS. NGUYỄN THÀNH THÁI

CHỦ TRÌ THIẾT KẾ:

KS. NGÔ TÙNG THÀNH

THIẾT KẾ:

KS. NGUYỄN MINH DUY BẰNG

KIỂM TRA:

KS. NGÔ TÙNG THÀNH

DỰ ÁN:

KHU DÂN CƯ A1-C1 (ĐÔ THỊ DẦU GIẤY)

ĐỊA ĐIỂM: XÃ DẦU GIẤY, TỈNH ĐỒNG NAI

CÔNG TRÌNH:

NHÀ Ở THƯƠNG MẠI LIÊN KẾ

HẠNG MỤC:

MẪU NHÀ T3\_2b

TÊN BẢN VẼ:

MẶT BẰNG VÁCH CHẴN ĐẤT BTCT

MỤC ĐÍCH PHÁT HÀNH:

BẢN VẼ MỜI THẦU

THIẾT KẾ CƠ SỞ

THIẾT KẾ BẢN VẼ THI CÔNG

BẢN VẼ HOÀN CÔNG

HOÀN THÀNH


07/2025

TỶ LỆ

NTS


SỐ HIỆU BẢN VẼ

KC-25

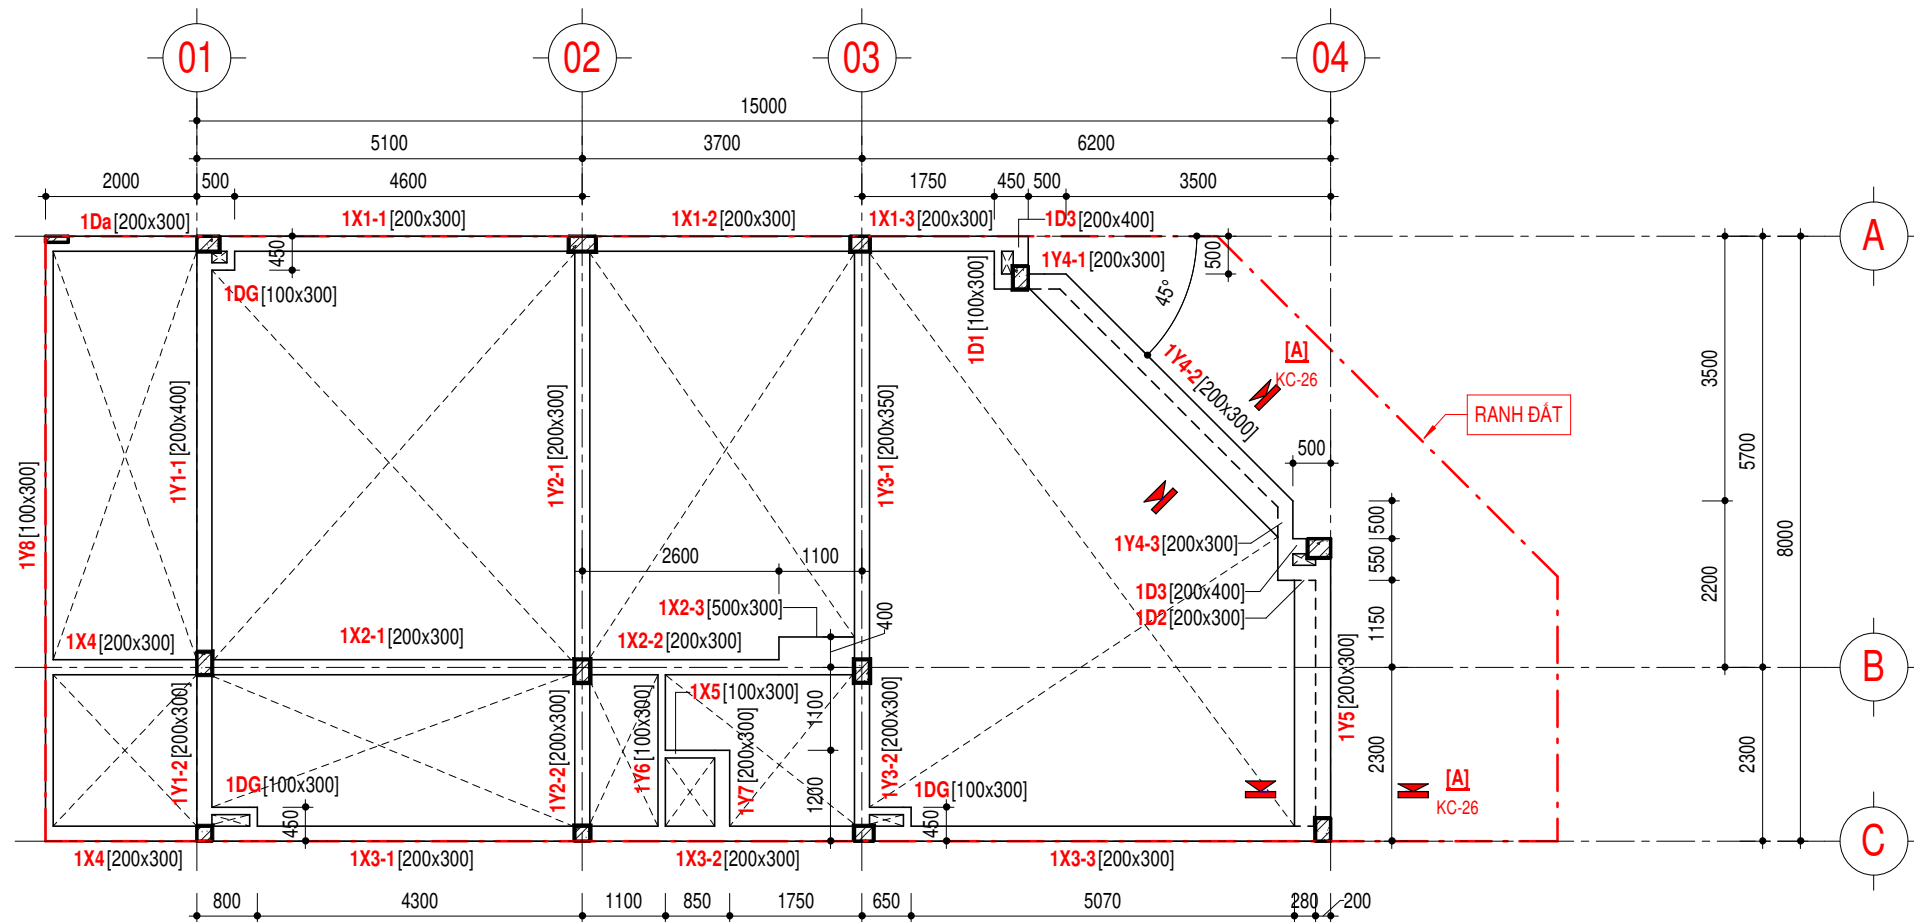

### MẶT BẰNG BỐ TRÍ DẦM SÀN - TẦNG 1

TL 1 : 100

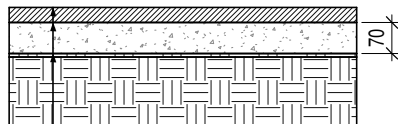

LỚP HOÀN THIỆN KIẾN TRÚC (XEM BẢN VẼ KIẾN TRÚC)

LỚP BÊ TÔNG ĐÁ 1x2 DÀY 70mm


LỚP NI LÔNG CHỐNG MẬT NƯỚC BÊ TÔNG DÀY 0.2mm

LỚP ĐẤT SAN NỀN TƯỚI NƯỚC ĐÁM CHẶT TỪNG LỚP ≤30cm, K = 0.9

### CẤU TẠO NỀN

| CAO ĐỘ DẦM - TẦNG 1 |        |
|---------------------|--------|
| TÊN DẦM             | CAO ĐỘ |
| 1D1 [100x300]       | -0.050 |
| 1D2 [200x300]       | -0.050 |
| 1D3 [200x400]       | -0.050 |
| 1DG [100x300]       | -0.050 |
| 1X1-1 [200x300]     | -0.050 |
| 1X1-2 [200x300]     | -0.050 |
| 1X1-3 [200x300]     | -0.050 |
| 1X2-1 [200x300]     | -0.050 |
| 1X2-2 [200x300]     | -0.100 |
| 1X2-3 [500x300]     | -0.100 |
| 1X3-1 [200x300]     | -0.050 |
| 1X3-2 [200x300]     | -0.100 |
| 1X3-3 [200x300]     | -0.050 |
| 1X4 [200x300]       | -0.150 |
| 1X5 [100x300]       | -0.100 |

| CAO ĐỘ DẦM - TẦNG 1 |        |
|---------------------|--------|
| TÊN DẦM             | CAO ĐỘ |
| 1Y1-1 [200x400]     | -0.050 |
| 1Y1-2 [200x300]     | -0.050 |
| 1Y2-1 [200x300]     | -0.050 |
| 1Y2-2 [200x300]     | -0.100 |
| 1Y3-1 [200x350]     | -0.050 |
| 1Y3-2 [200x300]     | -0.050 |
| 1Y4-1 [200x300]     | -0.050 |
| 1Y4-2 [200x300]     | -0.050 |
| 1Y4-3 [200x300]     | -0.050 |
| 1Y5 [200x300]       | -0.050 |
| 1Y6 [100x300]       | -0.100 |
| 1Y7 [200x300]       | -0.100 |
| 1Y8 [100x300]       | -0.150 |

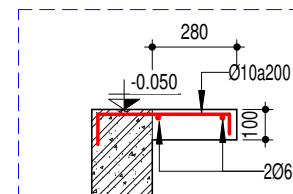

### MC A-A

TỶ LỆ 1 : 25

| CAO ĐỘ HOÀN THIỆN KIẾN TRÚC |         |
|-----------------------------|---------|
| MẶT BẰNG                    | CAO ĐỘ  |
| ĐÌNH MÃI                    | +11.000 |
| MÃI                         | +10.000 |
| TẦNG 3                      | +6.800  |
| TẦNG 2                      | +3.600  |
| TẦNG 1                      | +0.000  |

### GHI CHÚ:

- TẤT CẢ CÁC KÍCH THƯỚC ĐƯỢC KIỂM TRA VÀ XÁC NHẬN TRÊN CÔNG TRƯỜNG
  - KÍCH THƯỚC VÀ VỊ TRÍ CÁC LỖ GEN, MƯƠNG, LAM TRANG TRÍ PHẢI ĐƯỢC KIỂM TRA SO VỚI CÁC BẢN VẼ KIẾN TRÚC, MEP CÓ LIÊN QUAN.
  - CÁC VỊ TRÍ ỜNG XUYÊN DẦM XEM BẢN VẼ MEP.
- CHI TIẾT XUYÊN DẦM XEM BẢN VẼ GHI CHÚ CHUNG

### GHI CHÚ:

- CÁC ĐƠN VỊ THI CÔNG PHẢI PHỐI HỢP BẢN VẼ CỦA TẤT CẢ CÁC BỘ MÔN KHÁC NẾU THẤY SỰ KHÁC BIỆT PHẢI BẢO CHỨNG VÀ THIẾT KẾ ĐỂ XỬ LÝ.
- KHI XỬ LÝ SỰ KHÁC BIỆT, PHẢI THỰC HIỆN ƯU TIÊN THEO THỨ TỰ GIỮA CÁC BỘ MÔN: KIẾN TRÚC → KẾT CẤU / BỘ MÔN KHÁC; HOẶC ƯU TIÊN TRONG CÙNG BỘ MÔN: CHI TIẾT → TỔNG THỂ.
- CÁC SỐ LƯU KÍCH THƯỚC PHẢI ĐƯỢC KIỂM TRA THỰC TẾ TẠI CÔNG TRÌNH, NẾU THẤY SỰ KHÁC BIỆT SO VỚI BẢN VẼ THI PHẢI BẢO CHỨNG ĐƠN VỊ THIẾT KẾ.

### HIỆU CHỈNH:

| REV | NGÀY | NỘI DUNG |
|-----|------|----------|
|-----|------|----------|

### CHỦ ĐẦU TƯ:

CÔNG TY TNHH ĐẦU TƯ

**PHÚ VIỆT TÍN**

ĐỊA CHỈ: LÔ 18-19 QUỐC LỘ 1A, XÃ DẦU GIẤY, TỈNH ĐỒNG NAI, VIỆT NAM

CTHĐTV

ĐẠNG PHƯỚC BÌNH

### ĐƠN VỊ THIẾT KẾ:

CÔNG TY CỔ PHẦN TƯ VẤN THIẾT KẾ

**BASE ARC**

ĐỊA CHỈ: 138 ĐIỆN BIÊN PHỦ, PHƯỜNG TÂN ĐỊNH, TP. HỒ CHÍ MINH, VIỆT NAM

TỔNG GIÁM ĐỐC

TRẦN ĐỨC AN

CHỦ NHIỆM DỰ ÁN:

KTS. NGUYỄN THÀNH THÁI

CHỦ TRÌ THIẾT KẾ:

KS. NGÔ TÙNG THÀNH

THIẾT KẾ:

KS. NGUYỄN MINH DUY BẰNG

KIỂM TRA:

KS. NGÔ TÙNG THÀNH

DỰ ÁN:

KHU DÂN CƯ A1-C1 (ĐÔ THỊ DẦU GIẤY)

ĐỊA ĐIỂM: XÃ DẦU GIẤY, TỈNH ĐỒNG NAI

CÔNG TRÌNH:

NHÀ Ở THƯƠNG MẠI LIÊN KẾ

HẠNG MỤC:


MẪU NHÀ T3\_2b

TÊN BẢN VẼ:


MẶT BẰNG DẦM SÀN TẦNG 1

MỤC ĐÍCH PHÁT HÀNH:

|                            |         |
|----------------------------|---------|
| BẢN VẼ MỜI THẦU            |         |
| THIẾT KẾ CƠ SỞ             |         |
| ✓ THIẾT KẾ BẢN VẼ THI CÔNG |         |
| BẢN VẼ HOÀN CÔNG           |         |
| HOÀN THÀNH                 | 07/2025 |
| TỶ LỆ                      | NTS     |
| SỐ HIỆU BẢN VẼ             | KC-26   |

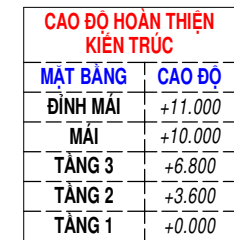

TL 1 : 100

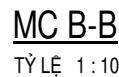

|                                                                                     |                                                                                |
|-------------------------------------------------------------------------------------|--------------------------------------------------------------------------------|
|  | KÝ HIỆU SÀN BTCT DÀY 130, MẶT TRÊN CAO ĐỘ<br>-0.050 SO VỚI COTE TẦNG KIẾN TRÚC |
|  | KÝ HIỆU SÀN BTCT DÀY 130, MẶT TRÊN CAO ĐỘ<br>-0.100 SO VỚI COTE TẦNG KIẾN TRÚC |
|  | KÝ HIỆU SÀN BTCT DÀY 120, MẶT TRÊN CAO ĐỘ<br>-0.050 SO VỚI COTE TẦNG KIẾN TRÚC |

|                                                                                     |                                                                                |
|-------------------------------------------------------------------------------------|--------------------------------------------------------------------------------|
|  | KÝ HIỆU SÀN BTCT DÀY 100, MẶT TRÊN CAO ĐỘ<br>-0.050 SO VỚI COTE TẦNG KIẾN TRÚC |
|  | KÝ HIỆU SÀN BTCT DÀY 100, MẶT TRÊN CAO ĐỘ<br>-0.100 SO VỚI COTE TẦNG KIẾN TRÚC |
|  | KÝ HIỆU SÀN BTCT DÀY 100, MẶT TRÊN CAO ĐỘ<br>-0.200 SO VỚI COTE TẦNG KIẾN TRÚC |

1. TẤT CẢ CÁC KÍCH THƯỚC ĐƯỢC KIỂM TRA VÀ XÁC NHẬN TRÊN CÔNG TRƯỜNG.  
2. KÍCH THƯỚC VÀ VỊ TRÍ CÁC LỖ GEN, MƯƠNG, LAM TRANG TRÍ PHẢI ĐƯỢC KIỂM TRA SO VỚI CÁC BẢN VẼ KIẾN TRÚC, MEP CÓ LIÊN QUAN.  
3. CÁC VỊ TRÍ ỜNG XUYỀN DÀM XEM BẢN VẼ MEP.  
CHI TIẾT XUYỀN DÀM XEM BẢN VẼ GHI CHÚ CHUNG

- CÁC ĐƠN VỊ THI CÔNG PHẢI PHỐI HỢP BẢN VẼ CỦA TẤT CẢ CÁC BỘ MÔN KHÁC NHAU THẬT SÚY KHÁC BIỆT PHẢI BẢO ĐẢM CHƠN ĐƠN VỊ THIẾT KẾ ĐÚNG LÝ.
- KHI XỬ LÝ SÚY KHÁC BIỆT, PHẢI THUẬN TIỆN ƯU TIÊN THỰC THỰC THỬ GIỮA CÁC BỘ MÔN: KIẾN TRÚC -> KẾT CẤU / BỘ MÔN KHÁC; HOẶC ƯU TIÊN TRONG CÙNG BỘ MÔN: CHỈ THIẾT -> TỔNG THỂ
- CÁC SÚY LỊCH THƯỜNG PHẢI ĐƯỢC KIỂM TRA THỰC THỰC TẠI CÔNG TRÌNH, NHƯ THỰC SÚY KHÁC BIỆT SÚY VỚI BẢN VẼ THIẾT KẾ PHẢI BẢO ĐẢM CHƠN ĐƠN VỊ THIẾT KẾ

| REV | NGÀY | NỘI DUNG |
|-----|------|----------|
|-----|------|----------|

ĐỊA CHỈ: LÔ 18-19 QUỐC LỘ 1A, XÃ DẦU GIẦY,  
TỈNH ĐỒNG NAI, VIỆT NAM

ĐẶNG PHƯỚC BÌNH

ĐỊA CHỈ: 138 ĐIỆN BIÊN PHỦ, PHƯỜNG TÂN ĐỊNH,  
TP. HỒ CHÍ MINH, VIỆT NAM

TRẦN ĐỨC AN

KS. NGÔ TÙNG THÀNH

ĐỊA ĐIỂM: XÃ DẦU GIẦY, TỈNH ĐỒNG NAI

NHÀ Ở THƯƠNG MẠI LIÊN KỀ

MẪU NHÀ T3 2b

MẶT BẰNG DẦM SÀN TẦNG 2

|  |                 |
|--|-----------------|
|  | BẢN VẼ MỜI THẦU |
|--|-----------------|

|  |                |
|--|----------------|
|  | THIẾT KẾ CƠ SỞ |
|--|----------------|

|   |                          |
|---|--------------------------|
| ✓ | THIẾT KẾ BẢN VẼ THI CÔNG |
|---|--------------------------|


|  |                  |
|--|------------------|
|  | BẢN VẼ HOÀN CÔNG |
|--|------------------|

|            |  |
|------------|--|
| HOÀN THÀNH |  |
|------------|--|

|            |         |
|------------|---------|
| HOÀN THÀNH | 07/2025 |
|------------|---------|


|       |     |
|-------|-----|
| TỶ LỆ | NTS |
|-------|-----|

|                |       |
|----------------|-------|
| SỐ HIỆU BẢN VẼ | KC-27 |
|----------------|-------|

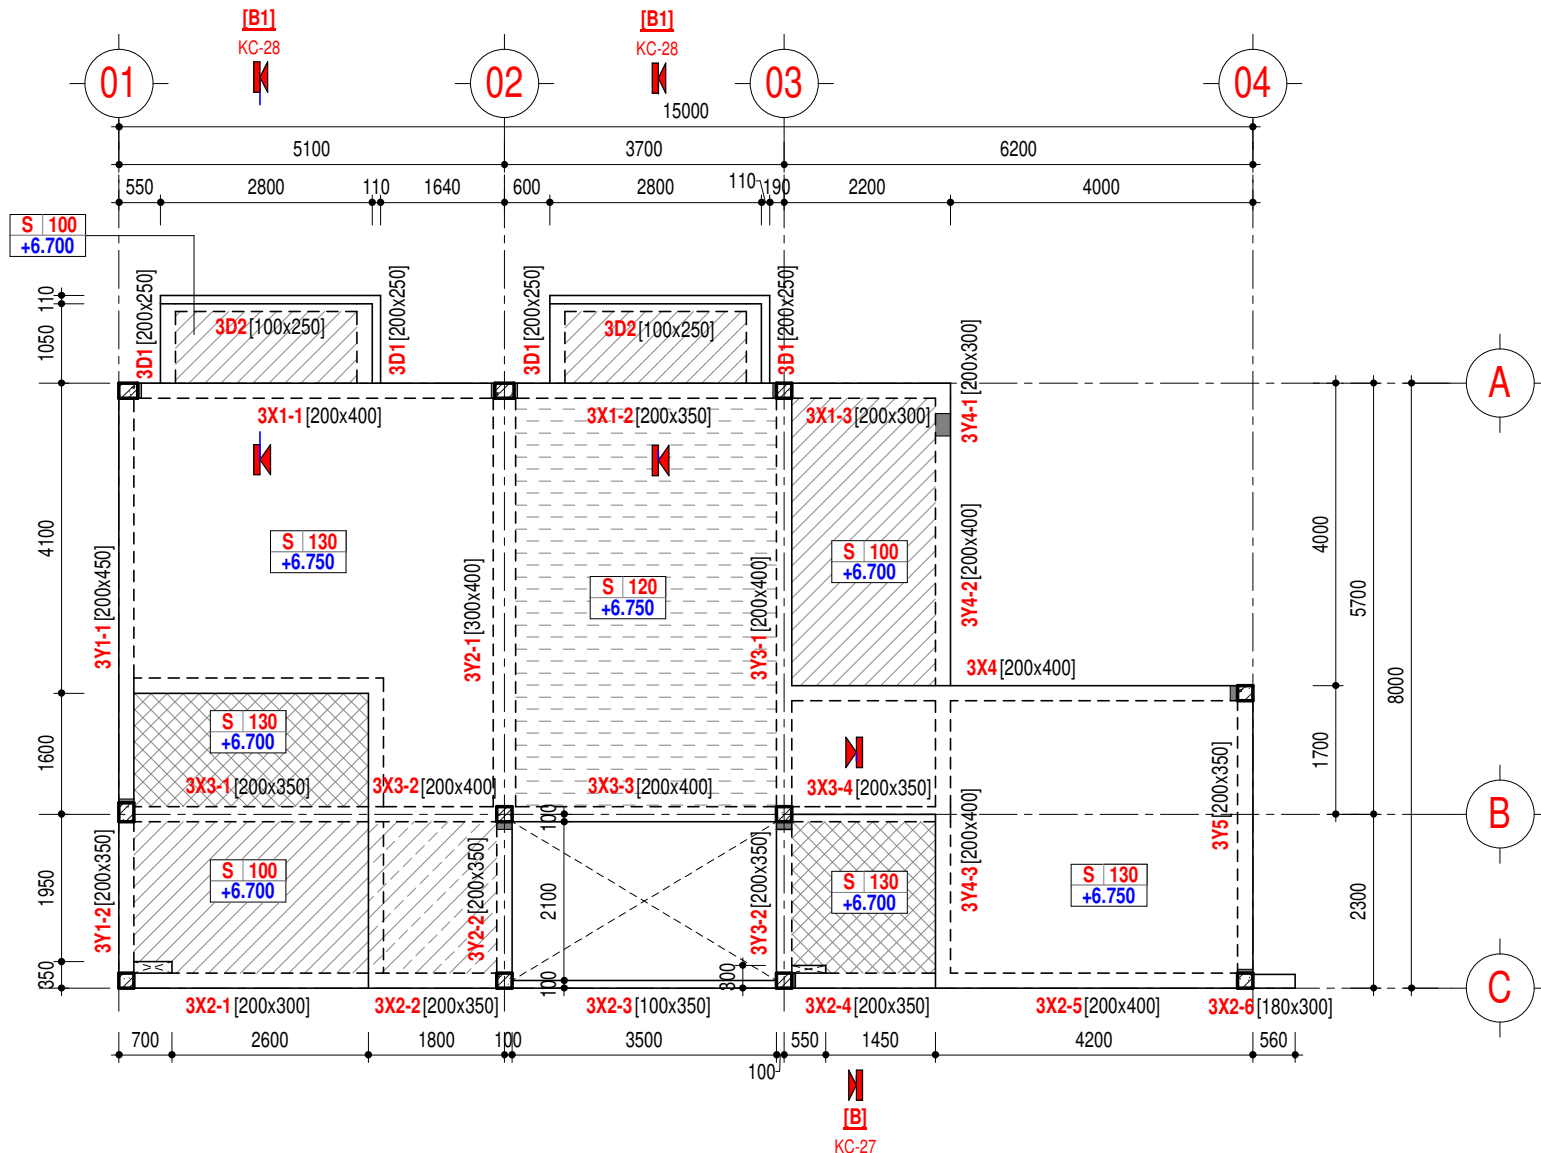

### MẶT BẰNG BỐ TRÍ DẦM SÀN - TẦNG 3

TL 1:100

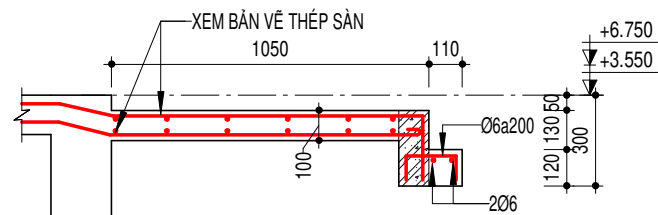

### MC B1-B1

TỶ LỆ 1:25

#### KÝ HIỆU SÀN:



KÝ HIỆU SÀN BTCT DÀY 130, MẶT TRÊN CAO ĐỘ -0.050 SO VỚI COTE TẦNG KIẾN TRÚC



KÝ HIỆU SÀN BTCT DÀY 130, MẶT TRÊN CAO ĐỘ -0.100 SO VỚI COTE TẦNG KIẾN TRÚC



KÝ HIỆU SÀN BTCT DÀY 120, MẶT TRÊN CAO ĐỘ -0.050 SO VỚI COTE TẦNG KIẾN TRÚC



KÝ HIỆU SÀN BTCT DÀY 100, MẶT TRÊN CAO ĐỘ -0.050 SO VỚI COTE TẦNG KIẾN TRÚC



KÝ HIỆU SÀN BTCT DÀY 100, MẶT TRÊN CAO ĐỘ -0.100 SO VỚI COTE TẦNG KIẾN TRÚC



KÝ HIỆU SÀN BTCT DÀY 100, MẶT TRÊN CAO ĐỘ -0.200 SO VỚI COTE TẦNG KIẾN TRÚC

#### GHI CHÚ:

- TẤT CẢ CÁC KÍCH THƯỚC ĐƯỢC KIỂM TRA VÀ XÁC NHẬN TRÊN CÔNG TRƯỜNG
- KÍCH THƯỚC VÀ VỊ TRÍ CÁC LỖ GEN, MƯƠNG, LAM TRANG TRÍ PHẢI ĐƯỢC KIỂM TRA SO VỚI CÁC BẢN VẼ KIẾN TRÚC, MEP CÓ LIÊN QUAN.
- CÁC VỊ TRÍ ỜNG XUYỀN DẦM XEM BẢN VẼ MEP. CHI TIẾT XUYỀN DẦM XEM BẢN VẼ GHI CHÚ CHUNG

| CAO ĐỘ HOÀN THIỆN KIẾN TRÚC |         |
|-----------------------------|---------|
| MẶT BẰNG                    | CAO ĐỘ  |
| ĐÌNH MÃI                    | +11.000 |
| MÃI                         | +10.000 |
| TẦNG 3                      | +6.800  |
| TẦNG 2                      | +3.600  |
| TẦNG 1                      | +0.000  |

| CAO ĐỘ DẦM - TẦNG 3 |        |
|---------------------|--------|
| TÊN DẦM             | CAO ĐỘ |
| 3D1 [200x250]       | +6.700 |
| 3D2 [100x250]       | +6.700 |
| 3X1-1 [200x400]     | +6.750 |
| 3X1-2 [200x350]     | +6.750 |
| 3X1-3 [200x300]     | +6.700 |
| 3X2-1 [200x300]     | +6.700 |
| 3X2-2 [200x350]     | +6.750 |
| 3X2-3 [100x350]     | +6.750 |
| 3X2-4 [200x350]     | +6.700 |
| 3X2-5 [200x400]     | +6.750 |
| 3X2-6 [180x300]     | +6.750 |
| 3X3-1 [200x350]     | +6.700 |
| 3X3-2 [200x400]     | +6.750 |
| 3X3-3 [200x400]     | +6.750 |
| 3X3-4 [200x350]     | +6.700 |
| 3X4 [200x400]       | +6.750 |
| 3Y1-1 [200x450]     | +6.750 |
| 3Y1-2 [200x350]     | +6.700 |
| 3Y2-1 [300x400]     | +6.750 |
| 3Y2-2 [200x350]     | +6.750 |
| 3Y3-1 [200x400]     | +6.750 |
| 3Y3-2 [200x350]     | +6.700 |
| 3Y4-1 [200x300]     | +6.700 |
| 3Y4-2 [200x400]     | +6.700 |
| 3Y4-3 [200x400]     | +6.750 |
| 3Y5 [200x350]       | +6.750 |

#### GHI CHÚ:

- CÁC ĐƠN VỊ THI CÔNG PHẢI PHỐI HỢP BẢN VẼ CỦA TẤT CẢ CÁC BỘ MÔN KHÁC NẾU THẤY SỰ KHÁC BIỆT PHẢI BẢO CHỨNG ĐƠN VỊ THIẾT KẾ XỬ LÝ.
- KHI XỬ LÝ SỰ KHÁC BIỆT, PHẢI THỰC HIỆN ƯU TIÊN THEO THỨ TỰ GIỮA CÁC BỘ MÔN: KIẾN TRÚC → KẾT CẤU / BỘ MÔN KHÁC; HOẶC ƯU TIÊN TRONG CÙNG BỘ MÔN: CHI TIẾT → TỔNG THỂ.
- CÁC SỐ LIỆU KÍCH THƯỚC PHẢI ĐƯỢC KIỂM TRA THỰC TẾ TẠI CÔNG TRÌNH, NẾU THẤY SỰ KHÁC BIỆT SO VỚI BẢN VẼ THI PHẢI BẢO CHỨNG ĐƠN VỊ THIẾT KẾ.

#### HIỆU CHỈNH:

| REV | NGÀY | NỘI DUNG |
|-----|------|----------|
|-----|------|----------|

#### CHỦ ĐẦU TƯ:

CÔNG TY TNHH ĐẦU TƯ

**PHÚ VIỆT TÍN**

ĐỊA CHỈ: LÔ 18-19 QUỐC LỘ 1A, XÃ DẦU GIẤY, TỈNH ĐỒNG NAI, VIỆT NAM

CTHĐT

ĐẶNG PHƯỚC BÌNH

#### ĐƠN VỊ THIẾT KẾ:

CÔNG TY CỔ PHẦN TƯ VẤN THIẾT KẾ

**BASE ARC**

ĐỊA CHỈ: 138 ĐIỆN BIÊN PHỦ, PHƯỜNG TÂN ĐỊNH, TP. HỒ CHÍ MINH, VIỆT NAM

TỔNG GIÁM ĐỐC

TRẦN ĐỨC AN

CHỦ NHIỆM DỰ ÁN:

KTS. NGUYỄN THÀNH THÁI

CHỦ TRÌ THIẾT KẾ:

KS. NGÔ TÙNG THÀNH

THIẾT KẾ:

KS. NGUYỄN MINH DUY BẰNG

KIỂM TRA:

KS. NGÔ TÙNG THÀNH

DỰ ÁN:

KHU DÂN CƯ A1-C1 (ĐÔ THỊ DẦU GIẤY)

ĐỊA ĐIỂM: XÃ DẦU GIẤY, TỈNH ĐỒNG NAI

CÔNG TRÌNH:

NHÀ Ở THƯƠNG MẠI LIÊN KẾ

HẠNG MỤC:

MẪU NHÀ T3\_2b

TÊN BẢN VẼ:

MẶT BẰNG DẦM SÀN TẦNG 3

MỤC ĐÍCH PHÁT HÀNH:

|                                     |                          |
|-------------------------------------|--------------------------|
| <input type="checkbox"/>            | BẢN VẼ MỜI THẦU          |
| <input type="checkbox"/>            | THIẾT KẾ CƠ SỞ           |
| <input checked="" type="checkbox"/> | THIẾT KẾ BẢN VẼ THI CÔNG |
| <input type="checkbox"/>            | BẢN VẼ HOÀN CÔNG         |

HOÀN THÀNH


07/2025

TỶ LỆ

NTS

SỐ HIỆU BẢN VẼ

KC-28

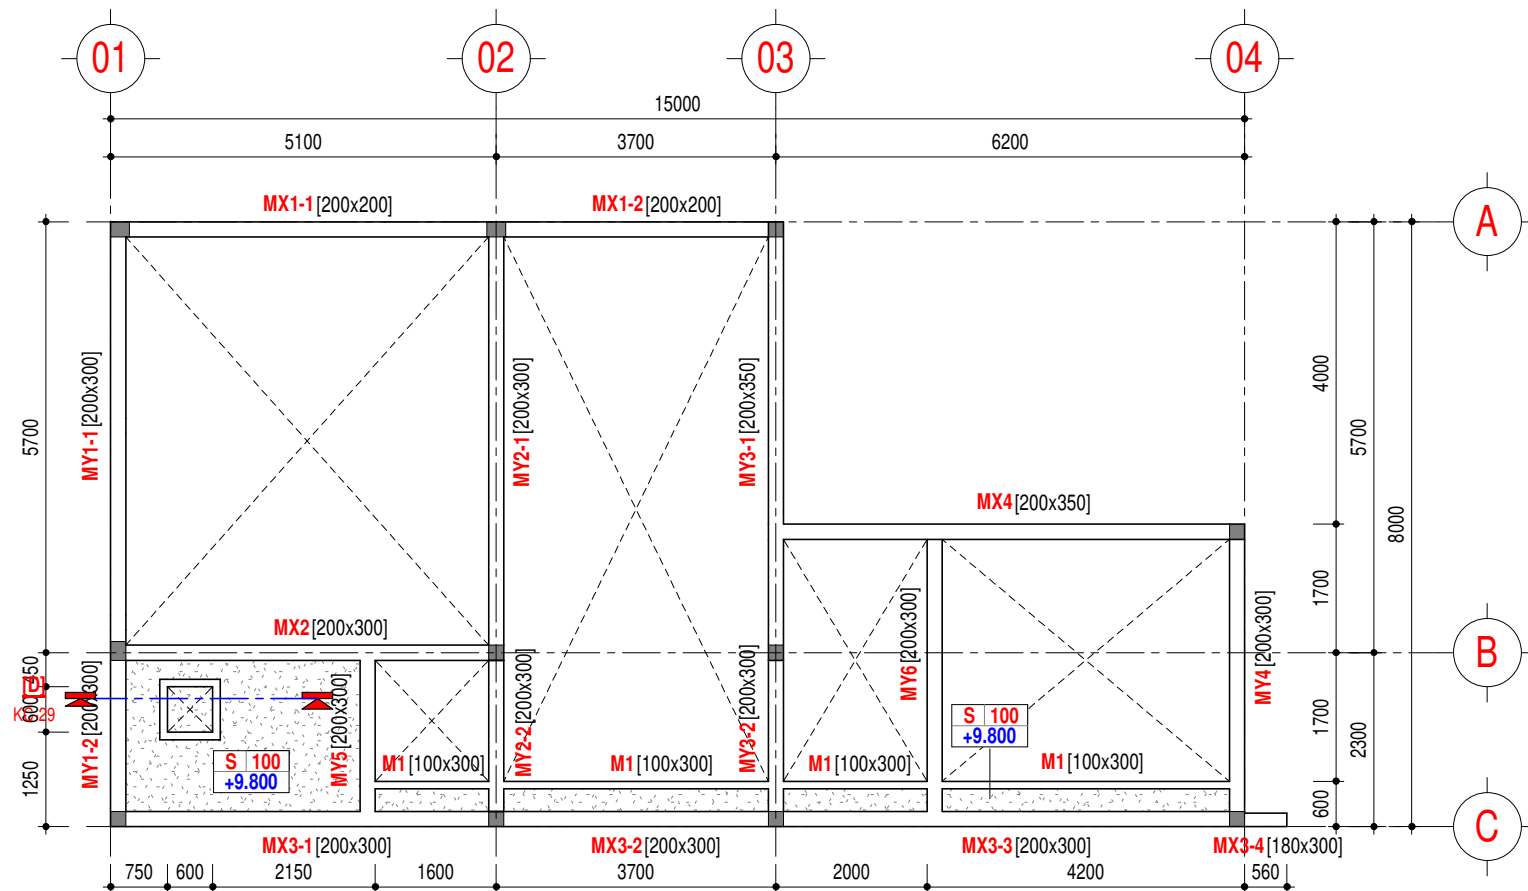

### MẶT BẰNG BỐ TRÍ DẦM SÀN MÁI

TL 1:100

#### GHI CHÚ:

- TẤT CẢ CÁC KÍCH THƯỚC ĐƯỢC KIỂM TRA VÀ XÁC NHẬN TRÊN CÔNG TRƯỜNG
  - KÍCH THƯỚC VÀ VỊ TRÍ CÁC LỖ GEN, MƯƠNG, LAM TRANG TRÍ PHẢI ĐƯỢC KIỂM TRA SO VỚI CÁC BẢN VẼ KIẾN TRÚC, MEP CÓ LIÊN QUAN.
  - CÁC VỊ TRÍ ỚNG XUYỀN DẦM XEM BẢN VẼ MEP.
- CHI TIẾT XUYỀN DẦM XEM BẢN VẼ GHI CHÚ CHUNG

#### KÝ HIỆU SÀN:



KÝ HIỆU SÀN BTCT DÀY 130, MẶT TRÊN CAO ĐỘ  
-0.050 SO VỚI COTE TẦNG KIẾN TRÚC



KÝ HIỆU SÀN BTCT DÀY 130, MẶT TRÊN CAO ĐỘ  
-0.100 SO VỚI COTE TẦNG KIẾN TRÚC




KÝ HIỆU SÀN BTCT DÀY 120, MẶT TRÊN CAO ĐỘ  
-0.050 SO VỚI COTE TẦNG KIẾN TRÚC




KÝ HIỆU SÀN BTCT DÀY 100, MẶT TRÊN CAO ĐỘ  
-0.050 SO VỚI COTE TẦNG KIẾN TRÚC



KÝ HIỆU SÀN BTCT DÀY 100, MẶT TRÊN CAO ĐỘ  
-0.100 SO VỚI COTE TẦNG KIẾN TRÚC

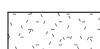

KÝ HIỆU SÀN BTCT DÀY 100, MẶT TRÊN CAO ĐỘ  
-0.200 SO VỚI COTE TẦNG KIẾN TRÚC

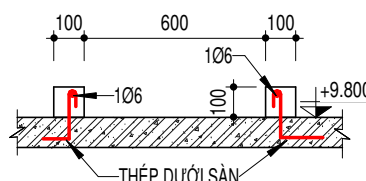

#### MC D-D

TỶ LỆ 1:25

#### CAO ĐỘ HOÀN THIỆN KIẾN TRÚC

| MẶT BẰNG | CAO ĐỘ  |
|----------|---------|
| ĐỈNH MÁI | +11.000 |
| MÁI      | +10.000 |
| TẦNG 3   | +6.800  |
| TẦNG 2   | +3.600  |
| TẦNG 1   | +0.000  |

#### CAO ĐỘ DẦM - MÁI

| TÊN DẦM         | CAO ĐỘ  |
|-----------------|---------|
| M1 [100x300]    | +10.000 |
| MX1-1 [200x200] | +10.000 |
| MX1-2 [200x200] | +10.000 |
| MX2 [200x300]   | +10.000 |
| MX3-1 [200x300] | +10.000 |
| MX3-2 [200x300] | +10.000 |
| MX3-3 [200x300] | +10.000 |
| MX3-4 [180x300] | +10.000 |
| MX4 [200x350]   | +10.050 |
| MY1-1 [200x300] | +10.000 |
| MY1-2 [200x300] | +10.000 |
| MY2-1 [200x300] | +10.000 |
| MY2-2 [200x300] | +10.000 |
| MY3-1 [200x350] | +10.050 |
| MY3-2 [200x300] | +10.000 |
| MY4 [200x300]   | +10.000 |
| MY5 [200x300]   | +10.000 |
| MY6 [200x300]   | +10.000 |

#### GHI CHÚ:

- CÁC ĐƠN VỊ THI CÔNG PHẢI PHỐI HỢP BẢN VẼ CỦA TẤT CẢ CÁC BỘ MÔN
- KHÁC NẾU THẤY SỰ KHÁC BIỆT PHẢI BẢO CHỨNG VỊ THIẾT KẾ ĐỂ XỬ LÝ.
- KHI XỬ LÝ SỰ KHÁC BIỆT, PHẢI THỰC HIỆN ƯU TIÊN THEO THỨ TỰ GIỮA CÁC BỘ MÔN: KIẾN TRÚC → KẾT CẤU / BỘ MÔN KHÁC; HOẶC ƯU TIÊN TRONG CÙNG BỘ MÔN: CHI TIẾT → TỔNG THỂ
- CÁC SỐ LƯU KÍCH THƯỚC PHẢI ĐƯỢC KIỂM TRA THỰC TẾ TẠI CÔNG TRÌNH, NẾU THẤY SỰ KHÁC BIỆT SO VỚI BẢN VẼ THI PHẢI BẢO CHỨNG VỊ THIẾT KẾ.

#### HIỆU CHỈNH:

| REV | NGÀY | NỘI DUNG |
|-----|------|----------|
|-----|------|----------|

#### CHỦ ĐẦU TƯ:

CÔNG TY TNHH ĐẦU TƯ

**PHÚ VIỆT TÍN**

ĐỊA CHỈ: LÔ 18-19 QUỐC LỘ 1A, XÃ DẦU GIẤY,  
TỈNH ĐỒNG NAI, VIỆT NAM

#### CTHĐT

ĐẠNG PHƯỚC BÌNH

#### ĐƠN VỊ THIẾT KẾ:

CÔNG TY CỔ PHẦN TƯ VẤN THIẾT KẾ

**BASE ARC**

ĐỊA CHỈ: 138 ĐIỆN BIÊN PHỦ, PHƯỜNG TÂN ĐỊNH,  
TP. HỒ CHÍ MINH, VIỆT NAM

#### TỔNG GIÁM ĐỐC

TRẦN ĐỨC AN

#### CHỦ NHIỆM DỰ ÁN:

KTS. NGUYỄN THÀNH THÁI

#### CHỦ TRÌ THIẾT KẾ:

KS. NGÔ TÙNG THÀNH

#### THIẾT KẾ:

KS. NGUYỄN MINH DUY BẰNG

#### KIỂM TRA:

KS. NGÔ TÙNG THÀNH

#### DỰ ÁN:

KHU DÂN CƯ A1-C1 (ĐÔ THỊ DẦU GIẤY)

ĐỊA ĐIỂM: XÃ DẦU GIẤY, TỈNH ĐỒNG NAI

#### CÔNG TRÌNH:

NHÀ Ở THƯƠNG MẠI LIÊN KẾ

#### HẠNG MỤC:

MẪU NHÀ T3\_2b

#### TÊN BẢN VẼ:

MẶT BẰNG DẦM SÀN MÁI

#### MỤC ĐÍCH PHÁT HÀNH:

|                                                              |  |
|--------------------------------------------------------------|--|
| BẢN VẼ MỜI THẦU                                              |  |
| THIẾT KẾ CƠ SỞ                                               |  |
| <input checked="" type="checkbox"/> THIẾT KẾ BẢN VẼ THI CÔNG |  |
| BẢN VẼ HOÀN CÔNG                                             |  |




HOÀN THÀNH 07/2025

TỶ LỆ NTS


SỐ HIỆU BẢN VẼ KC-29

|                |       |
|----------------|-------|
| SỐ HIỆU BẢN VẼ | KC-30 |
|----------------|-------|



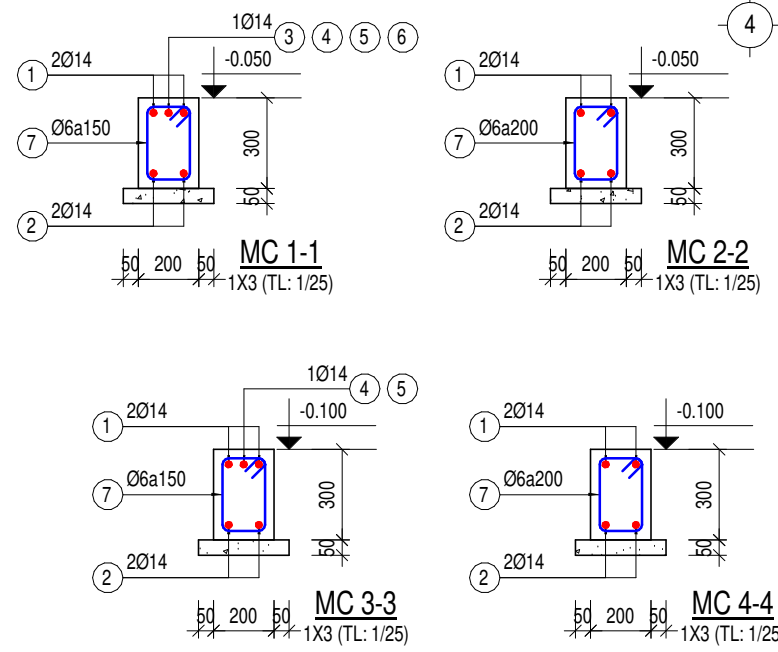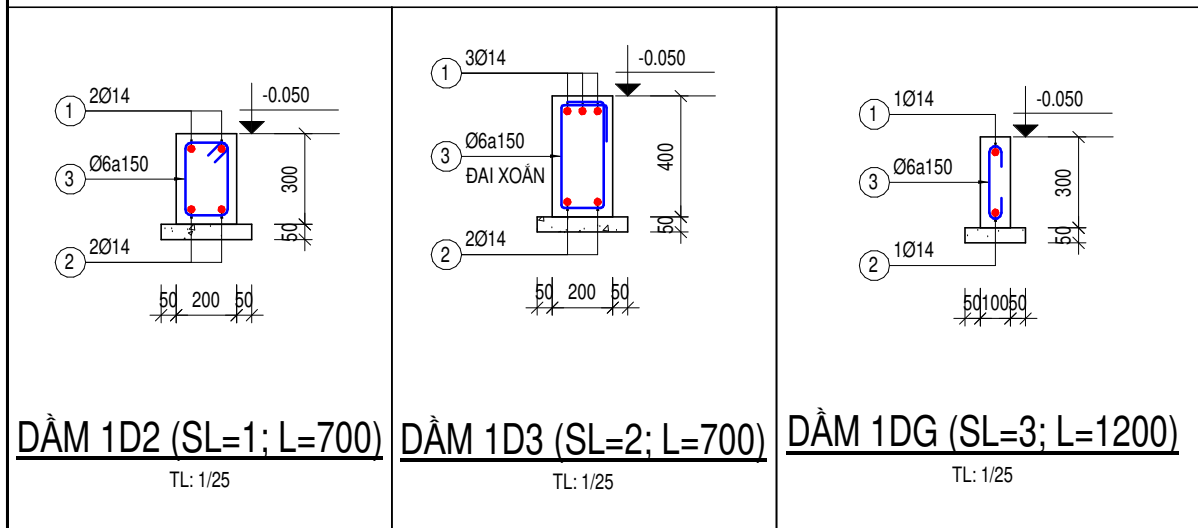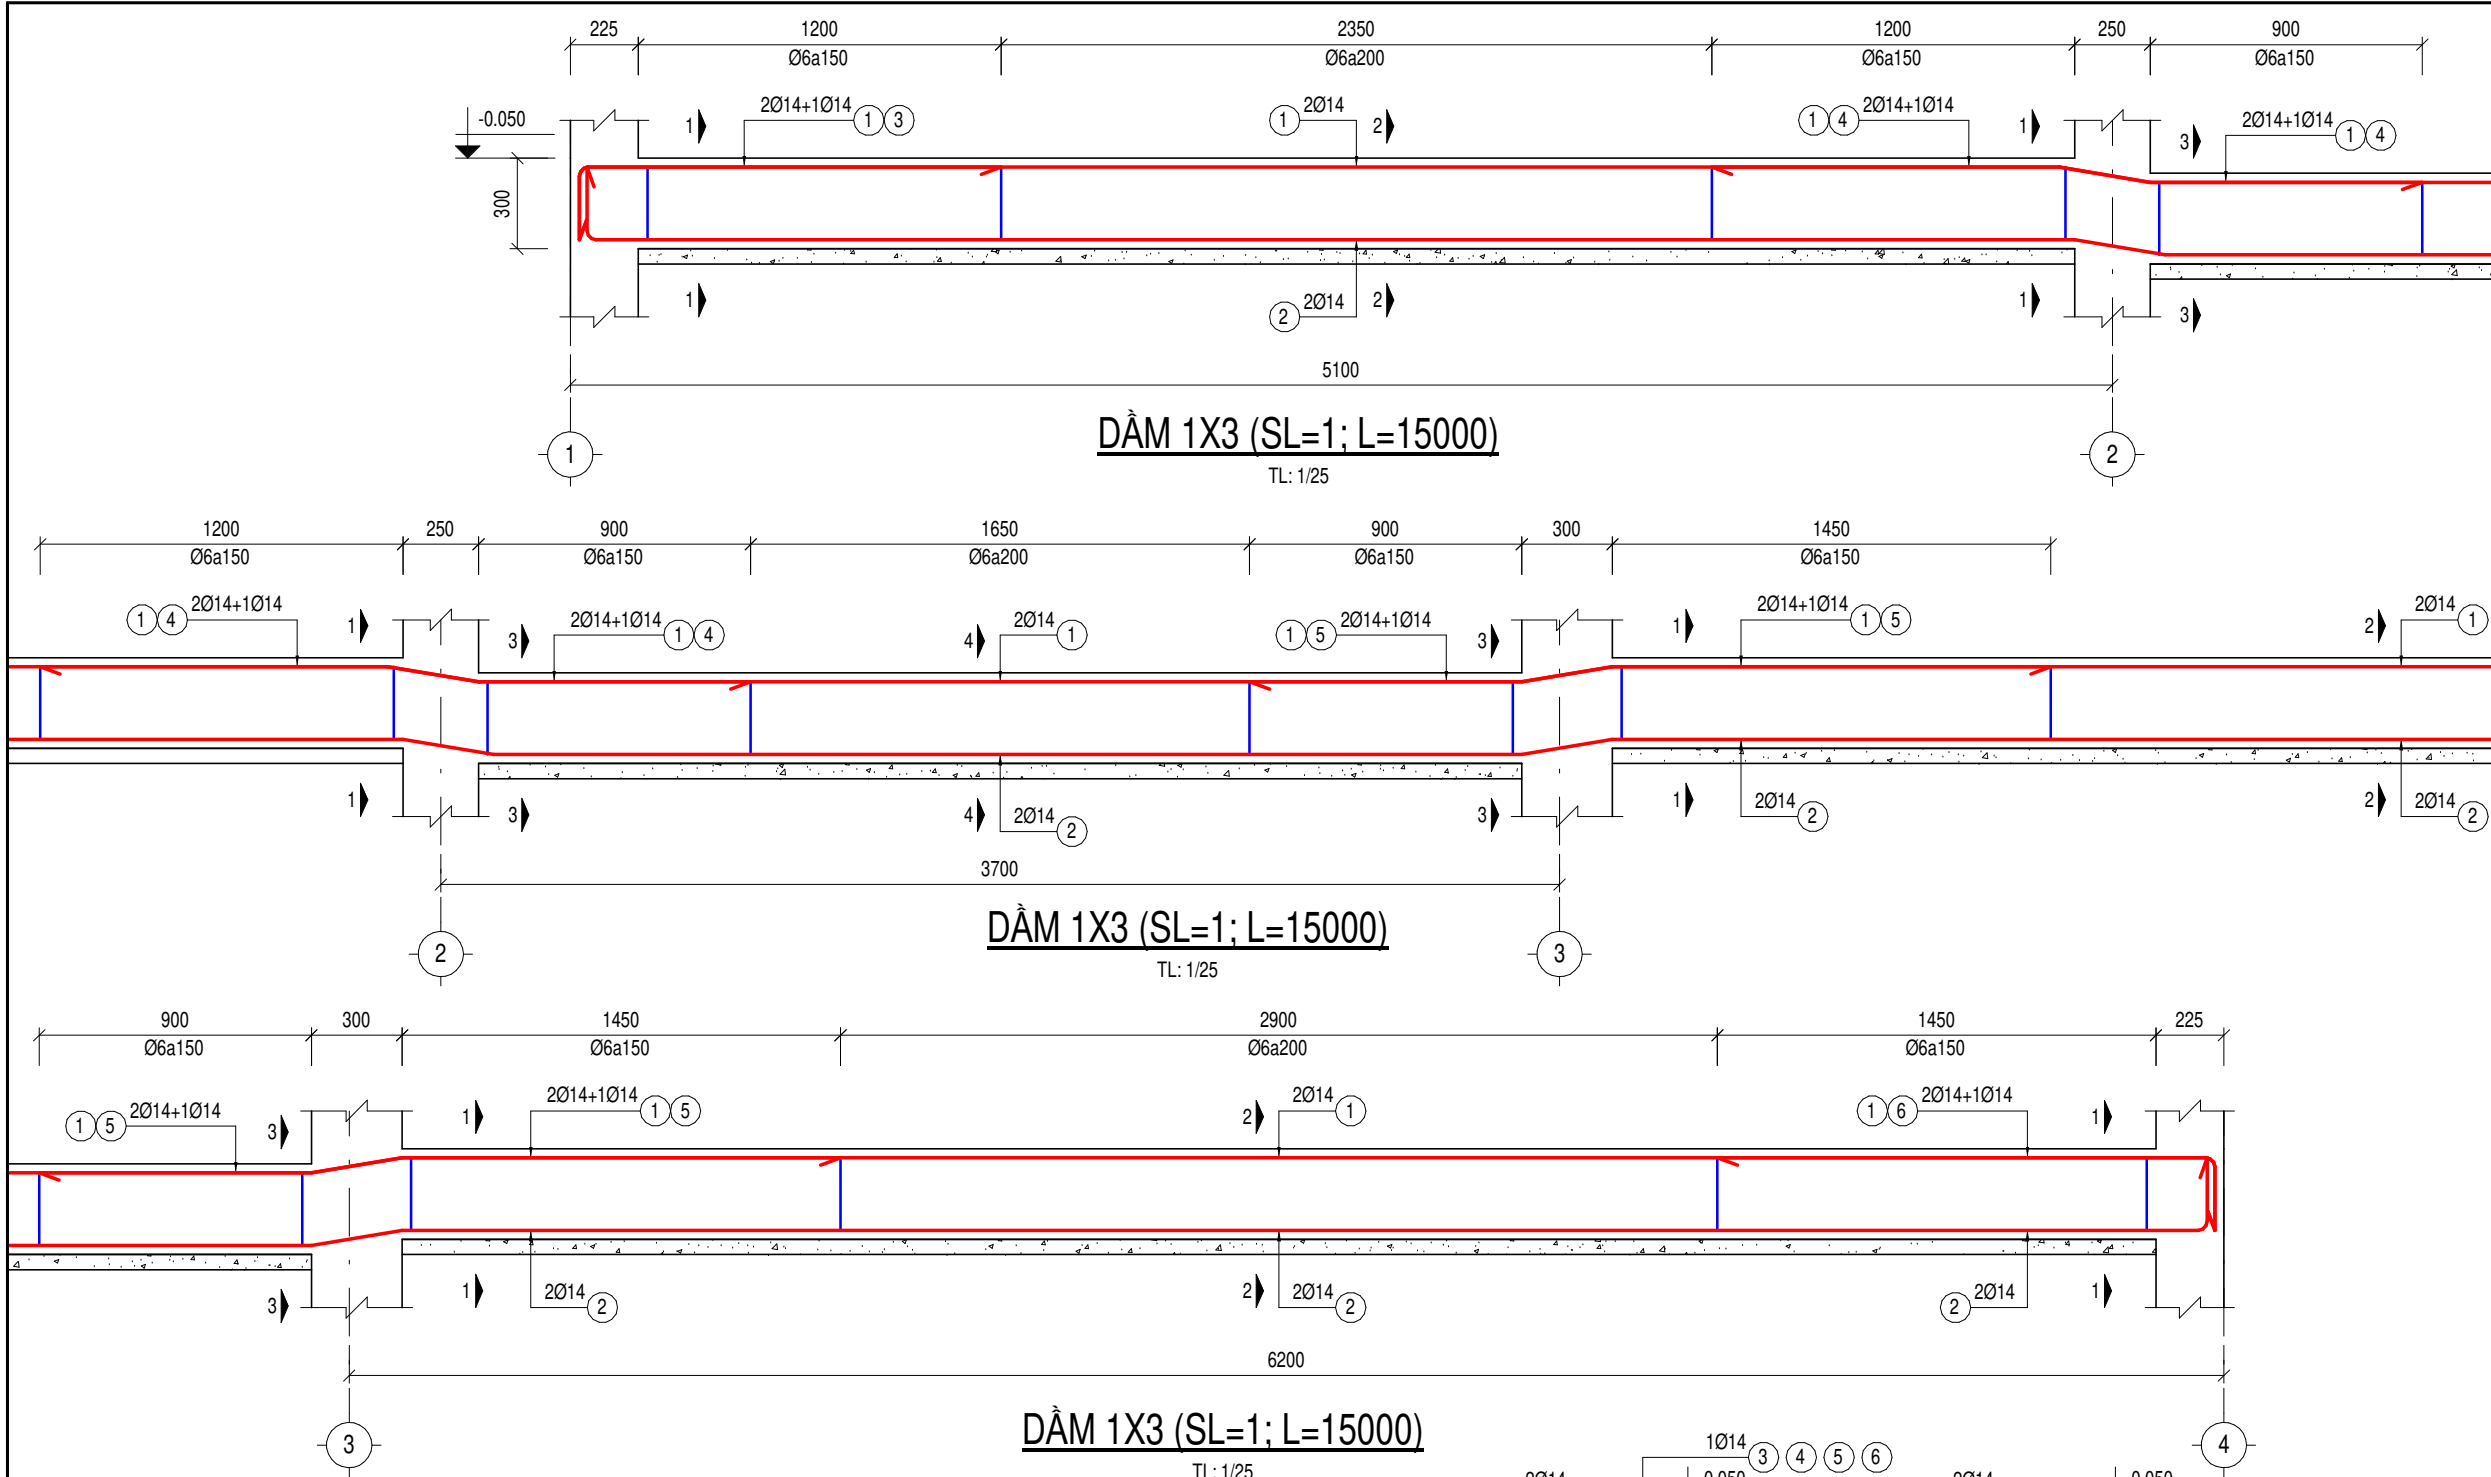

|   |      |          |
|---|------|----------|
| GHI CHÚ:<br>- CÁC ĐƠN VỊ THI CÔNG PHẢI PHỐI HỢP BẢN VẼ CỦA TẤT CẢ CÁC BỘ MÔN KHÁC NẾU THẤY SỰ KHÁC BIỆT PHẢI BÁO CHO ĐƠN VỊ THIẾT KẾ ĐỂ XỬ LÝ.<br>- KHI XỬ LÝ SỰ KHÁC BIỆT, PHẢI THỰC HIỆN ƯU TIÊN THEO THỨ TỰ GIỮA CÁC BỘ MÔN: KIẾN TRÚC → KẾT CẤU / BỘ MÔN KHÁC; HOẶC ƯU TIÊN TRONG CÙNG BỘ MÔN: CHI TIẾT → TỔNG THỂ.<br>- CÁC SỐ LIỆU KÍCH THƯỚC PHẢI ĐƯỢC KIỂM TRA THỰC TẾ TẠI CÔNG TRÌNH, NẾU THẤY SỰ KHÁC BIỆT SƠ VỚI BẢN VẼ THI PHẢI BÁO CHO ĐƠN VỊ THIẾT KẾ. |      |          |
| HIỆU CHỈNH:   |      |          |
| REV   | NGÀY | NỘI DUNG |
| CHỦ ĐẦU TƯ:   |      |          |
| CÔNG TY TNHH ĐẦU TƯ   |      |          |
| PHÚ VIỆT TÍN   |      |          |
| ĐỊA CHỈ: LÔ 18-19 QUỐC LỘ 1A, XÃ DẦU GIẤY, TỈNH ĐỒNG NAI, VIỆT NAM   |      |          |
| CHỦ ĐẦU TƯ:   |      |          |
| CÔNG TY CỔ PHẦN TƯ VẤN THIẾT KẾ   |      |          |
| BASE ARC   |      |          |
| ĐỊA CHỈ: 138 ĐIỆN BIÊN PHỦ, PHƯỜNG TÂN ĐỊNH, TP. HỒ CHÍ MINH, VIỆT NAM   |      |          |
| TỔNG GIÁM ĐỐC   |      |          |
| TRẦN ĐỨC AN   |      |          |
| CHỦ NHIỆM DỰ ÁN:   |      |          |
| KTS. NGUYỄN THÀNH THÁI   |      |          |
| CHỦ TRÌ THIẾT KẾ:   |      |          |
| KS. NGÔ TÙNG THÀNH   |      |          |
| THIẾT KẾ:   |      |          |
| KS. NGUYỄN MINH DUY BẰNG   |      |          |
| KIỂM TRA:   |      |          |
| KS. NGÔ TÙNG THÀNH   |      |          |
| DỰ ÁN:   |      |          |
| KHU DÂN CƯ A1-C1 (ĐÔ THỊ DẦU GIẤY)   |      |          |
| ĐỊA ĐIỂM: XÃ DẦU GIẤY, TỈNH ĐỒNG NAI   |      |          |
| CÔNG TRÌNH:   |      |          |
| NHÀ Ở THƯƠNG MẠI LIÊN KẾ   |      |          |
| HẠNG MỤC:   |      |          |
| MẪU NHÀ T3_2b   |      |          |
| TÊN BẢN VẼ:   |      |          |
| CHI TIẾT DẦM TẦNG 1-02   |      |          |
| MỤC ĐÍCH PHÁT HÀNH:   |      |          |
| BẢN VẼ MỜI THẦU   |      |          |
| THIẾT KẾ CƠ SỞ   |      |          |
| THIẾT KẾ BẢN VẼ THI CÔNG   |      |          |
| BẢN VẼ HOÀN CÔNG   |      |          |
| HOÀN THÀNH   |      | 07/2025  |
| TỶ LỆ   |      | NTS      |
| SỐ HIỆU BẢN VẼ   |      | KC-32    |

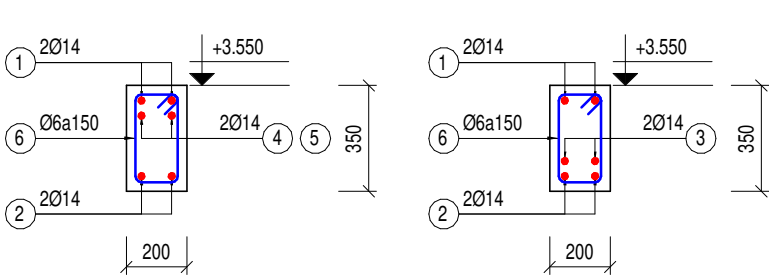


GÓI


NHIP

**DÀM 2X3 (SL=1; L=5200)**


TL: 1/25

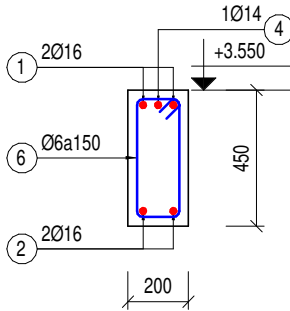

GÓI TRỤC 3

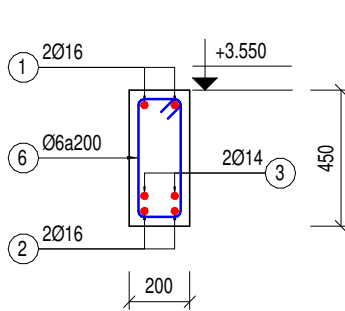


NHIP

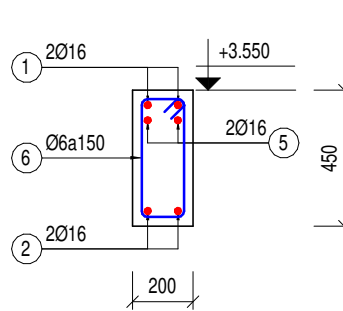


GÓI TRỤC 4

**DÀM 2X5 (SL=1; L=6300)**


TL: 1/25

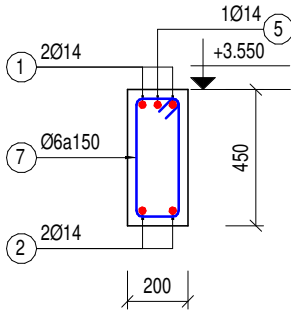

GÓI TRỤC A

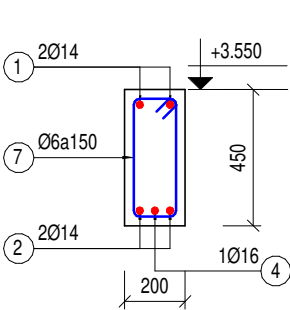


NHIP TRỤC A-B

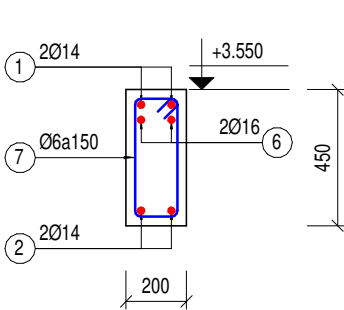


GÓI TRỤC B

ĐOẠN 2Y1-1

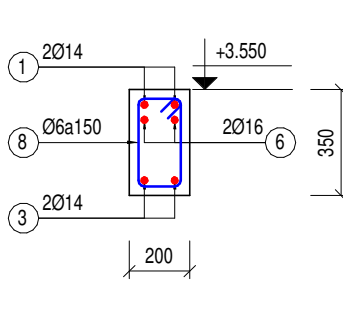

GÓI TRỤC B


ĐOẠN 2Y1-2

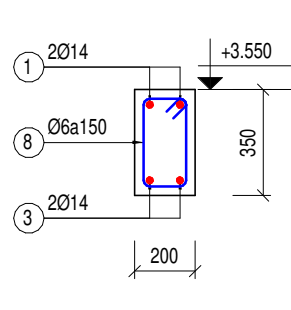


ĐOẠN CÒN LẠI

**DÀM 2Y1 (SL=1; L=8000)**


TL: 1/25

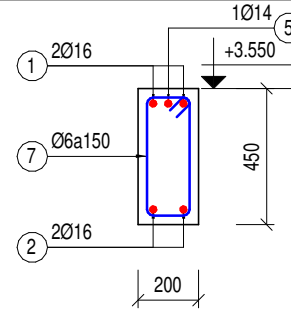

GÓI TRỤC A

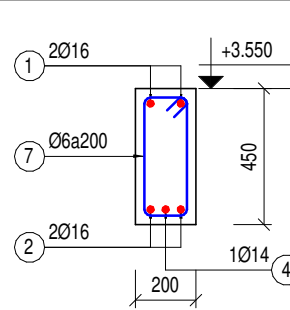


NHIP TRỤC A-B

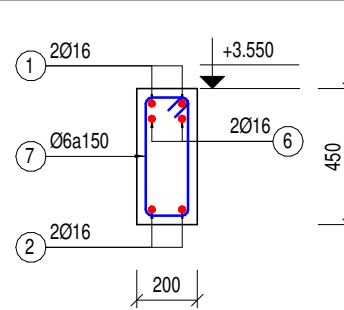


GÓI TRỤC B

ĐOẠN 2Y2-1

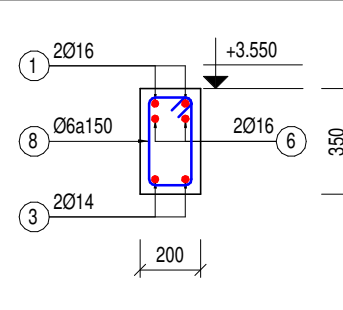

GÓI TRỤC B


ĐOẠN 2Y2-2

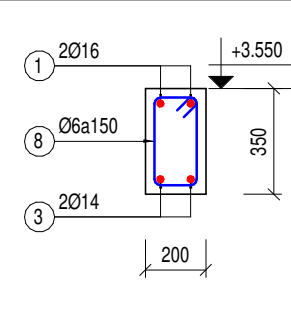


ĐOẠN CÒN LẠI

**DÀM 2Y2 (SL=1; L=8000)**


TL: 1/25

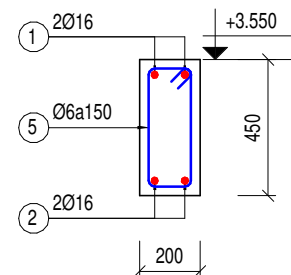

GÓI TRỤC A

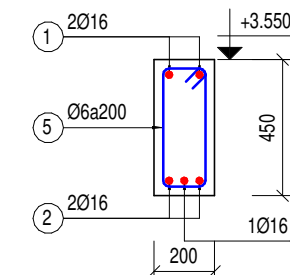


NHIP TRỤC A-B

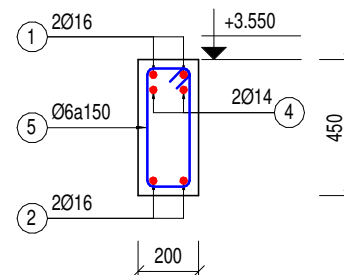


GÓI TRỤC B

ĐOẠN 2Y3-1

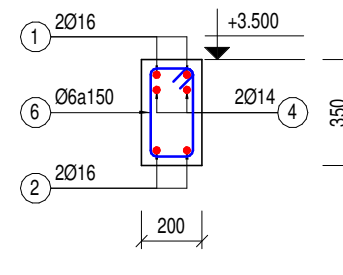

GÓI TRỤC B

ĐOẠN 2Y3-2

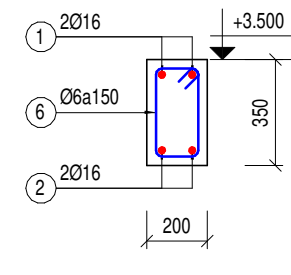

ĐOẠN CÒN LẠI

**DÀM 2Y3 (SL=1; L=8000)**

TL: 1/25

GHI CHÚ:

- CÁC ĐƠN VỊ THI CÔNG PHẢI PHỐI HỢP BẢN VẼ CỦA TẤT CẢ CÁC BỘ MÔN KHÁC NẾU THẤY SỰ KHÁC BIỆT PHẢI BẢO CHO ĐƠN VỊ THIẾT KẾ ĐỂ XỬ LÝ.  
- KHI XỬ LÝ SỰ KHÁC BIỆT, PHẢI THỰC HIỆN ƯU TIÊN THEO THỨ TỰ GIỮA CÁC BỘ MÔN: KIẾN TRÚC → KẾT CẤU / BỘ MÔN KHÁC; HOẶC ƯU TIÊN TRONG CÙNG BỘ MÔN: CHI TIẾT → TỔNG THỂ  
- CÁC SỐ LIỆU KÍCH THƯỚC PHẢI ĐƯỢC KIỂM TRA THỰC TẾ TẠI CÔNG TRÌNH, NẾU THẤY SỰ KHÁC BIỆT SƠ VỚI BẢN VẼ THI PHẢI BẢO CHO ĐƠN VỊ THIẾT KẾ.

HIỆU CHỈNH:

| REV | NGÀY | NỘI DUNG |
|-----|------|----------|
|-----|------|----------|

CHỦ ĐẦU TƯ:

CÔNG TY TNHH ĐẦU TƯ

**PHÚ VIỆT TÍN**

ĐỊA CHỈ: LÔ 18-19 QUỐC LỘ 1A, XÃ DẦU GIẤY, TỈNH ĐỒNG NAI, VIỆT NAM

CTHĐT

ĐẠNG PHƯỚC BÌNH

ĐƠN VỊ THIẾT KẾ:

CÔNG TY CỔ PHẦN TƯ VẤN THIẾT KẾ

**BASE ARC**

ĐỊA CHỈ: 138 ĐIỆN BIÊN PHỦ, PHƯỜNG TÂN ĐỊNH, TP. HỒ CHÍ MINH, VIỆT NAM

TỔNG GIÁM ĐỐC

TRẦN ĐỨC AN

CHỦ NHIỆM DỰ ÁN:

KTS. NGUYỄN THÀNH THÁI

CHỦ TRÌ THIẾT KẾ:

KS. NGÔ TÙNG THÀNH

THIẾT KẾ:

KS. NGUYỄN MINH DUY BẰNG

KIỂM TRA:

KS. NGÔ TÙNG THÀNH

DỰ ÁN:

KHU DÂN CƯ A1-C1 (ĐÔ THỊ DẦU GIẤY)

ĐỊA ĐIỂM: XÃ DẦU GIẤY, TỈNH ĐỒNG NAI

CÔNG TRÌNH:

NHÀ Ở THƯƠNG MẠI LIÊN KẾ

HẠNG MỤC:

MẪU NHÀ T3\_2b

TÊN BẢN VẼ:

CHI TIẾT DÀM TẦNG 2-01

MỤC ĐÍCH PHÁT HÀNH:

|                          |                 |
|--------------------------|-----------------|
| <input type="checkbox"/> | BẢN VẼ MỜI THẦU |
|--------------------------|-----------------|

|                          |                |
|--------------------------|----------------|
| <input type="checkbox"/> | THIẾT KẾ CƠ SỞ |
|--------------------------|----------------|


|                                     |                          |
|-------------------------------------|--------------------------|
| <input checked="" type="checkbox"/> | THIẾT KẾ BẢN VẼ THI CÔNG |
|-------------------------------------|--------------------------|


|                          |                  |
|--------------------------|------------------|
| <input type="checkbox"/> | BẢN VẼ HOÀN CÔNG |
|--------------------------|------------------|

|            |         |
|------------|---------|
| HOÀN THÀNH | 07/2025 |
|------------|---------|


|       |     |
|-------|-----|
| TỶ LỆ | NTS |
|-------|-----|

|                |       |
|----------------|-------|
| SỐ HIỆU BẢN VẼ | KC-33 |
|----------------|-------|

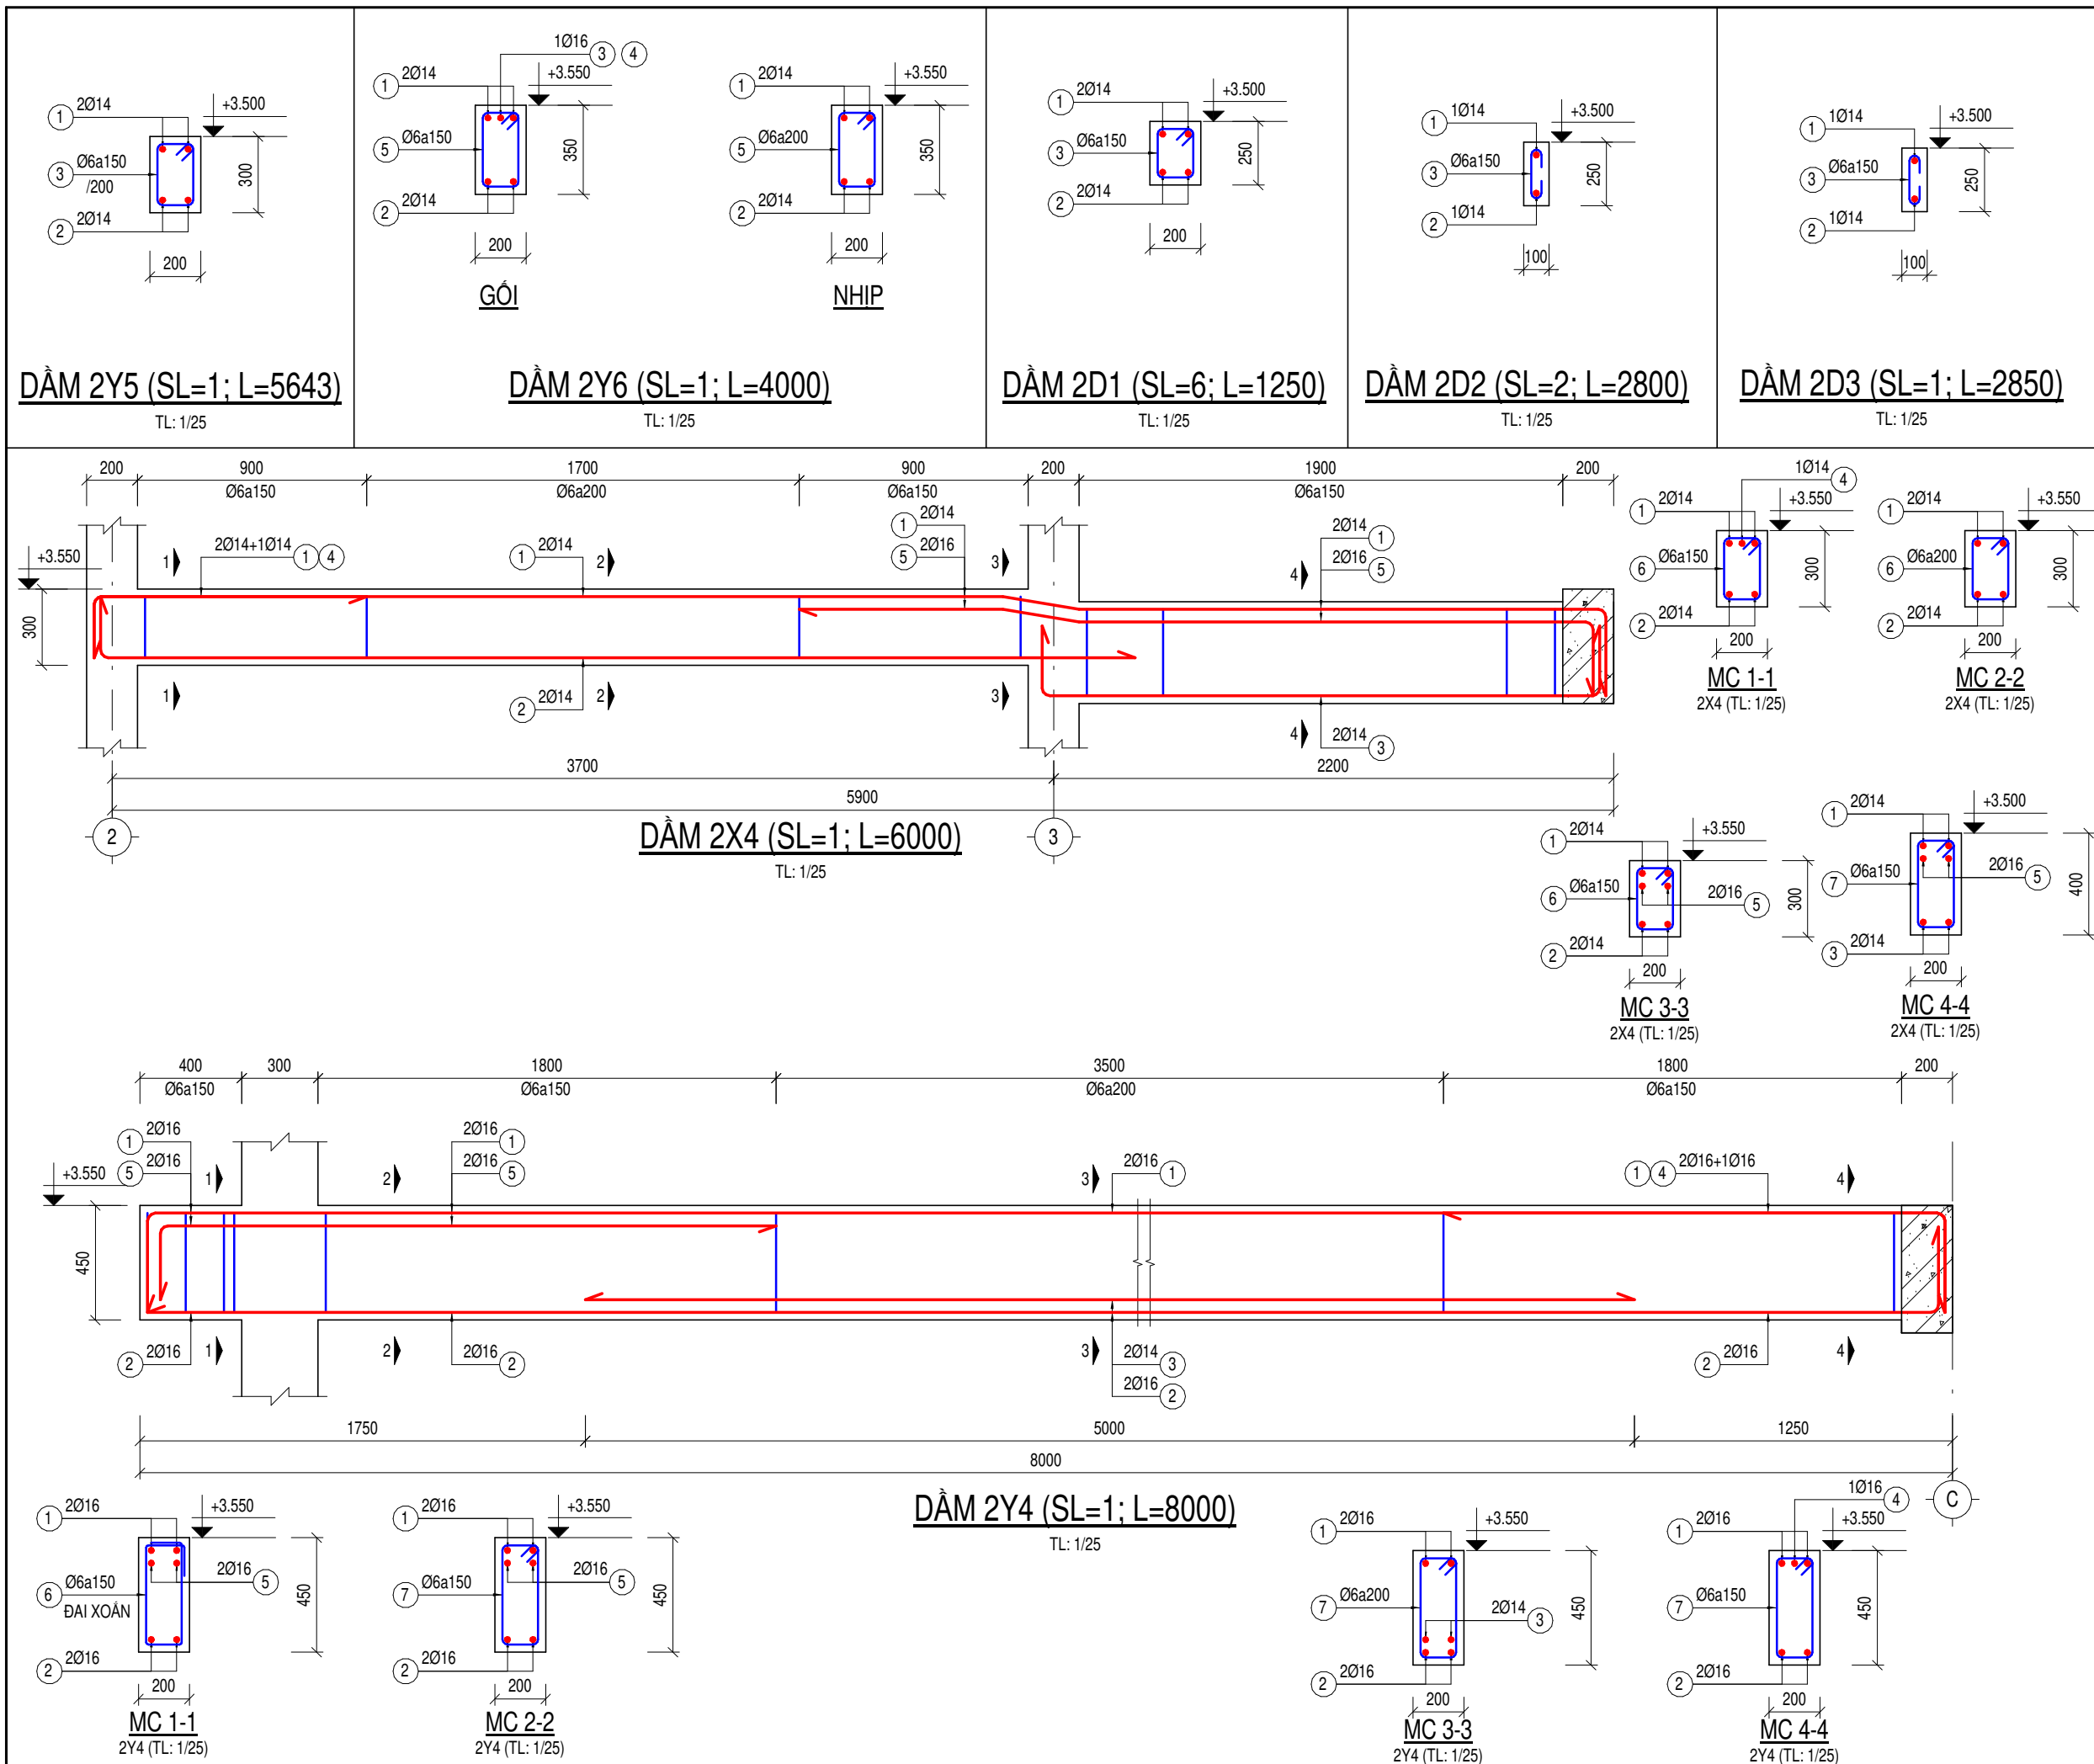[illegible]

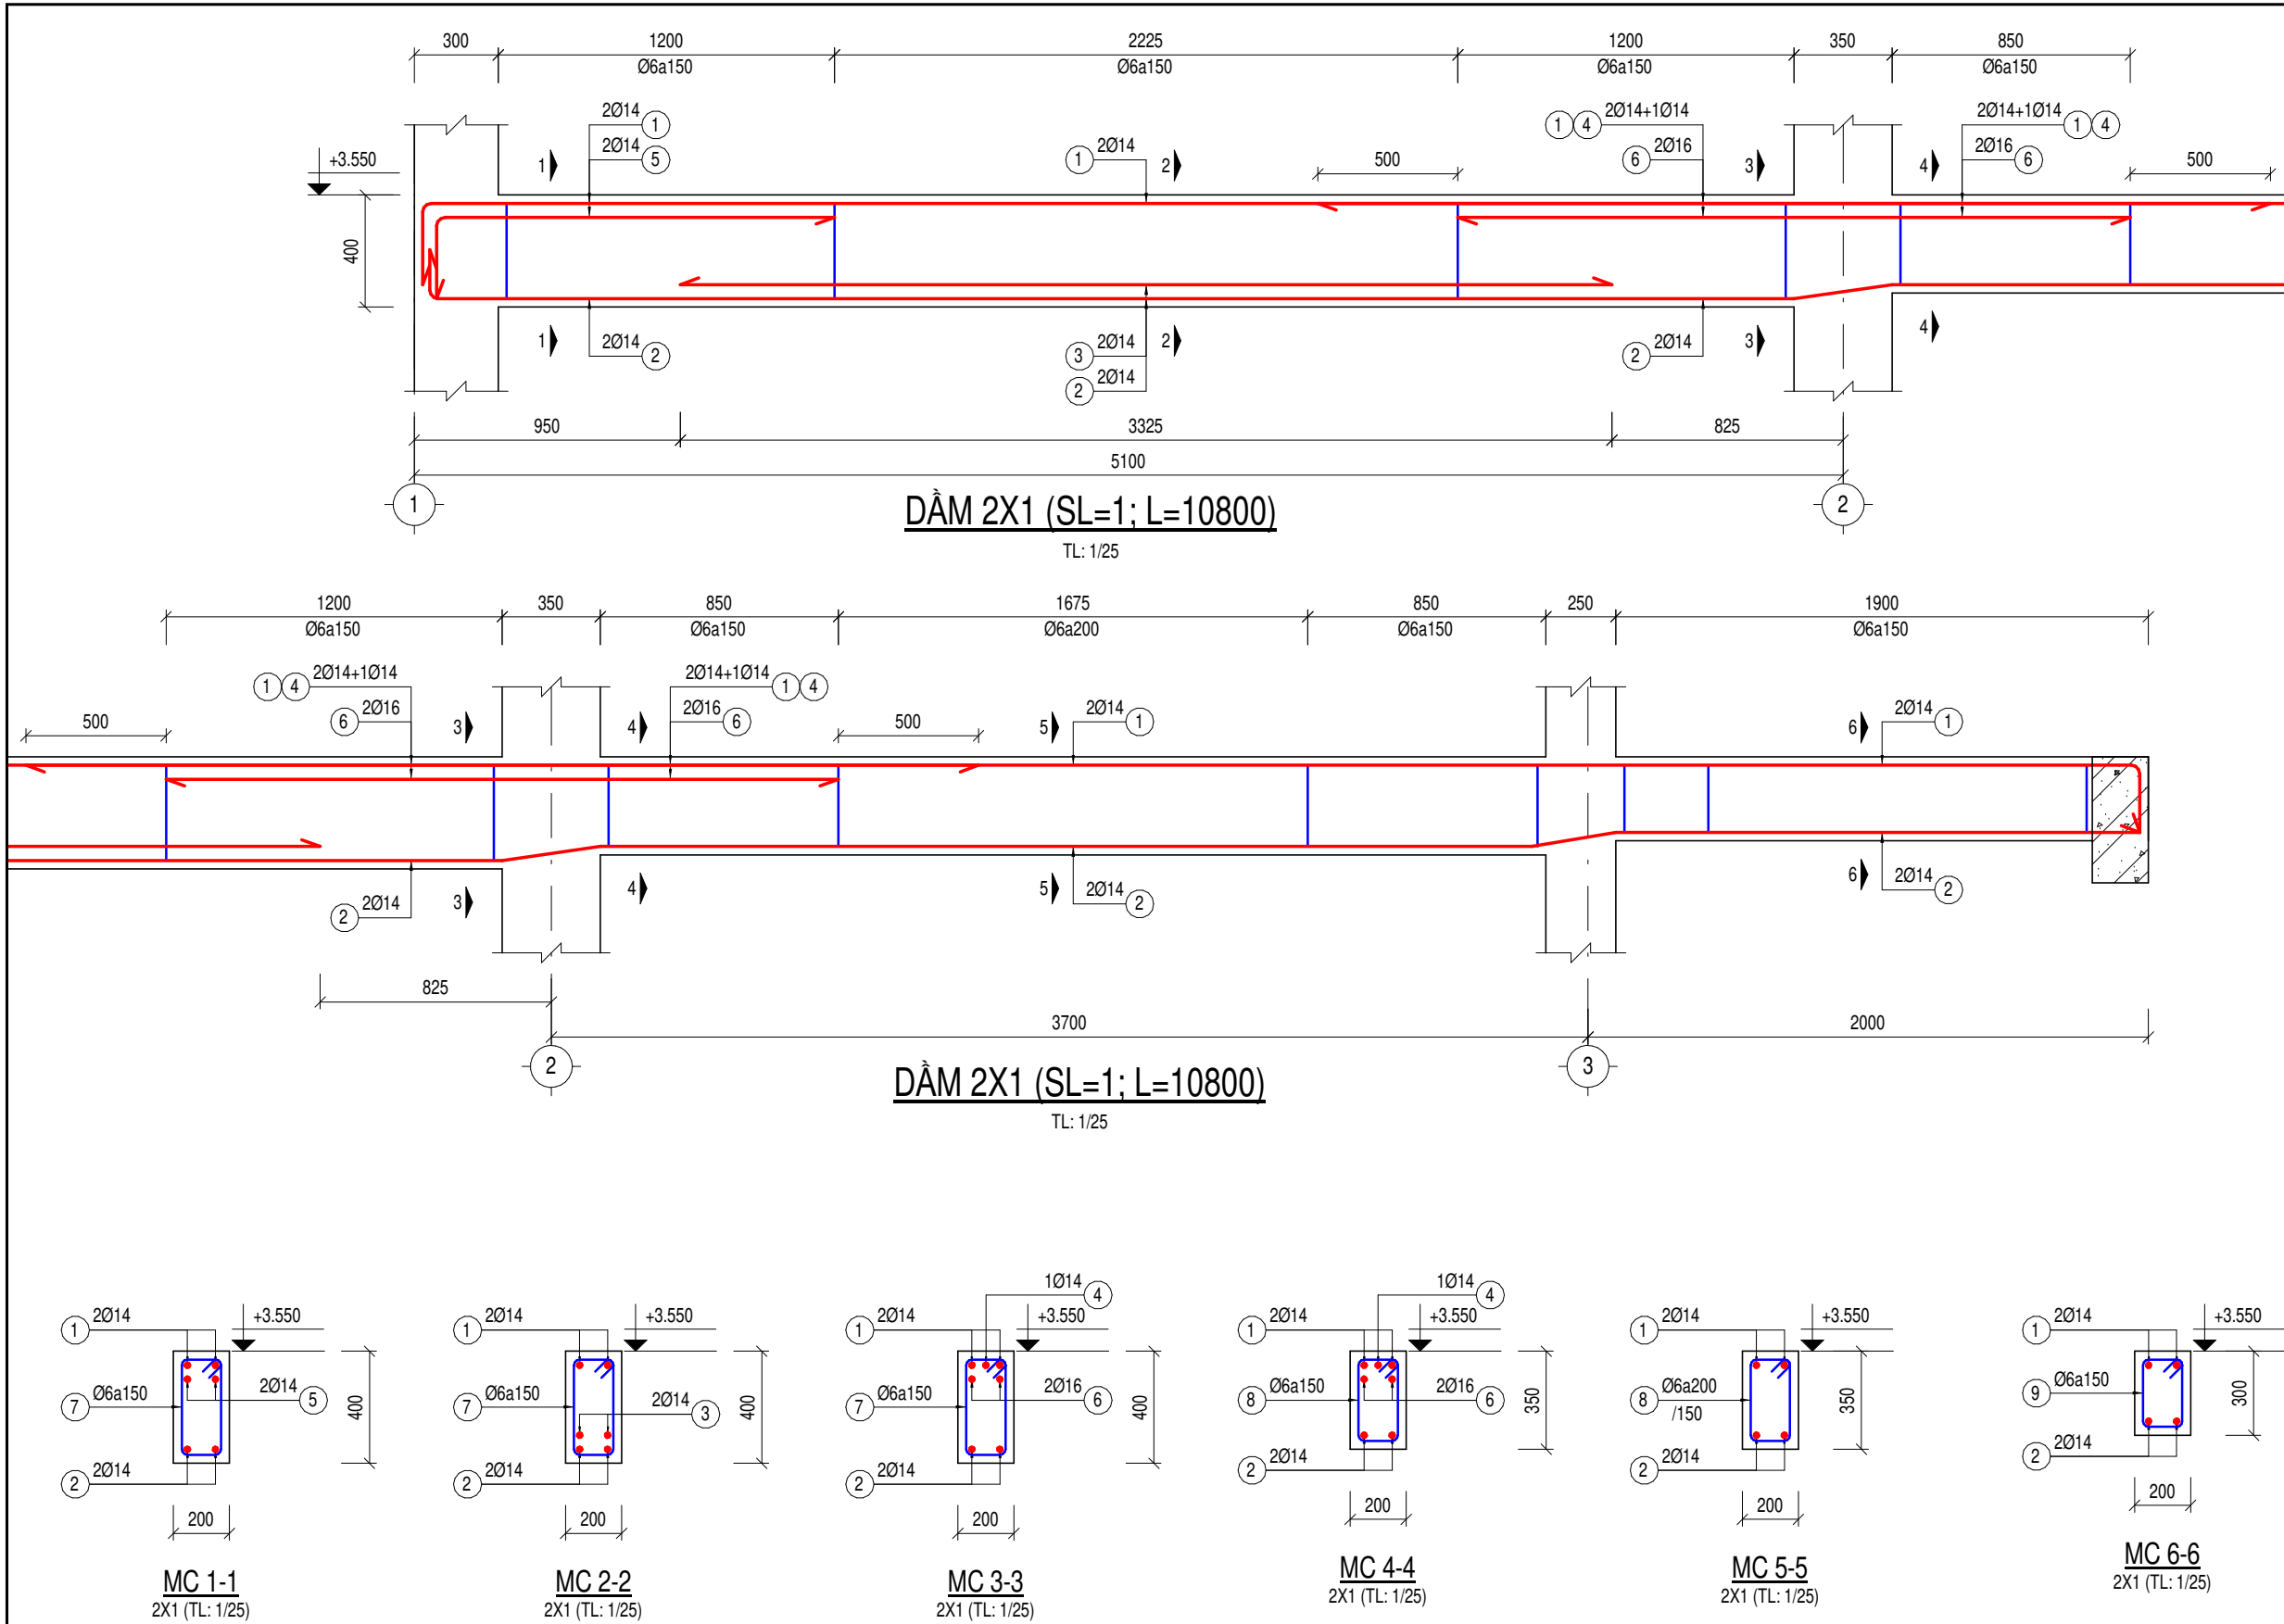

|   |         |                 |
|---|---------|-----------------|
| GHI CHÚ:<br>- CÁC ĐƠN VỊ THI CÔNG PHẢI PHỐI HỢP BẢN VẼ CỦA TẤT CẢ CÁC BỘ MÔN KHÁC NẾU THẤY SỰ KHÁC BIỆT PHẢI BÁO CHO ĐƠN VỊ THIẾT KẾ ĐỂ XỬ LÝ.<br>- KHI XỬ LÝ SỰ KHÁC BIỆT, PHẢI THỰC HIỆN ƯU TIÊN THEO THỨ TỰ GIỮA CÁC BỘ MÔN: KIẾN TRÚC → KẾT CẤU / BỘ MÔN KHÁC; HOẶC ƯU TIÊN TRONG CÙNG BỘ MÔN: CHI TIẾT → TỔNG THỂ<br>- CÁC SỐ LIỆU KỊCH THUỘC PHẢI ĐƯỢC KIỂM TRA THỰC TẾ TẠI CÔNG TRÌNH, NẾU THẤY SỰ KHÁC BIỆT SƠ VỚI BẢN VẼ THI PHẢI BÁO CHO ĐƠN VỊ THIẾT KẾ. |         |                 |
| HIỆU CHỈNH:   |         |                 |
| REV   | NGÀY    | NỘI DUNG        |
| CHỦ ĐẦU TƯ:   |         |                 |
| CÔNG TY TNHH ĐẦU TƯ   |         |                 |
| PHÚ VIỆT TÍN   |         |                 |
| ĐỊA CHỈ: LÔ 18-19 QUỐC LỘ 1A, XÃ DẦU GIẤY, TỈNH ĐỒNG NAI, VIỆT NAM   |         |                 |
| CĐT/ĐTV   |         | ĐẶNG PHƯỚC BÌNH |
| ĐƠN VỊ THIẾT KẾ:   |         |                 |
| CÔNG TY CỔ PHẦN TƯ VẤN THIẾT KẾ   |         |                 |
| BASE ARC   |         |                 |
| ĐỊA CHỈ: 138 ĐIỆN BIÊN PHỦ, PHƯỜNG TÂN ĐỊNH, TP. HỒ CHÍ MINH, VIỆT NAM   |         |                 |
| TỔNG GIÁM ĐỐC   |         | TRẦN ĐỨC AN     |
| CHỦ NHIỆM DỰ ÁN:   |         |                 |
| KTS. NGUYỄN THÀNH THÁI   |         |                 |
| CHỦ TRÌ THIẾT KẾ:   |         |                 |
| KS. NGÔ TÙNG THÀNH   |         |                 |
| THIẾT KẾ:   |         |                 |
| KS. NGUYỄN MINH DUY BẰNG   |         |                 |
| KIỂM TRA:   |         |                 |
| KS. NGÔ TÙNG THÀNH   |         |                 |
| DỰ ÁN:   |         |                 |
| KHU DÂN CƯ A1-C1 (ĐÔ THỊ DẦU GIẤY)   |         |                 |
| ĐỊA ĐIỂM: XÃ DẦU GIẤY, TỈNH ĐỒNG NAI   |         |                 |
| CÔNG TRÌNH:   |         |                 |
| NHÀ Ở THƯƠNG MẠI LIÊN KẾ   |         |                 |
| HẠNG MỤC:   |         |                 |
| MẪU NHÀ T3_2b   |         |                 |
| TÊN BẢN VẼ:   |         |                 |
| CHI TIẾT DẦM TẦNG 2-03   |         |                 |
| MỤC ĐÍCH PHÁT HÀNH:   |         |                 |
| <input type="checkbox"/> BẢN VẼ MỜI THẦU   |         |                 |
| <input type="checkbox"/> THIẾT KẾ CƠ SỞ   |         |                 |
| <input checked="" type="checkbox"/> THIẾT KẾ BẢN VẼ THI CÔNG   |         |                 |
| <input type="checkbox"/> BẢN VẼ HOÀN CÔNG   |         |                 |
| HOÀN THÀNH   | 07/2025 |                 |
| TỶ LỆ   | NTS     |                 |
| SỐ HIỆU BẢN VẼ   | KC-35   |                 |

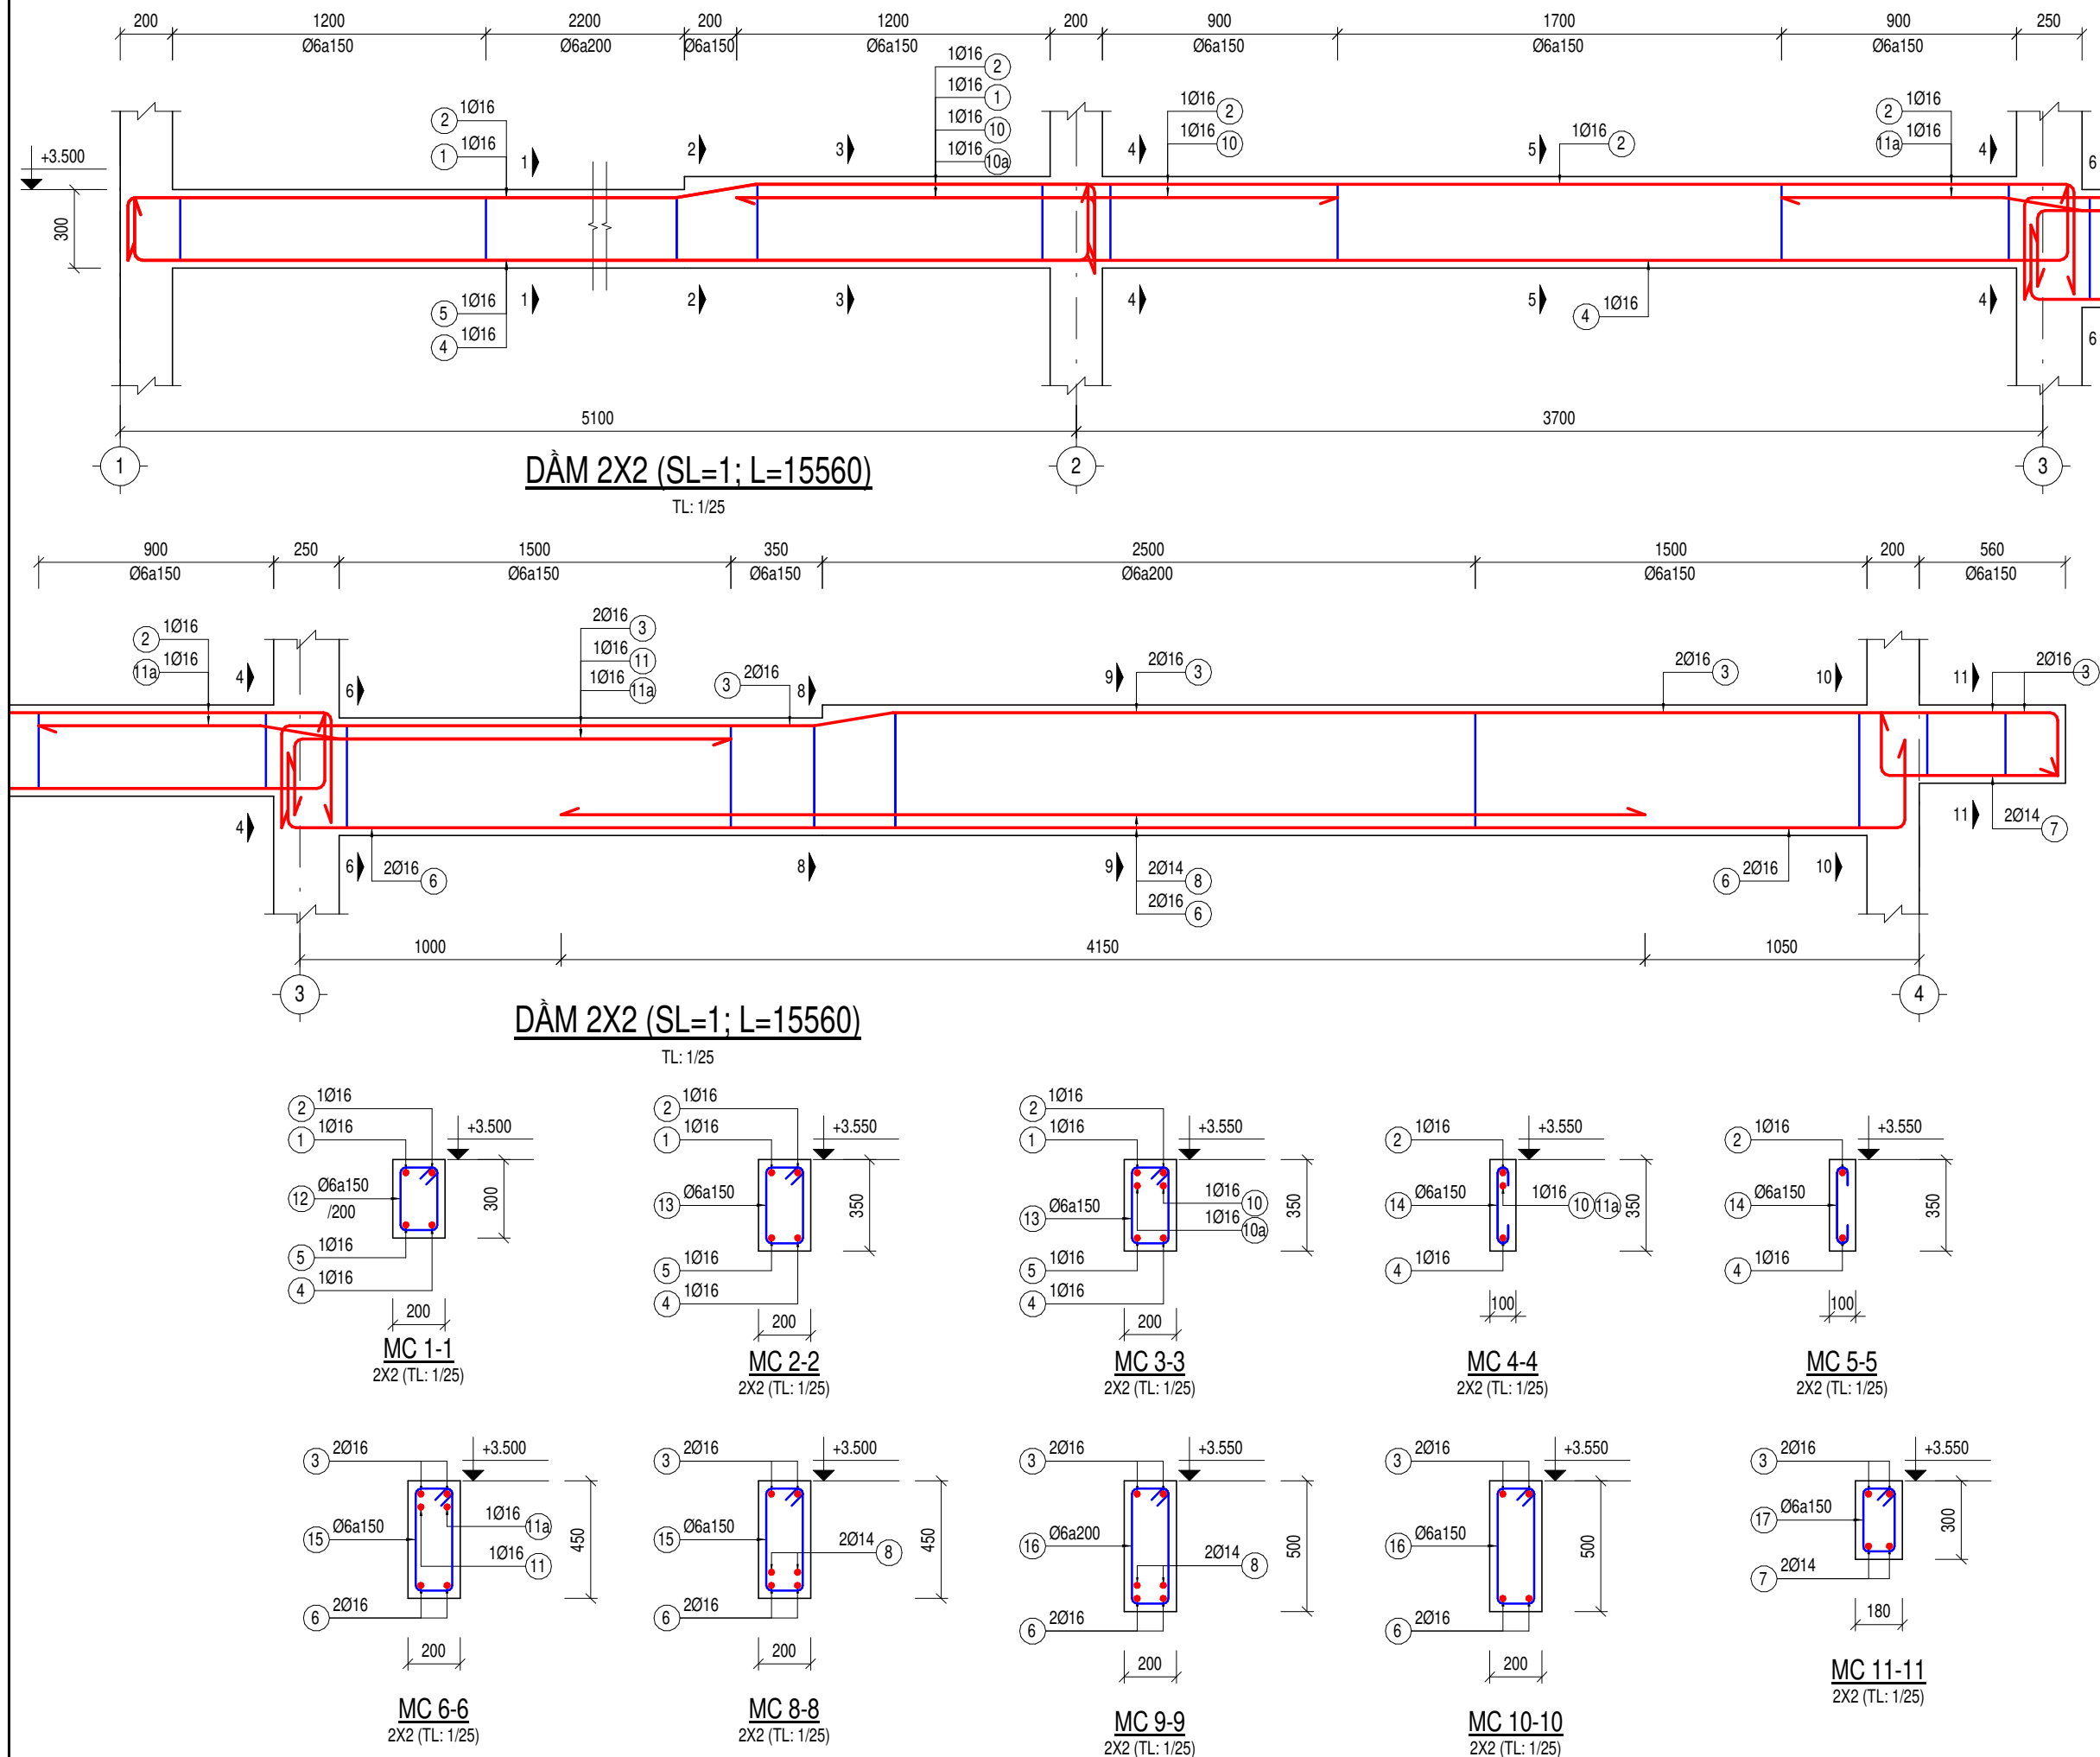

**GHI CHÚ:**

- CÁC ĐƠN VỊ TÀI CÔNG PHẢI PHỐI HỢP BẢN VẼ CỦA TẤT CẢ CÁC BỘ MÔN KHÁC NHAU THỰC SỰ KHÁC BIỆT PHẢI ĐÁP HỢP CÁC ĐƠN VỊ THIẾT KẾ ĐỂ XỬ LÝ.
- KHI XỬ LÝ SỰ KHÁC BIỆT, PHẢI THỰC HIỆN VU TIỀN THEO THỦ TỤC GIỮA CÁC BỘ MÔN: KIẾN TRÚC → KẾT CẤU / BỘ MÔN KHÁC; HOẶC ƯU TIÊN TRONG CÙNG BỘ MÔN: CHỈ THIẾT → TÔNG THÉ
- CÁC SỐ LIỆU KÍCH THƯỚC PHẢI ĐƯỢC KIỂM TRA THỰC TẾ TẠI CÔNG TRÌNH, NEU THỰC SỰ KHÁC BIỆT SƠ VỚI BẢN VẼ THIẾT KẾ PHẢI ĐÁP HỢP CÁC ĐƠN VỊ THIẾT KẾ.

|             |      |          |
|-------------|------|----------|
| HIỆU CHỈNH: |      |          |
| REV         | NGÀY | NỘI DUNG |

CHỦ ĐẦU TƯ:

CÔNG TY TNHH DẦU TƯ

**PHÚ VIỆT TÍN**

ĐỊA CHỈ: LÔ 18-19 QUỐC LỘ 1A, XÃ DẦU GIẤY,  
TỈNH ĐỒNG NAI, VIỆT NAM

CTHĐTV ĐẶNG PHƯỚC BÌNH

ĐƠN VỊ THIẾT KẾ:

CÔNG TY CỔ PHẦN TƯ VẤN THIẾT KẾ

**BASE ARC**

ĐỊA CHỈ: 138 ĐIỆN BIÊN PHỦ, PHƯỜNG TÂN ĐỊNH,  
TP. HỒ CHÍ MINH, VIỆT NAM

TỔNG GIÁM ĐỐC TRẦN ĐỨC AN

|                  |  |
|------------------|--|
| CHỦ NHIỆM DỰ ÁN: |  |
|------------------|--|

KTS. NGUYỄN THÀNH THÁI

|                   |  |
|-------------------|--|
| CHỦ TRÌ THIẾT KẾ: |  |
|-------------------|--|

KS. NGÔ TÙNG THÀNH

THIẾT KẾ:

\_\_\_\_\_

|                          |  |
|--------------------------|--|
| KS. NGUYEN MINH DUY BANG |  |
| KIỂM TRA                 |  |

|           |  |
|-----------|--|
| RIEM TRA. |  |
|-----------|--|

KS. NGÔ TÙNG THÀNH

DỰ ÁN:

KHU DẪN CƯ A1-C1 (ĐÔ THỊ DẦU GIẤY)

ĐỊA ĐIỂM: XÃ DẦU GIẤY, TỈNH ĐỒNG NAI

CÔNG TRÌNH:

### 3.1.2. $\lambda_1 = 2$ and $\lambda_2 = 1$

NHÀ ỦY THƯỜNG MẠI LIÊN KẾ

HANG MUC:

MÃ LƯU HÀNH T2 2b

WISCONSIN\_20

TÊN BẢN VẼ:

CHI TIẾT DẦM TẦNG 2-04

\_\_\_\_\_

**MỤC ĐÍCH PHÁT HÀNH:**

|                 |
|-----------------|
| BẢN VỀ MỜI THẦU |
|-----------------|

|   |                |
|---|----------------|
|   | THIẾT KẾ CƠ SỞ |
| 1 | Thiết kế cơ sở |


|   |                          |
|---|--------------------------|
| ▼ | THIẾT KẾ BẢN VẼ THI CÔNG |
|   | BẢN VẼ HOÀN CÔNG         |

|            |         |
|------------|---------|
| HOÀN THÀNH | 07/2025 |
|------------|---------|

|           |         |
|-----------|---------|
| NGÀY THAM | 07/2020 |
| TỶ LỆ     | NTS     |


|                |       |
|----------------|-------|
| SỐ QUÂN BẢO VỆ | KC 26 |
|----------------|-------|



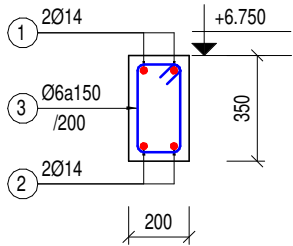


**DÀM 3Y5 (SL=1; L=4000)**

TL: 1/25

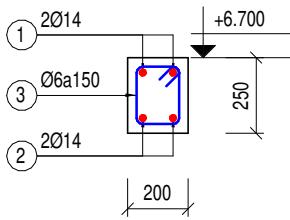

**DÀM 3D1 (SL=4; L=1250)**

TL: 1/25

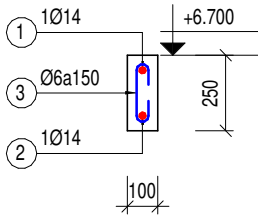

**DÀM 3D2 (SL=2; L=2800)**

TL: 1/25

**GHI CHÚ:**

- CÁC ĐƠN VỊ THI CÔNG PHẢI PHỐI HỢP BẢN VẼ CỦA TẤT CẢ CÁC BỘ MÔN KHÁC NẾU THẤY SỰ KHÁC BIỆT PHẢI BẢO CHO ĐƠN VỊ THIẾT KẾ ĐỂ XỬ LÝ.
- KHI XỬ LÝ SỰ KHÁC BIỆT, PHẢI THỰC HIỆN ƯU TIÊN THEO THỨ TỰ GIỮA CÁC BỘ MÔN: KIẾN TRÚC → KẾT CẤU / BỘ MÔN KHÁC; HOẶC ƯU TIÊN TRONG CÙNG BỘ MÔN: CHI TIẾT → TỔNG THỂ
- CÁC SỐ LIỆU KÍCH THƯỚC PHẢI ĐƯỢC KIỂM TRA THỰC TẾ TẠI CÔNG TRÌNH, NẾU THẤY SỰ KHÁC BIỆT SƠ VỚI BẢN VẼ THI PHẢI BẢO CHO ĐƠN VỊ THIẾT KẾ.

**HIỆU CHỈNH:**

| REV | NGÀY | NỘI DUNG |
|-----|------|----------|
|-----|------|----------|

**CHỦ ĐẦU TƯ:**

CÔNG TY TNHH ĐẦU TƯ

**PHÚ VIỆT TÍN**

ĐỊA CHỈ: LÔ 18-19 QUỐC LỘ 1A, XÃ DẦU GIẤY,  
TỈNH ĐỒNG NAI, VIỆT NAM

CTHĐT

ĐẠNG PHƯỚC BÌNH

**ĐƠN VỊ THIẾT KẾ:**

CÔNG TY CỔ PHẦN TƯ VẤN THIẾT KẾ

**BASE ARC**

ĐỊA CHỈ: 138 ĐIỆN BIÊN PHỦ, PHƯỜNG TÂN ĐỊNH,  
TP. HỒ CHÍ MINH, VIỆT NAM

**TỔNG GIÁM ĐỐC**

TRẦN ĐỨC AN

**CHỦ NHIỆM DỰ ÁN:**

KTS. NGUYỄN THÀNH THÁI

**CHỦ TRÌ THIẾT KẾ:**

KS. NGÔ TÙNG THÀNH

**THIẾT KẾ:**

KS. NGUYỄN MINH DUY BẰNG

**KIỂM TRA:**

KS. NGÔ TÙNG THÀNH

**DỰ ÁN:**

KHU DÂN CƯ A1-C1 (ĐÔ THỊ DẦU GIẤY)

ĐỊA ĐIỂM: XÃ DẦU GIẤY, TỈNH ĐỒNG NAI

**CÔNG TRÌNH:**

NHÀ Ở THƯƠNG MẠI LIÊN KẾ

**HẠNG MỤC:**

MẪU NHÀ T3\_2b

**TÊN BẢN VẼ:**

CHI TIẾT DÀM TẦNG 3-02


**MỤC ĐÍCH PHÁT HÀNH:**

|                                     |                          |
|-------------------------------------|--------------------------|
| <input type="checkbox"/>            | BẢN VẼ MỜI THẦU          |
| <input type="checkbox"/>            | THIẾT KẾ CƠ SỞ           |
| <input checked="" type="checkbox"/> | THIẾT KẾ BẢN VẼ THI CÔNG |
| <input type="checkbox"/>            | BẢN VẼ HOÀN CÔNG         |

HOÀN THÀNH 07/2025


TỶ LỆ NTS

SỐ HIỆU BẢN VẼ KC-38

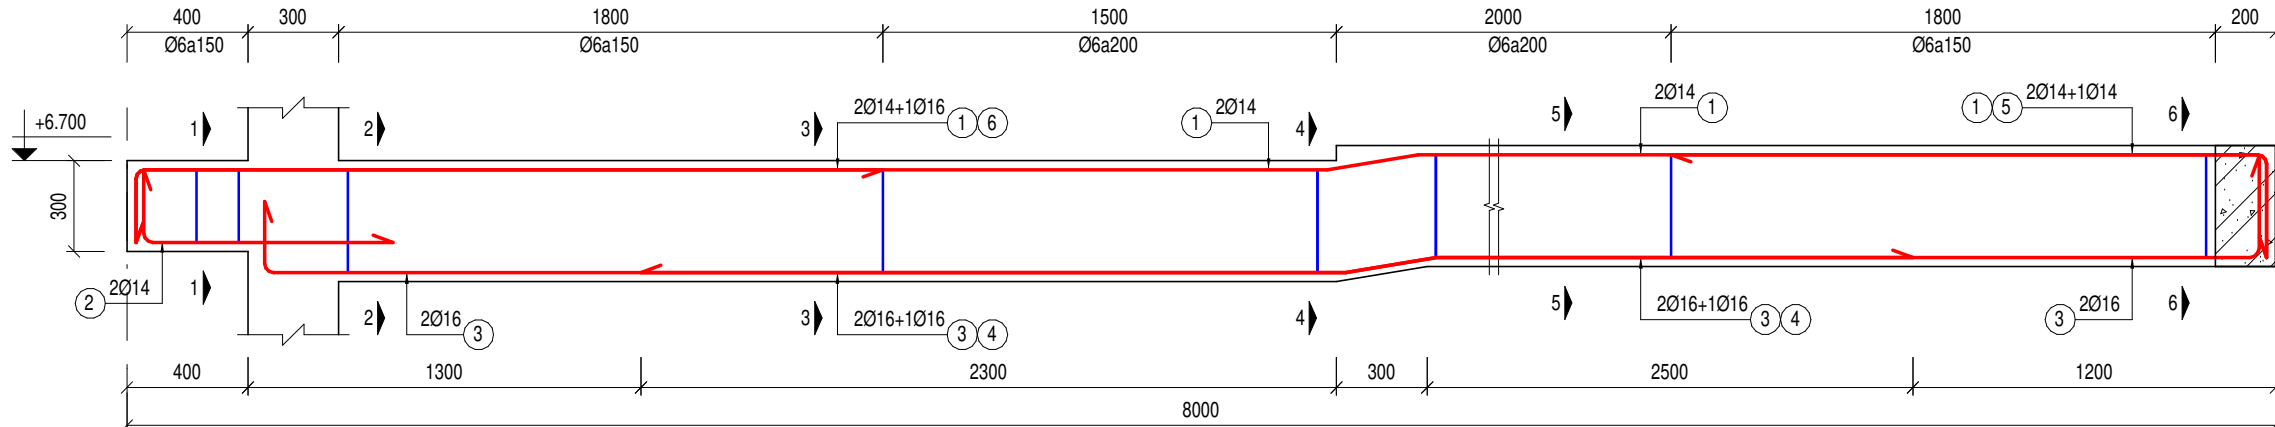


**DÀM 3Y4 (SL=1; L=8000)**


TL: 1/25

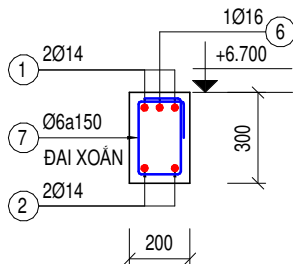


**MC 1-1**  
3Y4 (TL: 1/25)

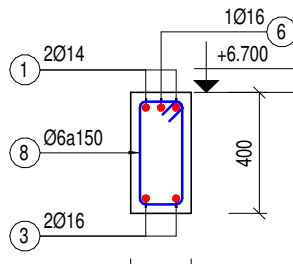


**MC 2-2**  
3Y4 (TL: 1/25)

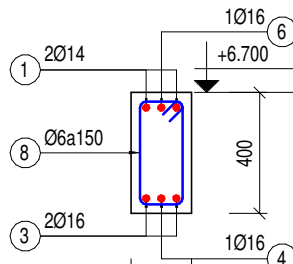


**MC 3-3**  
3Y4 (TL: 1/25)

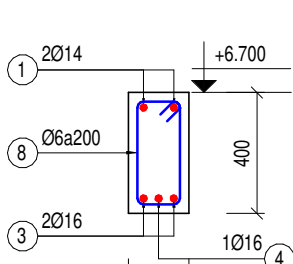

**MC 4-4**  
3Y4 (TL: 1/25)

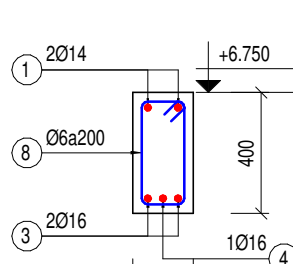

**MC 5-5**  
3Y4 (TL: 1/25)

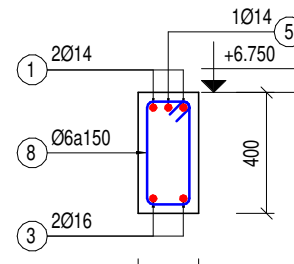

**MC 6-6**  
3Y4 (TL: 1/25)







**DÀM MX1 (SL=1; L=8900)**  
TL: 1/25

**DÀM MX2 (SL=1; L=5200)**  
TL: 1/25

**DÀM MX3 (SL=1; L=15560)**  
TL: 1/25

**DÀM MX3-4**  
TL: 1/25

**DÀM MX4 (SL=1; L=6300)**  
TL: 1/25

**DÀM MY1 (SL=1; L=8000)**  
TL: 1/25

**DÀM MY2 (SL=1; L=8000)**  
TL: 1/25

**DÀM MY4 (SL=1; L=4000)**  
TL: 1/25

**DÀM MY5 (SL=1; L=2400)**  
TL: 1/25

**DÀM MY6 (SL=1; L=4000)**  
TL: 1/25

**DÀM DM1 (SL=1; L=8900)**  
TL: 1/25

**DÀM DM2 (SL=1; L=4200)**  
TL: 1/25

**DÀM DM3 (SL=1; L=6300)**  
TL: 1/25

**DÀM DM4 (SL=1; L=4000)**  
TL: 1/25

**DÀM GT1 (SL=1; L=15000)**  
TL: 1/25

**DÀM GT2 (SL=1; L=8500)**  
TL: 1/25

**TAI GỒI ĐOAN MY3-1**  
TL: 1/25

**TAI NHIP ĐOAN MY3-1**  
TL: 1/25

**ĐOAN MY3-2**  
TL: 1/25

**DÀM MY3 (SL=1; L=8000)**  
TL: 1/25

**DÀM M1 (SL=1; L=11700)**  
TL: 1/25

**GHI CHÚ:**

- CÁC ĐƠN VỊ THI CÔNG PHẢI PHỐI HỢP BẢN VẼ CỦA TẤT CẢ CÁC BỘ MÔN KHÁC NẾU THẤY SỰ KHÁC BIỆT PHẢI BẢO CHỨNG CHO ĐƠN VỊ THIẾT KẾ ĐỂ XỬ LÝ.
- KHI XỬ LÝ SỰ KHÁC BIỆT, PHẢI THỰC HIỆN ƯU TIÊN THEO THỨ TỰ GIỮA CÁC BỘ MÔN: KIẾN TRÚC → KẾT CẤU / BỘ MÔN KHÁC; HOẶC ƯU TIÊN TRONG CÙNG BỘ MÔN: CHI TIẾT → TỔNG THỂ
- CÁC SỐ LIỆU KÍCH THƯỚC PHẢI ĐƯỢC KIỂM TRA THỰC TẾ TẠI CÔNG TRÌNH, NẾU THẤY SỰ KHÁC BIỆT SƠ VỚI BẢN VẼ THI PHẢI BẢO CHỨNG ĐƠN VỊ THIẾT KẾ.

| HIỆU CHỈNH: |      |          |
|-------------|------|----------|
| REV         | NGÀY | NỘI DUNG |
|             |      |          |

CHỦ ĐẦU TƯ:

CÔNG TY TNHH ĐẦU TƯ

**PHÚ VIỆT TÍN**

ĐỊA CHỈ: LÔ 18-19 QUỐC LỘ 1A, XÃ DẦU GIẤY, TỈNH ĐỒNG NAI, VIỆT NAM

CTHĐT

ĐẠNG PHƯỚC BÌNH

ĐƠN VỊ THIẾT KẾ:

CÔNG TY CỔ PHẦN TƯ VẤN THIẾT KẾ

**BASE ARC**

ĐỊA CHỈ: 138 ĐIỆN BIÊN PHỦ, PHƯỜNG TÂN ĐỊNH, TP. HỒ CHÍ MINH, VIỆT NAM

TỔNG GIÁM ĐỐC

TRẦN ĐỨC AN

CHỦ NHIỆM DỰ ÁN:

KTS. NGUYỄN THÀNH THÁI

CHỦ TRÌ THIẾT KẾ:

KS. NGÔ TÙNG THÀNH

THIẾT KẾ:

KS. NGUYỄN MINH DUY BẰNG

KIỂM TRA:

KS. NGÔ TÙNG THÀNH

DỰ ÁN:

KHU DÂN CƯ A1-C1 (ĐÔ THỊ DẦU GIẤY)

ĐỊA ĐIỂM: XÃ DẦU GIẤY, TỈNH ĐỒNG NAI

CÔNG TRÌNH:

NHÀ Ở THƯƠNG MẠI LIÊN KẾ

HẠNG MỤC:

MẪU NHÀ T3\_2b



TÊN BẢN VẼ:

CHI TIẾT DÀM MÁI


MỤC ĐÍCH PHÁT HÀNH:

|                                     |                          |
|-------------------------------------|--------------------------|
| <input type="checkbox"/>            | BẢN VẼ MỜI THẦU          |
| <input type="checkbox"/>            | THIẾT KẾ CƠ SỞ           |
| <input checked="" type="checkbox"/> | THIẾT KẾ BẢN VẼ THI CÔNG |
| <input type="checkbox"/>            | BẢN VẼ HOÀN CÔNG         |


|                |         |
|----------------|---------|
| HOÀN THÀNH     | 07/2025 |
| TỶ LỆ          | NTS     |
| SỐ HIỆU BẢN VẼ | KC-42   |

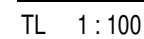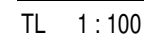

KC-43

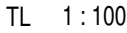


|                |       |
|----------------|-------|
| SỐ HIỆU BAN VE | KC-44 |
|----------------|-------|

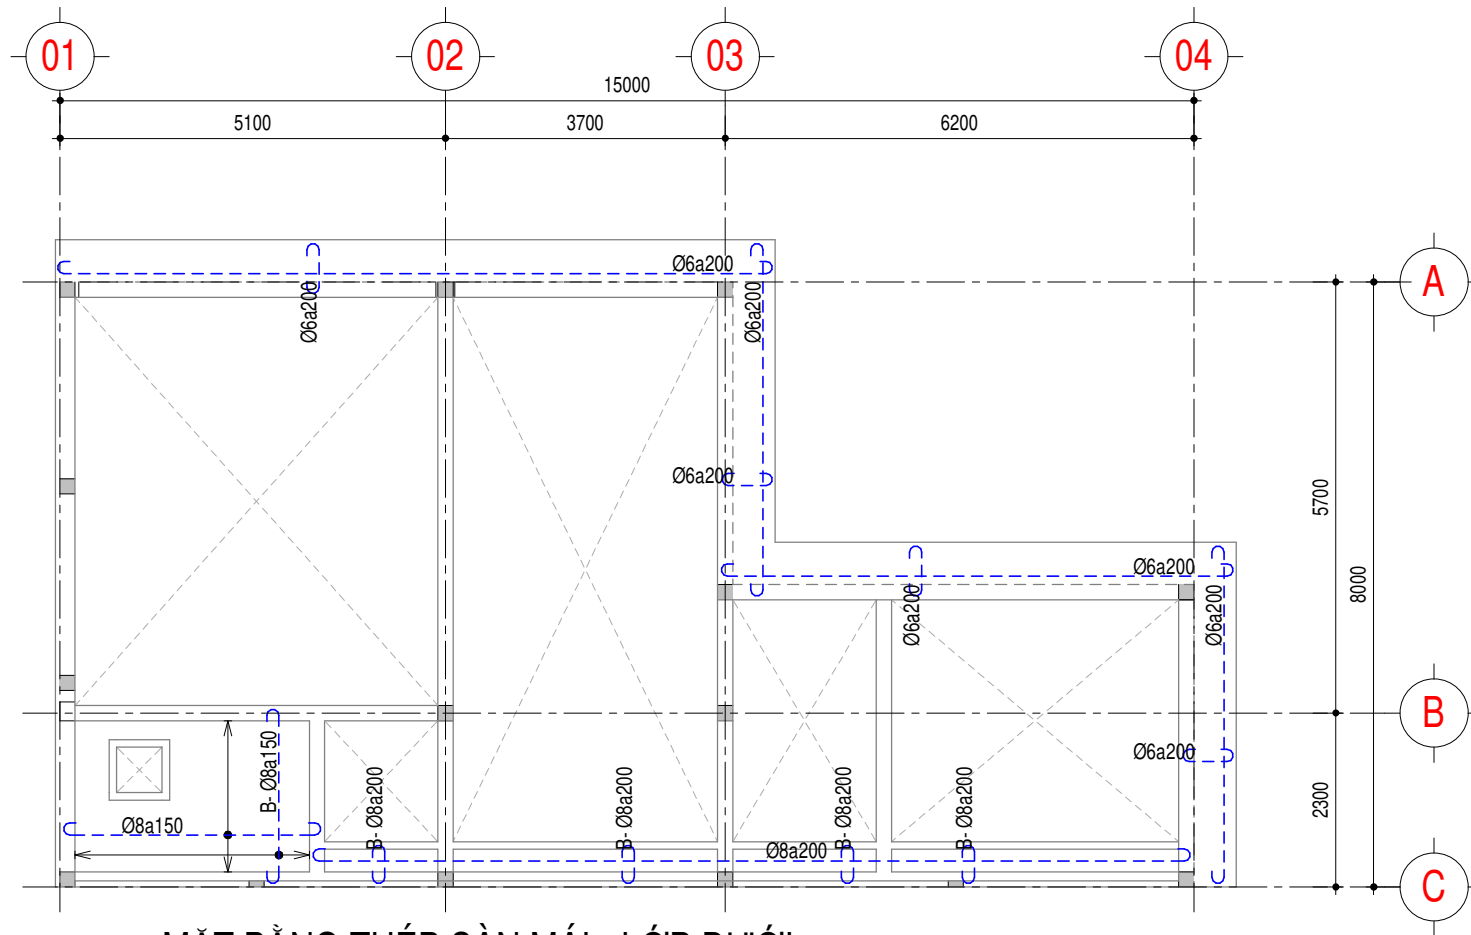

MẶT BẰNG THÉP SÀN MÁI - LỚP DƯỚI

TL 1:100

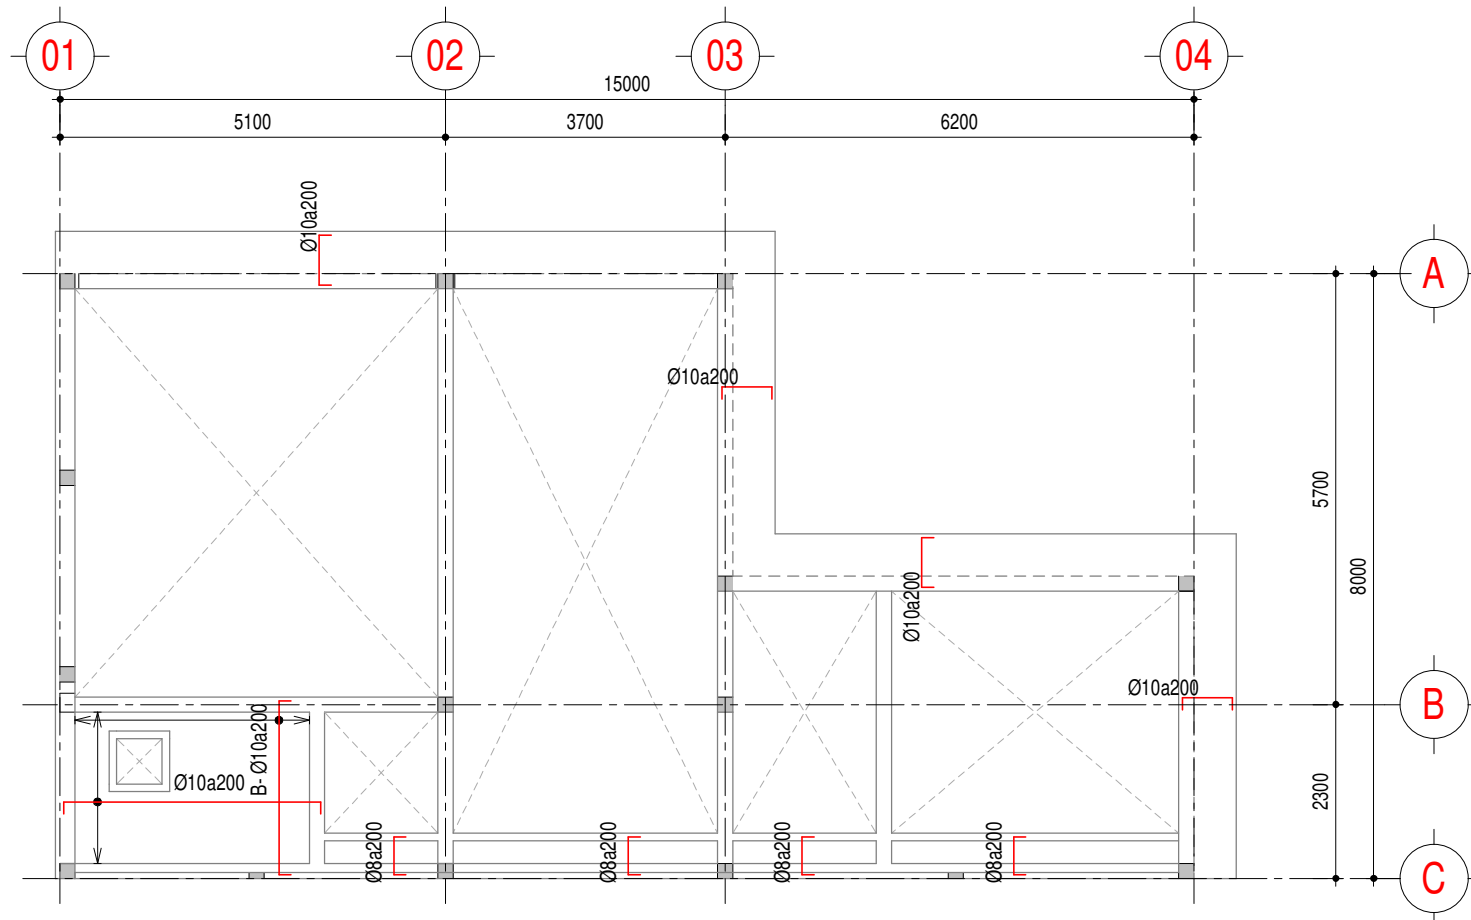

MẶT BẰNG THÉP SÀN MÁI - LỚP TRÊN

TL 1:100

GHI CHÚ:

- CÁC ĐƠN VỊ THI CÔNG PHẢI PHỐI HỢP BẢN VẼ CỦA TẤT CẢ CÁC BỘ MÔN KHÁC NẾU THẤY SỰ KHÁC BIỆT PHẢI BÁO CHO ĐƠN VỊ THIẾT KẾ ĐỂ XỬ LÝ.
- KHI XỬ LÝ SỰ KHÁC BIỆT, PHẢI THỰC HIỆN ƯU TIÊN THEO THỨ TỰ GIỮA CÁC BỘ MÔN: KIẾN TRÚC → KẾT CẤU / BỘ MÔN KHÁC; HOẶC ƯU TIÊN TRONG CÙNG BỘ MÔN: CHI TIẾT → TỔNG THỂ
- CÁC SỐ LƯỢNG KỊCH THUỘC PHẢI ĐƯỢC KIỂM TRA THỰC TẾ TẠI CÔNG TRÌNH, NẾU THẤY SỰ KHÁC BIỆT SƠ VỚI BẢN VẼ THI PHẢI BÁO CHO ĐƠN VỊ THIẾT KẾ.

HIỆU CHỈNH:

| REV | NGÀY | NỘI DUNG |
|-----|------|----------|
|-----|------|----------|

CHỦ ĐẦU TƯ:

CÔNG TY TNHH ĐẦU TƯ

**PHÚ VIỆT TÍN**

ĐỊA CHỈ: LÔ 18-19 QUỐC LỘ 1A, XÃ DẦU GIẤY,  
TỈNH ĐỒNG NAI, VIỆT NAM

CTHĐT

ĐẠNG PHƯỚC BÌNH

ĐƠN VỊ THIẾT KẾ:

CÔNG TY CỔ PHẦN TƯ VẤN THIẾT KẾ

**BASE ARC**

ĐỊA CHỈ: 138 ĐIỆN BIÊN PHỦ, PHƯỜNG TÂN ĐỊNH,  
TP. HỒ CHÍ MINH, VIỆT NAM

TỔNG GIÁM ĐỐC

TRẦN ĐỨC AN

CHỦ NHIỆM DỰ ÁN:

KTS. NGUYỄN THÀNH THÁI

CHỦ TRÌ THIẾT KẾ:

KS. NGÔ TÙNG THÀNH

THIẾT KẾ:

KS. NGUYỄN MINH DUY BẰNG

KIỂM TRA:

KS. NGÔ TÙNG THÀNH

DỰ ÁN:

KHU DÂN CƯ A1-C1 (ĐÔ THỊ DẦU GIẤY)

ĐỊA ĐIỂM: XÃ DẦU GIẤY, TỈNH ĐỒNG NAI

CÔNG TRÌNH:

NHÀ Ở THƯƠNG MẠI LIÊN KẾ

HẠNG MỤC:

MẪU NHÀ T3\_2b

TÊN BẢN VẼ:

MẶT BẰNG THÉP SÀN MÁI, ĐÌNH MÁI

MỤC ĐÍCH PHÁT HÀNH:

|                                     |                          |
|-------------------------------------|--------------------------|
| <input type="checkbox"/>            | BẢN VẼ MỜI THẦU          |
| <input type="checkbox"/>            | THIẾT KẾ CƠ SỞ           |
| <input checked="" type="checkbox"/> | THIẾT KẾ BẢN VẼ THI CÔNG |
| <input type="checkbox"/>            | BẢN VẼ HOÀN CÔNG         |

HOÀN THÀNH

07/2025

TỶ LỆ

NTS

SỐ HIỆU BẢN VẼ

KC-45

GHI CHÚ:  
- CÁC ĐƠN VỊ THI CÔNG PHẢI PHỐI HỢP BẢN VẼ CỦA TẤT CẢ CÁC BỘ MÔN KHÁC NẾU THẤY SỰ KHÁC BIỆT PHẢI BẢO CHO ĐƠN VỊ THIẾT KẾ XỬ LÝ.  
- KHI XỬ LÝ SỰ KHÁC BIỆT, PHẢI THỰC HIỆN ƯU TIÊN THEO THỨ TỰ GIỮA CÁC BỘ MÔN: KIẾN TRÚC → KẾT CẤU / BỘ MÔN KHÁC; HOẶC ƯU TIÊN TRONG CÙNG BỘ MÔN: CHI TIẾT → TỔNG THỂ  
- CÁC SỐ LIỆU KÍCH THƯỚC PHẢI ĐƯỢC KIỂM TRA THỰC TẾ TẠI CÔNG TRÌNH, NẾU THẤY SỰ KHÁC BIỆT SƠ VỚI BẢN VẼ THI PHẢI BẢO CHO ĐƠN VỊ THIẾT KẾ.

HIỆU CHỈNH:

| REV | NGÀY | NỘI DUNG |
|-----|------|----------|
|-----|------|----------|

CHỦ ĐẦU TƯ:  
CÔNG TY TNHH ĐẦU TƯ  
**PHÚ VIỆT TÍN**  
ĐỊA CHỈ: LÔ 18-19 QUỐC LỘ 1A, XÃ DẦU GIẤY,  
TỈNH ĐỒNG NAI, VIỆT NAM

CTHĐTV ĐẠNG PHƯỚC BÌNH

ĐƠN VỊ THIẾT KẾ:  
CÔNG TY CỔ PHẦN TƯ VẤN THIẾT KẾ  
**BASE ARC**  
ĐỊA CHỈ: 138 ĐIỆN BIÊN PHỦ, PHƯỜNG TÂN ĐỊNH,  
TP. HỒ CHÍ MINH, VIỆT NAM

TỔNG GIÁM ĐỐC TRẦN ĐỨC AN

CHỦ NHIỆM DỰ ÁN:

KTS. NGUYỄN THÀNH THÁI

CHỦ TRÌ THIẾT KẾ:

KS. NGÔ TÙNG THÀNH

THIẾT KẾ:

KS. NGUYỄN MINH DUY BẰNG

KIỂM TRA:

KS. NGÔ TÙNG THÀNH

DỰ ÁN:

KHU DÂN CƯ A1-C1 (ĐÔ THỊ DẦU GIẤY)

ĐỊA ĐIỂM: XÃ DẦU GIẤY, TỈNH ĐỒNG NAI

CÔNG TRÌNH:

NHÀ Ở THƯƠNG MẠI LIÊN KẾ

HẠNG MỤC:

MẪU NHÀ T3\_2b

TÊN BẢN VẼ:

MẶT BẰNG CẦU THANG


MỤC ĐÍCH PHÁT HÀNH:

|                                     |                          |
|-------------------------------------|--------------------------|
| <input type="checkbox"/>            | BẢN VẼ MỜI THẦU          |
| <input type="checkbox"/>            | THIẾT KẾ CƠ SỞ           |
| <input checked="" type="checkbox"/> | THIẾT KẾ BẢN VẼ THI CÔNG |
| <input type="checkbox"/>            | BẢN VẼ HOÀN CÔNG         |

HOÀN THÀNH 07/2025


TỶ LỆ NTS

SỐ HIỆU BẢN VẼ KC-46

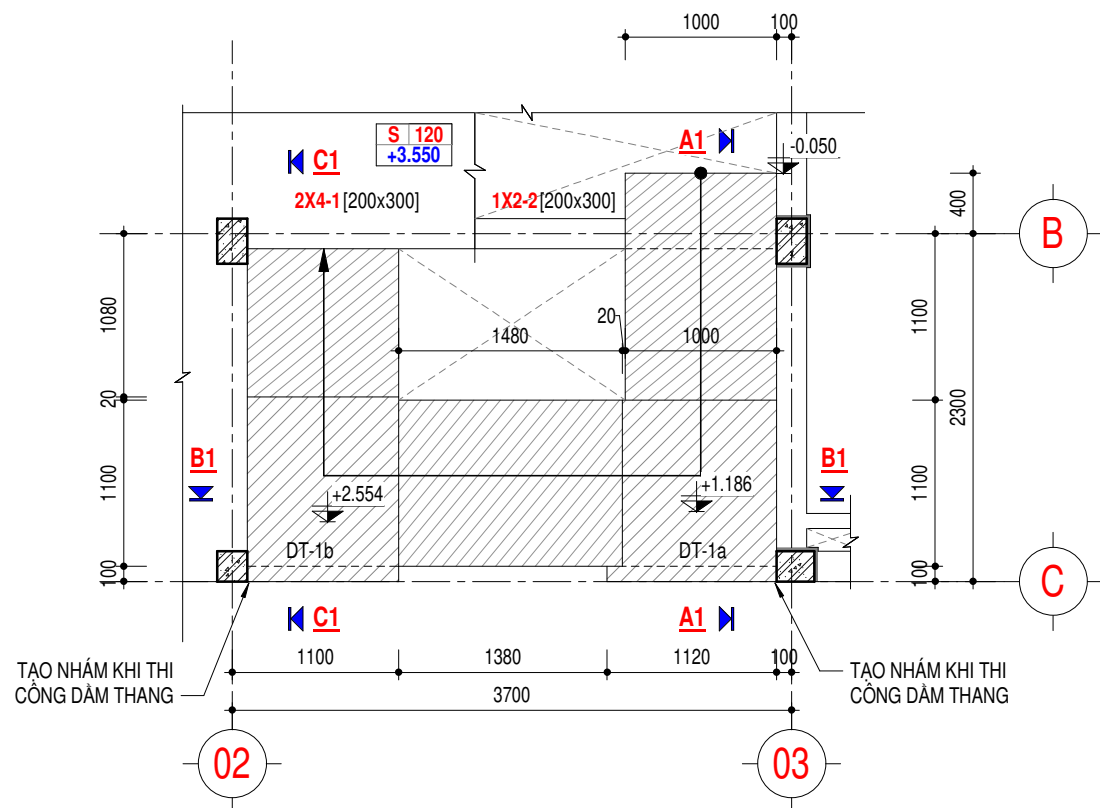


**MẶT BẰNG CẦU THANG TẦNG 1 - TẦNG 2**

TL 1 : 50

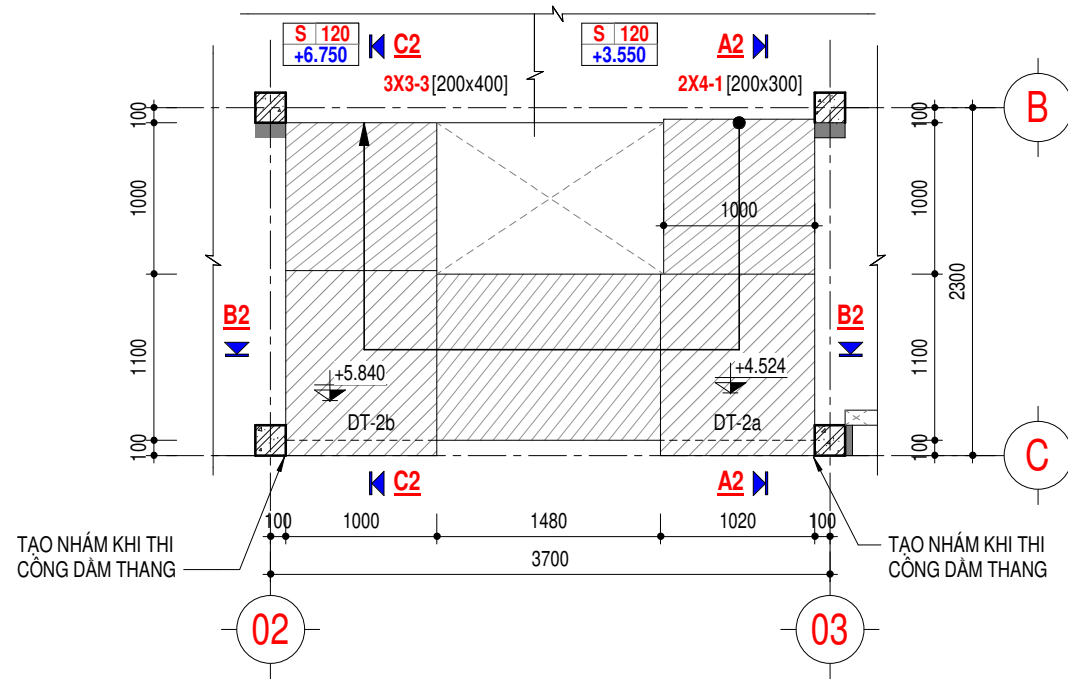


**MẶT BẰNG CẦU THANG TẦNG 2 - TẦNG 3**

TL 1 : 50

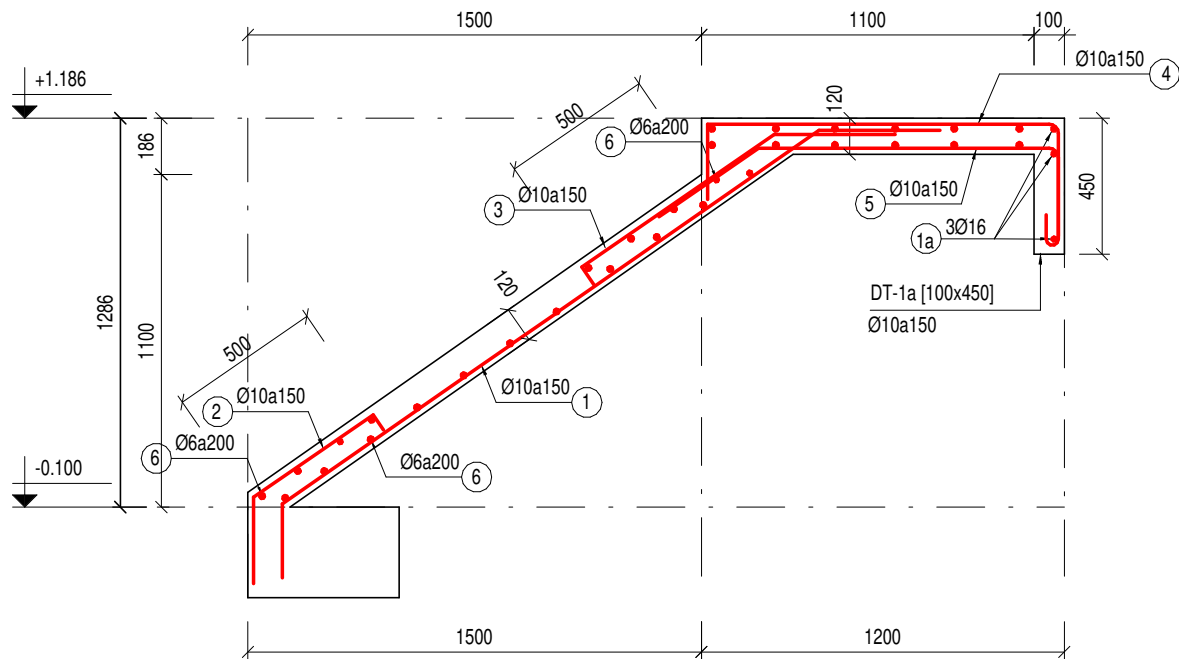


MC A1-A1

TL: 1/25

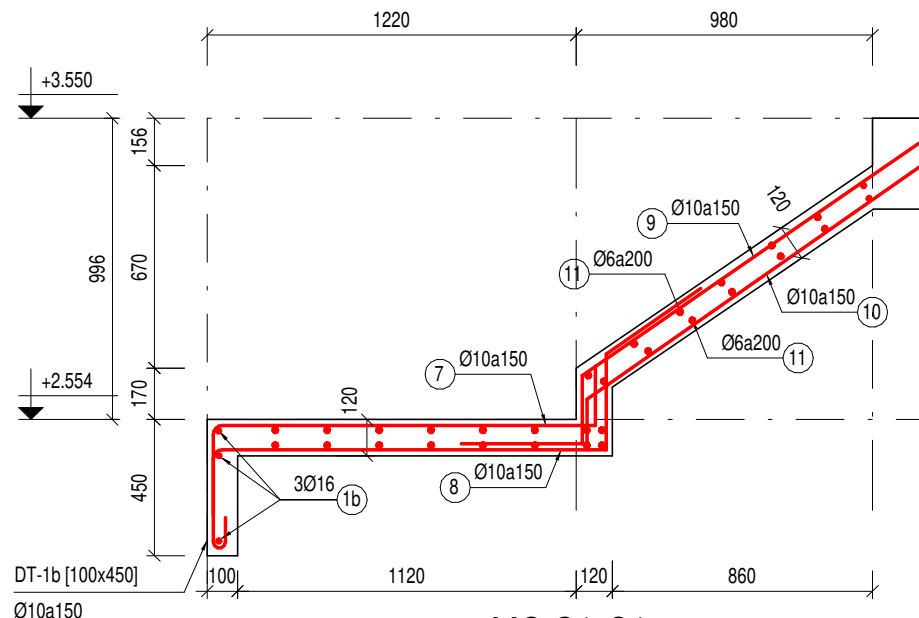

MC C1-C1

TL: 1/25

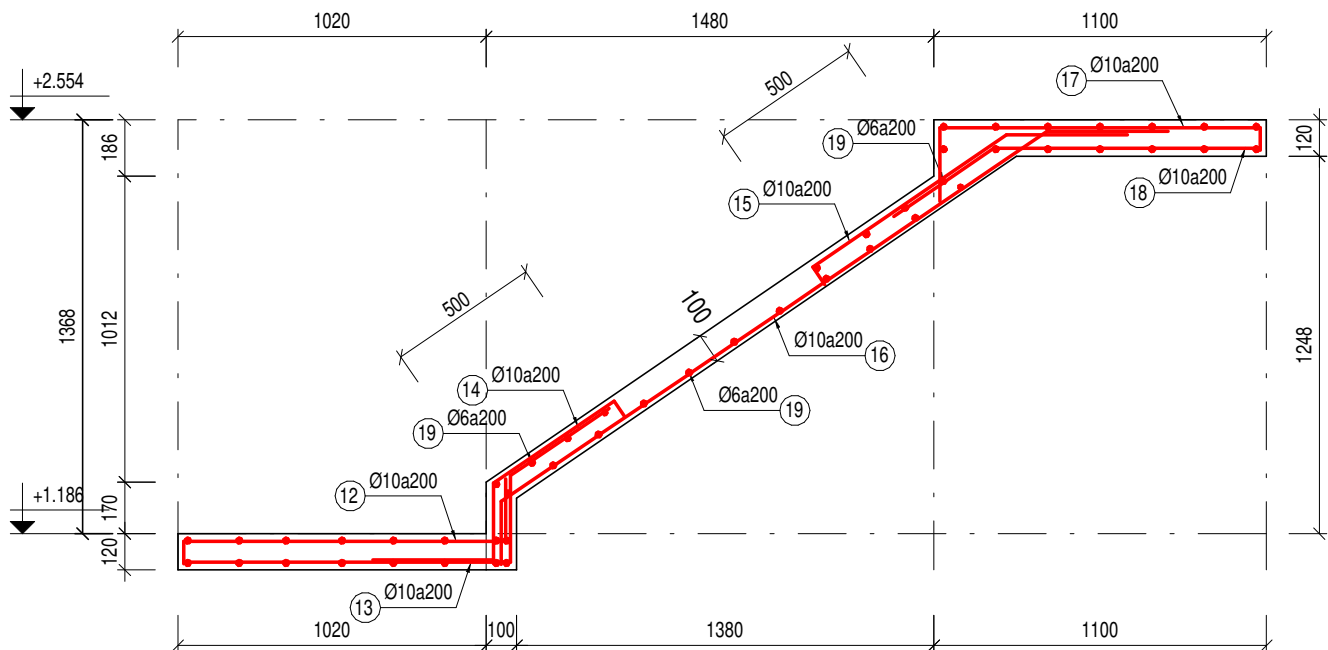

MC B1-B1

TL: 1/25

GHI CHÚ:

- CÁC ĐƠN VỊ THI CÔNG PHẢI PHỐI HỢP BẢN VẼ CỦA TẤT CẢ CÁC BỘ MÔN KHÁC NẾU THẤY SỰ KHÁC BIỆT PHẢI BÁO CHO ĐƠN VỊ THIẾT KẾ ĐỂ XỬ LÝ.
- KHI XỬ LÝ SỰ KHÁC BIỆT, PHẢI THỰC HIỆN ƯU TIÊN THEO THỨ TỰ GIỮA CÁC BỘ MÔN: KIẾN TRÚC → KẾT CẤU / BỘ MÔN KHÁC; HOẶC ƯU TIÊN TRONG CÙNG BỘ MÔN: CHI TIẾT → TỔNG THỂ
- CÁC SỐ LƯỢNG KỊCH THUỘC PHẢI ĐƯỢC KIỂM TRA THỰC TẾ TẠI CÔNG TRÌNH, NẾU THẤY SỰ KHÁC BIỆT SƠ VỚI BẢN VẼ THI PHẢI BÁO CHO ĐƠN VỊ THIẾT KẾ.

HIỆU CHỈNH:

| REV | NGÀY | NỘI DUNG |
|-----|------|----------|
|-----|------|----------|

CHỦ ĐẦU TƯ:

CÔNG TY TNHH ĐẦU TƯ  
**PHÚ VIỆT TÍN**  
ĐỊA CHỈ: LÔ 18-19 QUỐC LỘ 1A, XÃ DẦU GIẤY,  
TỈNH ĐỒNG NAI, VIỆT NAM

CTHĐT

ĐẠNG PHƯỚC BÌNH

ĐƠN VỊ THIẾT KẾ:

CÔNG TY CỔ PHẦN TƯ VẤN THIẾT KẾ  
**BASE ARC**  
ĐỊA CHỈ: 138 ĐIỆN BIÊN PHỦ, PHƯỜNG TÂN ĐỊNH,  
TP. HỒ CHÍ MINH, VIỆT NAM

TỔNG GIÁM ĐỐC

TRẦN ĐỨC AN

CHỦ NHIỆM DỰ ÁN:

KTS. NGUYỄN THÀNH THÁI

CHỦ TRÌ THIẾT KẾ:

KS. NGÔ TÙNG THÀNH

THIẾT KẾ:

KS. NGUYỄN MINH DUY BẰNG

KIỂM TRA:

KS. NGÔ TÙNG THÀNH

DỰ ÁN:

KHU DÂN CƯ A1-C1 (ĐÔ THỊ DẦU GIẤY)  
ĐỊA ĐIỂM: XÃ DẦU GIẤY, TỈNH ĐỒNG NAI

CÔNG TRÌNH:

NHÀ Ở THƯƠNG MẠI LIÊN KẾ

HẠNG MỤC:

MẪU NHÀ T3\_2b

TÊN BẢN VẼ:

CHI TIẾT CẦU THANG-01


MỤC ĐÍCH PHÁT HÀNH:

|                                     |                          |
|-------------------------------------|--------------------------|
| <input type="checkbox"/>            | BẢN VẼ MỜI THẦU          |
| <input type="checkbox"/>            | THIẾT KẾ CƠ SỞ           |
| <input checked="" type="checkbox"/> | THIẾT KẾ BẢN VẼ THI CÔNG |
| <input type="checkbox"/>            | BẢN VẼ HOÀN CÔNG         |

HOÀN THÀNH 07/2025


TỶ LỆ NTS

SỐ HIỆU BẢN VẼ KC-47

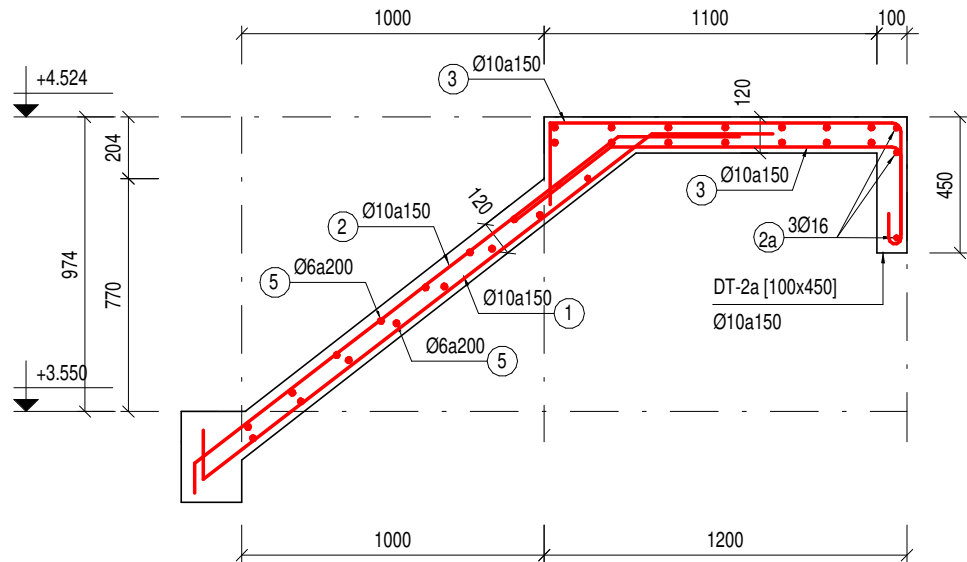


MC A2-A2

TL: 1/25

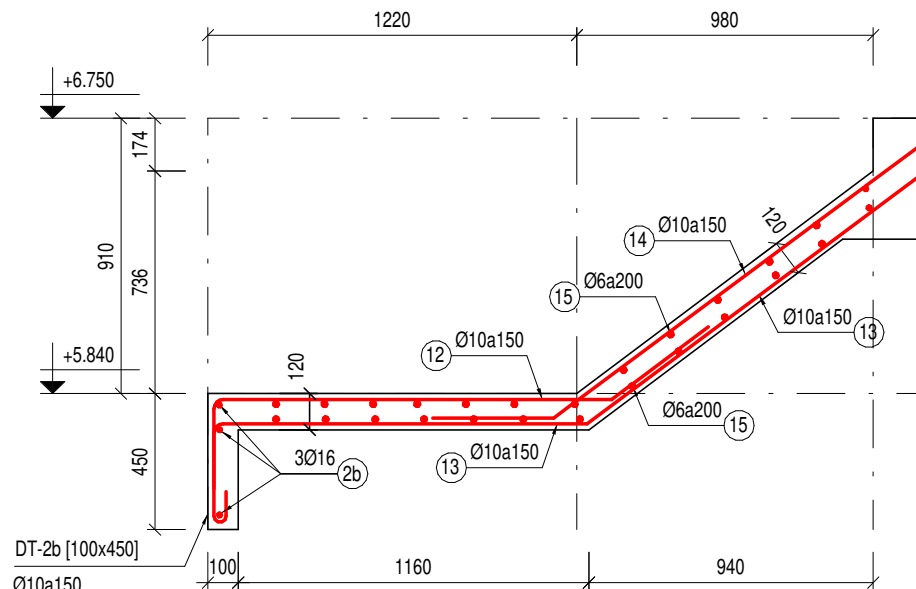

MC C2-C2

TL: 1/25

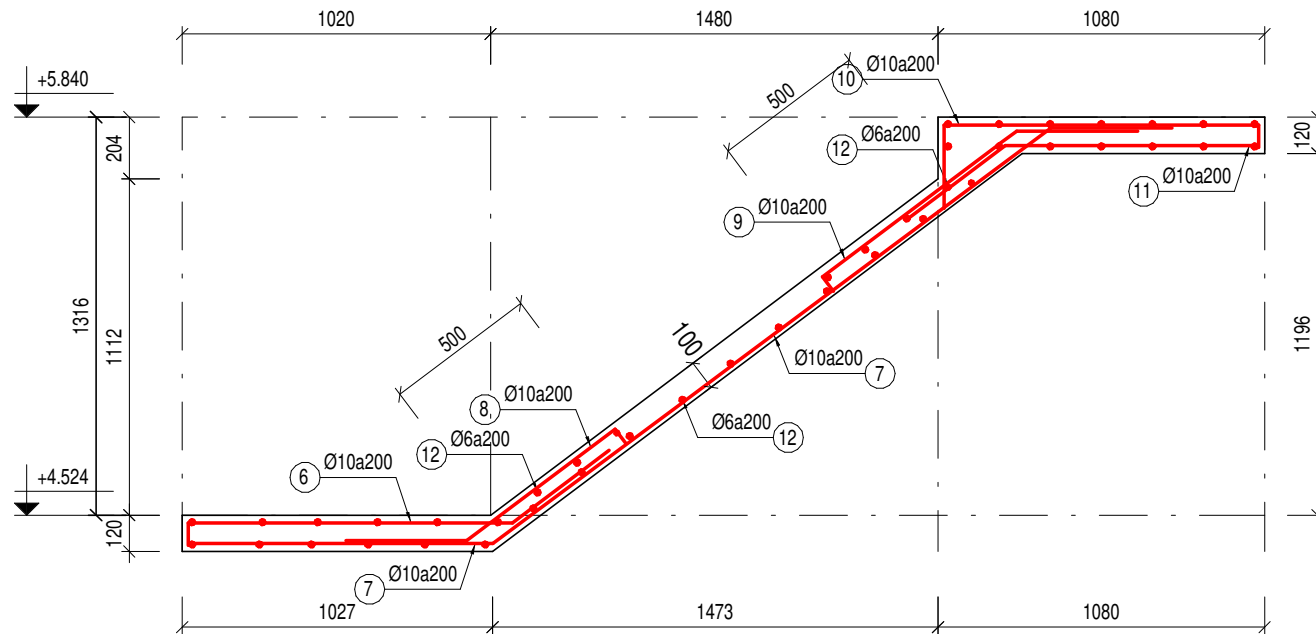

MC B2-B2

TL: 1/25

GHI CHÚ:  
- CÁC ĐƠN VỊ THI CÔNG PHẢI PHỐI HỢP BẢN VẼ CỦA TẤT CẢ CÁC BỘ MÔN KHÁC NẾU THẤY SỰ KHÁC BIỆT PHẢI BẢO CHỨNG ĐƠN VỊ THIẾT KẾ ĐỂ XỬ LÝ.  
- KHI XỬ LÝ SỰ KHÁC BIỆT, PHẢI THỰC HIỆN ƯU TIÊN THEO THỨ TỰ GIỮA CÁC BỘ MÔN: KIẾN TRÚC → KẾT CẤU / BỘ MÔN KHÁC; HOẶC ƯU TIÊN TRONG CÙNG BỘ MÔN: CHI TIẾT → TỔNG THỂ  
- CÁC SỐ LIỆU KÍCH THƯỚC PHẢI ĐƯỢC KIỂM TRA THỰC TẾ TẠI CÔNG TRÌNH, NẾU THẤY SỰ KHÁC BIỆT SƠ VỚI BẢN VẼ THI PHẢI BẢO CHỨNG ĐƠN VỊ THIẾT KẾ.

HIỆU CHỈNH:

| REV | NGÀY | NỘI DUNG |
|-----|------|----------|
|     |      |          |

CHỦ ĐẦU TƯ:  
CÔNG TY TNHH ĐẦU TƯ  
**PHÚ VIỆT TÍN**  
ĐỊA CHỈ: LÔ 18-19 QUỐC LỘ 1A, XÃ DẦU GIẤY,  
TỈNH ĐỒNG NAI, VIỆT NAM

CTHĐT V ĐẠNG PHƯỚC BÌNH

ĐƠN VỊ THIẾT KẾ:  
CÔNG TY CỔ PHẦN TƯ VẤN THIẾT KẾ  
**BASE ARC**  
ĐỊA CHỈ: 138 ĐIỆN BIÊN PHỦ, PHƯỜNG TÂN ĐỊNH,  
TP. HỒ CHÍ MINH, VIỆT NAM

TỔNG GIÁM ĐỐC TRẦN ĐỨC AN

CHỦ NHIỆM DỰ ÁN:

KTS. NGUYỄN THÀNH THÁI

CHỦ TRÌ THIẾT KẾ:

KS. NGÔ TÙNG THÀNH

THIẾT KẾ:

KS. NGUYỄN MINH DUY BẰNG

KIỂM TRA:

KS. NGÔ TÙNG THÀNH

DỰ ÁN:

KHU DÂN CƯ A1-C1 (ĐÔ THỊ DẦU GIẤY)

ĐỊA ĐIỂM: XÃ DẦU GIẤY, TỈNH ĐỒNG NAI

CÔNG TRÌNH:

NHÀ Ở THƯƠNG MẠI LIÊN KẾ

HẠNG MỤC:

MẪU NHÀ T3\_2b

TÊN BẢN VẼ:

CHI TIẾT CẦU THANG-02


MỤC ĐÍCH PHÁT HÀNH:

|   |                          |
|---|--------------------------|
|   | BẢN VẼ MỜI THẦU          |
|   | THIẾT KẾ CƠ SỞ           |
| ✓ | THIẾT KẾ BẢN VẼ THI CÔNG |
|   | BẢN VẼ HOÀN CÔNG         |

HOÀN THÀNH 07/2025


TỶ LỆ NTS

SỐ HIỆU BẢN VẼ KC-48

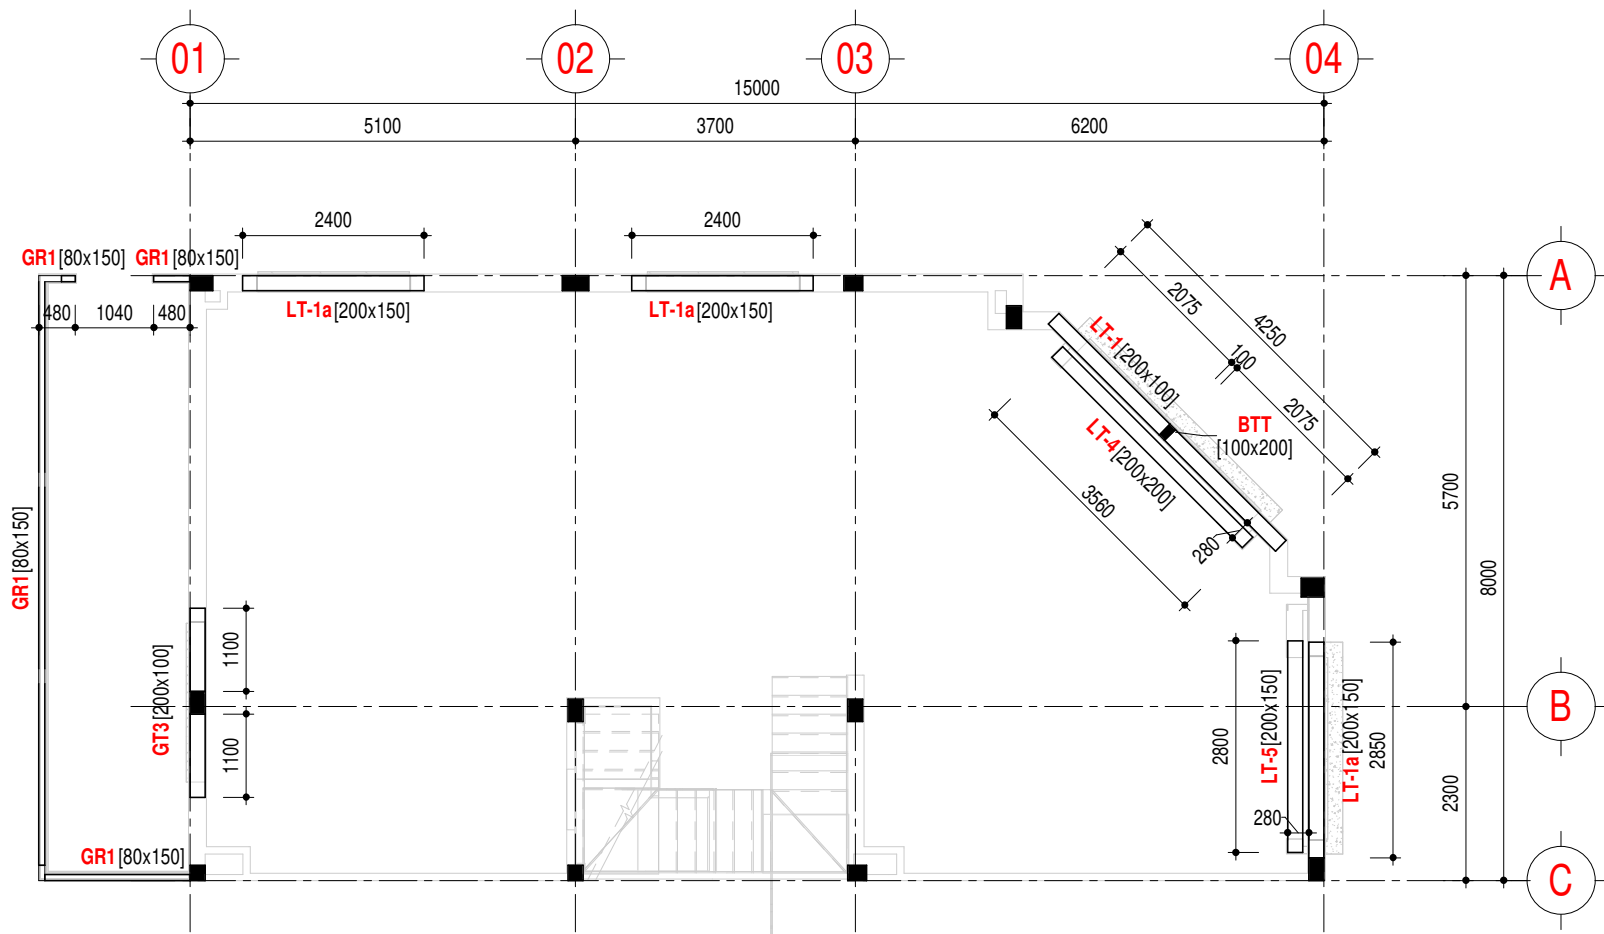


### MẶT BẰNG LANH TÔ - TẦNG 1

TL 1 : 100

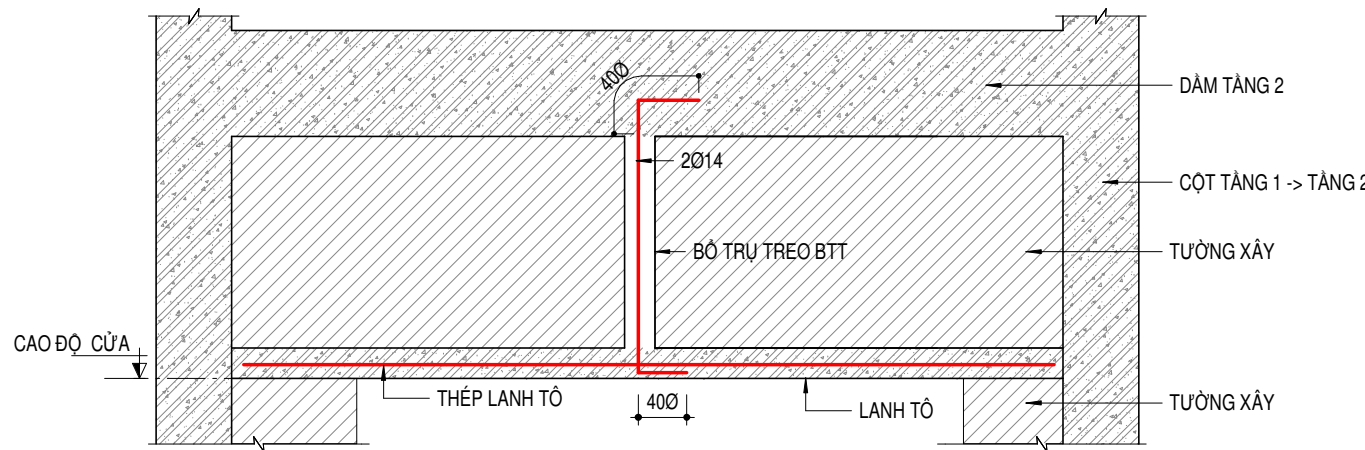

### CHI TIẾT BTT ĐIỂN HÌNH

TỶ LỆ 1 : 25

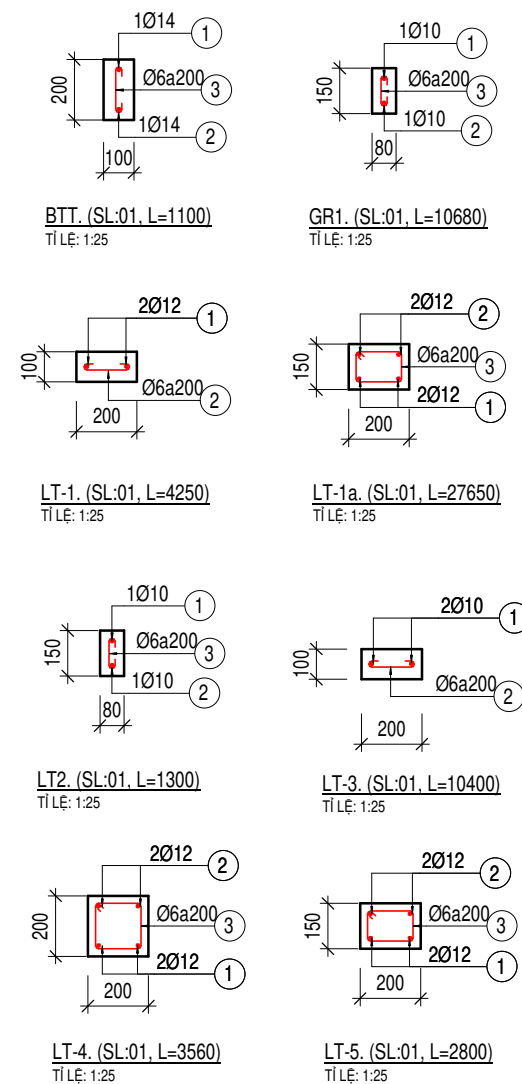

### GHI CHÚ:

- TẤT CẢ CÁC KÍCH THƯỚC ĐƯỢC KIỂM TRA VÀ XÁC NHẬN TRÊN CÔNG TRƯỜNG
  - KÍCH THƯỚC VÀ VỊ TRÍ CÁC LỖ GEN, MƯƠNG, LAM TRANG TRÍ PHẢI ĐƯỢC KIỂM TRA SO VỚI CÁC BẢN VẼ KIẾN TRÚC, MEP CÓ LIÊN QUAN.
  - CÁC VỊ TRÍ ỚNG XUYỀN DẦM XEM BẢN VẼ MEP.
- CHI TIẾT XUYỀN DẦM XEM BẢN VẼ GHI CHÚ CHUNG

### GHI CHÚ:

- CÁC ĐƠN VỊ THI CÔNG PHẢI PHỐI HỢP BẢN VẼ CỦA TẤT CẢ CÁC BỘ MÔN KHÁC NẾU THẤY SỰ KHÁC BIỆT PHẢI BÁO CHO ĐƠN VỊ THIẾT KẾ XỬ LÝ.
- KHI XỬ LÝ SỰ KHÁC BIỆT, PHẢI THỰC HIỆN ƯU TIÊN THEO THỨ TỰ GIỮA CÁC BỘ MÔN: KIẾN TRÚC → KẾT CẤU / BỘ MÔN KHÁC; HOẶC ƯU TIÊN TRONG CÙNG BỘ MÔN: CHI TIẾT → TỔNG THỂ
- CÁC SỐ LIEU KÍCH THƯỚC PHẢI ĐƯỢC KIỂM TRA THỰC TẾ TẠI CÔNG TRÌNH, NẾU THẤY SỰ KHÁC BIỆT SO VỚI BẢN VẼ THI PHẢI BÁO CHO ĐƠN VỊ THIẾT KẾ.

### HIỆU CHỈNH:

| REV | NGÀY | NỘI DUNG |
|-----|------|----------|
|-----|------|----------|

### CHỦ ĐẦU TƯ:

CÔNG TY TNHH ĐẦU TƯ

**PHÚ VIỆT TÍN**

ĐỊA CHỈ: LÔ 18-19 QUỐC LỘ 1A, XÃ DẦU GIẤY,  
TỈNH ĐỒNG NAI, VIỆT NAM

CTHĐT

ĐẠNG PHƯỚC BÌNH

### ĐƠN VỊ THIẾT KẾ:

CÔNG TY CỔ PHẦN TƯ VẤN THIẾT KẾ

**BASE ARC**

ĐỊA CHỈ: 138 ĐIỆN BIÊN PHỦ, PHƯỜNG TÂN ĐỊNH,  
TP. HỒ CHÍ MINH, VIỆT NAM

### TỔNG GIÁM ĐỐC

TRẦN ĐỨC AN

### CHỦ NHIỆM DỰ ÁN:

KTS. NGUYỄN THÀNH THÁI

### CHỦ TRÌ THIẾT KẾ:

KS. NGÔ TÙNG THÀNH

### THIẾT KẾ:

KS. NGUYỄN MINH DUY BẰNG

### KIỂM TRA:

KS. NGÔ TÙNG THÀNH

### DỰ ÁN:

KHU DÂN CƯ A1-C1 (ĐÔ THỊ DẦU GIẤY)

ĐỊA ĐIỂM: XÃ DẦU GIẤY, TỈNH ĐỒNG NAI

### CÔNG TRÌNH:

NHÀ Ở THƯƠNG MẠI LIÊN KẾ

### HẠNG MỤC:

MẪU NHÀ T3\_2b

### TÊN BẢN VẼ:

MẶT BẰNG LANH TÔ TẦNG 1


### MỤC ĐÍCH PHÁT HÀNH:

|                                     |                          |
|-------------------------------------|--------------------------|
| <input type="checkbox"/>            | BẢN VẼ MỜI THẦU          |
| <input type="checkbox"/>            | THIẾT KẾ CƠ SỞ           |
| <input checked="" type="checkbox"/> | THIẾT KẾ BẢN VẼ THI CÔNG |
| <input type="checkbox"/>            | BẢN VẼ HOÀN CÔNG         |

HOÀN THÀNH 07/2025


TỶ LỆ NTS

SỐ HIỆU BẢN VẼ KC-49

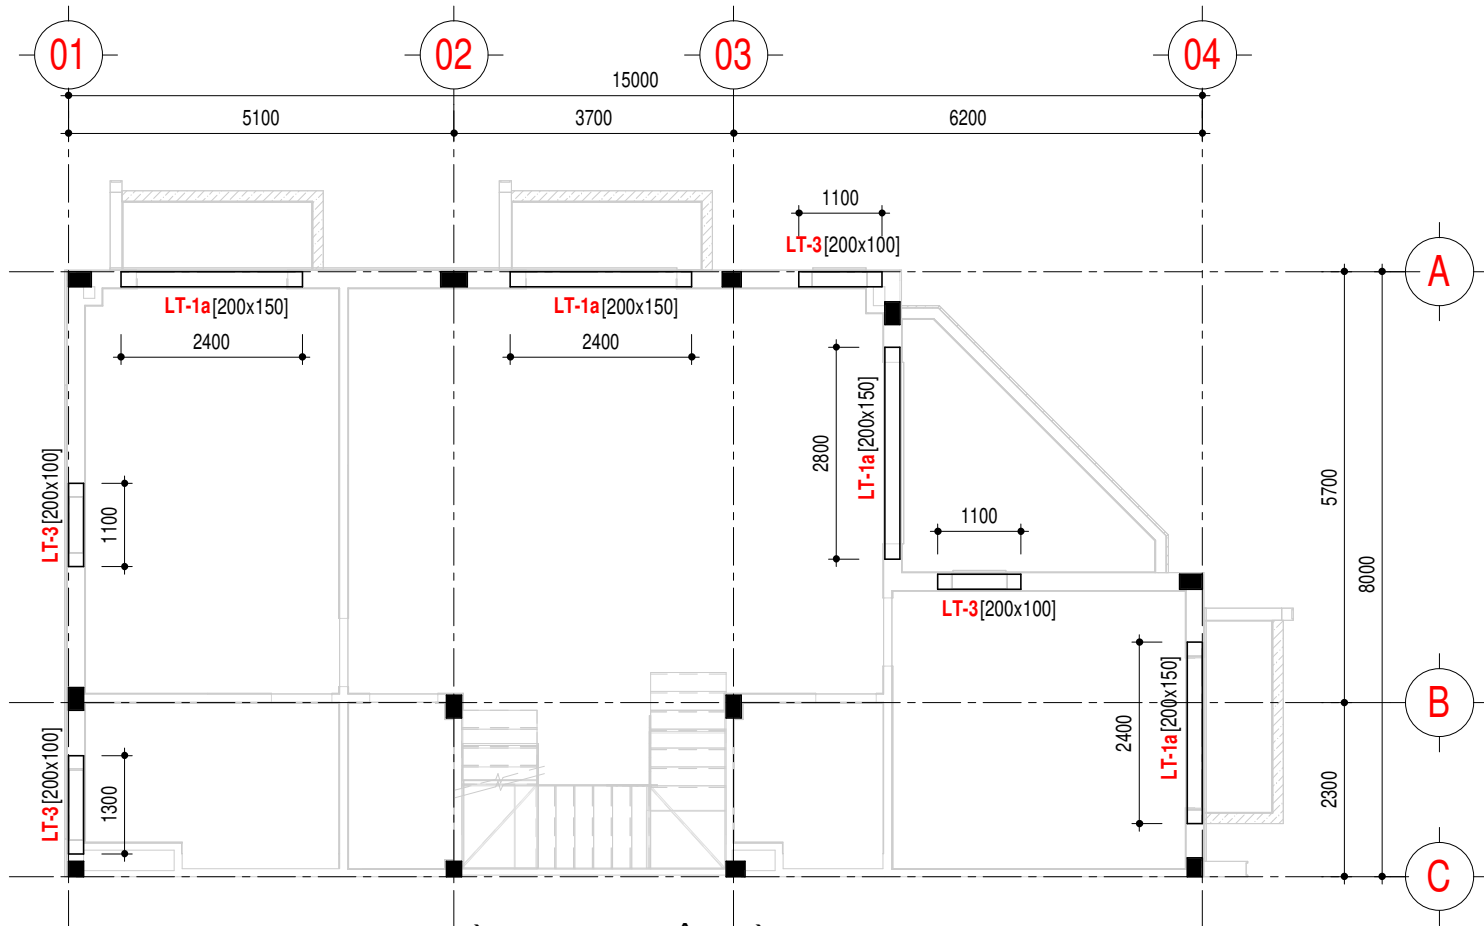

MẶT BẰNG LANH TÔ - TẦNG 2

TL 1 : 100

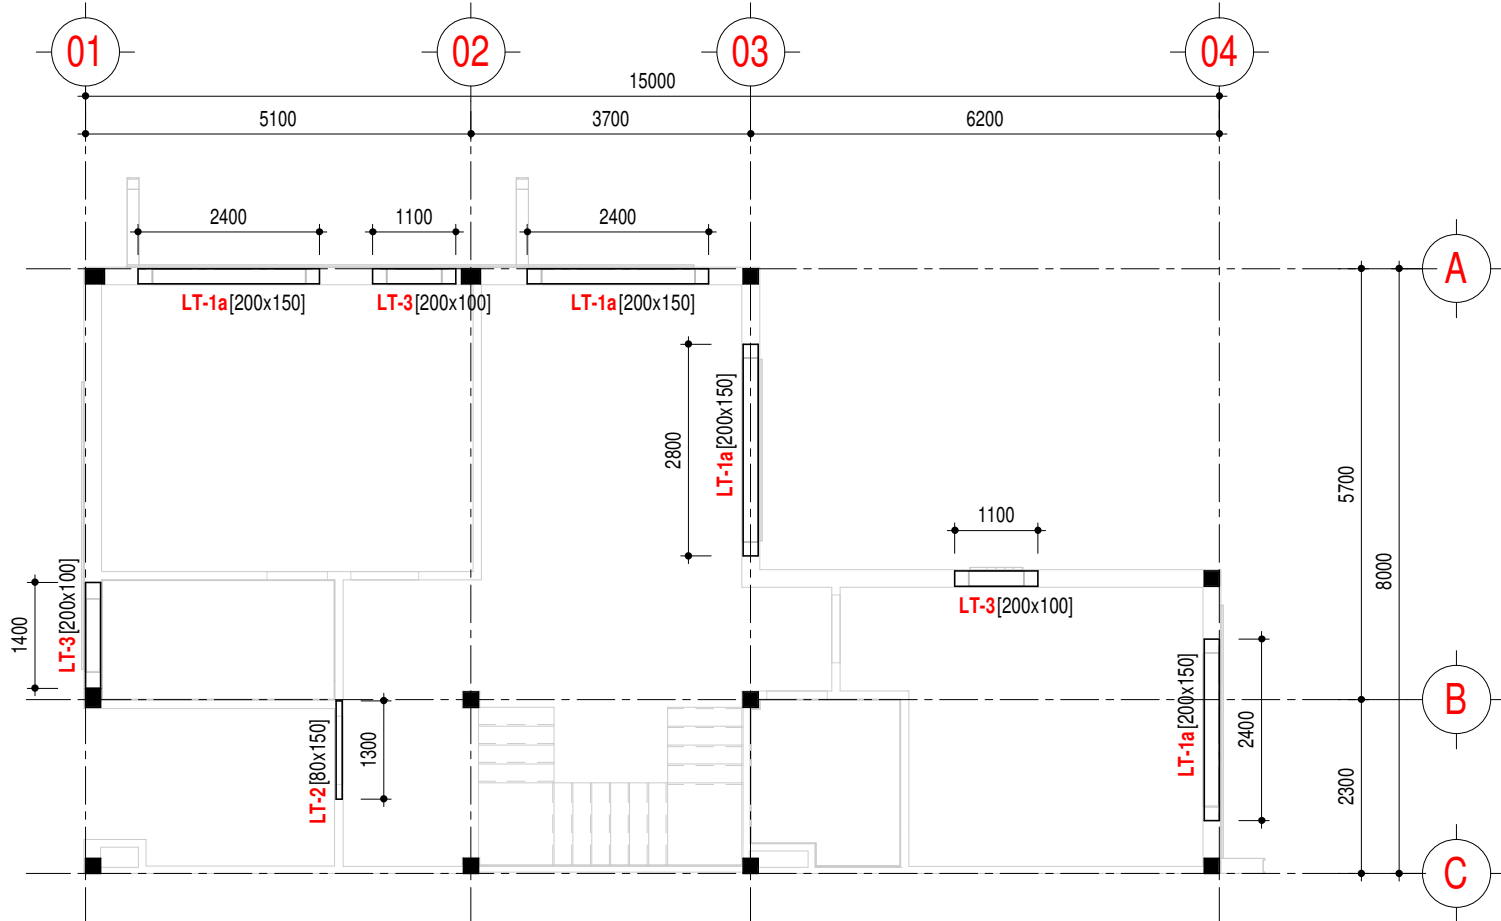

MẶT BẰNG LANH TÔ - TẦNG 3

TL 1 : 100

BẢNG THÔNG KÊ CỐT THÉP LANH TÔ

| TÊN C.KIỆN      | SỐ HIỆU | HÌNH DẠNG | Đ.KÍNH (mm) | A (mm) | B (mm) | C (mm) | CHIỀU DÀI 1 THANH (mm) | SỐ LƯỢNG<br>1 C.KIỆN | T.BỘ | TỔNG CHIỀU DÀI (m) | TỔNG T.LƯỢNG (kg) |
|-----------------|---------|-----------|-------------|--------|--------|--------|------------------------|----------------------|------|--------------------|-------------------|
| BTT.            |         |           |             |        |        |        |                        |                      |      |                    |                   |
| BTT. - SL: 01   | 1       | A B C     | 14          | 150    | 1100   | 150    | 1400                   | 1                    | 1    | 1.40               | 1.69              |
| BTT. - SL: 01   | 2       | A         | 14          | 1100   | 0      | 0      | 1100                   | 1                    | 1    | 1.10               | 1.33              |
| BTT. - SL: 01   | 3       | A B A     | 6           | 60     | 150    | 0      | 270                    | 6                    | 6    | 1.62               | 0.36              |
| GR1.            |         |           |             |        |        |        |                        |                      |      |                    |                   |
| GR1. - SL: 01   | 1       | A B C     | 10          | 100    | 10680  | 100    | 10880                  | 1                    | 1    | 10.88              | 6.71              |
| GR1. - SL: 01   | 2       | A         | 10          | 10680  | 0      | 0      | 10680                  | 1                    | 1    | 10.68              | 6.58              |
| GR1. - SL: 01   | 3       | A B A     | 6           | 60     | 100    | 0      | 220                    | 54                   | 54   | 11.88              | 2.64              |
| LT2.            |         |           |             |        |        |        |                        |                      |      |                    |                   |
| LT2. - SL: 01   | 1       | A B C     | 10          | 100    | 1300   | 100    | 1500                   | 1                    | 1    | 1.50               | 0.92              |
| LT2. - SL: 01   | 2       | A         | 10          | 1300   | 0      | 0      | 1300                   | 1                    | 1    | 1.30               | 0.80              |
| LT2. - SL: 01   | 3       | A B A     | 6           | 60     | 100    | 0      | 220                    | 7                    | 7    | 1.54               | 0.34              |
| LT-1.           |         |           |             |        |        |        |                        |                      |      |                    |                   |
| LT-1. - SL: 01  | 1       | A         | 12          | 4250   | 0      | 0      | 4250                   | 2                    | 2    | 8.50               | 7.55              |
| LT-1. - SL: 01  | 2       | A B C     | 6           | 60     | 150    | 0      | 270                    | 22                   | 22   | 5.94               | 1.32              |
| LT-1a.          |         |           |             |        |        |        |                        |                      |      |                    |                   |
| LT-1a. - SL: 01 | 1       | A         | 12          | 27650  | 0      | 0      | 27650                  | 2                    | 2    | 55.30              | 49.10             |
| LT-1a. - SL: 01 | 2       | A B C     | 12          | 100    | 27650  | 100    | 27850                  | 2                    | 2    | 55.70              | 49.45             |
| LT-1a. - SL: 01 | 3       | A B C     | 6           | 150    | 100    | 60     | 620                    | 139                  | 139  | 86.18              | 19.13             |
| LT-3.           |         |           |             |        |        |        |                        |                      |      |                    |                   |
| LT-3. - SL: 01  | 1       | A         | 10          | 10400  | 0      | 0      | 10400                  | 2                    | 2    | 20.80              | 12.82             |
| LT-3. - SL: 01  | 2       | A B A     | 6           | 60     | 150    | 0      | 270                    | 52                   | 52   | 14.04              | 3.12              |
| LT-4.           |         |           |             |        |        |        |                        |                      |      |                    |                   |
| LT-4. - SL: 01  | 1       | A         | 12          | 3560   | 0      | 0      | 3560                   | 2                    | 2    | 7.12               | 6.32              |
| LT-4. - SL: 01  | 2       | A B C     | 12          | 150    | 3560   | 150    | 3860                   | 2                    | 2    | 7.72               | 6.85              |
| LT-4. - SL: 01  | 3       | A B C     | 6           | 150    | 150    | 60     | 720                    | 18                   | 18   | 12.96              | 2.88              |
| LT-5.           |         |           |             |        |        |        |                        |                      |      |                    |                   |
| LT-5. - SL: 01  | 1       | A         | 12          | 2800   | 0      | 0      | 2800                   | 2                    | 2    | 5.60               | 4.97              |
| LT-5. - SL: 01  | 2       | A B C     | 12          | 100    | 2800   | 100    | 3000                   | 2                    | 2    | 6.00               | 5.33              |
| LT-5. - SL: 01  | 3       | A B C     | 6           | 150    | 100    | 60     | 620                    | 14                   | 14   | 8.68               | 1.93              |
| TỔNG            |         |           |             |        |        |        |                        | 334                  | 334  | 336.44             | 192.14            |

BẢNG TỔNG HỢP THÉP LANH TÔ

| Đ.KÍNH (mm) | TỔNG CHIỀU DÀI (m) | TỔNG T.LƯỢNG (kg) |
|-------------|--------------------|-------------------|
| 6           | 142.84             | 31.70             |
| 10          | 45.16              | 27.84             |
| 12          | 145.94             | 129.57            |
| 14          | 2.50               | 3.02              |
| TỔNG        | 336.44             | 192.14            |

GHI CHÚ:

- TẤT CẢ CÁC KÍCH THƯỚC ĐƯỢC KIỂM TRA VÀ XÁC NHẬN TRÊN CÔNG TRƯỜNG
  - KÍCH THƯỚC VÀ VỊ TRÍ CÁC LỖ GEN, MƯƠNG, LAM TRANG TRÍ PHẢI ĐƯỢC KIỂM TRA SO VỚI CÁC BẢN VẼ KIẾN TRÚC, MEP CÓ LIÊN QUAN.
  - CÁC VỊ TRÍ ỜNG XUYỀN DÀM XEM BẢN VẼ MEP.
- CHI TIẾT XUYỀN DÀM XEM BẢN VẼ GHI CHÚ CHUNG

GHI CHÚ:

- CÁC ĐƠN VỊ THI CÔNG PHẢI PHỐI HỢP BẢN VẼ CỦA TẤT CẢ CÁC BỘ MÔN KHÁC NẾU THẤY SỰ KHÁC BIỆT PHẢI BÁO CHO ĐƠN VỊ THIẾT KẾ ĐỂ XỬ LÝ.
- KHI XỬ LÝ SỰ KHÁC BIỆT, PHẢI THỰC HIỆN ƯU TIÊN THEO THỨ TỰ GIỮA CÁC BỘ MÔN: KIẾN TRÚC → KẾT CẤU / BỘ MÔN KHÁC; HOẶC ƯU TIÊN TRONG CÙNG BỘ MÔN: CHI TIẾT → TỔNG THỂ
- CÁC SỐ LIEU KÍCH THƯỚC PHẢI ĐƯỢC KIỂM TRA THỰC TẾ TẠI CÔNG TRÌNH, NẾU THẤY SỰ KHÁC BIỆT SƠ VỚI BẢN VẼ THI PHẢI BÁO CHO ĐƠN VỊ THIẾT KẾ.

HIỆU CHỈNH:

| REV | NGÀY | NỘI DUNG |
|-----|------|----------|
|-----|------|----------|

CHỦ ĐẦU TƯ:

CÔNG TY TNHH ĐẦU TƯ

**PHÚ VIỆT TÍN**

ĐỊA CHỈ: LÔ 18-19 QUỐC LỘ 1A, XÃ DẦU GIẤY, TỈNH ĐỒNG NAI, VIỆT NAM

CTHĐT

ĐẠNG PHƯỚC BÌNH

ĐƠN VỊ THIẾT KẾ:

CÔNG TY CỔ PHẦN TƯ VẤN THIẾT KẾ

**BASE ARC**

ĐỊA CHỈ: 138 ĐIỆN BIÊN PHỦ, PHƯỜNG TÂN ĐỊNH, TP. HỒ CHÍ MINH, VIỆT NAM

TỔNG GIÁM ĐỐC

TRẦN ĐỨC AN

CHỦ NHIỆM DỰ ÁN:

KTS. NGUYỄN THÀNH THÁI

CHỦ TRÌ THIẾT KẾ:

KS. NGÔ TÙNG THÀNH

THIẾT KẾ:

KS. NGUYỄN MINH DUY BẰNG

KIỂM TRA:

KS. NGÔ TÙNG THÀNH

DỰ ÁN:

KHU DÂN CƯ A1-C1 (ĐÔ THỊ DẦU GIẤY)

ĐỊA ĐIỂM: XÃ DẦU GIẤY, TỈNH ĐỒNG NAI

CÔNG TRÌNH:

NHÀ Ở THƯƠNG MẠI LIÊN KẾ

HẠNG MỤC:

MẪU NHÀ T3\_2b

TÊN BẢN VẼ:

MẶT BẰNG LANH TÔ TẦNG 2, TẦNG 3

MỤC ĐÍCH PHÁT HÀNH:

|                                     |                          |
|-------------------------------------|--------------------------|
| <input type="checkbox"/>            | BẢN VẼ MỜI THẦU          |
| <input type="checkbox"/>            | THIẾT KẾ CƠ SỞ           |
| <input checked="" type="checkbox"/> | THIẾT KẾ BẢN VẼ THI CÔNG |
| <input type="checkbox"/>            | BẢN VẼ HOÀN CÔNG         |
| HOÀN THÀNH                          | 07/2025                  |
| TỶ LỆ                               | NTS                      |
| SỐ HIỆU BẢN VẼ                      | KC-50                    |



| BẢNG THỐNG KÊ CỐT THÉP ĐÁY MÓNG PHƯƠNG ÁN 1 |         |                                                 |             |        |        |        |                        |          |      |                    |                   |
|---------------------------------------------|---------|-------------------------------------------------|-------------|--------|--------|--------|------------------------|----------|------|--------------------|-------------------|
| TÊN C.KIỆN                                  | SỐ HIỆU | HÌNH DẠNG                                       | Đ.KÍNH (mm) | A (mm) | B (mm) | C (mm) | CHIỀU DÀI 1 THANH (mm) | SỐ LƯỢNG |      | TỔNG CHIỀU DÀI (m) | TỔNG T.LƯỢNG (kg) |
|                                             |         |                                                 |             |        |        |        |                        | 1 C.KIỆN | T.BỘ |                    |                   |
| PHƯƠNG ÁN 1 - M1                            |         |                                                 |             |        |        |        |                        |          |      |                    |                   |
| PHƯƠNG ÁN 1 - M1 - SL: 01                   |         | <div><div>A</div><div>B</div><div>C</div></div> | 10          | 100    | 900    | 100    | 1100                   | 41       | 41   | 45.10              | 27.81             |
| PHƯƠNG ÁN 1 - M1 - SL: 01                   |         | <div><div>A</div></div>                         | 10          | 0      | 7900   | 0      | 7900                   | 4        | 4    | 31.60              | 19.48             |
| PHƯƠNG ÁN 1 - M2                            |         |                                                 |             |        |        |        |                        |          |      |                    |                   |
| PHƯƠNG ÁN 1 - M2 - SL: 01                   |         | <div><div>A</div><div>B</div><div>C</div></div> | 10          | 100    | 1100   | 100    | 1300                   | 50       | 50   | 65.00              | 40.07             |
| PHƯƠNG ÁN 1 - M2 - SL: 01                   |         | <div><div>A</div></div>                         | 10          | 0      | 7900   | 0      | 7900                   | 4        | 4    | 31.60              | 19.48             |
| PHƯƠNG ÁN 1 - M3                            |         |                                                 |             |        |        |        |                        |          |      |                    |                   |
| PHƯƠNG ÁN 1 - M3 - SL: 01                   |         | <div><div>A</div><div>B</div><div>C</div></div> | 10          | 100    | 1250   | 100    | 1450                   | 52       | 52   | 75.40              | 46.49             |
| PHƯƠNG ÁN 1 - M3 - SL: 01                   |         | <div><div>A</div></div>                         | 10          | 0      | 7900   | 0      | 7900                   | 6        | 6    | 47.40              | 29.22             |
| PHƯƠNG ÁN 1 - M4                            |         |                                                 |             |        |        |        |                        |          |      |                    |                   |
| PHƯƠNG ÁN 1 - M4 - SL: 01                   |         | <div><div>A</div><div>B</div><div>C</div></div> | 10          | 100    | 1000   | 100    | 1200                   | 26       | 26   | 31.20              | 19.24             |
| PHƯƠNG ÁN 1 - M4 - SL: 01                   |         | <div><div>A</div></div>                         | 10          | 0      | 3900   | 0      | 3900                   | 4        | 4    | 15.60              | 9.62              |
| TỔNG                                        |         |                                                 |             |        |        |        |                        | 187      | 187  | 342.90             | 211.41            |

| BẢNG TỔNG HỢP THÉP ĐÁY MÓNG PHƯƠNG ÁN 1 |                    |                   |
|-----------------------------------------|--------------------|-------------------|
| Đ.KÍNH (mm)                             | TỔNG CHIỀU DÀI (m) | TỔNG T.LƯỢNG (kg) |
| 10                                      | 342.90             | 211.41            |
| TỔNG                                    | 342.90             | 211.41            |

| BẢNG THỐNG KÊ CỐT THÉP ĐAN TỰ HOẠI |         |                         |             |        |        |        |                        |          |      |                    |                   |
|------------------------------------|---------|-------------------------|-------------|--------|--------|--------|------------------------|----------|------|--------------------|-------------------|
| TÊN C.KIỆN                         | SỐ HIỆU | HÌNH DẠNG               | Đ.KÍNH (mm) | A (mm) | B (mm) | C (mm) | CHIỀU DÀI 1 THANH (mm) | SỐ LƯỢNG |      | TỔNG CHIỀU DÀI (m) | TỔNG T.LƯỢNG (kg) |
|                                    |         |                         |             |        |        |        |                        | 1 C.KIỆN | T.BỘ |                    |                   |
| ĐAN ĐÁY BÉ TH                      |         |                         |             |        |        |        |                        |          |      |                    |                   |
| ĐAN ĐÁY BÉ TH - SL: 01             |         | <div><div>A</div></div> | 8           | 0      | 1450   | 0      | 1450                   | 48       | 48   | 69.60              | 27.46             |
| TỔNG                               |         |                         |             |        |        |        |                        | 48       | 48   | 69.60              | 27.46             |

| BẢNG THỐNG KÊ CỐT THÉP ĐÁY MÓNG PHƯƠNG ÁN 2 |         |                                                 |             |        |        |        |                        |          |      |                    |                   |
|---------------------------------------------|---------|-------------------------------------------------|-------------|--------|--------|--------|------------------------|----------|------|--------------------|-------------------|
| TÊN C.KIỆN                                  | SỐ HIỆU | HÌNH DẠNG                                       | Đ.KÍNH (mm) | A (mm) | B (mm) | C (mm) | CHIỀU DÀI 1 THANH (mm) | SỐ LƯỢNG |      | TỔNG CHIỀU DÀI (m) | TỔNG T.LƯỢNG (kg) |
|                                             |         |                                                 |             |        |        |        |                        | 1 C.KIỆN | T.BỘ |                    |                   |
| PHƯƠNG ÁN 2 - M1                            |         |                                                 |             |        |        |        |                        |          |      |                    |                   |
| PHƯƠNG ÁN 2 - M1 - SL: 01                   |         | <div><div>A</div><div>B</div><div>C</div></div> | 10          | 100    | 1100   | 100    | 1300                   | 44       | 44   | 57.20              | 35.27             |
| PHƯƠNG ÁN 2 - M1 - SL: 01                   |         | <div><div>A</div></div>                         | 10          | 0      | 7900   | 0      | 7900                   | 5        | 5    | 39.50              | 24.35             |
| PHƯƠNG ÁN 2 - M2                            |         |                                                 |             |        |        |        |                        |          |      |                    |                   |
| PHƯƠNG ÁN 2 - M2 - SL: 01                   |         | <div><div>A</div><div>B</div><div>C</div></div> | 10          | 100    | 1300   | 100    | 1500                   | 56       | 56   | 84.00              | 51.79             |
| PHƯƠNG ÁN 2 - M2 - SL: 01                   |         | <div><div>A</div></div>                         | 10          | 0      | 7900   | 0      | 7900                   | 6        | 6    | 47.40              | 29.22             |
| PHƯƠNG ÁN 2 - M3                            |         |                                                 |             |        |        |        |                        |          |      |                    |                   |
| PHƯƠNG ÁN 2 - M3 - SL: 01                   |         | <div><div>A</div><div>B</div><div>C</div></div> | 10          | 100    | 1450   | 100    | 1650                   | 58       | 58   | 95.70              | 59.00             |
| PHƯƠNG ÁN 2 - M3 - SL: 01                   |         | <div><div>A</div></div>                         | 10          | 0      | 7900   | 0      | 7900                   | 6        | 6    | 47.40              | 29.22             |
| PHƯƠNG ÁN 2 - M4                            |         |                                                 |             |        |        |        |                        |          |      |                    |                   |
| PHƯƠNG ÁN 2 - M4 - SL: 01                   |         | <div><div>A</div><div>B</div><div>C</div></div> | 10          | 100    | 1200   | 100    | 1400                   | 29       | 29   | 40.60              | 25.03             |
| PHƯƠNG ÁN 2 - M4 - SL: 01                   |         | <div><div>A</div></div>                         | 10          | 0      | 3900   | 0      | 3900                   | 6        | 6    | 23.40              | 14.43             |
| TỔNG                                        |         |                                                 |             |        |        |        |                        | 210      | 210  | 435.20             | 268.32            |

| BẢNG TỔNG HỢP THÉP ĐÁY MÓNG PHƯƠNG ÁN 2 |                    |                   |
|-----------------------------------------|--------------------|-------------------|
| Đ.KÍNH (mm)                             | TỔNG CHIỀU DÀI (m) | TỔNG T.LƯỢNG (kg) |
| 10                                      | 435.20             | 268.32            |
| TỔNG                                    | 435.20             | 268.32            |

GHI CHÚ:

- CÁC ĐƠN VỊ THI CÔNG PHẢI PHỐI HỢP BẢN VẼ CỦA TẤT CẢ CÁC BỘ MÔN KHÁC NẾU THẤY SỰ KHÁC BIỆT PHẢI BẢO CHO ĐƠN VỊ THIẾT KẾ XỬ LÝ.
- KHU XỬ LÝ SỰ KHÁC BIỆT, PHẢI THỰC HIỆN ƯU TIÊN THEO THỨ TỰ GIỮA CÁC BỘ MÔN: KIẾN TRÚC → KẾT CẤU / BỘ MÔN KHÁC; HOẶC ƯU TIÊN TRONG CÙNG BỘ MÔN: CHI TIẾT → TỔNG THỂ
- CÁC SỐ LIEU KÍCH THƯỚC PHẢI ĐƯỢC KIỂM TRA THỰC TẾ TẠI CÔNG TRÌNH, NẾU THẤY SỰ KHÁC BIỆT SƠ VỚI BẢN VẼ THI PHẢI BẢO CHO ĐƠN VỊ THIẾT KẾ.

| HIỆU CHỈNH: |      |          |
|-------------|------|----------|
| REV         | NGÀY | NỘI DUNG |
|             |      |          |

CHỦ ĐẦU TƯ:

CÔNG TY TNHH ĐẦU TƯ

PHÚ VIỆT TÍN

ĐỊA CHỈ: LÔ 18-19 QUỐC LỘ 1A, XÃ DẦU GIẤY, TỈNH ĐỒNG NAI, VIỆT NAM

CTHĐTVĐẠNG PHƯỚC BÌNH

ĐƠN VỊ THIẾT KẾ:

CÔNG TY CỔ PHẦN TƯ VẤN THIẾT KẾ

BASE ARC

ĐỊA CHỈ: 138 ĐIỆN BIÊN PHỦ, PHƯỜNG TÂN ĐỊNH, TP. HỒ CHÍ MINH, VIỆT NAM

TỔNG GIÁM ĐỐCTRẦN ĐỨC AN

|                          |  |
|--------------------------|--|
| CHỦ NHIỆM DỰ ÁN:         |  |
| KTS. NGUYỄN THÀNH THÁI   |  |
| CHỦ TRÌ THIẾT KẾ:        |  |
| KS. NGÔ TÙNG THÀNH       |  |
| THIẾT KẾ:                |  |
| KS. NGUYỄN MINH DUY BẰNG |  |
| KIỂM TRA:                |  |
| KS. NGÔ TÙNG THÀNH       |  |

DỰ ÁN:

KHU DÂN CƯ A1-C1 (ĐÔ THỊ DẦU GIẤY)

ĐỊA ĐIỂM: XÃ DẦU GIẤY, TỈNH ĐỒNG NAI

CÔNG TRÌNH:

NHÀ Ở THƯƠNG MẠI LIÊN KẾ






















HẠNG MỤC:

MẪU NHÀ T3\_2b

TÊN BẢN VẼ:

TKT ĐÁY MÓNG

| MỤC ĐÍCH PHÁT HÀNH: |                          |
|---------------------|--------------------------|
|                     | BẢN VẼ MỜI THẦU          |
|                     | THIẾT KẾ CƠ SỞ           |
| ✓                   | THIẾT KẾ BẢN VẼ THI CÔNG |
|                     | BẢN VẼ HOÀN CÔNG         |
| HOÀN THÀNH          | 07/2025                  |
| TỶ LỆ               | NTS                      |
| SỐ HIỆU BẢN VẼ      | KC-52                    |
                     
| BẢNG THỐNG KÊ CỘT THÉP DẦM MÓNG |         |                                                                                             |                 |                      |             |          |       |                    |                      |
|---------------------------------|---------|---------------------------------------------------------------------------------------------|-----------------|----------------------|-------------|----------|-------|--------------------|----------------------|
| TÊN CẦU KIỆN                    | SỐ HIỆU | HÌNH DẠNG, KÍCH THƯỚC                                                                       | ĐƯỜNG KÍNH (mm) | CHIỀU DÀI THANH (mm) | SỐ CẦU KIỆN | SỐ LƯỢNG |       | TỔNG CHIỀU DÀI (m) | TỔNG KHỐI LƯỢNG (kg) |
|                                 |         |                                                                                             |                 |                      |             | 1 CK     | T. BỘ |                    |                      |
| M5 SL: 1                        | 1       |            | 10              | 1000                 | 1           | 7        | 7     | 7.00               | 4.32                 |
|                                 | 2       |            | 10              | 1100                 | 1           | 6        | 6     | 6.60               | 4.07                 |
| PA1 - M1 SL: 1                  | 1       | 605  480   | 20              | 6850                 | 1           | 4        | 4     | 27.40              | 67.57                |
|                                 | 2       | 320  440   | 16              | 3225                 | 1           | 3        | 3     | 9.68               | 15.27                |
|                                 | 3       | 250  250   | 14              | 8390                 | 1           | 4        | 4     | 33.56              | 40.55                |
|                                 | 5       |            | 16              | 2200                 | 1           | 2        | 2     | 4.40               | 6.94                 |
|                                 | 6       |            | 18              | 3750                 | 1           | 4        | 4     | 15.00              | 29.96                |
|                                 | 7       |            | 12              | 5565                 | 1           | 2        | 2     | 11.13              | 9.88                 |
|                                 | 8       | 64  640    | 8               | 2090                 | 1           | 36       | 36    | 75.24              | 29.69                |
|                                 | 9       | 64  440    | 8               | 1690                 | 1           | 14       | 14    | 23.66              | 9.34                 |
|                                 | 10      | 64  64     | 8               | 555                  | 1           | 22       | 22    | 12.21              | 4.82                 |
| PA1 - M2 SL: 1                  | 1       | 605  480   | 20              | 6950                 | 1           | 4        | 4     | 27.80              | 68.56                |
|                                 | 2       | 320  440   | 16              | 3125                 | 1           | 3        | 3     | 9.38               | 14.80                |
|                                 | 3       | 250  250   | 14              | 8390                 | 1           | 4        | 4     | 33.56              | 40.55                |
|                                 | 5       |            | 16              | 2200                 | 1           | 2        | 2     | 4.40               | 6.94                 |
|                                 | 6       |            | 18              | 3750                 | 1           | 4        | 4     | 15.00              | 29.96                |
|                                 | 7       |            | 12              | 5665                 | 1           | 2        | 2     | 11.33              | 10.06                |
|                                 | 8       | 64  640    | 8               | 2090                 | 1           | 37       | 37    | 77.33              | 30.51                |
|                                 | 9       | 64  440    | 8               | 1690                 | 1           | 13       | 13    | 21.97              | 8.67                 |
|                                 | 10      | 64  64    | 8               | 555                  | 1           | 22       | 22    | 12.21              | 4.82                 |
| PA1 - M3 SL: 1                  | 1       | 605  480 | 20              | 6950                 | 1           | 4        | 4     | 27.80              | 68.56                |
|                                 | 2       | 320  440 | 16              | 3125                 | 1           | 4        | 4     | 12.50              | 19.73                |
|                                 | 3       | 310  310 | 16              | 8510                 | 1           | 4        | 4     | 34.04              | 53.73                |
|                                 | 5       |          | 16              | 2200                 | 1           | 2        | 2     | 4.40               | 6.94                 |
|                                 | 6       |          | 18              | 3750                 | 1           | 2        | 2     | 7.50               | 14.98                |
|                                 | 7       |          | 12              | 5665                 | 1           | 2        | 2     | 11.33              | 10.06                |
|                                 | 8       | 64  640  | 8               | 2090                 | 1           | 37       | 37    | 77.33              | 30.51                |
|                                 | 9       | 64  440  | 8               | 1690                 | 1           | 10       | 10    | 16.90              | 6.67                 |
|                                 | 10      | 64  64   | 8               | 555                  | 1           | 13       | 13    | 7.22               | 2.85                 |
| PA1 - M4 SL: 1                  | 1       | 555  505 | 20              | 5000                 | 1           | 3        | 3     | 15.00              | 36.99                |
|                                 | 2       | 200  150 | 14              | 4240                 | 1           | 3        | 3     | 12.72              | 15.37                |
|                                 | 4       | 540  540 | 20              | 4920                 | 1           | 3        | 3     | 14.76              | 36.40                |
|                                 | 5       | 64  590  | 8               | 1890                 | 1           | 24       | 24    | 45.36              | 17.90                |
|                                 | 6       | 64  64   | 8               | 505                  | 1           | 9        | 9     | 4.54               | 1.79                 |

| TỔNG HỢP CỐT THÉP DẦM MÓNG |        |      |       |       |        |      |        |
|----------------------------|--------|------|-------|-------|--------|------|--------|
| - Đường kính (mm):         | Ø8     | Ø10  | Ø12   | Ø14   | Ø16    | Ø18  | Ø20    |
| - Chiều dài (m):           | 373.97 | 13.6 | 33.79 | 79.84 | 78.8   | 37.5 | 112.76 |
| - Khối lượng (kg):         | 147.57 | 8.39 | 30    | 96.47 | 124.35 | 74.9 | 278.08 |
| - Chiều dài / 11.7         | -      | 2    | 3     | 7     | 7      | 4    | 10     |
|                            |        |      |       |       |        |      |        |
| - Nhóm Ø < 10:             | 147.57 | kg   |       |       |        |      |        |
| - Nhóm 10 <= Ø < 20:       | 334.11 | kg   |       |       |        |      |        |
| - Nhóm Ø >= 20:            | 278.08 | kg   |       |       |        |      |        |
| - Tổng cộng:               | 759.76 | kg   |       |       |        |      |        |

GHI CHÚ:

- CÁC ĐƠN VỊ THI CÔNG PHẢI PHỐI HỢP BẢN VẼ CỦA TẤT CẢ CÁC BỘ MÔN KHÁC NẾU THẤY SỰ KHÁC BIỆT PHẢI BẢO CHO ĐƠN VỊ THIẾT KẾ ĐỂ XỬ LÝ.

- KHI XỬ LÝ SỰ KHÁC BIỆT, PHẢI THỰC HIỆN ƯU TIÊN THEO THỨ TỰ GIỮA CÁC BỘ MÔN: KIẾN TRÚC → KẾT CẤU / BỘ MÔN KHÁC; HOẶC ƯU TIÊN TRONG CÙNG BỘ MÔN: CHI TIẾT → TỔNG THỂ

- CÁC SỐ LƯỢNG KÍCH THƯỚC PHẢI ĐƯỢC KIỂM TRA THỰC TẾ TẠI CÔNG TRÌNH, NẾU THẤY SỰ KHÁC BIỆT SƠ VỚI BẢN VẼ THI PHẢI BÁO CHO ĐƠN VỊ THIẾT KẾ.

HIỆU CHỈNH:

|     |      |          |
|-----|------|----------|
| REV | NGÀY | NỘI DUNG |
|     |      |          |

CHỦ ĐẦU TƯ:

CÔNG TY TNHH ĐẦU TƯ  
PHÚ VIỆT TÍN

ĐỊA CHỈ: LÔ 18-19 QUỐC LỘ 1A, XÃ DẦU GIẦY,  
TỈNH ĐỒNG NAI, VIỆT NAM

CTHĐT/V

ĐẠNG PHƯỚC BÌNH

ĐƠN VỊ THIẾT KẾ:

CÔNG TY CỔ PHẦN TƯ VẤN THIẾT KẾ  
BASE ARC

ĐỊA CHỈ: 138 ĐIỆN BIÊN PHŨ, PHƯỜNG TÂN ĐỊNH,  
TP. HỒ CHÍ MINH, VIỆT NAM

TỔNG GIÁM ĐỐC

TRẦN ĐỨC AN

CHỦ NHIỆM DỰ ÁN:

KTS. NGUYỄN THÀNH THÁI

CHỦ TRÌ THIẾT KẾ:

KS. NGÔ TÙNG THÀNH

THIẾT KẾ:

KS. NGUYỄN MINH DUY BẰNG

KIỂM TRA:

KS. NGÔ TÙNG THÀNH

DỰ ÁN:

KHU DÂN CƯ A1-C1 (ĐÔ THỊ DẦU GIẦY)  
ĐỊA ĐIỂM: XÃ DẦU GIẦY, TỈNH ĐỒNG NAI

CÔNG TRÌNH:

NHÀ Ở THƯƠNG MẠI LIỀN KỀ

HẠNG MỤC:

MẪU NHÀ T3\_2b

TÊN BẢN VẼ:

TKT DẪM MÓNG PA1

MỤC ĐÍCH PHÁT HÀNH:

|                                     |                          |
|-------------------------------------|--------------------------|
| <input type="checkbox"/>            | BẢN VẼ MỜI THẦU          |
| <input type="checkbox"/>            | THIẾT KẾ CƠ SỞ           |
| <input checked="" type="checkbox"/> | THIẾT KẾ BẢN VẼ THI CÔNG |
| <input type="checkbox"/>            | BẢN VẼ HOÀN CÔNG         |

HOÀN THÀNH

07/2025






















TỶ LỆ

NTS




















SỐ HIỆU BẢN VẼ

KC-53

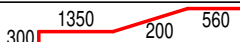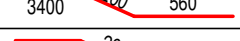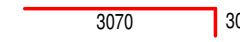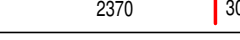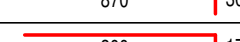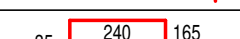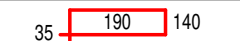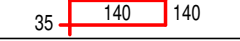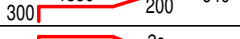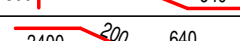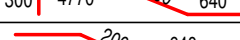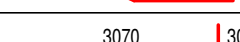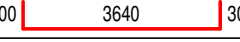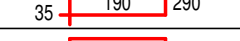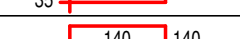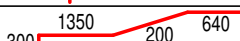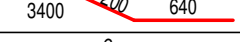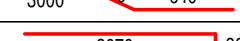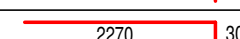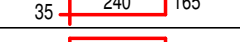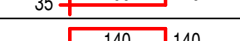

| BẢNG THỐNG KÊ CỐT THÉP CỘT |         |                                                                                     |                 |                      |             |          |       |                    |                      |
|----------------------------|---------|-------------------------------------------------------------------------------------|-----------------|----------------------|-------------|----------|-------|--------------------|----------------------|
| TÊN CẦU KIỆN               | SỐ HIỆU | HÌNH DẠNG, KÍCH THƯỚC                                                               | ĐƯỜNG KÍNH (mm) | CHIỀU DÀI THANH (mm) | SỐ CẦU KIỆN | SỐ LƯỢNG |       | TỔNG CHIỀU DÀI (m) | TỔNG KHỐI LƯỢNG (kg) |
|                            |         |                                                                                     |                 |                      |             | 1 CK     | T. BỘ |                    |                      |
| C7<br>SL: 1                | 1       |    | 14              | 2410                 | 1           | 2        | 2     | 4.82               | 5.82                 |
|                            | 2       |    | 14              | 3110                 | 1           | 2        | 2     | 6.22               | 7.52                 |
|                            | 3       |    | 14              | 4160                 | 1           | 4        | 4     | 16.64              | 20.11                |
|                            | 4       |    | 14              | 3760                 | 1           | 8        | 8     | 30.08              | 36.35                |
|                            | 5       |    | 14              | 4630                 | 1           | 1        | 1     | 4.63               | 5.59                 |
|                            | 6       |    | 14              | 5330                 | 1           | 1        | 1     | 5.33               | 6.44                 |
|                            | 7       |    | 14              | 3370                 | 1           | 1        | 1     | 3.37               | 4.07                 |
|                            | 8       |    | 14              | 2670                 | 1           | 1        | 1     | 2.67               | 3.23                 |
|                            | 9       |    | 14              | 1170                 | 1           | 2        | 2     | 2.34               | 2.83                 |
|                            | 10      |    | 170             | 470                  | 1           | 2        | 2     | 0.94               | 1.14                 |
|                            | 11      |    | 165             | 880                  | 1           | 14       | 14    | 12.32              | 2.73                 |
|                            | 12      |    | 140             | 730                  | 1           | 57       | 57    | 41.61              | 9.24                 |
|                            | 13      |    | 140             | 630                  | 1           | 37       | 37    | 23.31              | 5.17                 |
| C8<br>SL: 1                | 1       |  | 16              | 2490                 | 1           | 2        | 2     | 4.98               | 7.86                 |
|                            | 2       |  | 16              | 3290                 | 1           | 2        | 2     | 6.58               | 10.39                |
|                            | 3       |  | 16              | 4240                 | 1           | 4        | 4     | 16.96              | 26.77                |
|                            | 4       |  | 16              | 5110                 | 1           | 1        | 1     | 5.11               | 8.07                 |
|                            | 5       |  | 16              | 5910                 | 1           | 1        | 1     | 5.91               | 9.33                 |
|                            | 6       |  | 16              | 3840                 | 1           | 4        | 4     | 15.36              | 24.24                |
|                            | 7       |  | 300             | 3370                 | 1           | 3        | 3     | 10.11              | 15.96                |
|                            | 8       |  | 300             | 2570                 | 1           | 3        | 3     | 7.71               | 12.17                |
|                            | 9       |  | 300             | 4240                 | 1           | 2        | 2     | 8.48               | 13.38                |
|                            | 10      |  | 290             | 1030                 | 1           | 14       | 14    | 14.42              | 3.20                 |
|                            | 11      |  | 240             | 830                  | 1           | 57       | 57    | 47.31              | 10.50                |
|                            | 12      |  | 140             | 630                  | 1           | 27       | 27    | 17.01              | 3.78                 |
| C9<br>SL: 1                | 1       |  | 16              | 2490                 | 1           | 2        | 2     | 4.98               | 7.86                 |
|                            | 2       |  | 16              | 3290                 | 1           | 2        | 2     | 6.58               | 10.39                |
|                            | 3       |  | 16              | 4240                 | 1           | 4        | 4     | 16.96              | 26.77                |
|                            | 4       |  | 16              | 3840                 | 1           | 4        | 4     | 15.36              | 24.24                |
|                            | 5       |  | 300             | 3370                 | 1           | 2        | 2     | 6.74               | 8.14                 |
|                            | 6       |  | 300             | 2570                 | 1           | 2        | 2     | 5.14               | 6.21                 |
|                            | 7       |  | 165             | 880                  | 1           | 14       | 14    | 12.32              | 2.73                 |
|                            | 8       |  | 140             | 730                  | 1           | 57       | 57    | 41.61              | 9.24                 |
|                            | 9       |  | 140             | 630                  | 1           | 27       | 27    | 17.01              | 3.78                 |
| C10<br>SL: 1               | 1       |  | 16              | 2490                 | 1           | 2        | 2     | 4.98               | 7.86                 |
|                            | 2       |  | 16              | 3290                 | 1           | 2        | 2     | 6.58               | 10.39                |

LƯU Ý: THỐNG KÊ COT THÉP CHỈ MANG TÍNH CHẤT ĐỊNH HƯỚNG, NHÀ THẦU CẦN TRIỂN KHAI SHOPDRAWING ĐỂ CÓ HÌNH DẠNG VÀ KHỐI LƯỢNG CHÍNH XÁC.
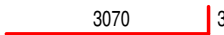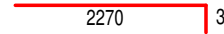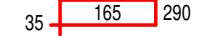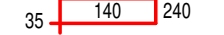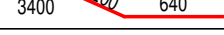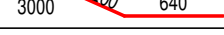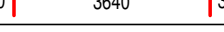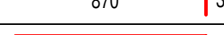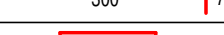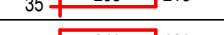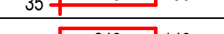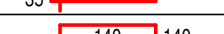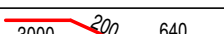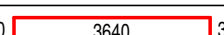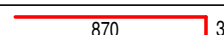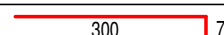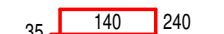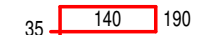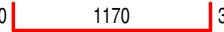
| TÊN CẦU KIỆN | SỐ HIỆU | HÌNH DẠNG, KÍCH THƯỚC                                                                 | ĐƯỜNG KÍNH (mm) | CHIỀU DÀI THANH (mm) | SỐ CẦU KIỆN | SỐ LƯỢNG |       | TỔNG CHIỀU DÀI (m) | TỔNG KHỐI LƯỢNG (kg) |
|--------------|---------|---------------------------------------------------------------------------------------|-----------------|----------------------|-------------|----------|-------|--------------------|----------------------|
|              |         |                                                                                       |                 |                      |             | 1 CK     | T. BỘ |                    |                      |
| C10<br>SL:1  | 3       |    | 16              | 4240                 | 1           | 4        | 4     | 16.96              | 26.77                |
|              | 4       |    | 16              | 3370                 | 1           | 2        | 2     | 6.74               | 10.64                |
|              | 5       |    | 16              | 2570                 | 1           | 2        | 2     | 5.14               | 8.11                 |
|              | 6       |    | 16              | 4240                 | 1           | 2        | 2     | 8.48               | 13.38                |
|              | 7       |    | 6               | 980                  | 1           | 14       | 14    | 13.72              | 3.05                 |
|              | 8       |    | 6               | 830                  | 1           | 57       | 57    | 47.31              | 10.50                |
| C11<br>SL:1  | 1       |    | 16              | 2490                 | 1           | 2        | 2     | 4.98               | 7.86                 |
|              | 2       |    | 16              | 3290                 | 1           | 2        | 2     | 6.58               | 10.39                |
|              | 3       |    | 16              | 4240                 | 1           | 4        | 4     | 16.96              | 26.77                |
|              | 4       |    | 16              | 3840                 | 1           | 8        | 8     | 30.72              | 48.49                |
|              | 5       |    | 16              | 4240                 | 1           | 2        | 2     | 8.48               | 13.38                |
|              | 6       |    | 14              | 1170                 | 1           | 2        | 2     | 2.34               | 2.83                 |
|              | 7       |    | 14              | 370                  | 1           | 2        | 2     | 0.74               | 0.89                 |
|              | 8       |    | 6               | 1030                 | 1           | 14       | 14    | 14.42              | 3.20                 |
|              | 9       |    | 6               | 930                  | 1           | 30       | 30    | 27.90              | 6.19                 |
|              | 10      |   | 6               | 830                  | 1           | 27       | 27    | 22.41              | 4.97                 |
|              | 11      |  | 6               | 630                  | 1           | 37       | 37    | 23.31              | 5.17                 |
| C12<br>SL:1  | 1       |  | 16              | 2490                 | 1           | 2        | 2     | 4.98               | 7.86                 |
|              | 2       |  | 16              | 3290                 | 1           | 2        | 2     | 6.58               | 10.39                |
|              | 3       |  | 16              | 4240                 | 1           | 4        | 4     | 16.96              | 26.77                |
|              | 4       |  | 16              | 3840                 | 1           | 8        | 8     | 30.72              | 48.49                |
|              | 5       |  | 16              | 4240                 | 1           | 2        | 2     | 8.48               | 13.38                |
|              | 6       |  | 14              | 1170                 | 1           | 2        | 2     | 2.34               | 2.83                 |
|              | 7       |  | 14              | 370                  | 1           | 2        | 2     | 0.74               | 0.89                 |
|              | 8       |  | 6               | 930                  | 1           | 14       | 14    | 13.02              | 2.89                 |
|              | 9       |  | 6               | 830                  | 1           | 30       | 30    | 24.90              | 5.53                 |
|              | 10      |  | 6               | 730                  | 1           | 27       | 27    | 19.71              | 4.37                 |
|              | 11      |  | 6               | 630                  | 1           | 37       | 37    | 23.31              | 5.17                 |
| CC1<br>SL:1  | 1       |  | 14              | 1770                 | 1           | 4        | 4     | 7.08               | 8.56                 |
|              | 2       |  | 6               | 630                  | 1           | 10       | 10    | 6.30               | 1.40                 |

| TỔNG HỢP CỐT THÉP CỘT |         |       |        |        |
|-----------------------|---------|-------|--------|--------|
| - Đường kính (mm):    | Ø6      | Ø12   | Ø14    | Ø16    |
| - Chiều dài (m):      | 953.16  | 35.02 | 220.2  | 632.84 |
| - Khối lượng (kg):    | 211.57  | 31.1  | 266.07 | 998.89 |
| - Chiều dài / 11.7    | -       | 3     | 19     | 55     |
|                       |         |       |        |        |
| - Nhóm Ø < 10:        | 211.57  | kg    |        |        |
| - Nhóm 10 <= Ø < 20:  | 1296.06 | kg    |        |        |
| - Tổng cộng:          | 1507.63 | kg    |        |        |

GHI CHÚ:

- CÁC ĐƠN VỊ THI CÔNG PHẢI PHỐI HỢP BẢN VẼ CỦA TẤT CẢ CÁC BỘ MÓN KHÁC NẾU THẤY SỰ KHÁC BIỆT PHẢI BÁO CHO ĐƠN VỊ THIẾT KẾ ĐỂ XỬ LÝ.

- KHI XỬ LÝ SỰ KHÁC BIỆT, PHẢI THỰC HIỆN ƯU TIÊN THEO THỨ TỰ GIỮA CÁC BỘ MÓN: KIẾN TRÚC → KẾT CẤU / BỘ MÓN KHÁC; HOẶC ƯU TIÊN TRONG CÙNG BỘ MÓN: CHI TIẾT → TỔNG THỂ

- CÁC SỐ LIỆU KÍCH THƯỚC PHẢI ĐƯỢC KIỂM TRA THỰC TẾ TẠI CÔNG TRÌNH, NẾU THẤY SỰ KHÁC BIỆT SƠ VỚI BẢN VẼ THI PHẢI BÁO CHO ĐƠN VỊ THIẾT KẾ.

HIỆU CHỈNH:

REV

NGÀY

NỘI DUNG

CHỦ ĐẦU TƯ:

CÔNG TY TNHH ĐẦU TƯ  
PHÚ VIỆT TÍN

ĐỊA CHỈ: LÔ 18-19 QUỐC LỘ 1A, XÃ DẦU GIẤY,  
TỈNH ĐỒNG NAI, VIỆT NAM

CTHĐT/V

ĐANG PHƯỚC BÌNH

ĐƠN VỊ THIẾT KẾ:

CÔNG TY CỔ PHẦN TƯ VẤN THIẾT KẾ  
BASE ARC

ĐỊA CHỈ: 138 ĐIỆN BIÊN PHŨ, PHƯỜNG TÂN ĐỊNH,  
TP. HỒ CHÍ MINH, VIỆT NAM

TỔNG GIÁM ĐỐC

TRẦN ĐỨC AN

CHỦ NHIỆM DỰ ÁN:

KTS. NGUYỄN THÀNH THÁI

CHỦ TRÌ THIẾT KẾ:

KS. NGÔ TÙNG THÀNH

THIẾT KẾ:

KS. NGUYỄN MINH DUY BẰNG

KIỂM TRA:

KS. NGÔ TÙNG THÀNH

DỰ ÁN:

KHU DÂN CƯ A1-C1 (ĐÔ THỊ DẦU GIẤY)  
ĐỊA ĐIỂM: XÃ DẦU GIẤY, TỈNH ĐỒNG NAI

CÔNG TRÌNH:

NHÀ Ở THƯƠNG MẠI LIÊN KỀ

HẠNG MỤC:

MẪU NHÀ T3\_2b

TÊN BẢN VẼ:

TKT CỘT-02

MỤC ĐÍCH PHÁT HÀNH:

BẢN VẼ MỜI THẦU

THIẾT KẾ CƠ SỞ

☒ THIẾT KẾ BẢN VẼ THI CÔNG

BẢN VẼ HOÀN CÔNG

HOÀN THÀNH

07/2025

TỶ LỆ

NTS

SỐ HIỆU BẢN VẼ

KC-55



| BẢNG THỐNG KÊ CỐT THÉP DẦM TẦNG 2 |         |                        |                 |                      |             |          |       |                    |                      |
|-----------------------------------|---------|------------------------|-----------------|----------------------|-------------|----------|-------|--------------------|----------------------|
| TÊN CẦU KIỆN                      | SỐ HIỆU | HÌNH DẠNG, KÍCH THƯỚC  | ĐƯỜNG KÍNH (mm) | CHIỀU DÀI THANH (mm) | SỐ CẦU KIỆN | SỐ LƯỢNG |       | TỔNG CHIỀU DÀI (m) | TỔNG KHỐI LƯỢNG (kg) |
|                                   |         |                        |                 |                      |             | 1 CK     | T. BỘ |                    |                      |
| 2D1<br>SL: 6                      | 1       | 390 1190 490           | 14              | 2070                 | 6           | 2        | 12    | 24.84              | 30.02                |
|                                   | 2       | 275 1140 375           | 14              | 1790                 | 6           | 2        | 12    | 21.48              | 25.96                |
|                                   | 3       | 60 140 190             | 6               | 780                  | 6           | 7        | 42    | 32.76              | 7.27                 |
| 2D2<br>SL: 2                      | 1       | 390 2740 390           | 14              | 3520                 | 2           | 1        | 2     | 7.04               | 8.51                 |
|                                   | 2       | 275 2690 275           | 14              | 3240                 | 2           | 1        | 2     | 6.48               | 7.83                 |
|                                   | 3       | 50 190 50              | 6               | 370                  | 2           | 17       | 34    | 12.58              | 2.79                 |
| 2D3<br>SL: 1                      | 1       | 390 2790 390           | 14              | 3570                 | 1           | 1        | 1     | 3.57               | 4.31                 |
|                                   | 2       | 275 2740 275           | 14              | 3290                 | 1           | 1        | 1     | 3.29               | 3.98                 |
|                                   | 3       | 50 190 50              | 6               | 370                  | 1           | 17       | 17    | 6.29               | 1.40                 |
| 2X1<br>SL: 1                      | 1       | 290 10740 240          | 14              | 11270                | 1           | 2        | 2     | 22.54              | 27.24                |
|                                   | 2       | 175 4870 355 3350 1845 | 14              | 10885                | 1           | 2        | 2     | 21.77              | 26.31                |
|                                   | 3       | 3325                   | 14              | 3325                 | 1           | 2        | 2     | 6.65               | 8.04                 |
|                                   | 4       | 3400                   | 14              | 3400                 | 1           | 1        | 1     | 3.40               | 4.11                 |
|                                   | 5       | 290 1420               | 14              | 1710                 | 1           | 2        | 2     | 3.42               | 4.13                 |
|                                   | 6       | 2400                   | 16              | 2400                 | 1           | 2        | 2     | 4.80               | 7.58                 |
|                                   | 7       | 60 140 340             | 6               | 1080                 | 1           | 32       | 32    | 34.56              | 7.67                 |
|                                   | 8       | 60 140 290             | 6               | 980                  | 1           | 22       | 22    | 21.56              | 4.79                 |
|                                   | 9       | 60 140 240             | 6               | 880                  | 1           | 14       | 14    | 12.32              | 2.73                 |
| 2X2<br>SL: 1                      | 1       | 240 3540 305 1300 290  | 16              | 5675                 | 1           | 1        | 1     | 5.68               | 8.96                 |
|                                   | 2       | 240 3540 305 5050 420  | 16              | 9555                 | 1           | 1        | 1     | 9.56               | 15.08                |
|                                   | 3       | 390 2040 305 4460 240  | 16              | 7435                 | 1           | 2        | 2     | 14.87              | 23.47                |
|                                   | 4       | 240 8840 285           | 16              | 9365                 | 1           | 1        | 1     | 9.36               | 14.78                |
|                                   | 5       | 240 5090 290           | 16              | 5620                 | 1           | 1        | 1     | 5.62               | 8.87                 |
|                                   | 6       | 285 6190 335           | 16              | 6810                 | 1           | 2        | 2     | 13.62              | 21.50                |
|                                   | 7       | 240 675                | 14              | 915                  | 1           | 2        | 2     | 1.83               | 2.21                 |
|                                   | 8       | 4150                   | 14              | 4150                 | 1           | 2        | 2     | 8.30               | 10.03                |
|                                   | 10      | 2300                   | 16              | 2300                 | 1           | 1        | 1     | 2.30               | 3.63                 |
|                                   | 11      | 1500 305 850           | 16              | 2655                 | 1           | 1        | 1     | 2.66               | 4.19                 |
|                                   | 12      | 60 140 240             | 6               | 880                  | 1           | 19       | 19    | 16.72              | 3.71                 |
|                                   | 13      | 60 140 290             | 6               | 980                  | 1           | 10       | 10    | 9.80               | 2.18                 |
|                                   | 14      | 50 290 50              | 6               | 470                  | 1           | 50       | 50    | 23.50              | 5.22                 |
|                                   | 15      | 60 140 390             | 6               | 1180                 | 1           | 11       | 11    | 12.98              | 2.88                 |
|                                   | 16      | 60 140 440             | 6               | 1280                 | 1           | 23       | 23    | 29.44              | 6.53                 |
|                                   | 17      | 60 120 240             | 6               | 840                  | 1           | 5        | 5     | 4.20               | 0.93                 |
|                                   | 10a     | 290 1370               | 16              | 1660                 | 1           | 1        | 1     | 1.66               | 2.62                 |
|                                   | 11a     | 290 1670               | 16              | 1960                 | 1           | 1        | 1     | 1.96               | 3.09                 |

| BẢNG THỐNG KÊ CỐT THÉP DẦM TẦNG 2 |         |                       |                 |                      |             |          |       |                    |                      |
|-----------------------------------|---------|-----------------------|-----------------|----------------------|-------------|----------|-------|--------------------|----------------------|
| TÊN CẦU KIỆN                      | SỐ HIỆU | HÌNH DẠNG, KÍCH THƯỚC | ĐƯỜNG KÍNH (mm) | CHIỀU DÀI THANH (mm) | SỐ CẦU KIỆN | SỐ LƯỢNG |       | TỔNG CHIỀU DÀI (m) | TỔNG KHỐI LƯỢNG (kg) |
|                                   |         |                       |                 |                      |             | 1 CK     | T. BỘ |                    |                      |
| 2X3<br>SL: 1                      | 1       | 390 5140 390          | 14              | 5920                 | 1           | 2        | 2     | 11.84              | 14.31                |
|                                   | 2       | 275 5090 275          | 14              | 5640                 | 1           | 2        | 2     | 11.28              | 13.63                |
|                                   | 3       | 3400                  | 14              | 3400                 | 1           | 2        | 2     | 6.80               | 8.22                 |
|                                   | 4       | 440 1320              | 14              | 1760                 | 1           | 2        | 2     | 3.52               | 4.25                 |
|                                   | 5       | 1320 440              | 14              | 1760                 | 1           | 2        | 2     | 3.52               | 4.25                 |
|                                   | 6       | 60 140 290            | 6               | 980                  | 1           | 33       | 33    | 32.34              | 7.18                 |
| 2X4<br>SL: 1                      | 1       | 240 3570 305 2070 290 | 14              | 6475                 | 1           | 2        | 2     | 12.95              | 15.65                |
|                                   | 2       | 240 4065              | 14              | 4305                 | 1           | 2        | 2     | 8.61               | 10.40                |
|                                   | 3       | 275 2190 275          | 14              | 2740                 | 1           | 2        | 2     | 5.48               | 6.62                 |
|                                   | 4       | 240 1070              | 14              | 1310                 | 1           | 1        | 1     | 1.31               | 1.58                 |
|                                   | 5       | 240 2020 305 800      | 16              | 3365                 | 1           | 2        | 2     | 6.73               | 10.62                |
|                                   | 6       | 60 140 240            | 6               | 880                  | 1           | 22       | 22    | 19.36              | 4.30                 |
|                                   | 7       | 60 140 290            | 6               | 980                  | 1           | 14       | 14    | 13.72              | 3.05                 |
| 2X5<br>SL: 1                      | 1       | 470 6240 370          | 16              | 7080                 | 1           | 2        | 2     | 14.16              | 22.35                |
|                                   | 2       | 335 6190 235          | 16              | 6760                 | 1           | 2        | 2     | 13.52              | 21.34                |
|                                   | 3       | 4100                  | 14              | 4100                 | 1           | 2        | 2     | 8.20               | 9.91                 |
|                                   | 4       | 390 1620              | 14              | 2010                 | 1           | 1        | 1     | 2.01               | 2.43                 |
|                                   | 5       | 1670 420              | 16              | 2090                 | 1           | 2        | 2     | 4.18               | 6.60                 |
|                                   | 6       | 60 140 390            | 6               | 1180                 | 1           | 36       | 36    | 42.48              | 9.43                 |
| 2Y1<br>SL: 1                      | 1       | 340 7940 290          | 14              | 8570                 | 1           | 2        | 2     | 17.14              | 20.71                |
|                                   | 2       | 275 5445 305 2145 275 | 14              | 8445                 | 1           | 2        | 2     | 16.89              | 20.41                |
|                                   | 3       | 3800                  | 16              | 3800                 | 1           | 1        | 1     | 3.80               | 6.00                 |
|                                   | 4       | 340 1520              | 14              | 1860                 | 1           | 1        | 1     | 1.86               | 2.25                 |
|                                   | 5       | 2150                  | 16              | 2150                 | 1           | 2        | 2     | 4.30               | 6.79                 |
|                                   | 6       | 60 140 340            | 6               | 1080                 | 1           | 37       | 37    | 39.96              | 8.87                 |
|                                   | 7       | 60 140 290            | 6               | 980                  | 1           | 14       | 14    | 13.72              | 3.05                 |
| 2Y2<br>SL: 1                      | 1       | 340 7940 290          | 16              | 8570                 | 1           | 2        | 2     | 17.14              | 27.05                |
|                                   | 2       | 335 5545 305 2045 290 | 16              | 8520                 | 1           | 2        | 2     | 17.04              | 26.89                |
|                                   | 3       | 3800                  | 14              | 3800                 | 1           | 1        | 1     | 3.80               | 4.59                 |
|                                   | 4       | 340 1520              | 14              | 1860                 | 1           | 1        | 1     | 1.86               | 2.25                 |
|                                   | 5       | 2150                  | 16              | 2150                 | 1           | 2        | 2     | 4.30               | 6.79                 |
|                                   | 6       | 60 140 340            | 6               | 1080                 | 1           | 33       | 33    | 35.64              | 7.91                 |
|                                   | 7       | 60 140 290            | 6               | 980                  | 1           | 14       | 14    | 13.72              | 3.05                 |
| 2Y3<br>SL: 1                      | 1       | 390 5570 305 2070 290 | 16              | 8625                 | 1           | 2        | 2     | 17.25              | 27.23                |
|                                   | 2       | 335 5545 305 2045 290 | 16              | 8520                 | 1           | 2        | 2     | 17.04              | 26.89                |
|                                   | 3       | 3800                  | 16              | 3800                 | 1           | 1        | 1     | 3.80               | 6.00                 |

GHI CHÚ:  
- CÁC ĐƠN VỊ THI CÔNG PHẢI PHỐI HỢP BẢN VẼ CỦA TẤT CẢ CÁC BỘ MÔN  
KHÁC NẾU THẤY SỰ KHÁC BIỆT PHẢI BẢO CHO ĐƠN VỊ THIẾT KẾ ĐỂ XỬ LÝ.  
- KHI XỬ LÝ SỰ KHÁC BIỆT, PHẢI THỰC HIỆN ƯU TIÊN THEO THỨ TỰ GIỮA CÁC  
BỘ MÔN: KIẾN TRÚC → KẾT CẤU / BỘ MÔN KHÁC; HOẶC ƯU TIÊN TRONG CÙNG  
BỘ MÔN: CHI TIẾT → TỔNG THỂ  
- CÁC SỐ LIỆU KÍCH THƯỚC PHẢI ĐƯỢC KIỂM TRA THỰC TẾ TẠI CÔNG TRÌNH,  
NẾU THẤY SỰ KHÁC BIỆT SƠ VỚI BẢN VẼ THI PHẢI BẢO CHO ĐƠN VỊ THIẾT KẾ.

HIỆU CHỈNH:  

|     |      |          |
|-----|------|----------|
| REV | NGÀY | NỘI DUNG |
|-----|------|----------|

CHỦ ĐẦU TƯ:  

CÔNG TY TNHH ĐẦU TƯ  
PHÚ VIỆT TÍN

ĐỊA CHỈ: LÔ 18-19 QUỐC LỘ 1A, XÃ DẦU GIẤY,  
TỈNH ĐỒNG NAI, VIỆT NAM

CĐTĐTVĐẠNG PHƯỚC BÌNH

ĐƠN VỊ THIẾT KẾ:  

CÔNG TY CỔ PHẦN TƯ VẤN THIẾT KẾ  
BASE ARC

ĐỊA CHỈ: 138 ĐIỆN BIÊN PHỦ, PHƯỜNG TÂN ĐỊNH,  
TP. HỒ CHÍ MINH, VIỆT NAM

TỔNG GIÁM ĐỐCTRẦN ĐỨC AN

CHỦ NHIỆM DỰ ÁN:

KTS. NGUYỄN THÀNH THÁI

CHỦ TRÌ THIẾT KẾ:

KS. NGÔ TÙNG THÀNH

THIẾT KẾ:

KS. NGUYỄN MINH DUY BẰNG

KIỂM TRA:

KS. NGÔ TÙNG THÀNH

DỰ ÁN:

KHU DÂN CƯ A1-C1 (ĐÔ THỊ DẦU GIẤY)

ĐỊA ĐIỂM: XÃ DẦU GIẤY, TỈNH ĐỒNG NAI

CÔNG TRÌNH:

NHÀ Ở THƯƠNG MẠI LIỀN KỀ

HẠNG MỤC:

MẪU NHÀ T3\_2b

TÊN BẢN VẼ:

THỐNG KÊ THÉP DẦM-02

MỤC ĐÍCH PHÁT HÀNH:

|                                     |                          |
|-------------------------------------|--------------------------|
| <input type="checkbox"/>            | BẢN VẼ MỜI THẦU          |
| <input type="checkbox"/>            | THIẾT KẾ CƠ SỞ           |
| <input checked="" type="checkbox"/> | THIẾT KẾ BẢN VẼ THI CÔNG |
| <input type="checkbox"/>            | BẢN VẼ HOÀN CÔNG         |

|                |         |
|----------------|---------|
| HOÀN THÀNH     | 07/2025 |
| TỶ LỆ          | NTS     |
| SỐ HIỆU BẢN VẼ | KC-57   |

| BẢNG THỐNG KÊ CỐT THÉP DẦM TẦNG 2 |         |                       |                 |                      |             |          |       |                    |                      |
|-----------------------------------|---------|-----------------------|-----------------|----------------------|-------------|----------|-------|--------------------|----------------------|
| TÊN CẤU KIỆN                      | SỐ HIỆU | HÌNH DẠNG, KÍCH THƯỚC | ĐƯỜNG KÍNH (mm) | CHIỀU DÀI THANH (mm) | SỐ CẤU KIỆN | SỐ LƯỢNG |       | TỔNG CHIỀU DÀI (m) | TỔNG KHỐI LƯỢNG (kg) |
|                                   |         |                       |                 |                      |             | 1 CK     | T. BỘ |                    |                      |
| 2Y3<br>SL: 1                      | 4       |                       | 14              | 2155                 | 1           | 2        | 2     | 4.31               | 5.21                 |
|                                   | 5       |                       | 6               | 1180                 | 1           | 33       | 33    | 38.94              | 8.64                 |
|                                   | 6       |                       | 6               | 980                  | 1           | 14       | 14    | 13.72              | 3.05                 |
| 2Y4<br>SL: 1                      | 1       |                       | 16              | 8720                 | 1           | 2        | 2     | 17.44              | 27.53                |
|                                   | 2       |                       | 16              | 8250                 | 1           | 2        | 2     | 16.50              | 26.04                |
|                                   | 3       |                       | 14              | 5000                 | 1           | 2        | 2     | 10.00              | 12.08                |
|                                   | 4       |                       | 16              | 2360                 | 1           | 1        | 1     | 2.36               | 3.72                 |
|                                   | 5       |                       | 16              | 2710                 | 1           | 2        | 2     | 5.42               | 8.55                 |
|                                   | 6       |                       | 6               | 1300                 | 1           | 4        | 4     | 5.20               | 1.15                 |
|                                   | 7       |                       | 6               | 1180                 | 1           | 43       | 43    | 50.74              | 11.26                |
| 2Y5<br>SL: 1                      | 1       |                       | 14              | 6065                 | 1           | 2        | 2     | 12.13              | 14.66                |
|                                   | 2       |                       | 14              | 6015                 | 1           | 2        | 2     | 12.03              | 14.54                |
|                                   | 3       |                       | 6               | 880                  | 1           | 36       | 36    | 31.68              | 7.03                 |
| 2Y6<br>SL: 1                      | 1       |                       | 14              | 4520                 | 1           | 2        | 2     | 9.04               | 10.92                |
|                                   | 2       |                       | 14              | 4290                 | 1           | 2        | 2     | 8.58               | 10.37                |
|                                   | 3       |                       | 16              | 1410                 | 1           | 1        | 1     | 1.41               | 2.23                 |
|                                   | 4       |                       | 16              | 1460                 | 1           | 1        | 1     | 1.46               | 2.30                 |
|                                   | 5       |                       | 6               | 980                  | 1           | 22       | 22    | 21.56              | 4.79                 |

| TỔNG HỢP CỐT THÉP DẦM TẦNG 2 |        |        |        |
|------------------------------|--------|--------|--------|
| - Đường kính (mm):           | Ø6     | Ø14    | Ø16    |
| - Chiều dài (m):             | 589.49 | 307.77 | 239.94 |
| - Khối lượng (kg):           | 130.86 | 371.92 | 378.69 |
| - Chiều dài / 11.7           | -      | 27     | 21     |
|                              |        |        |        |
| - Nhóm Ø < 10:               | 130.86 | kg     |        |
| - Nhóm 10 <= Ø < 20:         | 750.61 | kg     |        |
| - Tổng cộng:                 | 881.47 | kg     |        |

| BẢNG THỐNG KÊ CỐT THÉP DẦM TẦNG 3 |         |                       |                 |                      |             |          |       |                    |                      |
|-----------------------------------|---------|-----------------------|-----------------|----------------------|-------------|----------|-------|--------------------|----------------------|
| TÊN CẤU KIỆN                      | SỐ HIỆU | HÌNH DẠNG, KÍCH THƯỚC | ĐƯỜNG KÍNH (mm) | CHIỀU DÀI THANH (mm) | SỐ CẤU KIỆN | SỐ LƯỢNG |       | TỔNG CHIỀU DÀI (m) | TỔNG KHỐI LƯỢNG (kg) |
|                                   |         |                       |                 |                      |             | 1 CK     | T. BỘ |                    |                      |
| 3D1<br>SL: 4                      | 1       |                       | 14              | 2070                 | 4           | 2        | 8     | 16.56              | 20.01                |
|                                   | 2       |                       | 14              | 1790                 | 4           | 2        | 8     | 14.32              | 17.30                |
|                                   | 3       |                       | 6               | 780                  | 4           | 7        | 28    | 21.84              | 4.85                 |
| 3D2<br>SL: 2                      | 1       |                       | 14              | 3520                 | 2           | 1        | 2     | 7.04               | 8.51                 |
|                                   | 2       |                       | 14              | 3240                 | 2           | 1        | 2     | 6.48               | 7.83                 |
|                                   | 3       |                       | 6               | 370                  | 2           | 17       | 34    | 12.58              | 2.79                 |
| 3X1<br>SL: 1                      | 1       |                       | 14              | 11525                | 1           | 2        | 2     | 23.05              | 27.85                |
|                                   | 2       |                       | 14              | 11145                | 1           | 2        | 2     | 22.29              | 26.94                |
|                                   | 3       |                       | 16              | 3325                 | 1           | 1        | 1     | 3.32               | 5.25                 |
|                                   | 4       |                       | 14              | 1760                 | 1           | 1        | 1     | 1.76               | 2.13                 |
|                                   | 5       |                       | 16              | 2350                 | 1           | 2        | 2     | 4.70               | 7.42                 |
|                                   | 6       |                       | 6               | 1080                 | 1           | 33       | 33    | 35.64              | 7.91                 |
|                                   | 7       |                       | 6               | 980                  | 1           | 22       | 22    | 21.56              | 4.79                 |
|                                   | 8       |                       | 6               | 880                  | 1           | 15       | 15    | 13.20              | 2.93                 |
| 3X2<br>SL: 1                      | 1       |                       | 16              | 16605                | 1           | 1        | 1     | 16.60              | 26.21                |
|                                   | 2       |                       | 16              | 16110                | 1           | 1        | 1     | 16.11              | 25.43                |
|                                   | 3       |                       | 14              | 1010                 | 1           | 2        | 2     | 2.02               | 2.44                 |
|                                   | 4       |                       | 16              | 4150                 | 1           | 2        | 2     | 8.30               | 13.10                |
|                                   | 5       |                       | 16              | 1360                 | 1           | 1        | 1     | 1.36               | 2.15                 |
|                                   | 6       |                       | 16              | 2655                 | 1           | 1        | 1     | 2.66               | 4.19                 |
|                                   | 7       |                       | 16              | 2125                 | 1           | 1        | 1     | 2.12               | 3.35                 |
|                                   | 8       |                       | 6               | 880                  | 1           | 19       | 19    | 16.72              | 3.71                 |
|                                   | 9       |                       | 6               | 980                  | 1           | 24       | 24    | 23.52              | 5.22                 |
|                                   | 10      |                       | 6               | 470                  | 1           | 27       | 27    | 12.69              | 2.82                 |
|                                   | 11      |                       | 6               | 1080                 | 1           | 23       | 23    | 24.84              | 5.51                 |
|                                   | 12      |                       | 6               | 840                  | 1           | 5        | 5     | 4.20               | 0.93                 |
| 3X3<br>SL: 1                      | 1a      |                       | 16              | 5625                 | 1           | 1        | 1     | 5.62               | 8.88                 |
|                                   | 1b      |                       | 16              | 7285                 | 1           | 1        | 1     | 7.28               | 11.50                |
|                                   | 2a      |                       | 16              | 5640                 | 1           | 1        | 1     | 5.64               | 8.90                 |
|                                   | 2b      |                       | 16              | 6790                 | 1           | 1        | 1     | 6.79               | 10.72                |
|                                   | 1       |                       | 14              | 11500                | 1           | 2        | 2     | 23.00              | 27.79                |
|                                   | 2       |                       | 14              | 5640                 | 1           | 2        | 2     | 11.28              | 13.63                |
|                                   | 3       |                       | 14              | 4340                 | 1           | 2        | 2     | 8.68               | 10.49                |
|                                   | 4       |                       | 14              | 2490                 | 1           | 2        | 2     | 4.98               | 6.02                 |
|                                   | 5       |                       | 14              | 3400                 | 1           | 2        | 2     | 6.80               | 8.22                 |
|                                   | 6       |                       | 14              | 1710                 | 1           | 1        | 1     | 1.71               | 2.07                 |

|   |                            |
|---|----------------------------|
| GHI CHÚ:   |                            |
| - CÁC ĐƠN VỊ THI CÔNG PHẢI PHỐI HỢP BẢN VẼ CỦA TẤT CẢ CÁC BỘ MÔN KHÁC NẾU THẤY SỰ KHÁC BIỆT PHẢI BẢO CHO ĐƠN VỊ THIẾT KẾ ĐỂ XỬ LÝ.<br>- KHI XỬ LÝ SỰ KHÁC BIỆT, PHẢI THỰC HIỆN ƯU TIÊN THEO THỨ TỰ GIỮA CÁC BỘ MÔN: KIẾN TRÚC → KẾT CẤU / BỘ MÔN KHÁC; HOẶC ƯU TIÊN TRONG CÙNG BỘ MÔN: CHI TIẾT → TỔNG THỂ<br>- CÁC SỐ LIEU KỊCH THUỘC PHẢI ĐƯỢC KIỂM TRA THỰC TẾ TẠI CÔNG TRÌNH, NẾU THẤY SỰ KHÁC BIỆT SƠ VỚI BẢN VẼ THI PHẢI BẢO CHO ĐƠN VỊ THIẾT KẾ. |                            |
| HIỆU CHỈNH:   |                            |
| REV   | NỘI DUNG                   |
|   |                            |
| CHỦ ĐẦU TƯ:   |                            |
| CÔNG TY TNHH ĐẦU TƯ<br><b>PHÚ VIỆT TÍN</b><br>ĐỊA CHỈ: LÔ 18-19 QUỐC LỘ 1A, XÃ DẦU GIẤY, TỈNH ĐỒNG NAI, VIỆT NAM   |                            |
|   |                            |
| CTHĐT.V   | ĐẠNG PHƯỚC BÌNH            |
| ĐƠN VỊ THIẾT KẾ:   |                            |
| CÔNG TY CỔ PHẦN TƯ VẤN THIẾT KẾ<br><b>BASE ARC</b><br>ĐỊA CHỈ: 138 ĐIỆN BIÊN PHỦ, PHƯỜNG TÂN ĐỊNH, TP. HỒ CHÍ MINH, VIỆT NAM   |                            |
|   |                            |
| TỔNG GIÁM ĐỐC   |                            |
| TRẦN ĐỨC AN   |                            |
| CHỦ NHIỆM DỰ ÁN:   |                            |
| KTS. NGUYỄN THÀNH THÁI   |                            |
| CHỦ TRÌ THIẾT KẾ:   |                            |
| KS. NGÔ TÙNG THÀNH   |                            |
| THIẾT KẾ:   |                            |
| KS. NGUYỄN MINH DUY BẰNG   |                            |
| KIỂM TRA:   |                            |
| KS. NGÔ TÙNG THÀNH   |                            |
| DỰ ÁN:   |                            |
| KHU DÂN CƯ A1-C1 (ĐÔ THỊ DẦU GIẤY)<br>ĐỊA ĐIỂM: XÃ DẦU GIẤY, TỈNH ĐỒNG NAI   |                            |
| CÔNG TRÌNH:   |                            |
| NHÀ Ở THƯƠNG MẠI LIÊN KẾ   |                            |
| HẠNG MỤC:   |                            |
| MẪU NHÀ T3_2b   |                            |
| TÊN BẢN VẼ:   |                            |
| THỐNG KÊ THÉP DẦM-03   |                            |
| MỤC ĐÍCH PHÁT HÀNH:   |                            |
|   | BẢN VẼ MỜI THẦU            |
|   | THIẾT KẾ CƠ SỞ             |
|   | ✓ THIẾT KẾ BẢN VẼ THI CÔNG |
|   | BẢN VẼ HOÀN CÔNG           |
| HOÀN THÀNH   | 07/2025                    |
| TỶ LỆ   | NTS                        |
| SỐ HIỆU BẢN VẼ   | KC-58                      |

| BẢNG THỐNG KÊ CỐT THÉP DẦM TẦNG 3 |         |                       |                 |                      |             |          |       |                    |                      |
|-----------------------------------|---------|-----------------------|-----------------|----------------------|-------------|----------|-------|--------------------|----------------------|
| TÊN CẤU KIỆN                      | SỐ HIỆU | HÌNH DẠNG, KÍCH THƯỚC | ĐƯỜNG KÍNH (mm) | CHIỀU DÀI THANH (mm) | SỐ CẤU KIỆN | SỐ LƯỢNG |       | TỔNG CHIỀU DÀI (m) | TỔNG KHỐI LƯỢNG (kg) |
|                                   |         |                       |                 |                      |             | 1 CK     | T. BỘ |                    |                      |
| 3X3<br>SL: 1                      | 7       |                       | 16              | 2350                 | 1           | 1        | 1     | 2.35               | 3.71                 |
|                                   | 8       |                       | 16              | 3315                 | 1           | 2        | 2     | 6.63               | 10.46                |
|                                   | 9       |                       | 6               | 980                  | 1           | 34       | 34    | 33.32              | 7.40                 |
|                                   | 10      |                       | 6               | 1080                 | 1           | 12       | 12    | 12.96              | 2.88                 |
|                                   | 11      |                       | 6               | 880                  | 1           | 22       | 22    | 19.36              | 4.30                 |
| 3X4<br>SL: 1                      | 1       |                       | 16              | 6920                 | 1           | 2        | 2     | 13.84              | 21.84                |
|                                   | 2       |                       | 16              | 6760                 | 1           | 2        | 2     | 13.52              | 21.34                |
|                                   | 3       |                       | 16              | 4100                 | 1           | 1        | 1     | 4.10               | 6.47                 |
|                                   | 4       |                       | 16              | 1960                 | 1           | 1        | 1     | 1.96               | 3.09                 |
|                                   | 5       |                       | 14              | 1960                 | 1           | 2        | 2     | 3.92               | 4.74                 |
|                                   | 6       |                       | 6               | 1080                 | 1           | 36       | 36    | 38.88              | 8.63                 |
| 3Y1<br>SL: 1                      | 1       |                       | 14              | 8575                 | 1           | 2        | 2     | 17.15              | 20.72                |
|                                   | 2       |                       | 14              | 8440                 | 1           | 2        | 2     | 16.88              | 20.40                |
|                                   | 3       |                       | 16              | 3800                 | 1           | 1        | 1     | 3.80               | 6.00                 |
|                                   | 4       |                       | 14              | 1860                 | 1           | 1        | 1     | 1.86               | 2.25                 |
|                                   | 5       |                       | 14              | 2155                 | 1           | 2        | 2     | 4.31               | 5.21                 |
|                                   | 6       |                       | 6               | 1080                 | 1           | 37       | 37    | 39.96              | 8.87                 |
|                                   | 7       |                       | 6               | 980                  | 1           | 14       | 14    | 13.72              | 3.05                 |
| 3Y2<br>SL: 1                      | 1       |                       | 14              | 8570                 | 1           | 2        | 2     | 17.14              | 20.71                |
|                                   | 2       |                       | 14              | 8445                 | 1           | 2        | 2     | 16.89              | 20.41                |
|                                   | 3       |                       | 14              | 3800                 | 1           | 2        | 2     | 7.60               | 9.18                 |
|                                   | 4       |                       | 14              | 1860                 | 1           | 1        | 1     | 1.86               | 2.25                 |
|                                   | 5       |                       | 16              | 2100                 | 1           | 2        | 2     | 4.20               | 6.63                 |
|                                   | 6       |                       | 6               | 1080                 | 1           | 37       | 37    | 39.96              | 8.87                 |
|                                   | 7       |                       | 6               | 980                  | 1           | 14       | 14    | 13.72              | 3.05                 |
| 3Y3<br>SL: 1                      | 1       |                       | 16              | 8575                 | 1           | 2        | 2     | 17.15              | 27.07                |
|                                   | 2       |                       | 16              | 8515                 | 1           | 2        | 2     | 17.03              | 26.88                |
|                                   | 3       |                       | 16              | 3800                 | 1           | 1        | 1     | 3.80               | 6.00                 |
|                                   | 4       |                       | 14              | 1860                 | 1           | 1        | 1     | 1.86               | 2.25                 |
|                                   | 5       |                       | 16              | 2105                 | 1           | 2        | 2     | 4.21               | 6.64                 |
|                                   | 6       |                       | 6               | 1080                 | 1           | 33       | 33    | 35.64              | 7.91                 |
|                                   | 7       |                       | 6               | 980                  | 1           | 14       | 14    | 13.72              | 3.05                 |
| 3Y4<br>SL: 1                      | 1       |                       | 14              | 8525                 | 1           | 2        | 2     | 17.05              | 20.60                |
|                                   | 2       |                       | 14              | 8470                 | 1           | 2        | 2     | 16.94              | 20.47                |
|                                   | 3       |                       | 16              | 5100                 | 1           | 1        | 1     | 5.10               | 8.05                 |
|                                   | 4       |                       | 14              | 2310                 | 1           | 1        | 1     | 2.31               | 2.79                 |

| BẢNG THỐNG KÊ CỐT THÉP DẦM TẦNG 3 |         |                       |                 |                      |             |          |       |                    |                      |
|-----------------------------------|---------|-----------------------|-----------------|----------------------|-------------|----------|-------|--------------------|----------------------|
| TÊN CẤU KIỆN                      | SỐ HIỆU | HÌNH DẠNG, KÍCH THƯỚC | ĐƯỜNG KÍNH (mm) | CHIỀU DÀI THANH (mm) | SỐ CẤU KIỆN | SỐ LƯỢNG |       | TỔNG CHIỀU DÀI (m) | TỔNG KHỐI LƯỢNG (kg) |
|                                   |         |                       |                 |                      |             | 1 CK     | T. BỘ |                    |                      |
| 3Y4<br>SL: 1                      | 5       |                       | 16              | 2710                 | 1           | 1        | 1     | 2.71               | 4.28                 |
|                                   | 6       |                       | 6               | 1000                 | 1           | 2        | 2     | 2.00               | 0.44                 |
|                                   | 7       |                       | 6               | 980                  | 1           | 22       | 22    | 21.56              | 4.79                 |
|                                   | 8       |                       | 6               | 1080                 | 1           | 22       | 22    | 23.76              | 5.27                 |
| 3Y5<br>SL: 1                      | 1       |                       | 14              | 4520                 | 1           | 2        | 2     | 9.04               | 10.92                |
|                                   | 2       |                       | 14              | 4390                 | 1           | 2        | 2     | 8.78               | 10.61                |
|                                   | 3       |                       | 6               | 980                  | 1           | 22       | 22    | 21.56              | 4.79                 |

| TỔNG HỢP CỐT THÉP DẦM TẦNG 3 |        |        |        |
|------------------------------|--------|--------|--------|
| - Đường kính (mm):           | Ø6     | Ø14    | Ø16    |
| - Chiều dài (m):             | 516.91 | 276.62 | 197.84 |
| - Khối lượng (kg):           | 114.76 | 334.27 | 312.3  |
| - Chiều dài / 11.7           | -      | 24     | 17     |
|                              |        |        |        |
| - Nhóm Ø < 10:               | 114.76 | kg     |        |
| - Nhóm 10 <= Ø < 20:         | 646.57 | kg     |        |
| - Tổng cộng:                 | 761.33 | kg     |        |

GHI CHÚ:  
- CÁC ĐƠN VỊ THI CÔNG PHẢI PHỐI HỢP BẢN VẼ CỦA TẤT CẢ CÁC BỘ MÔN KHÁC NẾU THẤY SỰ KHÁC BIỆT PHẢI BẢO CHO ĐƠN VỊ THIẾT KẾ ĐỂ XỬ LÝ.  
- KHI XỬ LÝ SỰ KHÁC BIỆT, PHẢI THỰC HIỆN ƯU TIÊN THEO THỨ TỰ GIỮA CÁC BỘ MÔN: KIẾN TRÚC → KẾT CẤU / BỘ MÔN KHÁC; HOẶC ƯU TIÊN TRONG CÙNG BỘ MÔN: CHI TIẾT → TỔNG THỂ  
- CÁC SỐ LIỆU KÍCH THƯỚC PHẢI ĐƯỢC KIỂM TRA THỰC TẾ TẠI CÔNG TRÌNH, NẾU THẤY SỰ KHÁC BIỆT SƠ VỚI BẢN VẼ THI PHẢI BẢO CHO ĐƠN VỊ THIẾT KẾ.

HIỆU CHỈNH:  

|     |      |          |
|-----|------|----------|
| REV | NGÀY | NỘI DUNG |
|-----|------|----------|

CHỦ ĐẦU TƯ:  

CÔNG TY TNHH ĐẦU TƯ  
**PHÚ VIỆT TÍN**  
ĐỊA CHỈ: LÔ 18-19 QUỐC LỘ 1A, XÃ DẦU GIẤY, TỈNH ĐỒNG NAI, VIỆT NAM

CTHĐTVPĐẠNG PHƯỚC BÌNH

ĐƠN VỊ THIẾT KẾ:  

CÔNG TY CỔ PHẦN TƯ VẤN THIẾT KẾ  
**BASE ARC**  
ĐỊA CHỈ: 138 ĐIỆN BIÊN PHỦ, PHƯỜNG TÂN ĐỊNH, TP. HỒ CHÍ MINH, VIỆT NAM

TỔNG GIÁM ĐỐCTRẦN ĐỨC AN

CHỦ NHIỆM DỰ ÁN:

KTS. NGUYỄN THÀNH THÁI

CHỦ TRÌ THIẾT KẾ:

KS. NGÔ TÙNG THÀNH

THIẾT KẾ:

KS. NGUYỄN MINH DUY BẰNG

KIỂM TRA:

KS. NGÔ TÙNG THÀNH

DỰ ÁN:

KHU DÂN CƯ A1-C1 (ĐÔ THỊ DẦU GIẤY)  
ĐỊA ĐIỂM: XÃ DẦU GIẤY, TỈNH ĐỒNG NAI

CÔNG TRÌNH:

NHÀ Ở THƯƠNG MẠI LIỀN KỀ

HẠNG MỤC:

MẪU NHÀ T3\_2b


























TÊN BẢN VẼ:















THỐNG KÊ THÉP DẦM-04

MỤC ĐÍCH PHÁT HÀNH:

|                                     |                          |
|-------------------------------------|--------------------------|
| <input type="checkbox"/>            | BẢN VẼ MỜI THẦU          |
| <input type="checkbox"/>            | THIẾT KẾ CƠ SỞ           |
| <input checked="" type="checkbox"/> | THIẾT KẾ BẢN VẼ THI CÔNG |
| <input type="checkbox"/>            | BẢN VẼ HOÀN CÔNG         |

|                |         |
|----------------|---------|
| HOÀN THÀNH     | 07/2025 |
| TỶ LỆ          | NTS     |
| SỐ HIỆU BẢN VẼ | KC-59   |
           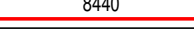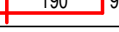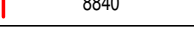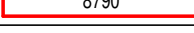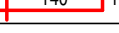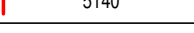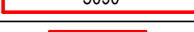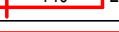 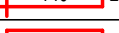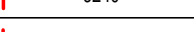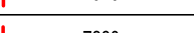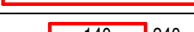 
| TÊN CẤU KIỆN | SỐ HIỆU | HÌNH DẠNG, KÍCH THƯỚC                                                                         | ĐƯỜNG KÍNH (mm) | CHIỀU DÀI THANH (mm) | SỐ CẤU KIỆN | SỐ LƯỢNG |       | TỔNG CHIỀU DÀI (m) | TỔNG KHỐI LƯỢNG (kg) |
|--------------|---------|-----------------------------------------------------------------------------------------------|-----------------|----------------------|-------------|----------|-------|--------------------|----------------------|
|              |         |                                                                                               |                 |                      |             | 1 CK     | T. BỘ |                    |                      |
| DM1<br>SL: 1 | 1       | 310  310     | 12              | 9460                 | 1           | 2        | 2     | 18.92              | 16.80                |
|              | 2       | 215  215     | 12              | 9220                 | 1           | 2        | 2     | 18.44              | 16.37                |
|              | 3       | 240  190     | 6               | 900                  | 1           | 65       | 65    | 58.50              | 12.98                |
| DM2<br>SL: 1 | 1       | 190  190     | 12              | 4520                 | 1           | 2        | 2     | 9.04               | 8.03                 |
|              | 2       | 190  165     | 12              | 4445                 | 1           | 2        | 2     | 8.89               | 7.89                 |
|              | 3       | 240  190     | 6               | 900                  | 1           | 26       | 26    | 23.40              | 5.19                 |
| DM3<br>SL: 1 | 1       | 310  310     | 12              | 6860                 | 1           | 2        | 2     | 13.72              | 12.18                |
|              | 2       | 215  215     | 12              | 6620                 | 1           | 2        | 2     | 13.24              | 11.75                |
|              | 3       | 240  190     | 6               | 900                  | 1           | 40       | 40    | 36.00              | 7.99                 |
| DM4<br>SL: 1 | 1       | 190  190     | 12              | 4320                 | 1           | 2        | 2     | 8.64               | 7.67                 |
|              | 2       | 190  190     | 12              | 4270                 | 1           | 2        | 2     | 8.54               | 7.58                 |
|              | 3       | 240  190     | 6               | 900                  | 1           | 25       | 25    | 22.50              | 4.99                 |
| GT1<br>SL: 1 | 1       | 90  90       | 10              | 15520                | 1           | 1        | 1     | 15.52              | 9.57                 |
|              | 2       |  14940       | 10              | 15340                | 1           | 1        | 1     | 15.34              | 9.46                 |
|              | 3       | 50  50       | 6               | 255                  | 1           | 76       | 76    | 19.38              | 4.30                 |
| GT2<br>SL: 1 | 1       | 90  90      | 10              | 8620                 | 1           | 2        | 2     | 17.24              | 10.63                |
|              | 2       |  8440      | 10              | 8440                 | 1           | 2        | 2     | 16.88              | 10.41                |
|              | 3       | 60  90     | 6               | 680                  | 1           | 44       | 44    | 29.92              | 6.64                 |
| MX1<br>SL: 1 | 1       | 140  140   | 14              | 9120                 | 1           | 2        | 2     | 18.24              | 22.04                |
|              | 2       | 140  140   | 14              | 9070                 | 1           | 2        | 2     | 18.14              | 21.92                |
|              | 3       | 60  140    | 6               | 680                  | 1           | 68       | 68    | 46.24              | 10.26                |
| MX2<br>SL: 1 | 1       | 240  240   | 14              | 5620                 | 1           | 2        | 2     | 11.24              | 13.58                |
|              | 2       | 240  240   | 14              | 5570                 | 1           | 2        | 2     | 11.14              | 13.46                |
|              | 3       | 60  240    | 6               | 880                  | 1           | 29       | 29    | 25.52              | 5.66                 |
| MX3<br>SL: 1 | 1       | 240  240   | 14              | 16540                | 1           | 2        | 2     | 33.08              | 39.97                |
|              | 2       | 240  15475 | 14              | 16275                | 1           | 2        | 2     | 32.55              | 39.33                |
|              | 3       | 60  240    | 6               | 880                  | 1           | 87       | 87    | 76.56              | 16.99                |
|              | 4       | 60  240    | 6               | 840                  | 1           | 5        | 5     | 4.20               | 0.93                 |
| MX4<br>SL: 1 | 1       | 290  290   | 14              | 6820                 | 1           | 2        | 2     | 13.64              | 16.48                |
|              | 2       | 275  275   | 14              | 6740                 | 1           | 2        | 2     | 13.48              | 16.29                |
|              | 3       | 60  290    | 6               | 980                  | 1           | 36       | 36    | 35.28              | 7.83                 |
| MY1<br>SL: 1 | 1       | 240  240   | 14              | 8420                 | 1           | 2        | 2     | 16.84              | 20.35                |
|              | 2       | 240  240   | 14              | 8370                 | 1           | 2        | 2     | 16.74              | 20.23                |
|              | 3       | 60  240    | 6               | 880                  | 1           | 48       | 48    | 42.24              | 9.38                 |
| MY2<br>SL: 1 | 1       | 240  240   | 14              | 8420                 | 1           | 2        | 2     | 16.84              | 20.35                |
|              | 2       | 240  240   | 14              | 8370                 | 1           | 2        | 2     | 16.74              | 20.23                |
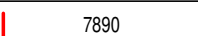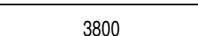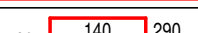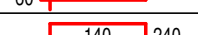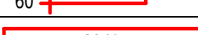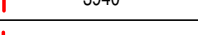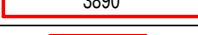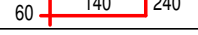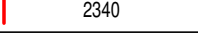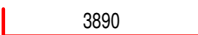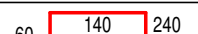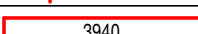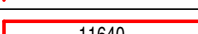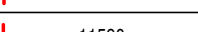
| BẢNG THỐNG KÊ CỐT THÉP DÀM MÁI |         |                                                                                      |                 |                      |             |          |       |                    |                      |  |
|--------------------------------|---------|--------------------------------------------------------------------------------------|-----------------|----------------------|-------------|----------|-------|--------------------|----------------------|--|
| TÊN CẤU KIỆN                   | SỐ HIỆU | HÌNH DẠNG, KÍCH THƯỚC                                                                | ĐƯỜNG KÍNH (mm) | CHIỀU DÀI THANH (mm) | SỐ CẤU KIỆN | SỐ LƯỢNG |       | TỔNG CHIỀU DÀI (m) | TỔNG KHỐI LƯỢNG (kg) |  |
|                                |         |                                                                                      |                 |                      |             | 1 CK     | T. BỘ |                    |                      |  |
| MY2 SL: 1                      | 3       |   | 6               | 880                  | 1           | 47       | 47    | 41.36              | 9.18                 |  |
| MY3 SL: 1                      | 1       |   | 14              | 8475                 | 1           | 2        | 2     | 16.95              | 20.48                |  |
|                                | 2       |   | 14              | 8405                 | 1           | 2        | 2     | 16.81              | 20.31                |  |
|                                | 3       |   | 16              | 3800                 | 1           | 1        | 1     | 3.80               | 6.00                 |  |
|                                | 4       |   | 6               | 980                  | 1           | 33       | 33    | 32.34              | 7.18                 |  |
|                                | 5       |   | 6               | 880                  | 1           | 14       | 14    | 12.32              | 2.73                 |  |
| MY4 SL: 1                      | 1       |   | 14              | 4420                 | 1           | 2        | 2     | 8.84               | 10.68                |  |
|                                | 2       |   | 14              | 4370                 | 1           | 2        | 2     | 8.74               | 10.56                |  |
|                                | 3       |   | 6               | 880                  | 1           | 22       | 22    | 19.36              | 4.30                 |  |
| MY5 SL: 1                      | 1       |   | 14              | 2820                 | 1           | 2        | 2     | 5.64               | 6.82                 |  |
|                                | 2       |   | 14              | 2770                 | 1           | 2        | 2     | 5.54               | 6.69                 |  |
|                                | 3       |   | 6               | 880                  | 1           | 14       | 14    | 12.32              | 2.73                 |  |
| MY6 SL: 1                      | 2       |   | 14              | 4370                 | 1           | 2        | 2     | 8.74               | 10.56                |  |
|                                | 3       |   | 6               | 880                  | 1           | 19       | 19    | 16.72              | 3.71                 |  |
|                                | 4       |   | 14              | 4420                 | 1           | 2        | 2     | 8.84               | 10.68                |  |
| PA1 - M1 SL: 1                 | 1       |   | 14              | 12680                | 1           | 1        | 1     | 12.68              | 15.32                |  |
|                                | 2       |   | 14              | 12630                | 1           | 1        | 1     | 12.63              | 15.26                |  |
|                                | 3       |  | 6               | 420                  | 1           | 67       | 67    | 28.14              | 6.25                 |  |

| TỔNG HỢP CỐT THÉP DẦM MÁI |        |       |       |        |     |
|---------------------------|--------|-------|-------|--------|-----|
| - Đường kính (mm):        | Ø6     | Ø10   | Ø12   | Ø14    | Ø16 |
| - Chiều dài (m):          | 582.3  | 64.98 | 99.43 | 324.08 | 3.8 |
| - Khối lượng (kg):        | 129.22 | 40.07 | 88.27 | 391.59 | 6   |
| - Chiều dài / 11.7        | -      | 6     | 9     | 28     | 1   |
|                           |        |       |       |        |     |
| - Nhóm Ø < 10:            | 129.22 | kg    |       |        |     |
| - Nhóm 10 <= Ø < 20:      | 525.93 | kg    |       |        |     |
| - Tổng cộng:              | 655.15 | kg    |       |        |     |

[illegible]

| BẢNG THỐNG KÊ CỐT THÉP SÀN |         |                                                 |             |        |        |        |                        |          |      |                    |                   |
|----------------------------|---------|-------------------------------------------------|-------------|--------|--------|--------|------------------------|----------|------|--------------------|-------------------|
| TÊN C.KIỆN                 | SỐ HIỆU | HÌNH DẠNG                                       | Đ.KINH (mm) | A (mm) | B (mm) | C (mm) | CHIỀU DÀI 1 THANH (mm) | SỐ LƯỢNG |      | TỔNG CHIỀU DÀI (m) | TỔNG T.LƯỢNG (kg) |
|                            |         |                                                 |             |        |        |        |                        | 1 C.KIỆN | T.BỘ |                    |                   |
| M                          |         |                                                 |             |        |        |        |                        |          |      |                    |                   |
| M - SL: 01                 |         | <div><div>A</div><div>B</div><div>C</div></div> | 6           | 60     | 660    | 60     | 780                    | 112      | 112  | 87.36              | 19.39             |
| M - SL: 01                 |         | <div><div>A</div></div>                         | 6           | 1500   | 0      | 0      | 1500                   | 2        | 2    | 3.00               | 0.67              |
| M - SL: 01                 |         | <div><div>A</div></div>                         | 6           | 1900   | 0      | 0      | 1900                   | 2        | 2    | 3.80               | 0.84              |
| M - SL: 01                 |         | <div><div>A</div></div>                         | 6           | 3500   | 0      | 0      | 3500                   | 2        | 2    | 7.00               | 1.55              |
| M - SL: 01                 |         | <div><div>A</div></div>                         | 6           | 3800   | 0      | 0      | 3800                   | 2        | 2    | 7.60               | 1.69              |
| M - SL: 01                 |         | <div><div>A</div></div>                         | 6           | 3993   | 0      | 0      | 3993                   | 2        | 2    | 7.99               | 1.77              |
| M - SL: 01                 |         | <div><div>A</div></div>                         | 6           | 4015   | 0      | 0      | 4015                   | 2        | 2    | 8.03               | 1.78              |
| M - SL: 01                 |         | <div><div>A</div><div>B</div><div>C</div></div> | 6           | 60     | 4460   | 60     | 4580                   | 3        | 3    | 13.74              | 3.05              |
| M - SL: 01                 |         | <div><div>A</div><div>B</div><div>C</div></div> | 6           | 60     | 4660   | 60     | 4780                   | 3        | 3    | 14.34              | 3.18              |
| M - SL: 01                 |         | <div><div>A</div></div>                         | 6           | 6100   | 0      | 0      | 6100                   | 2        | 2    | 12.20              | 2.71              |
| M - SL: 01                 |         | <div><div>A</div><div>B</div><div>C</div></div> | 6           | 60     | 6770   | 60     | 6890                   | 3        | 3    | 20.67              | 4.59              |
| M - SL: 01                 |         | <div><div>A</div></div>                         | 6           | 9460   | 0      | 0      | 9460                   | 2        | 2    | 18.92              | 4.20              |
| M - SL: 01                 |         | <div><div>A</div><div>B</div><div>C</div></div> | 6           | 60     | 9449   | 60     | 9569                   | 3        | 3    | 28.71              | 6.37              |
| M - SL: 01                 |         |                                                 | 8           | 170    | 500    | 70     | 740                    | 121      | 121  | 89.54              | 35.33             |
| M - SL: 01                 |         | <div><div>A</div><div>B</div><div>C</div></div> | 8           | 70     | 2300   | 70     | 2440                   | 21       | 21   | 51.24              | 20.22             |
| M - SL: 01                 |         | <div><div>A</div><div>B</div><div>C</div></div> | 8           | 70     | 3400   | 70     | 3540                   | 14       | 14   | 49.56              | 19.56             |
| M - SL: 01                 |         | <div><div>A</div><div>B</div><div>C</div></div> | 8           | 70     | 11600  | 70     | 11740                  | 2        | 2    | 23.48              | 9.26              |
| M - SL: 01                 |         | <div><div>A</div><div>B</div><div>C</div></div> | 10          | 230    | 660    | 130    | 1020                   | 120      | 120  | 122.40             | 75.46             |
| M - SL: 01                 |         | <div><div>A</div><div>B</div><div>C</div></div> | 10          | 330    | 2300   | 330    | 2960                   | 16       | 16   | 47.36              | 29.20             |
| M - SL: 01                 |         | <div><div>A</div><div>B</div><div>C</div></div> | 10          | 330    | 3400   | 330    | 4060                   | 10       | 10   | 40.60              | 25.03             |
| T2                         |         |                                                 |             |        |        |        |                        |          |      |                    |                   |
| T2 - SL: 01                |         | <div><div>A</div></div>                         | 6           | 1000   | 0      | 0      | 1000                   | 15       | 15   | 15.00              | 3.33              |
| T2 - SL: 01                |         | <div><div>A</div></div>                         | 6           | 1100   | 0      | 0      | 1100                   | 9        | 9    | 9.90               | 2.20              |
| T2 - SL: 01                |         | <div><div>A</div></div>                         | 6           | 1200   | 0      | 0      | 1200                   | 14       | 14   | 16.80              | 3.73              |
| T2 - SL: 01                |         | <div><div>A</div></div>                         | 6           | 1300   | 0      | 0      | 1300                   | 8        | 8    | 10.40              | 2.31              |
| T2 - SL: 01                |         | <div><div>A</div></div>                         | 6           | 1400   | 0      | 0      | 1400                   | 13       | 13   | 18.20              | 4.04              |
| T2 - SL: 01                |         | <div><div>A</div></div>                         | 6           | 1402   | 0      | 0      | 1402                   | 9        | 9    | 12.62              | 2.80              |
| T2 - SL: 01                |         | <div><div>A</div></div>                         | 6           | 1500   | 0      | 0      | 1500                   | 12       | 12   | 18.00              | 4.00              |
| T2 - SL: 01                |         | <div><div>A</div></div>                         | 6           | 1548   | 0      | 0      | 1548                   | 9        | 9    | 13.93              | 3.09              |
| T2 - SL: 01                |         | <div><div>A</div></div>                         | 6           | 1850   | 0      | 0      | 1850                   | 5        | 5    | 9.25               | 2.05              |
| T2 - SL: 01                |         | <div><div>A</div></div>                         | 6           | 1897   | 0      | 0      | 1897                   | 16       | 16   | 30.35              | 6.74              |
| T2 - SL: 01                |         | <div><div>A</div></div>                         | 6           | 1900   | 0      | 0      | 1900                   | 2        | 2    | 3.80               | 0.84              |
| T2 - SL: 01                |         | <div><div>A</div></div>                         | 6           | 2000   | 0      | 0      | 2000                   | 9        | 9    | 18.00              | 4.00              |
| T2 - SL: 01                |         | <div><div>A</div></div>                         | 6           | 2100   | 0      | 0      | 2100                   | 9        | 9    | 18.90              | 4.19              |
| T2 - SL: 01                |         | <div><div>A</div></div>                         | 6           | 2300   | 0      | 0      | 2300                   | 8        | 8    | 18.40              | 4.08              |
| T2 - SL: 01                |         | <div><div>A</div></div>                         | 6           | 2600   | 0      | 0      | 2600                   | 8        | 8    | 20.80              | 4.62              |
| T2 - SL: 01                |         | <div><div>A</div></div>                         | 6           | 2800   | 0      | 0      | 2800                   | 13       | 13   | 36.40              | 8.08              |
| T2 - SL: 01                |         | <div><div>A</div></div>                         | 6           | 3300   | 0      | 0      | 3300                   | 9        | 9    | 29.70              | 6.59              |
| T2 - SL: 01                |         | <div><div>A</div></div>                         | 6           | 3500   | 0      | 0      | 3500                   | 12       | 12   | 42.00              | 9.32              |
| T2 - SL: 01                |         | <div><div>A</div></div>                         | 6           | 3600   | 0      | 0      | 3600                   | 14       | 14   | 50.40              | 11.19             |
| T2 - SL: 01                |         | <div><div>A</div></div>                         | 6           | 4000   | 0      | 0      | 4000                   | 23       | 23   | 92.00              | 20.42             |
| T2 - SL: 01                |         | <div><div>A</div></div>                         | 6           | 5300   | 0      | 0      | 5300                   | 5        | 5    | 26.50              | 5.88              |
| T2 - SL: 01                |         | <div><div>A</div></div>                         | 6           | 5900   | 0      | 0      | 5900                   | 4        | 4    | 23.60              | 5.24              |
| T2 - SL: 01                |         | <div><div>A</div><div>B</div><div>C</div></div> | 8           | 70     | 1150   | 170    | 1390                   | 36       | 36   | 50.04              | 19.74             |
| T2 - SL: 01                |         | <div><div>A</div><div>B</div><div>C</div></div> | 8           | 70     | 2750   | 70     | 2890                   | 5        | 5    | 14.45              | 5.70              |
| T2 - SL: 01                |         | <div><div>A</div><div>B</div><div>C</div></div> | 8           | 70     | 2794   | 70     | 2934                   | 10       | 10   | 29.34              | 11.58             |

| BẢNG THỐNG KÊ CỐT THÉP SÀN |         |                                                 |             |        |        |        |                        |          |      |                    |                   |
|----------------------------|---------|-------------------------------------------------|-------------|--------|--------|--------|------------------------|----------|------|--------------------|-------------------|
| TÊN C.KIỆN                 | SỐ HIỆU | HÌNH DẠNG                                       | Đ.KINH (mm) | A (mm) | B (mm) | C (mm) | CHIỀU DÀI 1 THANH (mm) | SỐ LƯỢNG |      | TỔNG CHIỀU DÀI (m) | TỔNG T.LƯỢNG (kg) |
|                            |         |                                                 |             |        |        |        |                        | 1 C.KIỆN | T.BỘ |                    |                   |
| T2 - SL: 01                |         | <div><div>A</div><div>B</div><div>C</div></div> | 10          | 230    | 650    | 80     | 960                    | 21       | 21   | 20.16              | 12.43             |
| T2 - SL: 01                |         | <div><div>A</div><div>B</div><div>C</div></div> | 10          | 100    | 1050   | 110    | 1260                   | 22       | 22   | 27.72              | 17.09             |
| T2 - SL: 01                |         | <div><div>A</div><div>B</div><div>C</div></div> | 10          | 230    | 1000   | 110    | 1340                   | 30       | 30   | 40.20              | 24.78             |
| T2 - SL: 01                |         | <div><div>A</div><div>B</div><div>C</div></div> | 10          | 230    | 1050   | 100    | 1380                   | 18       | 18   | 24.84              | 15.31             |
| T2 - SL: 01                |         | <div><div>A</div><div>B</div><div>C</div></div> | 10          | 230    | 1350   | 110    | 1690                   | 27       | 27   | 45.63              | 28.13             |
| T2 - SL: 01                |         | <div><div>A</div><div>B</div><div>C</div></div> | 10          | 330    | 1350   | 110    | 1790                   | 13       | 13   | 23.27              | 14.35             |
| T2 - SL: 01                |         | <div><div>A</div><div>B</div><div>C</div></div> | 10          | 230    | 1650   | 110    | 1990                   | 9        | 9    | 17.91              | 11.04             |
| T2 - SL: 01                |         | <div><div>A</div><div>B</div><div>C</div></div> | 10          | 230    | 1750   | 80     | 2060                   | 11       | 11   | 22.66              | 13.97             |
| T2 - SL: 01                |         | <div><div>A</div><div>B</div><div>C</div></div> | 10          | 330    | 2050   | 110    | 2490                   | 26       | 26   | 64.74              | 39.91             |
| T2 - SL: 01                |         | <div><div>A</div><div>B</div><div>C</div></div> | 10          | 110    | 2300   | 100    | 2510                   | 32       | 32   | 80.32              | 49.52             |
| T2 - SL: 01                |         | <div><div>A</div><div>B</div><div>C</div></div> | 10          | 330    | 2100   | 100    | 2530                   | 24       | 24   | 60.72              | 37.44             |
| T2 - SL: 01                |         | <div><div>A</div><div>B</div><div>C</div></div> | 10          | 230    | 2450   | 0      | 2680                   | 10       | 10   | 26.80              | 16.52             |
| T2 - SL: 01                |         | <div><div>A</div><div>B</div><div>C</div></div> | 10          | 0      | 2800   | 0      | 2800                   | 14       | 14   | 39.20              | 24.17             |
| T2 - SL: 01                |         | <div><div>A</div><div>B</div><div>C</div></div> | 10          | 330    | 2400   | 110    | 2840                   | 23       | 23   | 65.32              | 40.27             |
| T2 - SL: 01                |         | <div><div>A</div><div>B</div><div>C</div></div> | 10          | 110    | 3000   | 100    | 3210                   | 10       | 10   | 32.10              | 19.79             |
| T2 - SL: 01                |         | <div><div>A</div><div>B</div><div>C</div></div> | 10          | 0      | 3500   | 0      | 3500                   | 13       | 13   | 45.50              | 28.05             |
| T2 - SL: 01                |         | <div><div>A</div><div>B</div><div>C</div></div> | 10          | 230    | 3250   | 110    | 3590                   | 14       | 14   | 50.26              | 30.99             |
| T2 - SL: 01                |         | <div><div>A</div><div>B</div><div>C</div></div> | 10          | 100    | 3400   | 110    | 3610                   | 7        | 7    | 25.27              | 15.58             |
| T2 - SL: 01                |         | <div><div>A</div><div>B</div><div>C</div></div> | 10          | 230    | 3650   | 110    | 3990                   | 26       | 26   | 103.74             | 63.96             |
| T2 - SL: 01                |         | <div><div>A</div><div>B</div><div>C</div></div> | 10          | 230    | 4150   | 80     | 4460                   | 13       | 13   | 57.98              | 35.75             |
| T2 - SL: 01                |         | <div><div>A</div><div>B</div><div>C</div></div> | 10          | 130    | 5100   | 130    | 5360                   | 11       | 11   | 58.96              | 36.35             |
| T2 - SL: 01                |         | <div><div>A</div><div>B</div><div>C</div></div> | 10          | 130    | 5700   | 130    | 5960                   | 18       | 18   | 107.28             | 66.14             |
| T2 - SL: 01                |         | <div><div>A</div><div>B</div><div>C</div></div> | 10          | 230    | 5887   | 80     | 6197                   | 20       | 20   | 123.95             | 76.42             |
| T2 - SL: 01                |         | <div><div>A</div><div>B</div><div>C</div></div> | 10          | 130    | 6200   | 130    | 6460                   | 18       | 18   | 116.28             | 71.69             |
| T2 - SL: 01                |         | <div><div>A</div><div>B</div><div>C</div></div> | 10          | 130    | 6835   | 130    | 7095                   | 19       | 19   | 134.81             | 83.12             |
| T2 - SL: 01                |         | <div><div>A</div><div>B</div><div>C</div></div> | 10          | 130    | 7900   | 130    | 8160                   | 37       | 37   | 301.92             | 186.15            |
| T2 - SL: 01                |         | <div><div>A</div><div>B</div><div>C</div></div> | 10          | 130    | 8800   | 130    | 9060                   | 7        | 7    | 63.42              | 39.10             |
| T2 - SL: 01                |         | <div><div>A</div><div>B</div><div>C</div></div> | 10          | 130    | 14270  | 130    | 14530                  | 21       | 21   | 305.13             | 188.12            |
| T3                         |         |                                                 |             |        |        |        |                        |          |      |                    |                   |
| T3 - SL: 01                |         | <div><div>A</div></div>                         | 6           | 1000   | 0      | 0      | 1000                   | 9        | 9    | 9.00               | 2.00              |
| T3 - SL: 01                |         | <div><div>A</div></div>                         | 6           | 1500   | 0      | 0      | 1500                   | 15       | 15   | 22.50              | 4.99              |
| T3 - SL: 01                |         | <div><div>A</div></div>                         | 6           | 1600   | 0      | 0      | 1600                   | 13       | 13   | 20.80              | 4.62              |
| T3 - SL: 01                |         | <div><div>A</div></div>                         | 6           | 1850   | 0      | 0      | 1850                   | 5        | 5    | 9.25               | 2.05              |
| T3 - SL: 01                |         | <div><div>A</div></div>                         | 6           | 1897   | 0      | 0      | 1897                   | 17       | 17   | 32.25              | 7.16              |
| T3 - SL: 01                |         | <div><div>A</div></div>                         | 6           | 1900   | 0      | 0      | 1900                   | 2        | 2    | 3.80               | 0.84              |
| T3 - SL: 01                |         | <div><div>A</div></div>                         | 6           | 2000   | 0      | 0      | 2000                   | 9        | 9    | 18.00              | 4.00              |
| T3 - SL: 01                |         | <div><div>A</div></div>                         | 6           | 2100   | 0      | 0      | 2100                   | 10       | 10   | 21.00              | 4.66              |
| T3 - SL: 01                |         | <div><div>A</div></div>                         | 6           | 2900   | 0      | 0      | 2900                   | 9        | 9    | 26.10              | 5.79              |
| T3 - SL: 01                |         | <div><div>A</div></div>                         | 6           | 2950   | 0      | 0      | 2950                   | 9        | 9    | 26.55              | 5.89              |
| T3 - SL: 01                |         | <div><div>A</div></div>                         | 6           | 3300   | 0      | 0      | 3300                   | 17       | 17   | 56.10              | 12.45             |
| T3 - SL: 01                |         | <div><div>A</div></div>                         | 6           | 3500   | 0      | 0      | 3500                   | 12       | 12   | 42.00              | 9.32              |
| T3 - SL: 01                |         | <div><div>A</div></div>                         | 6           | 3600   | 0      | 0      | 3600                   | 4        | 4    | 14.40              | 3.20              |
| T3 - SL: 01                |         | <div><div>A</div></div>                         | 6           | 3800   | 0      | 0      | 3800                   | 16       | 16   | 60.80              | 13.49             |
| T3 - SL: 01                |         | <div><div>A</div></div>                         | 6           | 4800   | 0      | 0      | 4800                   | 5        | 5    | 24.00              | 5.33              |
| T3 - SL: 01                |         | <div><div>A</div></div>                         | 6           | 5900   | 0      | 0      | 5900                   | 4        | 4    | 23.60              | 5.24              |

| BẢNG THỐNG KÊ CỐT THÉP SÀN |         |                                                 |             |        |        |        |                        |          |      |                    |                   |
|----------------------------|---------|-------------------------------------------------|-------------|--------|--------|--------|------------------------|----------|------|--------------------|-------------------|
| TÊN C.KIỆN                 | SỐ HIỆU | HÌNH DẠNG                                       | Đ.KINH (mm) | A (mm) | B (mm) | C (mm) | CHIỀU DÀI 1 THANH (mm) | SỐ LƯỢNG |      | TỔNG CHIỀU DÀI (m) | TỔNG T.LƯỢNG (kg) |
|                            |         |                                                 |             |        |        |        |                        | C.KIỆN   | T.BỘ |                    |                   |
| T3 - SL: 01                |         | <div><div>A</div><div>B</div><div>C</div></div> | 8           | 170    | 1150   | 70     | 1390                   | 24       | 24   | 33.36              | 13.16             |
| T3 - SL: 01                |         | <div><div>A</div><div>B</div><div>C</div></div> | 8           | 70     | 2794   | 70     | 2934                   | 10       | 10   | 29.34              | 11.58             |
| T3 - SL: 01                |         | <div><div>A</div><div>B</div><div>C</div></div> | 10          | 230    | 650    | 80     | 960                    | 21       | 21   | 20.16              | 12.43             |
| T3 - SL: 01                |         | <div><div>A</div><div>B</div><div>C</div></div> | 10          | 230    | 1000   | 110    | 1340                   | 67       | 67   | 89.78              | 55.35             |
| T3 - SL: 01                |         | <div><div>A</div><div>B</div><div>C</div></div> | 10          | 230    | 1050   | 100    | 1380                   | 21       | 21   | 28.98              | 17.87             |
| T3 - SL: 01                |         | <div><div>A</div><div>B</div><div>C</div></div> | 10          | 230    | 1350   | 110    | 1690                   | 37       | 37   | 62.53              | 38.55             |
| T3 - SL: 01                |         | <div><div>A</div><div>B</div><div>C</div></div> | 10          | 230    | 2050   | 80     | 2360                   | 11       | 11   | 25.96              | 16.01             |
| T3 - SL: 01                |         | <div><div>A</div><div>B</div><div>C</div></div> | 10          | 110    | 2300   | 100    | 2510                   | 22       | 22   | 55.22              | 34.05             |
| T3 - SL: 01                |         | <div><div>A</div><div>B</div><div>C</div></div> | 10          | 330    | 2100   | 100    | 2530                   | 24       | 24   | 60.72              | 37.44             |
| T3 - SL: 01                |         | <div><div>A</div><div>B</div><div>C</div></div> | 10          | 230    | 2450   | 110    | 2790                   | 10       | 10   | 27.90              | 17.20             |
| T3 - SL: 01                |         | <div><div>A</div><div>B</div><div>C</div></div> | 10          | 0      | 2800   | 0      | 2800                   | 14       | 14   | 39.20              | 24.17             |
| T3 - SL: 01                |         | <div><div>A</div><div>B</div><div>C</div></div> | 10          | 330    | 2400   | 110    | 2840                   | 20       | 20   | 56.80              | 35.02             |
| T3 - SL: 01                |         | <div><div>A</div><div>B</div><div>C</div></div> | 10          | 100    | 3150   | 80     | 3330                   | 19       | 19   | 63.27              | 39.01             |
| T3 - SL: 01                |         | <div><div>A</div><div>B</div><div>C</div></div> | 10          | 0      | 3500   | 0      | 3500                   | 13       | 13   | 45.50              | 28.05             |
| T3 - SL: 01                |         | <div><div>A</div><div>B</div><div>C</div></div> | 10          | 100    | 3400   | 110    | 3610                   | 8        | 8    | 28.88              | 17.81             |
| T3 - SL: 01                |         | <div><div>A</div><div>B</div><div>C</div></div> | 10          | 130    | 3900   | 130    | 4160                   | 22       | 22   | 91.52              | 56.43             |
| T3 - SL: 01                |         | <div><div>A</div><div>B</div><div>C</div></div> | 10          | 230    | 3850   | 110    | 4190                   | 10       | 10   | 41.90              | 25.83             |
| T3 - SL: 01                |         | <div><div>A</div><div>B</div><div>C</div></div> | 10          | 230    | 4250   | 110    | 4590                   | 17       | 17   | 78.03              | 48.11             |
| T3 - SL: 01                |         | <div><div>A</div><div>B</div><div>C</div></div> | 10          | 230    | 4450   | 80     | 4760                   | 13       | 13   | 61.88              | 38.15             |
| T3 - SL: 01                |         | <div><div>A</div><div>B</div><div>C</div></div> | 10          | 130    | 5100   | 130    | 5360                   | 10       | 10   | 53.60              | 33.05             |
| T3 - SL: 01                |         | <div><div>A</div><div>B</div><div>C</div></div> | 10          | 130    | 5700   | 130    | 5960                   | 18       | 18   | 107.28             | 66.14             |
| T3 - SL: 01                |         | <div><div>A</div><div>B</div><div>C</div></div> | 10          | 130    | 6200   | 130    | 6460                   | 18       | 18   | 116.28             | 71.69             |
| T3 - SL: 01                |         | <div><div>A</div><div>B</div><div>C</div></div> | 10          | 130    | 7900   | 130    | 8160                   | 37       | 37   | 301.92             | 186.15            |
| T3 - SL: 01                |         | <div><div>A</div><div>B</div><div>C</div></div> | 10          | 130    | 8800   | 130    | 9060                   | 7        | 7    | 63.42              | 39.10             |
| T3 - SL: 01                |         | <div><div>A</div><div>B</div><div>C</div></div> | 10          | 130    | 10900  | 130    | 11160                  | 21       | 21   | 234.36             | 144.49            |
| DÀN DÂY BÊ TH              |         |                                                 |             |        |        |        |                        |          |      |                    |                   |
| DÀN DÂY BÊ TH - SL: 01     |         | <div><div>A</div></div>                         | 8           | 0      | 1450   | 0      | 1450                   | 48       | 48   | 69.60              | 27.46             |
| TỔNG                       |         |                                                 |             |        |        |        |                        | 1933     | 1933 | 5669.94            | 2933.00           |

| BẢNG THỐNG KÊ CỐT THÉP CẦU THANG |                   |                                                                                     |                                                                                     |                      |             |          |       |                    |                      |
|----------------------------------|-------------------|-------------------------------------------------------------------------------------|-------------------------------------------------------------------------------------|----------------------|-------------|----------|-------|--------------------|----------------------|
| TÊN CẦU KIỆN                     | SỐ HIỆU           | HÌNH DẠNG, KÍCH THƯỚC                                                               | ĐƯỜNG KÍNH (mm)                                                                     | CHIỀU DÀI THANH (mm) | SỐ CẦU KIỆN | SỐ LƯỢNG |       | TỔNG CHIỀU DÀI (m) | TỔNG KHỐI LƯỢNG (kg) |
|                                  |                   |                                                                                     |                                                                                     |                      |             | 1 CK     | T. BỘ |                    |                      |
| DT-1a<br>SL: 1                   | 1a                |    | 16                                                                                  | 2090                 | 1           | 3        | 3     | 6.27               | 9.90                 |
|                                  | 1b                |    | 16                                                                                  | 1940                 | 1           | 3        | 3     | 5.82               | 9.19                 |
|                                  | 2a                |    | 16                                                                                  | 2090                 | 1           | 3        | 3     | 6.27               | 9.90                 |
|                                  | 2b                |    | 16                                                                                  | 1940                 | 1           | 3        | 3     | 5.82               | 9.19                 |
| MC A1-A1<br>SL: 1                | 1                 |    | 10                                                                                  | 2555                 | 1           | 8        | 8     | 20.44              | 12.60                |
|                                  | 2                 |    | 10                                                                                  | 825                  | 1           | 8        | 8     | 6.60               | 4.07                 |
|                                  | 3                 |    | 10                                                                                  | 1250                 | 1           | 8        | 8     | 10.00              | 6.17                 |
|                                  | 4                 |    | 10                                                                                  | 1920                 | 1           | 8        | 8     | 15.36              | 9.47                 |
|                                  | 5                 |    | 10                                                                                  | 1670                 | 1           | 8        | 8     | 13.36              | 8.24                 |
|                                  | 6                 |    | 6                                                                                   | 960                  | 1           | 22       | 22    | 21.12              | 4.69                 |
| MC A2-A2<br>SL: 1                | 1                 |    | 10                                                                                  | 2425                 | 1           | 8        | 8     | 19.40              | 11.96                |
|                                  | 2                 |    | 10                                                                                  | 2255                 | 1           | 8        | 8     | 18.04              | 11.12                |
|                                  | 3                 |   | 10                                                                                  | 1940                 | 1           | 8        | 8     | 15.52              | 9.57                 |
|                                  | 4                 |  | 10                                                                                  | 1635                 | 1           | 8        | 8     | 13.08              | 8.06                 |
|                                  | 4                 |  | 6                                                                                   | 960                  | 1           | 16       | 16    | 15.36              | 3.41                 |
| MC B1-B1<br>SL: 1                | 12                |  | 10                                                                                  | 1335                 | 1           | 6        | 6     | 8.01               | 4.94                 |
|                                  | 13                |  | 10                                                                                  | 1735                 | 1           | 6        | 6     | 10.41              | 6.42                 |
|                                  | 14                |  | 10                                                                                  | 1185                 | 1           | 6        | 6     | 7.11               | 4.38                 |
|                                  | 15                |  | 10                                                                                  | 1240                 | 1           | 6        | 6     | 7.44               | 4.59                 |
|                                  | 16                |  | 10                                                                                  | 2785                 | 1           | 6        | 6     | 16.71              | 10.30                |
|                                  | 17                |  | 10                                                                                  | 1380                 | 1           | 6        | 6     | 8.28               | 5.10                 |
|                                  | 18                |  | 10                                                                                  | 1260                 | 1           | 6        | 6     | 7.56               | 4.66                 |
|                                  | 19                |  | 6                                                                                   | 960                  | 1           | 19       | 19    | 18.24              | 4.05                 |
|                                  | MC B2-B2<br>SL: 1 | 6                                                                                   |  | 10                   | 1560        | 1        | 6     | 6                  | 9.36                 |
| 7                                |                   |  | 10                                                                                  | 3695                 | 1           | 6        | 6     | 22.17              | 13.67                |

| BẢNG THỐNG KÊ CỘT THÉP CẦU THANG |         |                                                                                     |                 |                      |             |          |       |                    |                      |
|----------------------------------|---------|-------------------------------------------------------------------------------------|-----------------|----------------------|-------------|----------|-------|--------------------|----------------------|
| TÊN CẦU KIỆN                     | SỐ HIỆU | HÌNH DẠNG, KÍCH THƯỚC                                                               | ĐƯỜNG KÍNH (mm) | CHIỀU DÀI THANH (mm) | SỐ CẦU KIỆN | SỐ LƯỢNG |       | TỔNG CHIỀU DÀI (m) | TỔNG KHỐI LƯỢNG (kg) |
|                                  |         |                                                                                     |                 |                      |             | 1 CK     | T. BỘ |                    |                      |
| MC B2-B2<br>SL: 1                | 8       |  | 10              | 1075                 | 1           | 6        | 6     | 6.45               | 3.98                 |
|                                  | 9       |  | 10              | 1270                 | 1           | 6        | 6     | 7.62               | 4.70                 |
|                                  | 10      |  | 10              | 1390                 | 1           | 6        | 6     | 8.34               | 5.14                 |
|                                  | 11      |  | 10              | 1220                 | 1           | 6        | 6     | 7.32               | 4.51                 |
|                                  | 12      |  | 6               | 960                  | 1           | 19       | 19    | 18.24              | 4.05                 |
| MC C1-C1<br>SL: 1                | 7       |  | 10              | 1965                 | 1           | 8        | 8     | 15.72              | 9.69                 |
|                                  | 8       |  | 10              | 2210                 | 1           | 8        | 8     | 17.68              | 10.90                |
|                                  | 9       |  | 10              | 2110                 | 1           | 8        | 8     | 16.88              | 10.41                |
|                                  | 10      |  | 10              | 1660                 | 1           | 8        | 8     | 13.28              | 8.19                 |
|                                  | 11      |  | 6               | 960                  | 1           | 14       | 14    | 13.44              | 2.98                 |
| MC C2-C2<br>SL: 1                | 12      |  | 10              | 2245                 | 1           | 8        | 8     | 17.96              | 11.07                |
|                                  | 13      |  | 10              | 2970                 | 1           | 8        | 8     | 23.76              | 14.65                |
|                                  | 14      |  | 10              | 1985                 | 1           | 8        | 8     | 15.88              | 9.79                 |
|                                  | 15      |  | 6               | 960                  | 1           | 14       | 14    | 13.44              | 2.98                 |

| TỔNG HỢP CỐT THÉP  |       |        |       |
|--------------------|-------|--------|-------|
| - Đường kính (mm): | Ø6    | Ø10    | Ø16   |
| - Chiều dài (m):   | 99.84 | 379.74 | 24.18 |
| - Khối lượng (kg): | 22.16 | 234.12 | 38.18 |
| - Chiều dài / 11.7 | -     | 33     | 3     |

|              |        |    |
|--------------|--------|----|
| - Tổng cộng: | 294.46 | kg |
|--------------|--------|----|

CHỦ ĐẦU TƯ: CÔNG TY TNHH ĐẦU TƯ  
**PHÚ VIỆT TÍN**  
ĐỊA CHỈ: LÔ 18-19 QUỐC LỘ 1A, XÃ DẦU GIẤY,  
TỈNH ĐỒNG NAI, VIỆT NAM

ĐƠN VỊ THIẾT KẾ:

CÔNG TY CỔ PHẦN TƯ VẤN THIẾT KẾ

**BASE ARC**

ĐỊA CHỈ: 138 ĐIỆN BIÊN PHỦ, PHƯỜNG TÂN ĐỊNH,  
TP. HỒ CHÍ MINH, VIỆT NAM

|                          |  |
|--------------------------|--|
| CHỦ NHIỆM DỰ ÁN:         |  |
| KTS. NGUYỄN THÀNH THÁI   |  |
| CHỦ TRÌ THIẾT KẾ:        |  |
| KS. NGÔ TÙNG THÀNH       |  |
| THIẾT KẾ:                |  |
| KS. NGUYỄN MINH DUY BẰNG |  |
| KIỂM TRA:                |  |
| KS. NGÔ TÙNG THÀNH       |  |

CÔNG TRÌNH:

NHÀ Ở THƯƠNG MẠI LIÊN KÈ


TÊN BẢN VẼ:

THỐNG KÊ THÉP CẦU THANG


|                |         |
|----------------|---------|
| HOÀN THÀNH     | 07/2025 |
| TỶ LỆ          | NTS     |
| SỐ HIỆU BẢN VẼ | KC-62   |

# PHẦN ĐIỆN NƯỚC



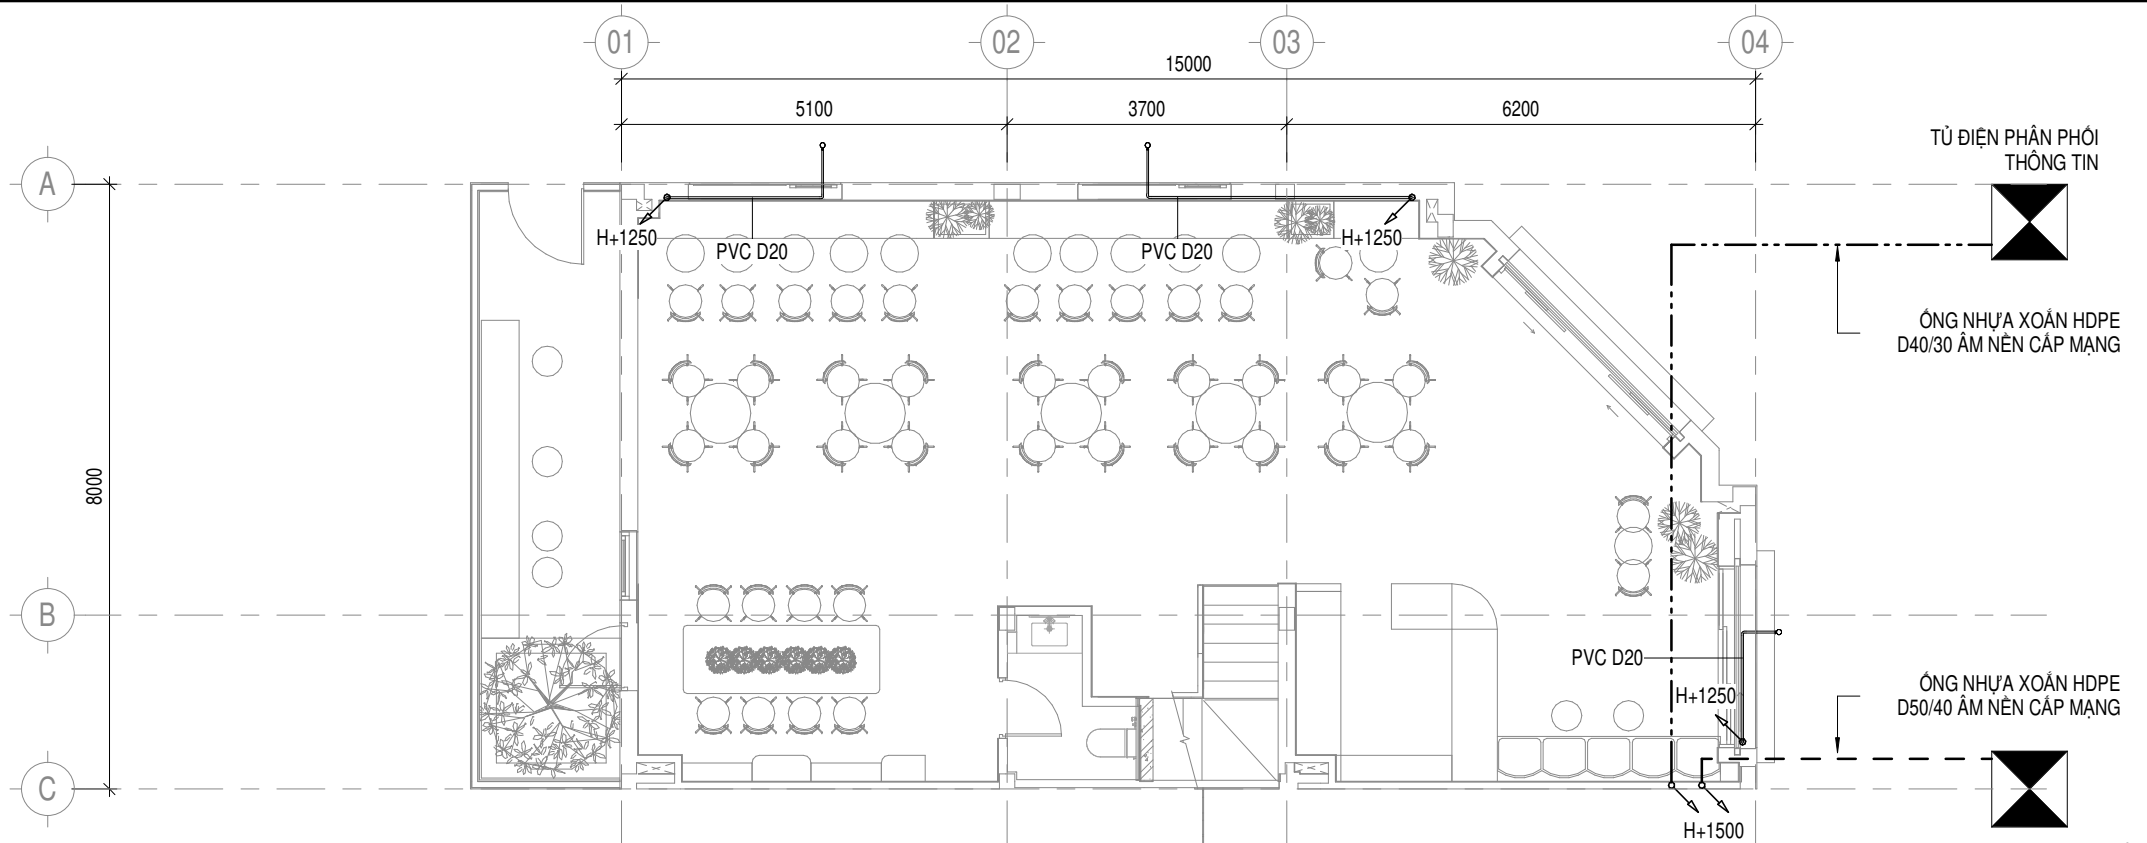


**MẶT BẰNG CẤP NGUỒN, THÔNG TIN LIÊN LẠC TẦNG 1**  
TỶ LỆ 1 : 100

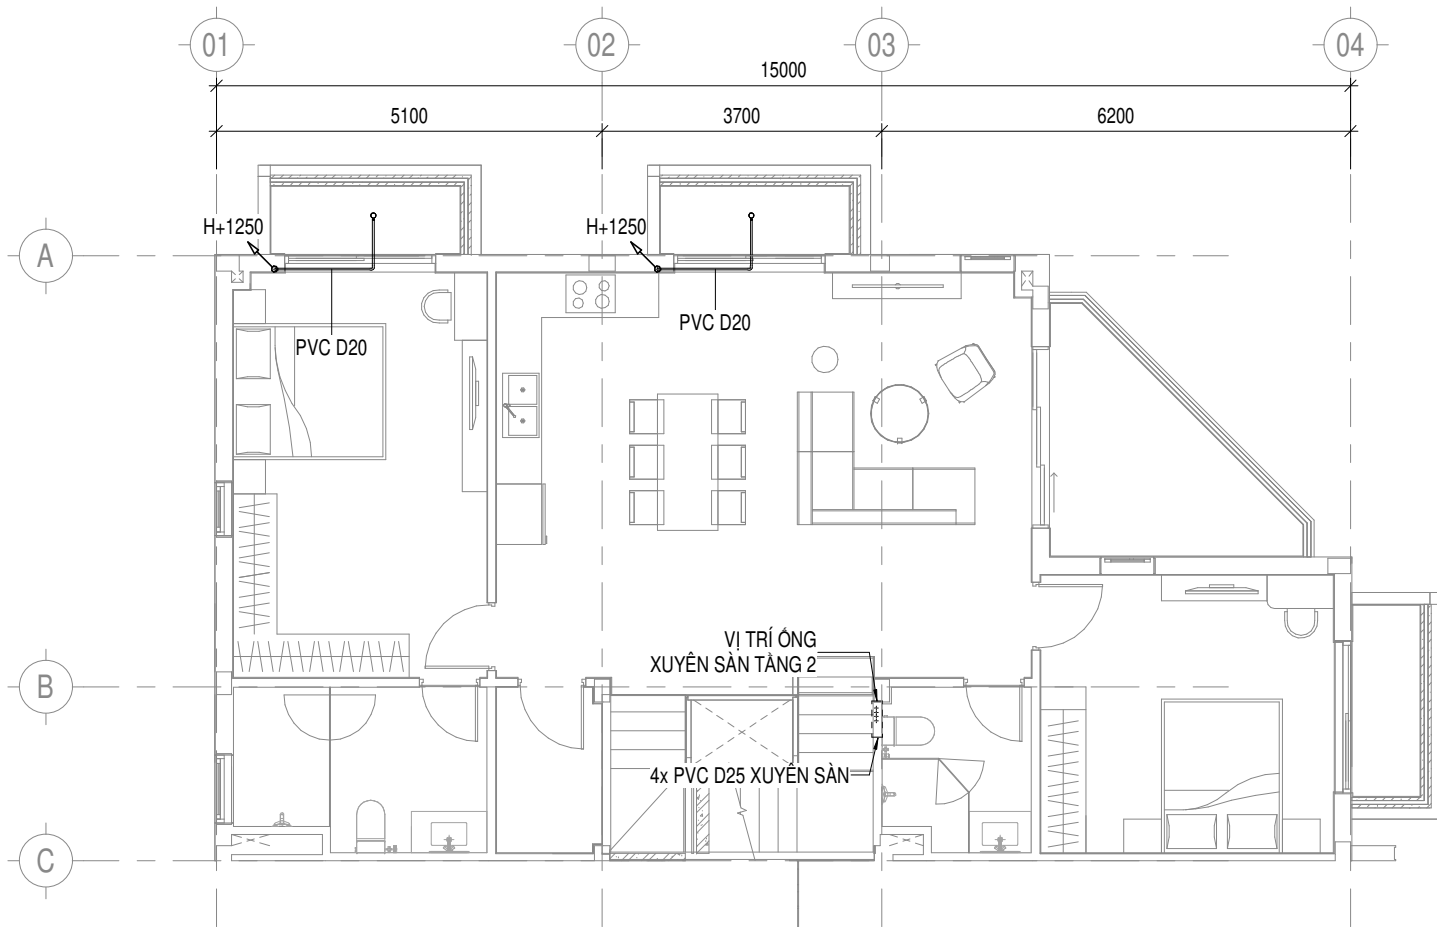

**MẶT BẰNG CẤP NGUỒN, THÔNG TIN LIÊN LẠC TẦNG 2**  
TỶ LỆ 1 : 100

|   |         |                 |
|---|---------|-----------------|
| GHI CHÚ:<br>- CÁC ĐƠN VỊ THI CÔNG PHẢI PHỐI HỢP BẢN VẼ CỦA TẤT CẢ CÁC BỘ MÔN KHÁC NẾU THẤY SỰ KHÁC BIỆT PHẢI BÁO CHO ĐƠN VỊ THIẾT KẾ XỬ LÝ.<br>- KHI XỬ LÝ SỰ KHÁC BIỆT, PHẢI THỰC HIỆN ƯU TIÊN THEO THỨ TỰ GIỮA CÁC BỘ MÔN: KIẾN TRÚC → KẾT CẤU / BỐ MÔN KHÁC; HOẶC ƯU TIÊN TRONG CÙNG BỘ MÔN: CHI TIẾT → TỔNG THỂ<br>- CÁC SỐ LIỆU KỊCH THUỘC PHẢI ĐƯỢC KIỂM TRA THỰC TẾ TẠI CÔNG TRÌNH, NẾU THẤY SỰ KHÁC BIỆT SƠ VỚI BẢN VẼ THI PHẢI BÁO CHO ĐƠN VỊ THIẾT KẾ. |         |                 |
| HIỆU CHỈNH:   |         |                 |
| REV   | NGÀY    | NỘI DUNG        |
|   |         |                 |
| CHỦ ĐẦU TƯ:<br>CÔNG TY TNHH ĐẦU TƯ<br><b>PHÚ VIỆT TÍN</b><br>ĐỊA CHỈ: LÔ 18-19 QUỐC LỘ 1A, XÃ DẦU GIẤY,<br>TỈNH ĐỒNG NAI, VIỆT NAM   |         |                 |
|   |         |                 |
| CHỦ ĐẦU TƯ:   |         | ĐẶNG PHƯỚC BÌNH |
| ĐƠN VỊ THIẾT KẾ:<br>CÔNG TY CỔ PHẦN TƯ VẤN THIẾT KẾ<br><b>BASE ARC</b><br>ĐỊA CHỈ: 138 ĐIỆN BIÊN PHỦ, PHƯỜNG TÂN ĐỊNH,<br>TP. HỒ CHÍ MINH, VIỆT NAM   |         |                 |
|   |         |                 |
| TỔNG GIÁM ĐỐC   |         | TRẦN ĐỨC AN     |
| CHỦ NHIỆM DỰ ÁN:   |         |                 |
| KTS. NGUYỄN THÀNH THÁI   |         |                 |
| CHỦ TRÌ THIẾT KẾ:   |         |                 |
| KS. TRƯƠNG NGỌC TRỌNG   |         |                 |
| THIẾT KẾ:   |         |                 |
| KS. TRẦN HỒNG ÂN   |         |                 |
| KIỂM TRA:   |         |                 |
| KS. TRƯƠNG NGỌC TRỌNG   |         |                 |
| DỰ ÁN:<br>KHU DÂN CƯ A1-C1 (ĐÔ THỊ DẦU GIẤY)<br>ĐỊA ĐIỂM: XÃ DẦU GIẤY, TỈNH ĐỒNG NAI   |         |                 |
| CÔNG TRÌNH:<br><br>NHÀ Ở THƯƠNG MẠI LIÊN KẾ   |         |                 |
| HẠNG MỤC:<br><br>MẪU NHÀ T3-2b   |         |                 |
| TÊN BẢN VẼ:<br>MẶT BẰNG CẤP NGUỒN, THÔNG TIN LIÊN LẠC<br>TẦNG 1, TẦNG 2   |         |                 |
| MỤC ĐÍCH PHÁT HÀNH:   |         |                 |
| BẢN VẼ MỜI THẦU   |         |                 |
| THIẾT KẾ CƠ SỞ   |         |                 |
| ✓ THIẾT KẾ BẢN VẼ THI CÔNG   |         |                 |
| BẢN VẼ HOÀN CÔNG   |         |                 |
| HOÀN THÀNH   | 07/2025 |                 |
| TỶ LỆ   | NTS     |                 |
| SỐ HIỆU BẢN VẼ   | E2-02   |                 |

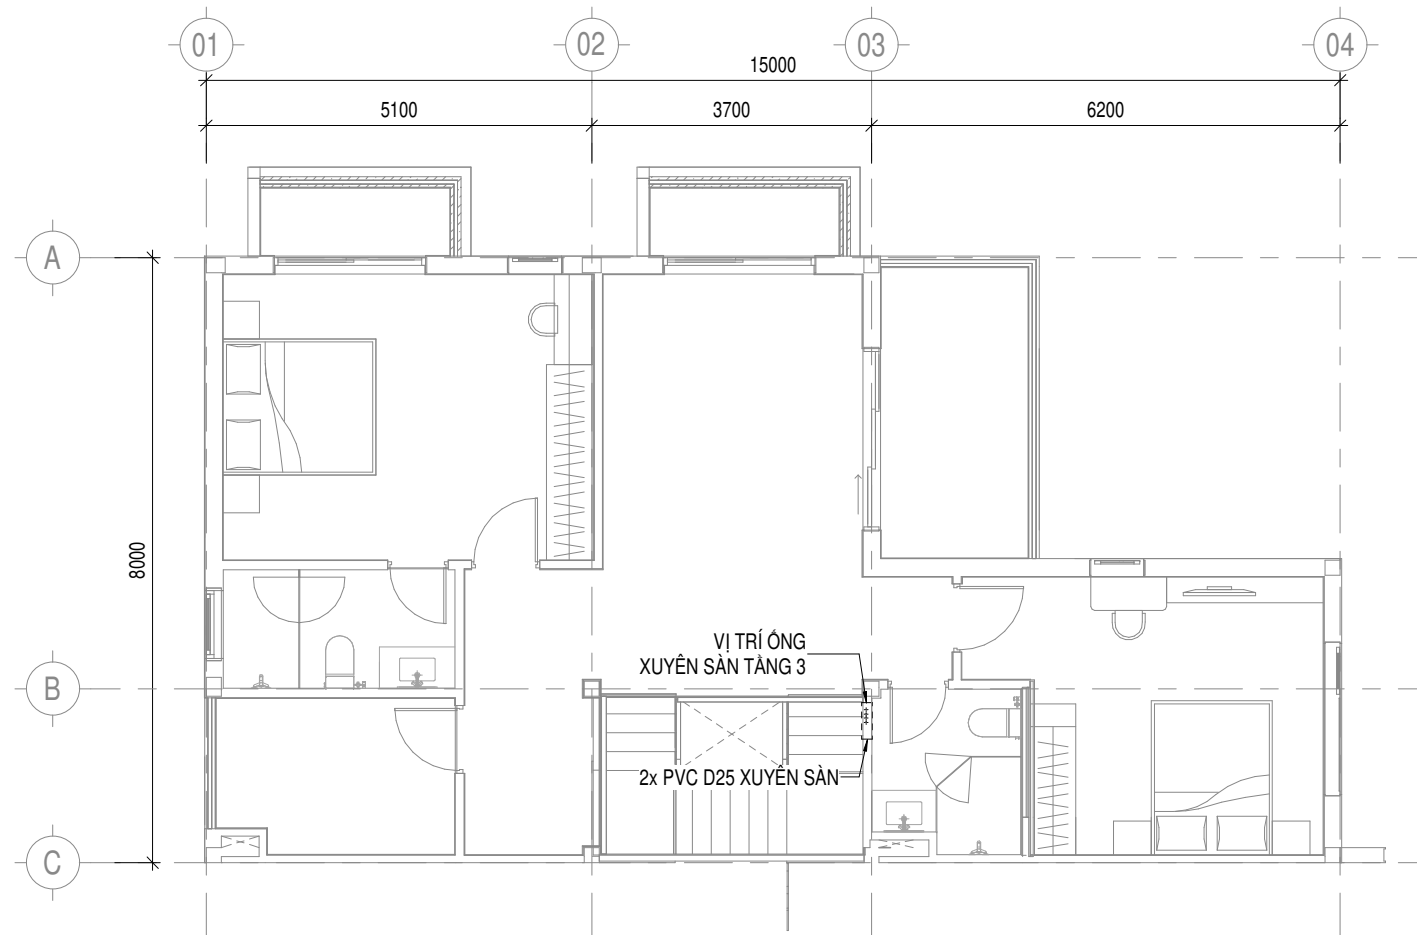

**MẶT BẰNG CẤP NGUỒN, THÔNG TIN LIÊN LẠC TẦNG 3**  
TỶ LỆ 1 : 100

**GHI CHÚ:**  
- CÁC ĐƠN VỊ THI CÔNG PHẢI PHỐI HỢP BẢN VẼ CỦA TẤT CẢ CÁC BỘ MÔN KHÁC NẾU THẤY SỰ KHÁC BIỆT PHẢI BẢO CHO ĐƠN VỊ THIẾT KẾ XỬ LÝ.  
- KHI XỬ LÝ SỰ KHÁC BIỆT, PHẢI THỰC HIỆN ƯU TIÊN THEO THỨ TỰ GIỮA CÁC BỘ MÔN: KIẾN TRÚC → KẾT CẤU / BỘ MÔN KHÁC; HOẶC ƯU TIÊN TRONG CÙNG BỘ MÔN: CHI TIẾT → TỔNG THỂ  
- CÁC SỐ LƯỢNG KỊCH THUỘC PHẢI ĐƯỢC KIỂM TRA THỰC TẾ TẠI CÔNG TRÌNH, NẾU THẤY SỰ KHÁC BIỆT SO VỚI BẢN VẼ THI PHẢI BẢO CHO ĐƠN VỊ THIẾT KẾ.

**HIỆU CHỈNH:**

| REV | NGÀY | NỘI DUNG |
|-----|------|----------|
|-----|------|----------|

**CHỦ ĐẦU TƯ:**  
CÔNG TY TNHH ĐẦU TƯ  
**PHÚ VIỆT TÍN**  
ĐỊA CHỈ: LÔ 18-19 QUỐC LỘ 1A, XÃ DẦU GIẤY,  
TỈNH ĐỒNG NAI, VIỆT NAM

**CTHĐT:** ĐẶNG PHƯỚC BÌNH

**ĐƠN VỊ THIẾT KẾ:**  
CÔNG TY CỔ PHẦN TƯ VẤN THIẾT KẾ  
**BASE ARC**  
ĐỊA CHỈ: 138 ĐIỆN BIÊN PHỦ, PHƯỜNG TÂN ĐỊNH,  
TP. HỒ CHÍ MINH, VIỆT NAM

**TỔNG GIÁM ĐỐC** TRẦN ĐỨC AN

**CHỦ NHIỆM DỰ ÁN:**

KTS. NGUYỄN THÀNH THÁI

**CHỦ TRÌ THIẾT KẾ:**

KS. TRƯƠNG NGỌC TRỌNG

**THIẾT KẾ:**

KS. TRẦN HỒNG AN

**KIỂM TRA:**

KS. TRƯƠNG NGỌC TRỌNG

**DỰ ÁN:**  
KHU DÂN CƯ A1-C1 (ĐÔ THỊ DẦU GIẤY)  
ĐỊA ĐIỂM: XÃ DẦU GIẤY, TỈNH ĐỒNG NAI

**CÔNG TRÌNH:**  
NHÀ Ở THƯƠNG MẠI LIÊN KẾ

**HẠNG MỤC:**  
MẪU NHÀ T3-2b

**TÊN BẢN VẼ:**  
MẶT BẰNG CẤP NGUỒN, THÔNG TIN LIÊN LẠC  
TẦNG 3

**MỤC ĐÍCH PHÁT HÀNH:**

|                                     |                          |
|-------------------------------------|--------------------------|
| <input type="checkbox"/>            | BẢN VẼ MỜI THẦU          |
| <input type="checkbox"/>            | THIẾT KẾ CƠ SỞ           |
| <input checked="" type="checkbox"/> | THIẾT KẾ BẢN VẼ THI CÔNG |
| <input type="checkbox"/>            | BẢN VẼ HOÀN CÔNG         |

|            |         |
|------------|---------|
| HOÀN THÀNH | 07/2025 |
|------------|---------|

|       |     |
|-------|-----|
| TỶ LỆ | NTS |
|-------|-----|

|                |       |
|----------------|-------|
| SỐ HIỆU BẢN VẼ | E2-03 |
|----------------|-------|

## THUYẾT MINH HỆ THỐNG CẤP THOÁT NƯỚC:

- QUY CHUẨN XÂY DỰNG VIỆT NAM.
- QUY CHUẨN HỆ THỐNG CẤP THOÁT NƯỚC TRONG NHÀ VÀ CÔNG TRÌNH.
- TCVN 4513-1988: CẤP NƯỚC BÊN TRONG - TIÊU CHUẨN THIẾT KẾ.
- TCVN 4474-1987: THOÁT NƯỚC BÊN TRONG - TIÊU CHUẨN THIẾT KẾ.
- TCVN 13606-2023: CẤP NƯỚC. MANG LƯỚI ĐƯỜNG ống VÀ CÔNG TRÌNH - YÊU CẦU THIẾT KẾ.
- TCVN 7957-2023: THOÁT NƯỚC. MANG LƯỚI VÀ CÔNG TRÌNH BÊN NGOÀI - YÊU CẦU THIẾT KẾ.
- TCVN 5673-1992: HỆ THỐNG TẢI LIU THIẾT KẾ XÂY DỰNG CẤP THOÁT NƯỚC BÊN TRONG NHÀ.

## 2. HỆ THỐNG CẤP NƯỚC SINH HOẠT:

NGUỒN NƯỚC CẤP ĐƯỢC LẤY TỪ HỆ THỐNG CẤP NƯỚC THÀNH PHỐ. SAU KHI QUA ĐỒNG HỒ NƯỚC TỔNG, NƯỚC ĐƯỢC DẪN VÀO BỂ CHỨA NƯỚC SINH HOẠT MÃI. TỪ ĐÂY, NƯỚC CẤP XUỐNG CẤP TĂNG THEO NGUYÊN TẮC TRỌNG LỰC.

- TIÊU CHUẨN DÙNG NƯỚC:  $q = 150 \text{ L/NGƯỜI.NGÀY}$
- ĐƯỜNG ỐNG CẤP NƯỚC LÊN BỂ NƯỚC MÃI DÙNG ỐNG uPVC, NỐI BẰNG PHƯƠNG PHÁP KEO DÁN.
- ĐƯỜNG ỐNG CẤP NƯỚC LẠNH DÙNG ỐNG uPVC, NỐI BẰNG PHƯƠNG PHÁP KEO DÁN.
- ĐƯỜNG ỐNG CẤP NƯỚC NÓNG DÙNG ỐNG PPR, NỐI BẰNG PHƯƠNG PHÁP HÀN NHIỆT.

### 3. HỆ THỐNG THOÁT NƯỚC SINH HOẠT:

- HỆ THỐNG THOÁT PHÂN (CHẬU XÍ, CHẬU TIỂU) ĐƯỢC THU GOM ĐƯA VỀ BỂ TỰ HOẠI ĐỂ XỬ LÝ SƠ BỘ. SAU ĐÓ NƯỚC THẢI ĐƯỢC THOÁT RA HỆ THỐNG THU NƯỚC THẢI CHUNG.
- HỆ THỐNG THOÁT NƯỚC SINH HOẠT (LAVABO, CHẬU RỬA, PHỄU THU...) ĐƯỢC THOÁT RA HỆ THỐNG THU NƯỚC THẢI CHUNG.
- ĐƯỜNG ỐNG THOÁT NƯỚC THẢI SINH HOẠT DÙNG ỐNG uPVC. NỐI BẰNG PHƯƠNG PHÁP KEO DÁN

#### 4. HỆ THỐNG THOÁT NƯỚC MƯA

- HỆ THỐNG THOÁT NƯỚC MƯA BAO GOM HỆ THỐNG THOÁT NƯỚC MÃI, BÀN CÔNG.
- NƯỚC MƯA ĐƯỢC THU GOM TRÊN CÁC MÃI CÔNG TRÌNH DẪN TẬP TRUNG VÀ CÁC ỒNG ĐƯỜNG, THOÁT RA CÁC HỒ GA TỌNG THÊ GẦN NHẤT.
  - NƯỚC MƯA MẶT SÀN CÔNG TRÌNH ĐƯỢC THU GOM TRỰC TIẾP VÀO CÁC HỒ GA NƯỚC MƯA VÀ THOÁT RA NGOÀI HỆ THỐNG THOÁT NƯỚC CHUNG.
  - ĐƯỜNG ỒNG THOÁT NƯỚC MƯA DÙNG ỒNG uPVC. NỘI BẢNG PHƯƠNG PHÁP KẸO DÁN.

## GHI CHÚ CHUNG HỆ THỐNG CẤP THOÁT NƯỚC

1. ĐƯỜNG KÍNH ỒNG THỂ HIỆN TRÊN BẢN VẼ LÀ ĐƯỜNG KÍNH NGOÀI VỚI ĐƠN VỊ LÀ MILIMET.  
2. NẾU KHÔNG ĐƯỢC GHI RÕ TRONG BẢN VẼ NƯỚC, CÁC ỒNG NHÁNH CÓ KÍCH THƯỚC THEO BẢNG SAU.

| THIẾT BỊ VỆ SINH | ĐƯỜNG KÍNH NHỎ NHẤT CỦA ỐNG CẤP NƯỚC(mm)<br>(ĐƯỜNG KÍNH NGOÀI) |
|------------------|----------------------------------------------------------------|
| WC               | 21                                                             |
| LAVABO           | 21                                                             |
| HƯƠNG SEN        | 21                                                             |
| CHẬU RỬA         | 21                                                             |
| VỒI NƯỚC         | 21                                                             |

3. ĐỒNG HỒ NƯỚC PHẢI ĐƯỢC CUNG CẤP BỞI NHÀ CUNG CẤP CÓ THẨM QUYỀN VÀ ĐƯỢC NIÊM PHONG.
4. TRONG QUÁ TRÌNH THI CÔNG, CÁC ĐẦU ÔNG HỒ PHẢI ĐƯỢC BÍT KÍN THÍCH HỢP ĐỂ TRÁNH SỰ THÂM NHẬP CÁC TẠP CHẤT BÊN NGOÀI.
5. ÔNG THOÁT NƯỚC ĐƯỢC TREO BẰNG TY REN THÉP GẮN VỚI SÀN BẰNG BU LÔNG NỖ.
6. TẤT CẢ CÁC ÔNG CẤP NƯỚC PPR SẼ SỬ DỤNG MÔI NỐI HÀN GIA NHIỆT
7. CAO ĐỘ SỬ DỤNG TRÊN BẢN VẼ LÀ CAO ĐỘ TƯƠNG ĐỐI, CAO ĐỘ NÀY SO VỚI CAO ĐỘ QUỐC GIA SẼ ĐƯỢC CHỈ RÕ TRÊN BẢN VẼ
8. ÔNG SỬ DỤNG CẤP NƯỚC NƯỚC NONG LÀ PPR.
9. ÔNG SỬ DỤNG CẤP NƯỚC KHU VỰC SINH LẠC uPVC.
10. ÔNG SỬ DỤNG CHO HỆ THỐNG THOÁT NƯỚC LÀ uPVC.
11. KHÔNG SỬ DỤNG CỘ 90° TRONG HỆ THỐNG THOÁT NƯỚC.
12. CHỤP ÔNG THOÁT HƠI ĐƯỢC LẮP ĐẶT CÁCH SÀN TẦNG MÃI 700mm.
13. ĐỘ DỐC CỦA ÔNG THOÁT NƯỚC THẢI SẼ ĐƯỢC LẤY THEO BẢNG SAU, TRỪ KHI CÓ GHI CHÚ CỤ THỂ KHÁC:

| KÍCH CỠ ỐNG | ĐỘ DỐC (%) |
|-------------|------------|
| D60         | 2          |
| D90         | 2          |
| D114        | 1          |

14. PHẢI XEM PHỐI HỢP BẢN VẼ KIẾN TRÚC, KẾT CẤU, CƠ ĐIỆN ĐỂ XÁC ĐỊNH RÕ CÁC TUYẾN ÔNG VỊ TRÍ ÔNG XUYỀN SÀN, TƯỜNG TRONG QUÁ TRÌNH THI CÔNG.
15. ĐƠN VỊ THI CÔNG PHẢI LÀM DẤU CÁC VỊ TRÍ CỬA THÂM THEO BẢN VẼ Ở CÁC KHU VỰC MÀ HỆ THỐNG BỊ DẤU KÍN ĐỂ THUẬN LỢI CHO VIỆC BẢO TRÌ.
16. BẢO ĐẢM TẤT CẢ CÁC LỖ XUYỀN TƯỜNG, XUYỀN MÀI, XUYỀN SÀN PHẢI ĐƯỢC CHỒNG THÂM THEO QUY TRÌNH CỦA NHÀ SẢN XUẤT.
17. LỒ HÚT PHẦN D90 DÙNG LOẠI BÍT TRƠN
18. CÁC ĐƯỜNG ÔNG THOÁT NƯỚC NHANH CỎ KÍCH THƯỚC NHƯ BẢNG SAU. TRỪ KHI CỎ GỒI CHÚ CỤ THỂ KHÁC:

| TIÊU CHUẨN KÍCH THƯỚC ỐNG NƯỚC XẢ CỦA THIẾT BỊ VỆ SINH (MM),(ĐƯỜNG KÍNH NGOÀI) |      |
|--------------------------------------------------------------------------------|------|
| LAVABO                                                                         | D42  |
| XÍ BỆT                                                                         | D114 |
| PHÉU THU SÀN                                                                   | D60  |
| CHẬU RỬA BẾP                                                                   | D60  |

|   |                          |                 |
|---|--------------------------|-----------------|
| GHI CHÚ:   |                          |                 |
| <div>- CÁC ĐƠN VỊ THI CÔNG PHẢI PHỐI HỢP BẢN VẼ CỦA TẤT CẢ CÁC BỘ MÔN KHÁC NẾU THẤY SỰ KHÁC BIỆT PHẢI BÁO CHO ĐƠN VỊ THIẾT KẾ ĐỂ XỬ LÝ.</div> <div>- KHI XỬ LÝ SỰ KHÁC BIỆT, PHẢI THỰC HIỆN ƯU TIÊN THEO THỨ TỰ GIỮA CÁC BỘ MÔN: KIẾN TRÚC → KẾT CẤU / BỘ MÔN KHÁC; HOẶC ƯU TIÊN TRONG CÙNG BỘ MÔN: CHI TIẾT → TỔNG THỂ</div> <div>- CÁC SỐ LIỆU KÍCH THƯỚC PHẢI ĐƯỢC KIỂM TRA THỰC TẾ TẠI CÔNG TRÌNH, NẾU THẤY SỰ KHÁC BIỆT SÓ VỚI BẢN VẼ THÌ PHẢI BÁO CHO ĐƠN VỊ THIẾT KẾ.</div> |                          |                 |
| HIỆU CHỈNH:   |                          |                 |
| REV   | NGÀY                     | NỘI DUNG        |
|   |                          |                 |
| CHỦ ĐẦU TƯ:   |                          |                 |
| CÔNG TY TNHH ĐẦU TƯ   |                          |                 |
| PHÚ VIỆT TÍN   |                          |                 |
| ĐỊA CHỈ: LÔ 18-19 QUỐC LỘ 1A, XÃ DẦU GIẤY, TỈNH ĐỒNG NAI, VIỆT NAM   |                          |                 |
|   |                          |                 |
| CTHĐT/V:   |                          | ĐANG PHƯỚC BÌNH |
| ĐƠN VỊ THIẾT KẾ:   |                          |                 |
| CÔNG TY CỔ PHẦN TƯ VẤN THIẾT KẾ   |                          |                 |
| BASE ARC   |                          |                 |
| ĐỊA CHỈ: 138 ĐIỆN BIÊN PHŨ, PHƯỜNG TÂN ĐỊNH, TP. HỒ CHÍ MINH, VIỆT NAM   |                          |                 |
|   |                          |                 |
| TỔNG GIÁM ĐỐC   |                          | TRẦN ĐỨC AN     |
| CHỦ NHIỆM DỰ ÁN:   |                          |                 |
| KTS. NGUYỄN THÀNH THÁI   |                          |                 |
| CHỦ TRÌ THIẾT KẾ:   |                          |                 |
| KS. TRƯƠNG NGỌC TRỌNG   |                          |                 |
| THIẾT KẾ:   |                          |                 |
| KS. PHẠM BÁ LINH   |                          |                 |
| KIỂM TRA:   |                          |                 |
| KS. TRƯƠNG NGỌC TRỌNG   |                          |                 |
| DỰ ÁN:   |                          |                 |
| KHU DÂN CƯ A1-C1 (ĐÔ THỊ DẦU GIẤY)   |                          |                 |
| ĐỊA ĐIỂM: XÃ DẦU GIẤY, TỈNH ĐỒNG NAI   |                          |                 |
| CÔNG TRÌNH:   |                          |                 |
| NHÀ Ở THƯƠNG MẠI LIỀN KỀ   |                          |                 |
| HẠNG MỤC:   |                          |                 |
| MẪU NHÀ T3-2b   |                          |                 |
| TÊN BẢN VẼ:   |                          |                 |
| GHI CHÚ CHUNG CẤP THOÁT NƯỚC   |                          |                 |
| MỤC ĐÍCH PHÁT HÀNH:   |                          |                 |
|   | BẢN VẼ MỜI THẦU          |                 |
|   | THIẾT KẾ CƠ SỞ           |                 |
| ✓   | THIẾT KẾ BẢN VẼ THI CÔNG |                 |
|   | BẢN VẼ HOÀN CÔNG         |                 |
| HOÀN THÀNH   |                          | 07/2025         |
| TỶ LỆ   |                          | NTS             |
| SỐ HIỆU BẢN VẼ   |                          | P2-01           |



GHI CHÚ:

- CÁC ĐƠN VỊ THI CÔNG PHẢI PHỐI HỢP BẢN VẼ CỦA TẤT CẢ CÁC BỘ MÔN KHÁC NẾU THẤY SỰ KHÁC BIỆT PHẢI BẢO CHO ĐƠN VỊ THIẾT KẾ ĐỂ XỬ LÝ.  
- KHI XỬ LÝ SỰ KHÁC BIỆT, PHẢI THỰC HIỆN ƯU TIÊN THEO THỨ TỰ GIỮA CÁC BỘ MÔN: KIẾN TRÚC → KẾT CẤU / BỘ MÔN KHÁC; HOẶC ƯU TIÊN TRONG CÙNG BỘ MÔN: CHI TIẾT → TỔNG THỂ  
- CÁC SỐ LIỆU KÍCH THƯỚC PHẢI ĐƯỢC KIỂM TRA THỰC TẾ TẠI CÔNG TRÌNH, NẾU THẤY SỰ KHÁC BIỆT SƠ VỚI BẢN VẼ THI PHẢI BÁO CHO ĐƠN VỊ THIẾT KẾ.

HIỆU CHÍNH:

|     |      |          |
|-----|------|----------|
| REV | NGÀY | NỘI DUNG |
|     |      |          |

CHỦ ĐẦU TƯ:

CÔNG TY TNHH ĐẦU TƯ

PHÚ VIỆT TÍN

ĐỊA CHỈ: LÔ 18-19 QUỐC LỘ 1A, XÃ DẦU GIẦY,  
TỈNH ĐỒNG NAI, VIỆT NAM

CTHĐT.V:ĐẠNG PHƯỚC BÌNH

ĐƠN VỊ THIẾT KẾ:

CÔNG TY CỔ PHẦN TƯ VẤN THIẾT KẾ

BASE ARC

ĐỊA CHỈ: 138 ĐIỆN BIÊN PHỦ, PHƯỜNG TÂN ĐỊNH,  
TP. HỒ CHÍ MINH, VIỆT NAM

TỔNG GIÁM ĐỐCTRẦN ĐỨC AN

|                        |  |
|------------------------|--|
| CHỦ NHIỆM DỰ ÁN:       |  |
| KTS. NGUYỄN THÀNH THÁI |  |
| CHỦ TRÌ THIẾT KẾ:      |  |
| KS. TRƯƠNG NGỌC TRỌNG  |  |
| THIẾT KẾ:              |  |
| KS. PHẠM BÁ LINH       |  |
| KIỂM TRA:              |  |
| KS. TRƯƠNG NGỌC TRỌNG  |  |

DỰ ÁN:

KHU DÂN CƯ A1-C1 (ĐÔ THỊ DẦU GIẦY)

ĐỊA ĐIỂM: XÃ DẦU GIẦY, TỈNH ĐỒNG NAI

CÔNG TRÌNH:

NHÀ Ở THƯƠNG MẠI LIÊN KỀ


HẠNG MỤC:MẪU NHÀ T3-2b

TÊN BẢN VẼ:SƠ ĐỒ NGUYÊN LÝ THOÁT NƯỚC MƯA

MỤC ĐÍCH PHÁT HÀNH:



|   |                          |
|---|--------------------------|
|   | BẢN VẼ MỜI THẦU          |
|   | THIẾT KẾ CƠ SỞ           |
| ✓ | THIẾT KẾ BẢN VẼ THI CÔNG |
|   | BẢN VẼ HOÀN CÔNG         |

|                |         |
|----------------|---------|
| HOÀN THÀNH     | 07/2025 |
| TÝ LỆ          | NTS     |
| SỐ HIỆU BẢN VẼ | P2-02   |

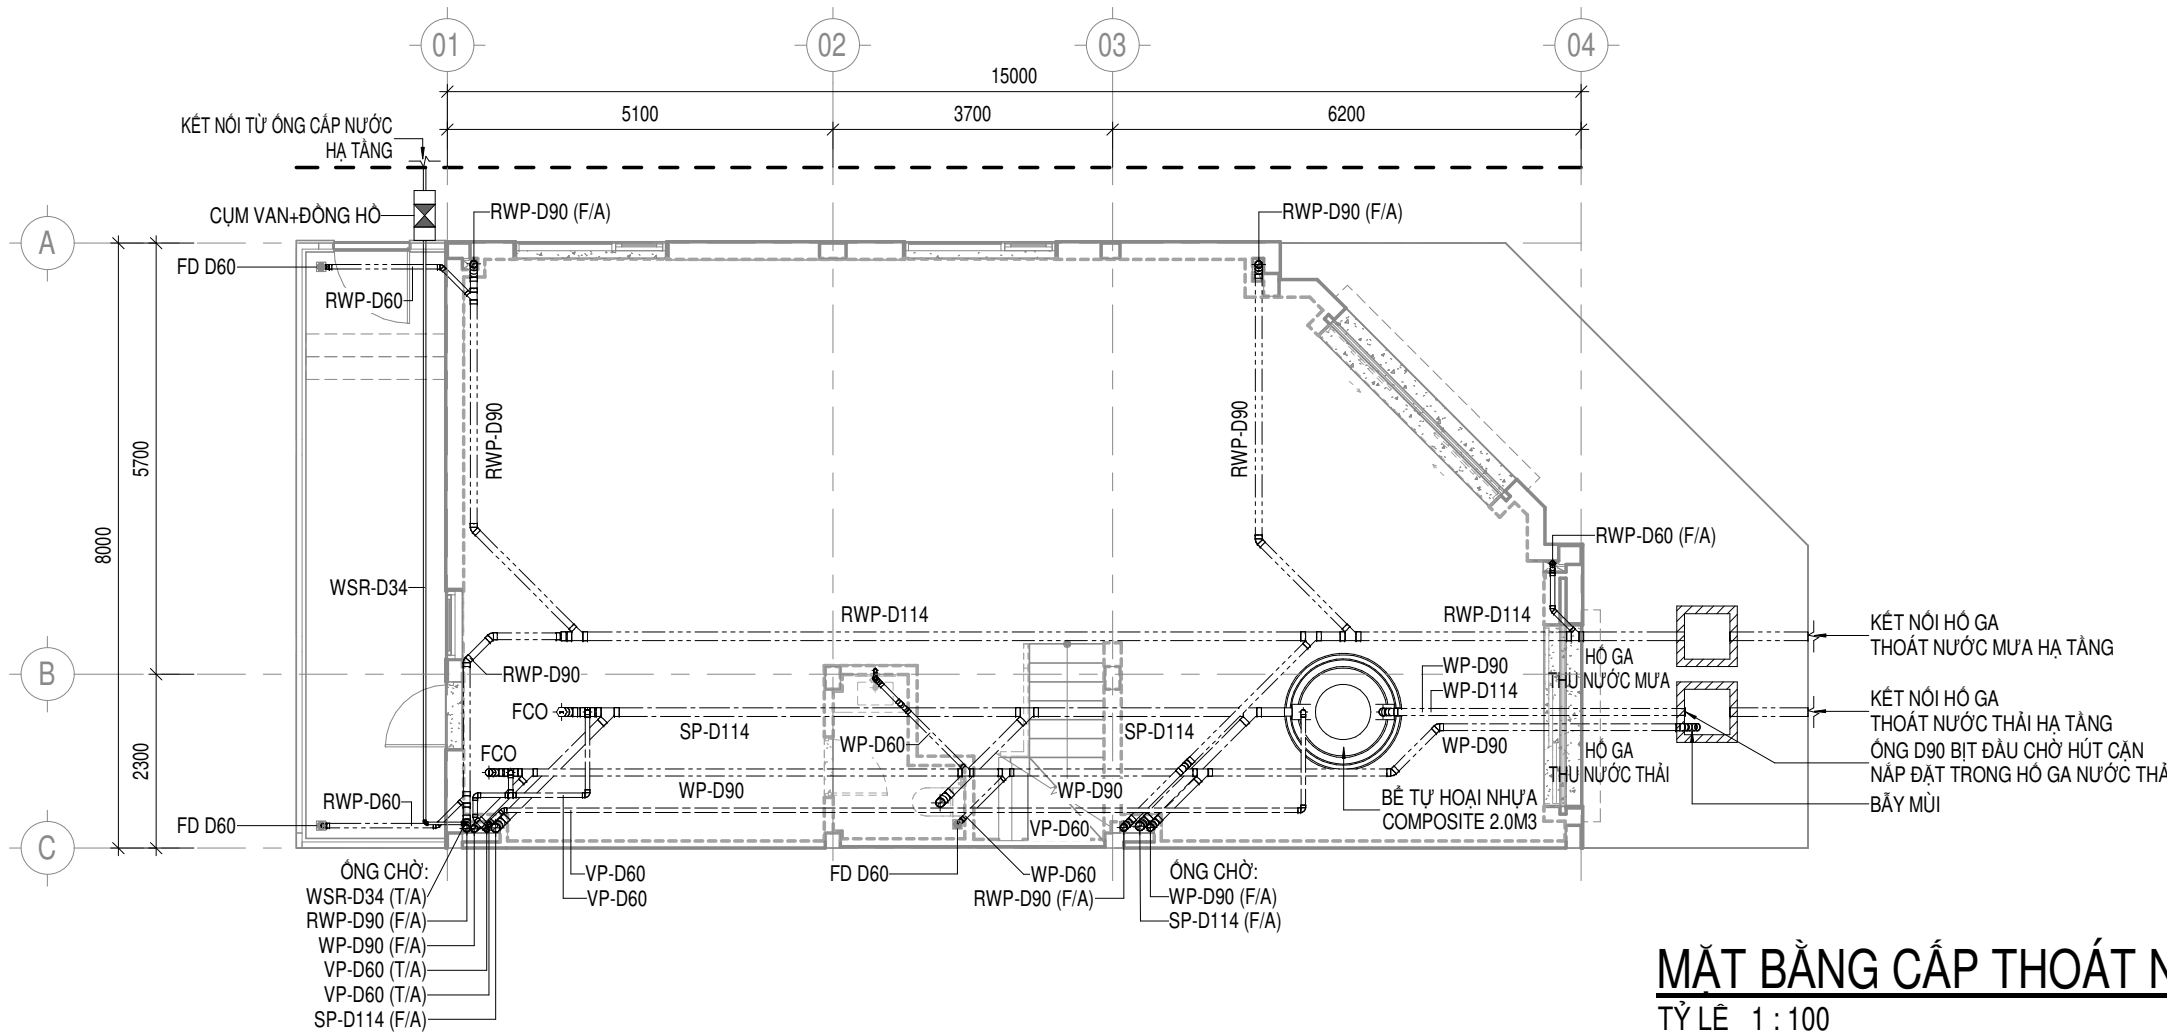

## MẶT BẰNG CẤP THOÁT NƯỚC TẦNG 1

TỶ LỆ 1 : 100

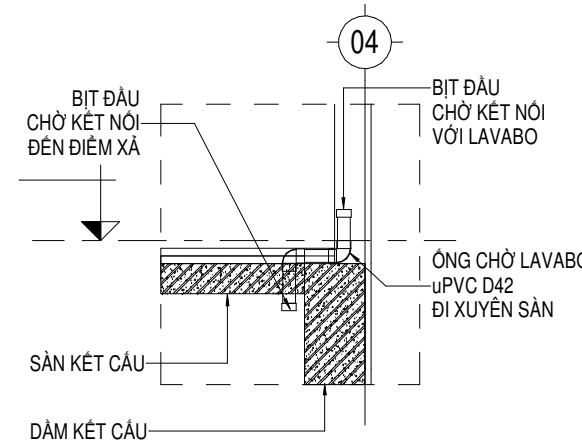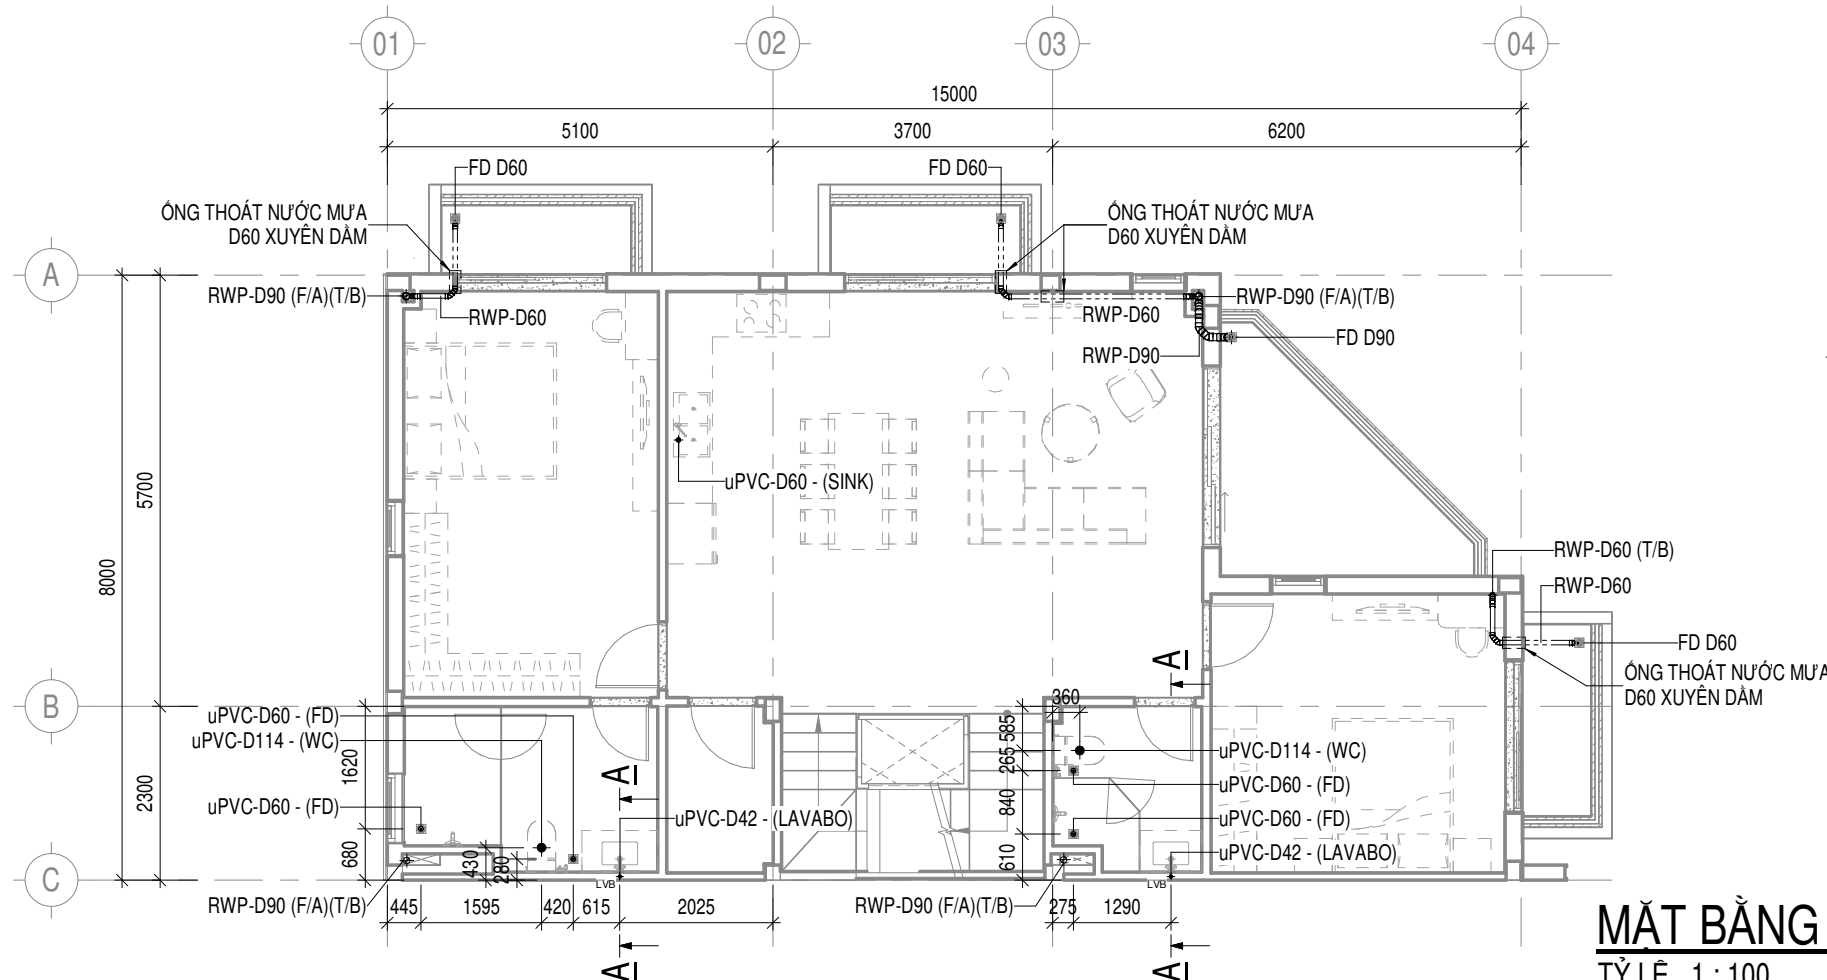

## MẶT CẮT A-A

TỶ LỆ 1 : 25

## MẶT BẰNG CẤP THOÁT NƯỚC TẦNG 2

TỶ LỆ 1 : 100

GHI CHÚ:  
- CÁC ĐƠN VỊ THI CÔNG PHẢI PHỐI HỢP BẢN VẼ CỦA TẤT CẢ CÁC BỘ MÔN KHÁC NẾU THẤY SỰ KHÁC BIỆT PHẢI BẢO CHỨNG ĐƠN VỊ THIẾT KẾ XỬ LÝ.  
- KHI XỬ LÝ SỰ KHÁC BIỆT, PHẢI THỰC HIỆN ƯU TIÊN THEO THỨ TỰ GIỮA CÁC BỘ MÔN: KIẾN TRÚC → KẾT CẤU / BỘ MÔN KHÁC; HOẶC ƯU TIÊN TRONG CÙNG BỘ MÔN: CHI TIẾT → TỔNG THỂ  
- CÁC SỐ LIỆU KÍCH THƯỚC PHẢI ĐƯỢC KIỂM TRA THỰC TẾ TẠI CÔNG TRÌNH, NẾU THẤY SỰ KHÁC BIỆT SƠ VỚI BẢN VẼ THI PHẢI BẢO CHỨNG ĐƠN VỊ THIẾT KẾ.

HIỆU CHỈNH:  
REV NGÀY NỘI DUNG

CHỦ ĐẦU TƯ:  
CÔNG TY TNHH ĐẦU TƯ  
**PHÚ VIỆT TÍN**  
ĐỊA CHỈ: LÔ 18-19 QUỐC LỘ 1A, XÃ DẦU GIẤY,  
TỈNH ĐỒNG NAI, VIỆT NAM

CTHĐT: ĐẶNG PHƯỚC BÌNH

ĐƠN VỊ THIẾT KẾ:  
CÔNG TY CỔ PHẦN TƯ VẤN THIẾT KẾ  
**BASE ARC**  
ĐỊA CHỈ: 138 ĐIỆN BIÊN PHỦ, PHƯỜNG TÂN ĐỊNH,  
TP. HỒ CHÍ MINH, VIỆT NAM

TỔNG GIÁM ĐỐC: TRẦN ĐỨC AN

CHỦ NHIỆM DỰ ÁN:

KTS. NGUYỄN THÀNH THÁI

CHỦ TRÌ THIẾT KẾ:

KS. TRƯƠNG NGỌC TRỌNG

THIẾT KẾ:

KS. PHẠM BÁ LINH

KIỂM TRA:

KS. TRƯƠNG NGỌC TRỌNG

DỰ ÁN:

KHU DÂN CƯ A1-C1 (ĐÔ THỊ DẦU GIẤY)  
ĐỊA ĐIỂM: XÃ DẦU GIẤY, TỈNH ĐỒNG NAI

CÔNG TRÌNH:

NHÀ Ở THƯƠNG MẠI LIÊN KẾ

HẠNG MỤC:

MẪU NHÀ T3-2b

TÊN BẢN VẼ:

MẶT BẰNG CẤP THOÁT NƯỚC TẦNG 1, TẦNG 2

MỤC ĐÍCH PHÁT HÀNH:

BẢN VẼ MỜI THẦU

THIẾT KẾ CƠ SỞ



THIẾT KẾ BẢN VẼ THI CÔNG

BẢN VẼ HOÀN CÔNG

HOÀN THÀNH 07/2025


TỶ LỆ NTS

SỐ HIỆU BẢN VẼ P2-03

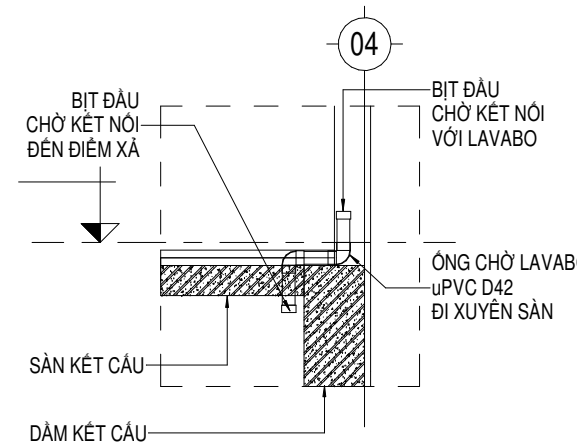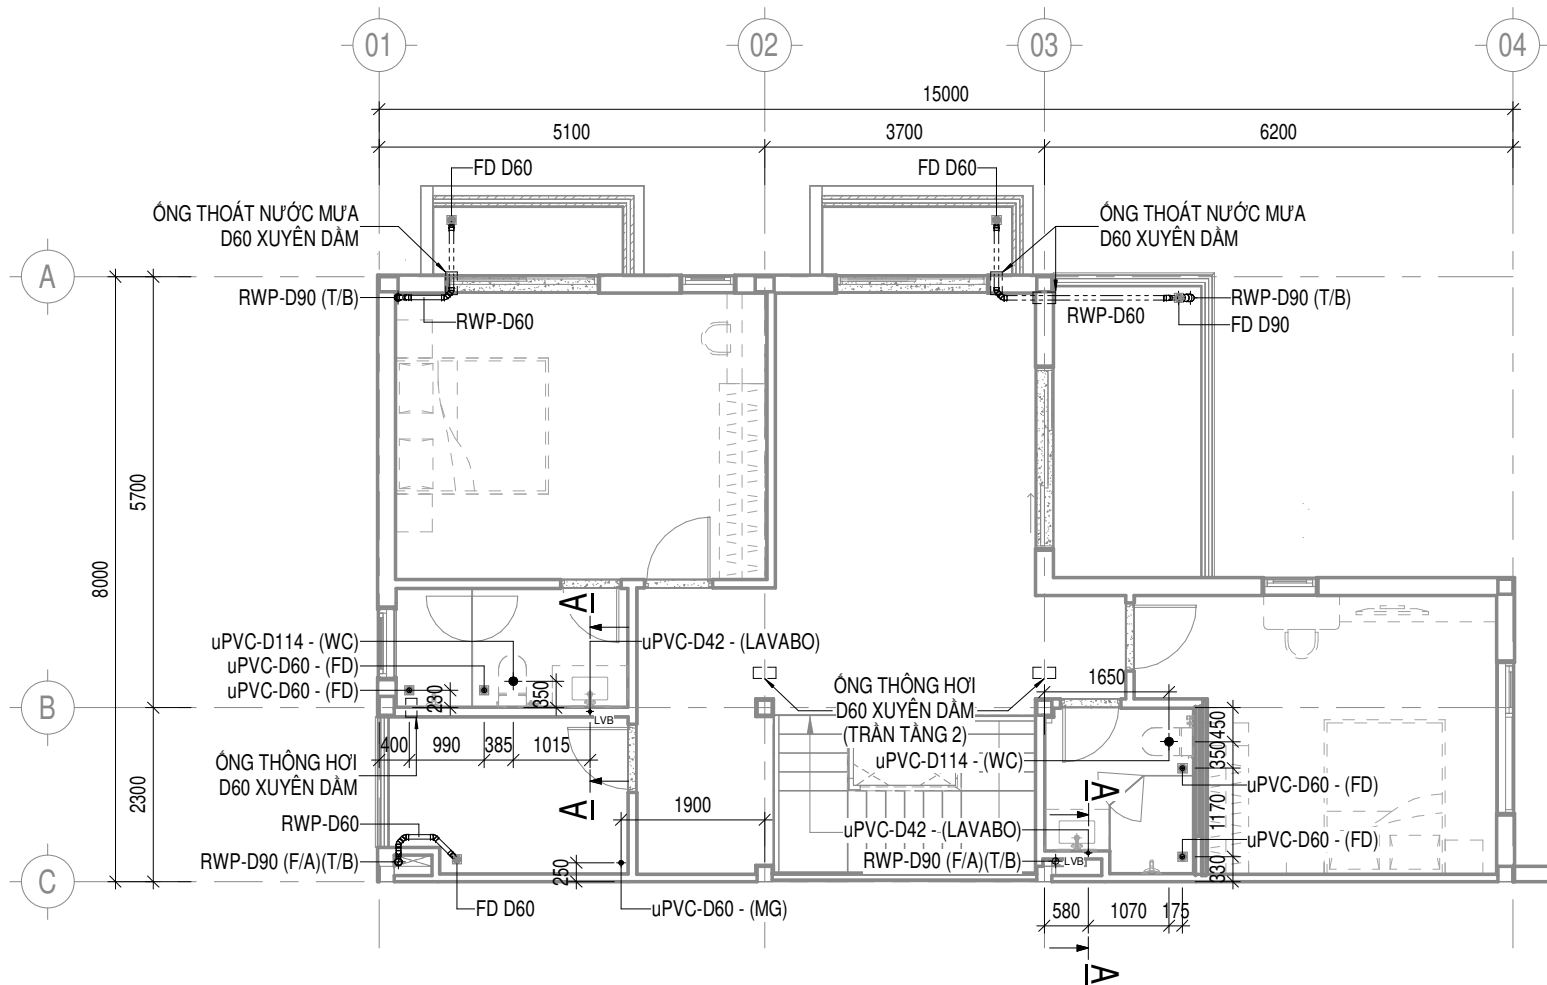


**MẶT CẮT A-A**  
TỶ LỆ 1 : 25

**MẶT BẰNG CẤP THOÁT NƯỚC TẦNG 3**  
TỶ LỆ 1 : 100

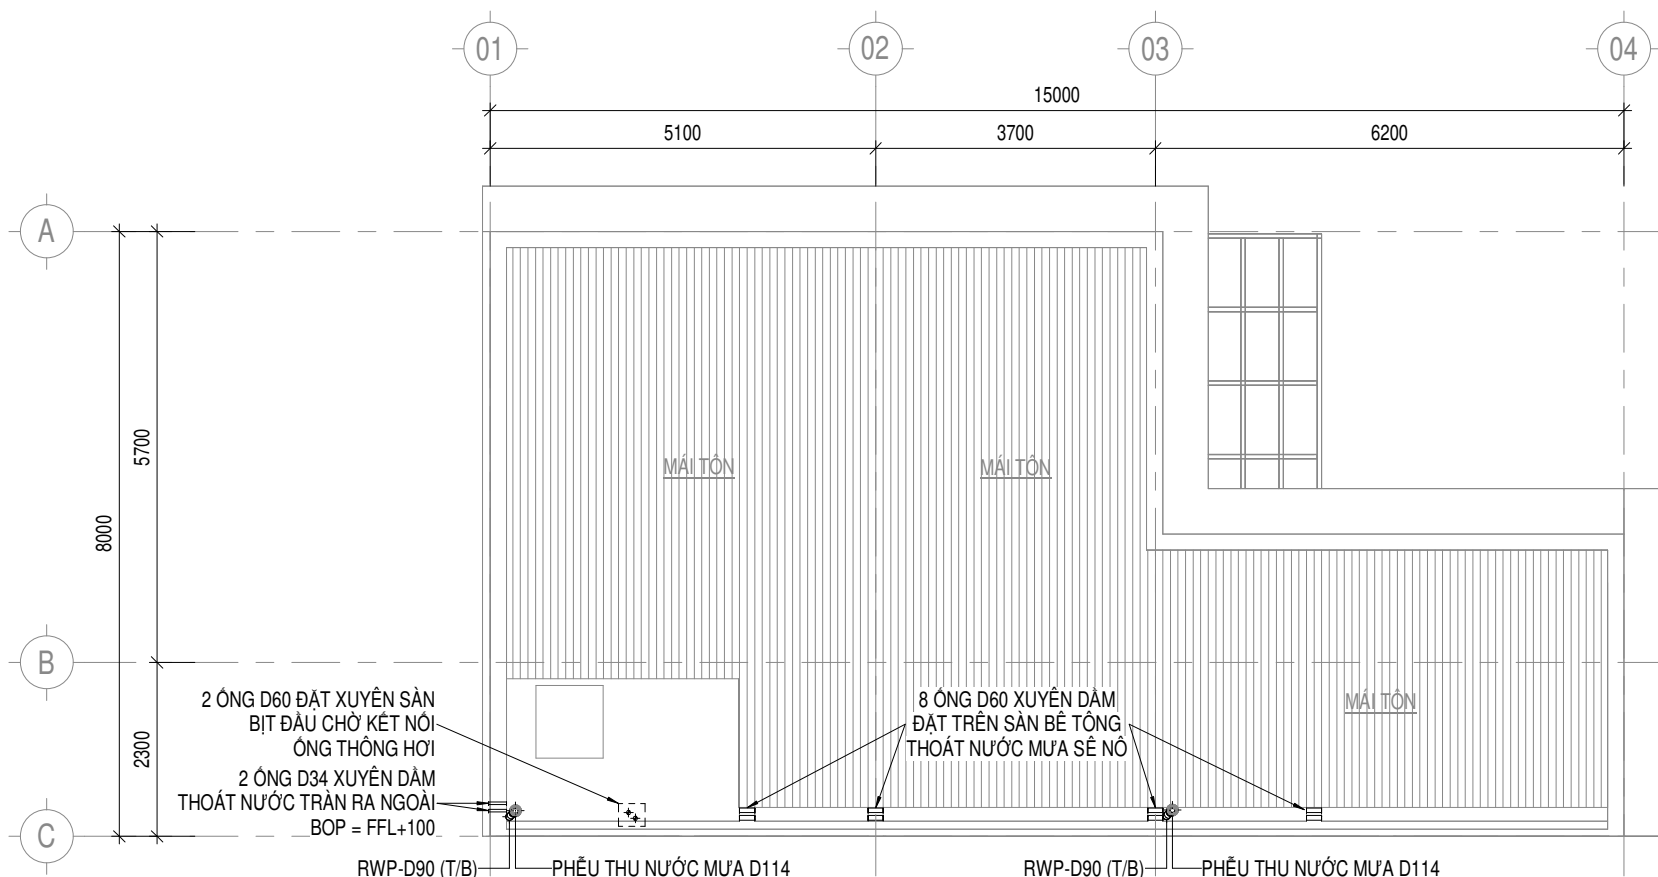



**MẶT BẰNG CẤP THOÁT NƯỚC TẦNG MÁI**  
TỶ LỆ 1 : 100

|   |         |                 |
|---|---------|-----------------|
| GHI CHÚ:<br>- CÁC ĐƠN VỊ THI CÔNG PHẢI PHỐI HỢP BẢN VẼ CỦA TẤT CẢ CÁC BỘ MÔN KHÁC NẾU THẤY SỰ KHÁC BIỆT PHẢI BÁO CHO ĐƠN VỊ THIẾT KẾ ĐỂ XỬ LÝ.<br>- KHI XỬ LÝ SỰ KHÁC BIỆT, PHẢI THỰC HIỆN ƯU TIÊN THEO THỨ TỰ GIỮA CÁC BỘ MÔN: KIẾN TRÚC → KẾT CẤU / BỘ MÔN KHÁC; HOẶC ƯU TIÊN TRONG CÙNG BỘ MÔN: CHI TIẾT → TỔNG THỂ<br>- CÁC SỐ LƯỢNG KỊCH THUỘC PHẢI ĐƯỢC KIỂM TRA THỰC TẾ TẠI CÔNG TRÌNH, NẾU THẤY SỰ KHÁC BIỆT SƠ VỚI BẢN VẼ THI PHẢI BÁO CHO ĐƠN VỊ THIẾT KẾ. |         |                 |
| HIỆU CHỈNH:   |         |                 |
| REV   | NGÀY    | NỘI DUNG        |
|   |         |                 |
| CHỦ ĐẦU TƯ:<br>CÔNG TY TNHH ĐẦU TƯ<br><b>PHÚ VIỆT TÍN</b><br>ĐỊA CHỈ: LÔ 18-19 QUỐC LỘ 1A, XÃ DẦU GIẤY,<br>TỈNH ĐỒNG NAI, VIỆT NAM   |         |                 |
|   |         |                 |
| CHTĐTV:   |         | ĐẶNG PHƯỚC BÌNH |
| ĐƠN VỊ THIẾT KẾ:<br>CÔNG TY CỔ PHẦN TƯ VẤN THIẾT KẾ<br><b>BASE ARC</b><br>ĐỊA CHỈ: 138 ĐIỆN BIÊN PHỦ, PHƯỜNG TÂN ĐỊNH,<br>TP. HỒ CHÍ MINH, VIỆT NAM   |         |                 |
|   |         |                 |
| TỔNG GIÁM ĐỐC   |         | TRẦN ĐỨC AN     |
| CHỦ NHIỆM DỰ ÁN:   |         |                 |
| KTS. NGUYỄN THÀNH THÁI   |         |                 |
| CHỦ TRÌ THIẾT KẾ:   |         |                 |
| KS. TRƯƠNG NGỌC TRỌNG   |         |                 |
| THIẾT KẾ:   |         |                 |
| KS. PHẠM BÁ LINH   |         |                 |
| KIỂM TRA:   |         |                 |
| KS. TRƯƠNG NGỌC TRỌNG   |         |                 |
| DỰ ÁN:<br>KHU DÂN CƯ A1-C1 (ĐÔ THỊ DẦU GIẤY)<br>ĐỊA ĐIỂM: XÃ DẦU GIẤY, TỈNH ĐỒNG NAI   |         |                 |
| CÔNG TRÌNH:<br><br>NHÀ Ở THƯƠNG MẠI LIÊN KẾ   |         |                 |
| HẠNG MỤC:<br><br>MẪU NHÀ T3-2b   |         |                 |
| TÊN BẢN VẼ:<br><br>MẶT BẰNG CẤP THOÁT NƯỚC TẦNG 3, TẦNG MÁI   |         |                 |
| MỤC ĐÍCH PHÁT HÀNH:   |         |                 |
| BẢN VẼ MỜI THẦU   |         |                 |
| THIẾT KẾ CƠ SỞ   |         |                 |
| ✓ THIẾT KẾ BẢN VẼ THI CÔNG   |         |                 |
| BẢN VẼ HOÀN CÔNG   |         |                 |
| HOÀN THÀNH   | 07/2025 |                 |
| TỶ LỆ   | NTS     |                 |
| SỐ HIỆU BẢN VẼ   | P2-04   |                 |

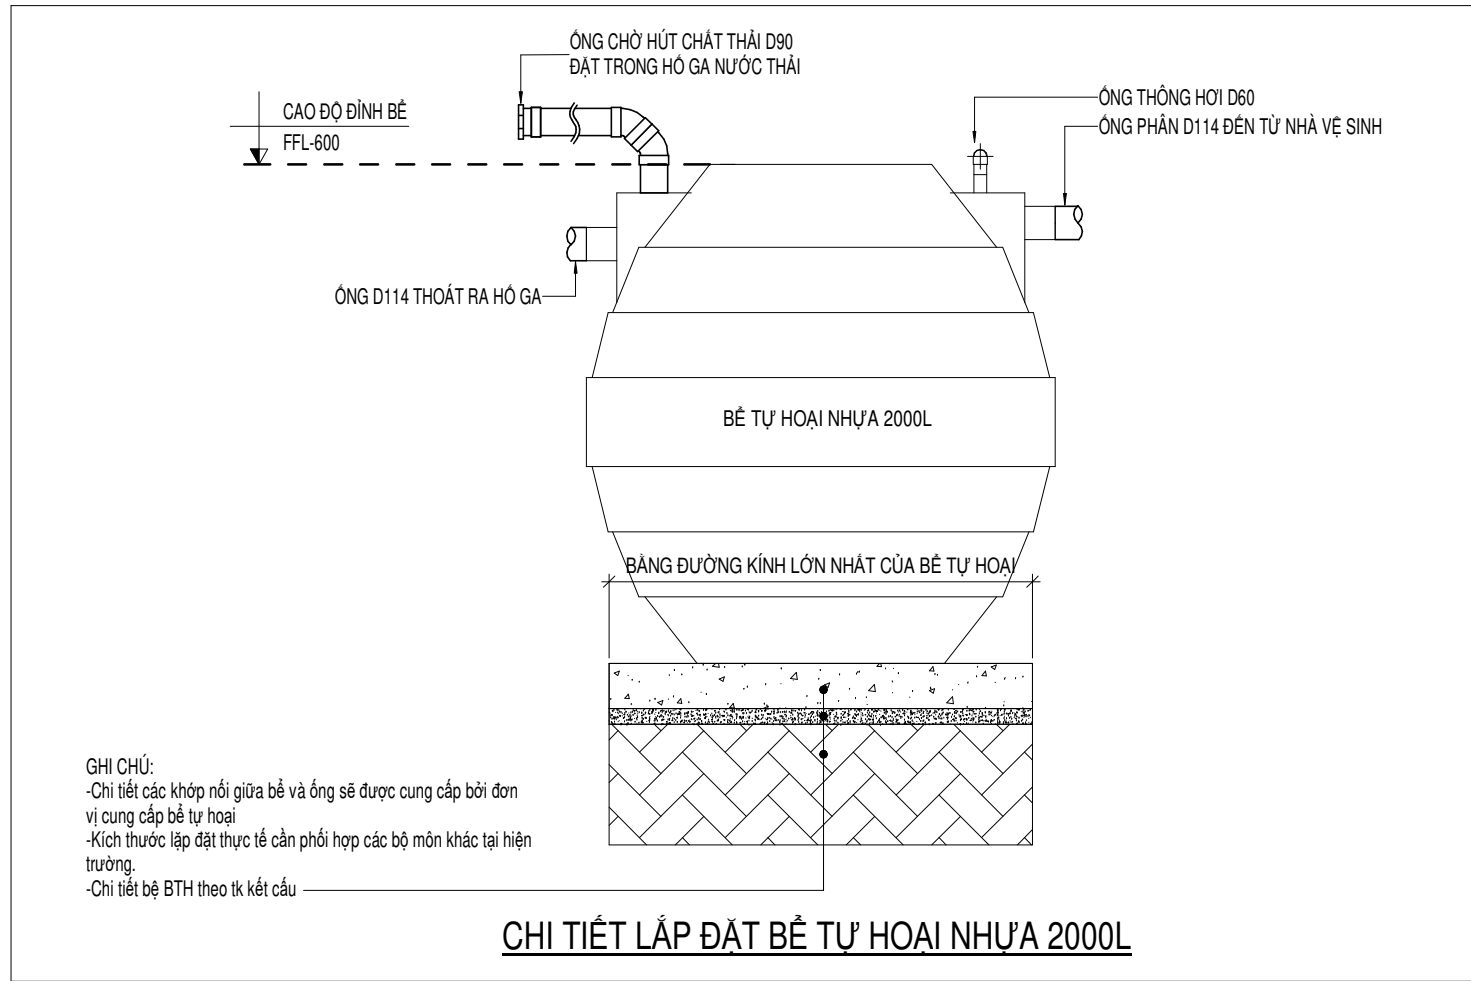


#### PHẦN KẾT CẤU HỒ GA (CHI TIẾT THEO THIẾT KẾ KẾT CẤU)

- SỬ DỤNG BÊ TÔNG ĐÁ 1x2, CẤP ĐỘ BỀN B15
- ĐÁY HỒ GA ĐÀM CHẶT K=0.9, LÓT NILON DÀY 0.2mm

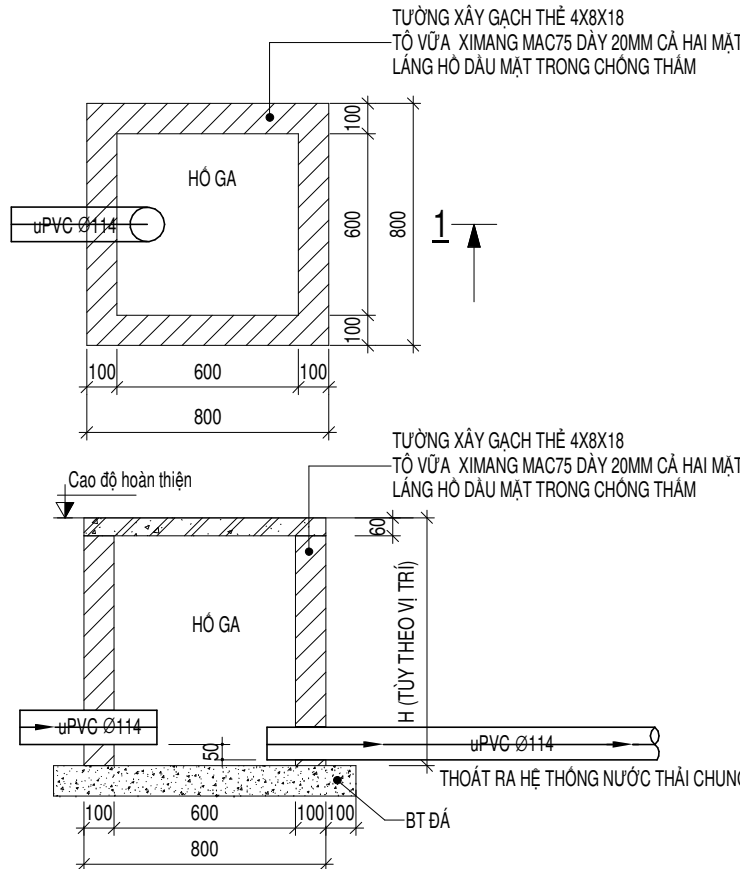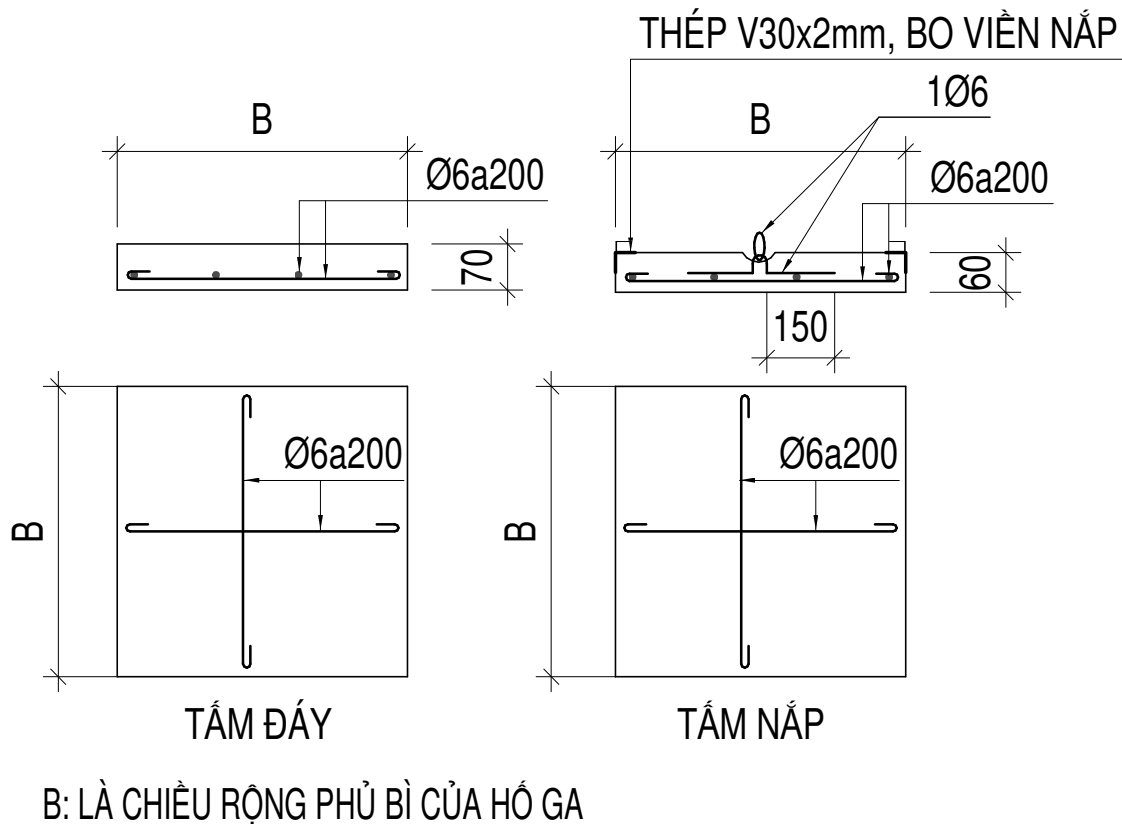


**CHI TIẾT HỒ GA, TỶ LỆ 1/25**

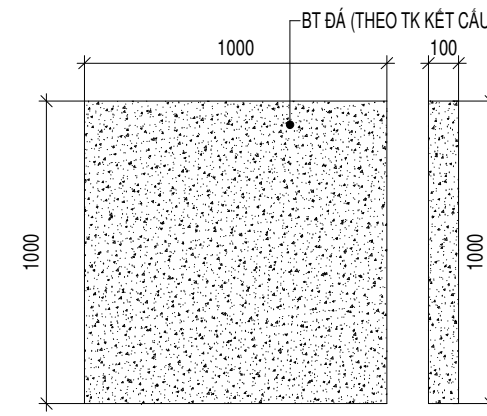


**TẦM ĐẠN ĐÁY HỒ GA, TỶ LỆ 1/25**  
(TẦM ĐẠN 2)


|   |         |                 |
|---|---------|-----------------|
| GHI CHÚ:<br>- CÁC ĐƠN VỊ THI CÔNG PHẢI PHỐI HỢP BẢN VẼ CỦA TẤT CẢ CÁC BỘ MÔN KHÁC NẾU THẤY SỰ KHÁC BIỆT PHẢI BẢO CHO ĐƠN VỊ THIẾT KẾ XỬ LÝ.<br>- KHI XỬ LÝ SỰ KHÁC BIỆT, PHẢI THỰC HIỆN ƯU TIÊN THEO THỨ TỰ GIỮA CÁC BỘ MÔN: KIẾN TRÚC → KẾT CẤU / BỘ MÔN KHÁC; HOẶC ƯU TIÊN TRONG CÙNG BỘ MÔN: CHI TIẾT → TỔNG THỂ<br>- CÁC SỐ LIỆU KỊCH THUỘC PHẢI ĐƯỢC KIỂM TRA THỰC TẾ TẠI CÔNG TRÌNH, NẾU THẤY SỰ KHÁC BIỆT SƠ VỚI BẢN VẼ THI PHẢI BẢO CHO ĐƠN VỊ THIẾT KẾ. |         |                 |
| HIỆU CHỈNH:   |         |                 |
| REV   | NGÀY    | NỘI DUNG        |
|   |         |                 |
| CHỦ ĐẦU TƯ:   |         |                 |
| CÔNG TY TNHH ĐẦU TƯ   |         |                 |
| <b>PHÚ VIỆT TÍN</b>   |         |                 |
| ĐỊA CHỈ: LÔ 18-19 QUỐC LỘ 1A, XÃ DẦU GIẤY, TỈNH ĐỒNG NAI, VIỆT NAM   |         |                 |
|   |         |                 |
| CĐT/ĐTV:   |         | ĐẶNG PHƯỚC BÌNH |
| ĐƠN VỊ THIẾT KẾ:   |         |                 |
| CÔNG TY CỔ PHẦN TƯ VẤN THIẾT KẾ   |         |                 |
| <b>BASE ARC</b>   |         |                 |
| ĐỊA CHỈ: 138 ĐIỆN BIÊN PHỦ, PHƯỜNG TÂN ĐỊNH, TP. HỒ CHÍ MINH, VIỆT NAM   |         |                 |
|   |         |                 |
| TỔNG GIÁM ĐỐC   |         | TRẦN ĐỨC AN     |
| CHỦ NHIỆM DỰ ÁN:   |         |                 |
| KTS. NGUYỄN THÀNH THÁI   |         |                 |
| CHỦ TRÌ THIẾT KẾ:   |         |                 |
| KS. TRƯƠNG NGỌC TRỌNG   |         |                 |
| THIẾT KẾ:   |         |                 |
| KS. PHẠM BÁ LINH   |         |                 |
| KIỂM TRA:   |         |                 |
| KS. TRƯƠNG NGỌC TRỌNG   |         |                 |
| DỰ ÁN:   |         |                 |
| KHU DÂN CƯ A1-C1 (ĐÔ THỊ DẦU GIẤY)   |         |                 |
| ĐỊA ĐIỂM: XÃ DẦU GIẤY, TỈNH ĐỒNG NAI   |         |                 |
| CÔNG TRÌNH:   |         |                 |
| NHÀ Ở THƯƠNG MẠI LIÊN KẾ   |         |                 |
| HẠNG MỤC:   |         |                 |
| MẪU NHÀ T3-2b   |         |                 |
| TÊN BẢN VẼ:   |         |                 |
| CHI TIẾT BỂ TỰ HOẠI 2000L   |         |                 |
| MỤC ĐÍCH PHÁT HÀNH:   |         |                 |
| BẢN VẼ MỜI THẦU   |         |                 |
| THIẾT KẾ CƠ SỞ   |         |                 |
| ✓ THIẾT KẾ BẢN VẼ THI CÔNG   |         |                 |
| BẢN VẼ HOÀN CÔNG   |         |                 |
| HOÀN THÀNH   | 07/2025 |                 |
| TỶ LỆ   | NTS     |                 |
| SỐ HIỆU BẢN VẼ   | P2-05   |                 |

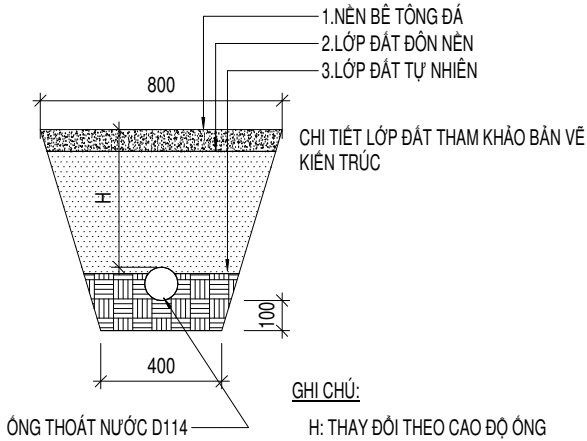


CHI TIẾT PHUI ĐÀO CHO ØNG THOÁT NƯỚC

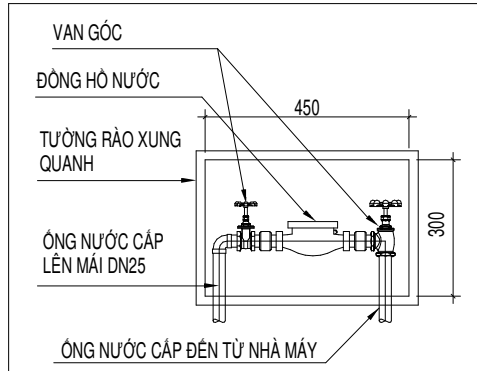


CHI TIẾT MẶT TRONG ĐỒNG HỒ NƯỚC

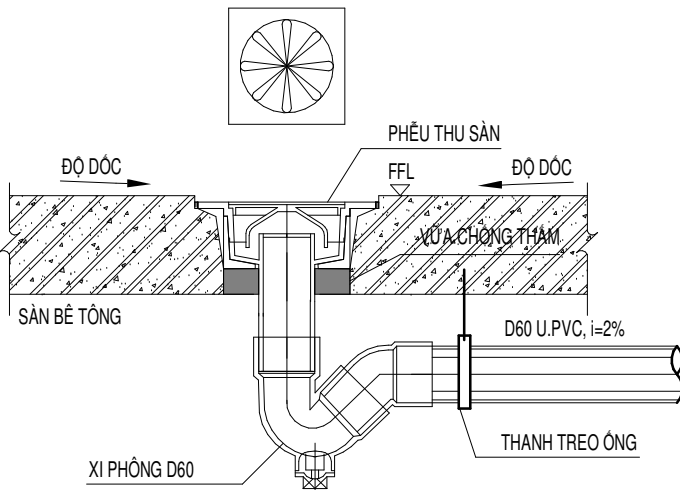


CHI TIẾT LẮP ĐẶT PHỄU THU SÀN (TREGO TRẦN)

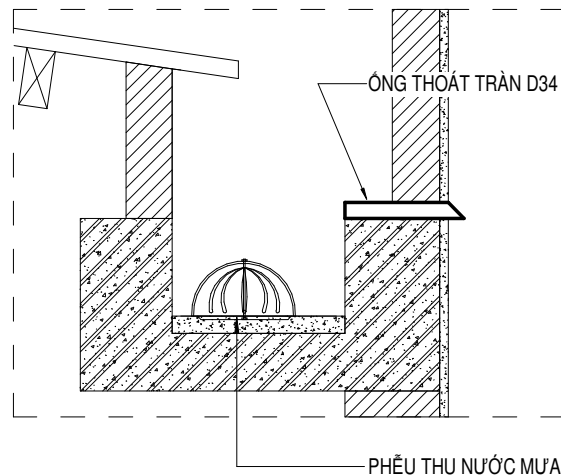


CHI TIẾT ØNG THOÁT TRẦN SÊ NÔ

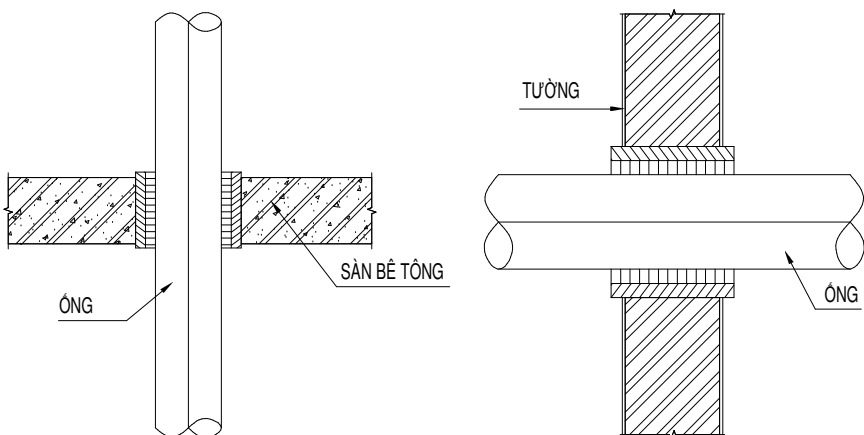


CHI TIẾT ØNG XUYỀN SÀN, TƯỜNG ĐIỂN HÌNH

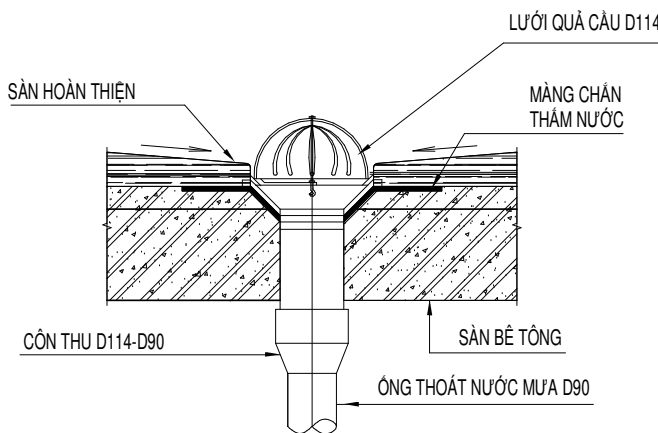


CHI TIẾT LẮP ĐẶT PHỄU THU NƯỚC MƯA

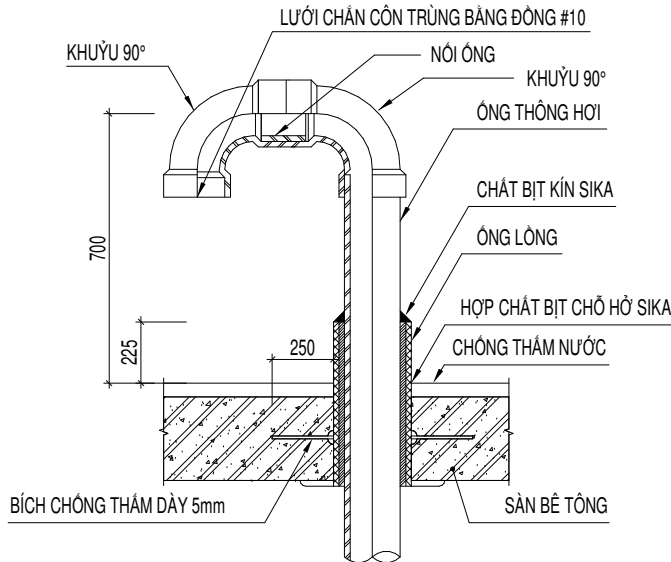

CHI TIẾT ØNG THÔNG HƠI VƯỢT MÁI

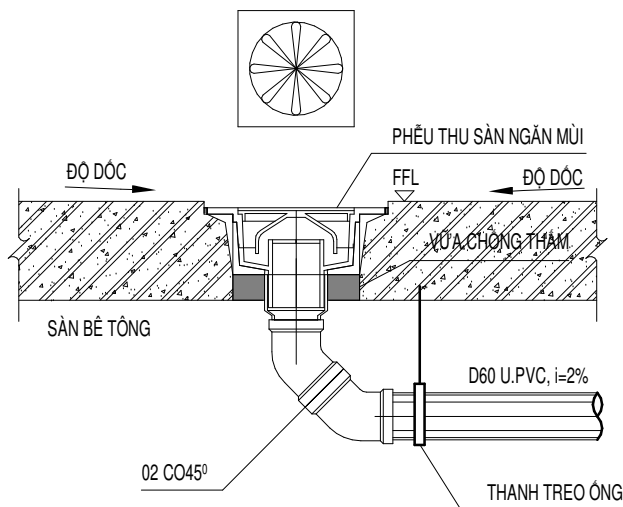

CHI TIẾT LẮP ĐẶT PHỄU THU SÀN (TẦNG 1)

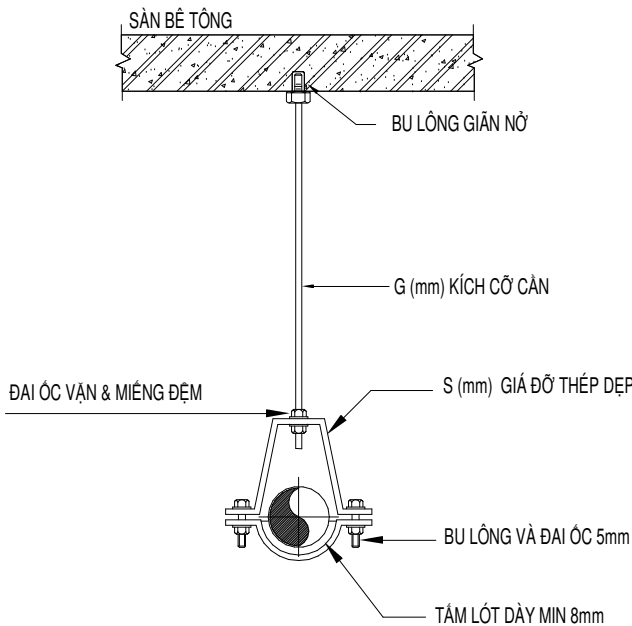

CHI TIẾT TREGO ØNG

BẢNG THÔNG SỐ GIÁ TREGO ØNG

| CỖ ØNG ( mm ) | KHOẢNG CÁCH (mm) |         | CỖ GIÁ TREGO ( G ) ( mm ) |
|---------------|------------------|---------|---------------------------|
|               | NHỰA uPVC        | ØNG PPR |                           |
| 15            | 1200             | 1200    | 8                         |
| 20            | 1200             | 1200    | 8                         |
| 25            | 1200             | 1200    | 8                         |
| 32            | 1200             | 1200    | 8                         |
| 40            | 1200             | 1200    | 8                         |
| 50            | 1200             | 1200    | 8                         |
| 65            | 1200             | 1200    | 10                        |
| 80            | 1500             | 1500    | 10                        |
| 100           | 1500             | 1500    | 10                        |
| 150           | 1800             | 1800    | 10                        |
| 200           | -                | -       | 10                        |

THÔNG SỐ GIÁ TREGO ØNG

| CỖ ØNG ( mm ) | THANH ( S x b ) |        |
|---------------|-----------------|--------|
|               | S (mm)          | b (mm) |
| DN < 50       | 3               | 18     |
| DN > 50       | 5               | 25     |

GHI CHÚ:  
- CÁC ĐƠN VỊ THI CÔNG PHẢI PHỐI HỢP BẢN VẼ CỦA TẤT CẢ CÁC BỘ MÔN KHÁC NẾU THẤY SỰ KHÁC BIỆT PHẢI BẢO CHỨNG ĐƠN VỊ THIẾT KẾ XỬ LÝ.  
- KHI XỬ LÝ SỰ KHÁC BIỆT, PHẢI THỰC HIỆN ƯU TIÊN THEO THỨ TỰ GIỮA CÁC BỘ MÔN: KIẾN TRÚC → KẾT CẤU / BỐ MÔN KHÁC; HOẶC ƯU TIÊN TRONG CÙNG BỘ MÔN: CHI TIẾT → TỔNG THỂ.  
- CÁC SỐ LƯU KỊCH THUỘC PHẢI ĐƯỢC KIỂM TRA THỰC TẾ TẠI CÔNG TRÌNH, NẾU THẤY SỰ KHÁC BIỆT SƠ VỚI BẢN VẼ THI PHẢI BẢO CHỨNG ĐƠN VỊ THIẾT KẾ.

HIỆU CHỈNH:  
REV NGÀY NỘI DUNG

CHỦ ĐẦU TƯ:  
CÔNG TY TNHH ĐẦU TƯ  
**PHÚ VIỆT TÍN**  
ĐỊA CHỈ: LÔ 18-19 QUỐC LỘ 1A, XÃ DẦU GIẤY, TỈNH ĐỒNG NAI, VIỆT NAM

CTHĐT: ĐẶNG PHƯỚC BÌNH

ĐƠN VỊ THIẾT KẾ:  
CÔNG TY CỔ PHẦN TƯ VẤN THIẾT KẾ  
**BASE ARC**  
ĐỊA CHỈ: 138 ĐIỆN BIÊN PHỦ, PHƯỜNG TÂN ĐỊNH, TP. HỒ CHÍ MINH, VIỆT NAM

TỔNG GIÁM ĐỐC: TRẦN ĐỨC AN

CHỦ NHIỆM DỰ ÁN:

KTS. NGUYỄN THÀNH THÁI

CHỦ TRÌ THIẾT KẾ:

KS. TRƯƠNG NGỌC TRỌNG

THIẾT KẾ:

KS. PHẠM BÁ LINH

KIỂM TRA:

KS. TRƯƠNG NGỌC TRỌNG

DỰ ÁN:

KHU DÂN CƯ A1-C1 (ĐÔ THỊ DẦU GIẤY)

ĐỊA ĐIỂM: XÃ DẦU GIẤY, TỈNH ĐỒNG NAI

CÔNG TRÌNH:

NHÀ Ở THƯƠNG MẠI LIÊN KẾ

HẠNG MỤC:

MẪU NHÀ T3-2b

TÊN BẢN VẼ:

CHI TIẾT ĐIỂN HÌNH

MỤC ĐÍCH PHÁT HÀNH:

BẢN VẼ MỜI THẦU

THIẾT KẾ CƠ SỞ

✓ THIẾT KẾ BẢN VẼ THI CÔNG

BẢN VẼ HOÀN CÔNG

HOÀN THÀNH 07/2025

TỶ LỆ NTS

SỐ HIỆU BẢN VẼ P2-06